CADERNO DE MARCENARIA

EMPÓRIO HASS ambientes planejados

contato.emporiohass@gmail.com
(61)99303-3151/98274-3709
Instagram: @emporiohass

ARQUITETO RESPONSÁVEL:
José Adalberto Meuren
CAU Nº 000A487848
(61)98274-3709
jmeuren@gmail.com


CONTEÚDO DA PRANCHA:
CAPA

ESCALA:
Indicada na Prancha

CLIENTE:
Gisele Landim de Souza


ENDEREÇO:
SGCV LT 20 COND. NEW YORK
BLOCO A APT 101
Brasília


ARQUIVO:
Arq_Int_Gis_Park_Sul
REVISÃO Nº:
R00
DATA REVISÃO:
23-10-2024

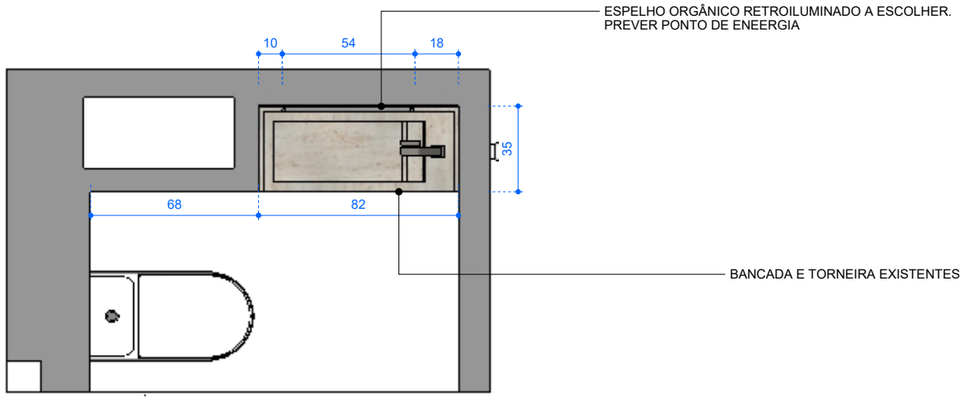

LAVABO - PLANTA BAIXA


ESCALA 1:25

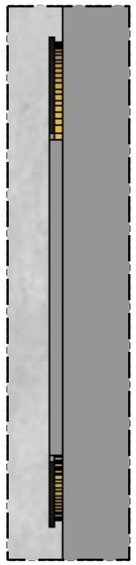

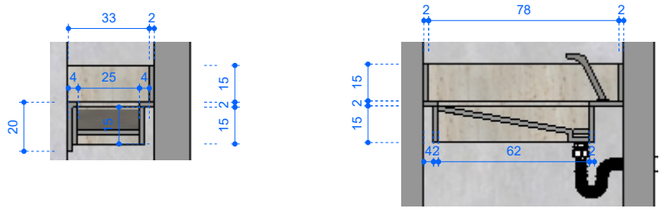


LAVABO - BANCADA

ESCALA 1:25

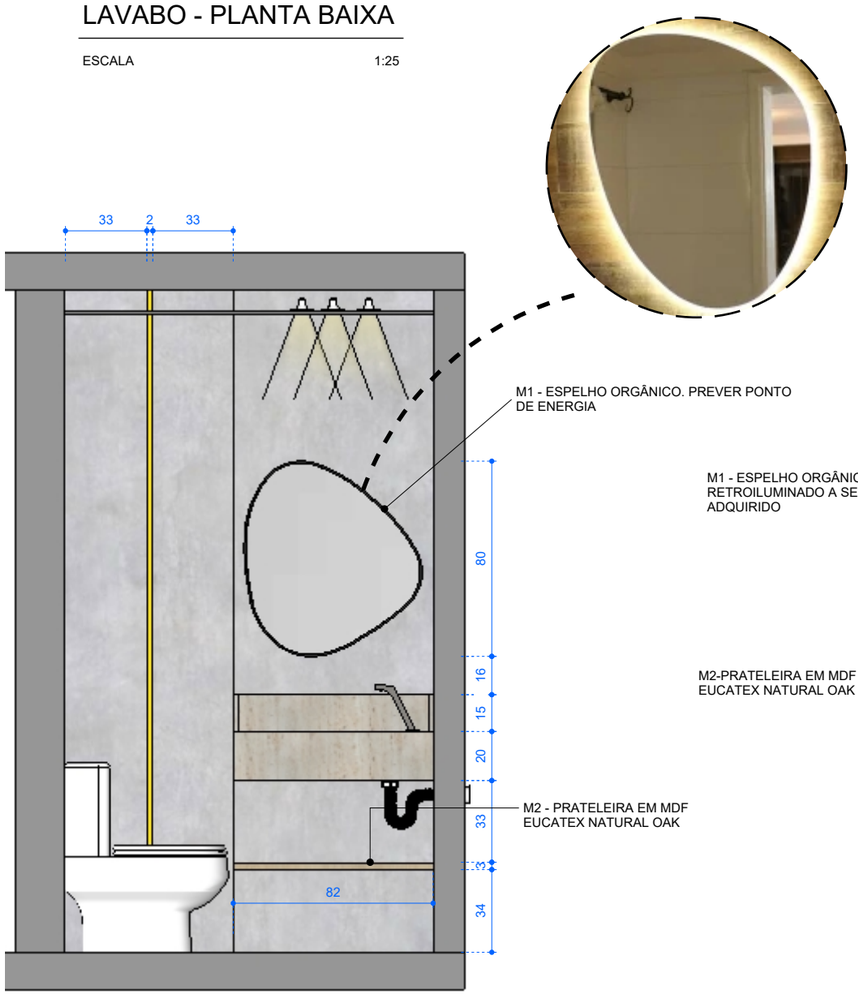


LAVABO - ELEVAÇÃO

ESCALA 1:25

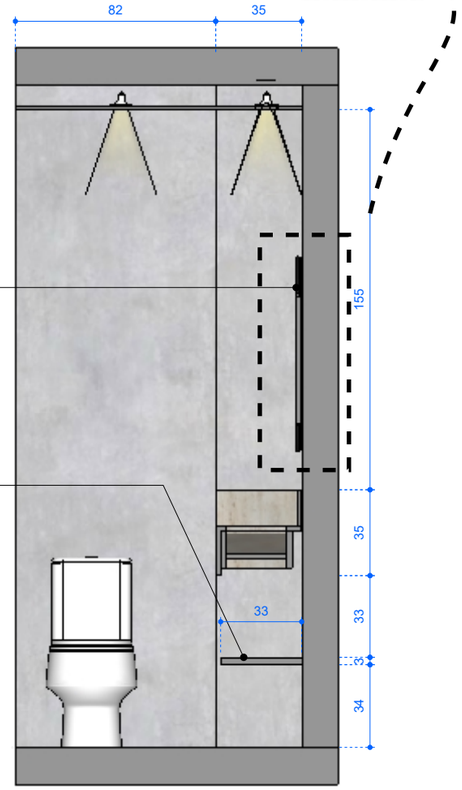

LAVABO - ELEVAÇÃO

ESCALA 1:25

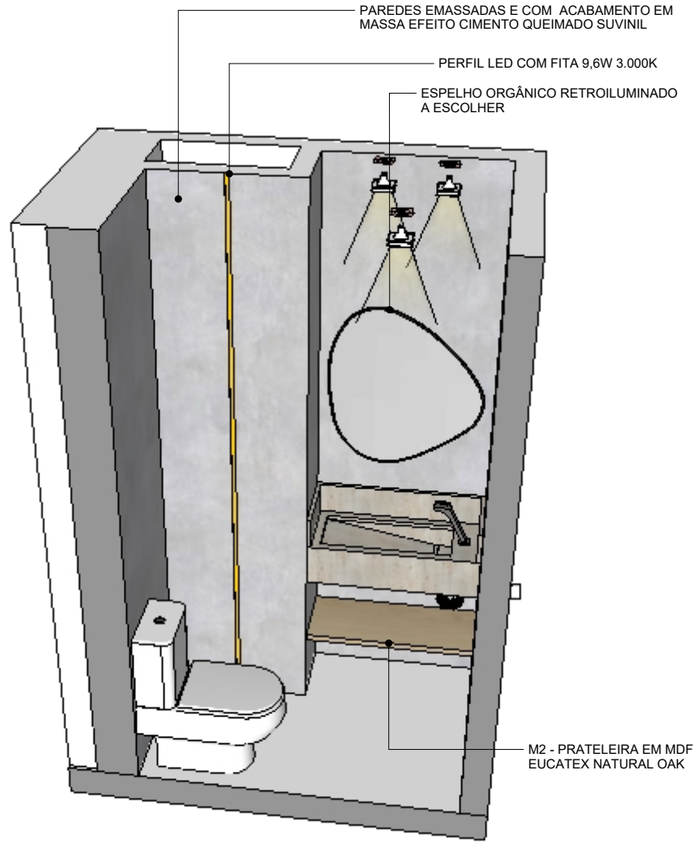

LAVABO - ISOMÉTRICA

ESCALA 1:25

EMPÓRIO HASS ambientes planejados

contato.emporiohass@gmail.com
(61)99303-3151/98274-3709
Instagram: @emporiohass

ARQUITETO RESPONSÁVEL:
José Adalberto Meuren
CAU Nº 000A487848
(61)98274-3709
jmeuren@gmail.com

CONTEÚDO DA PRANCHA:
M1/M2 - LAVABO - ESPELHO E PRATELEIRA

ESCALA:
Indicada na Prancha


CLIENTE:
Gisele Landim de Souza

ENDEREÇO:
SGCV LT 20 COND. NEW YORK
BLOCO A APT 101
Brasília

ARQUIVO:
Arq_Int_Gis_Park_Sul
REVISÃO Nº:
R00
DATA REVISÃO:
23-10-2024


OBSERVAÇÕES:
Consultar arquiteto em caso de dúvida e/ou alteração;
Conferir medidas no local;
Medidas em cota prevalecem sobre o desenho

FOLHA:
1/24

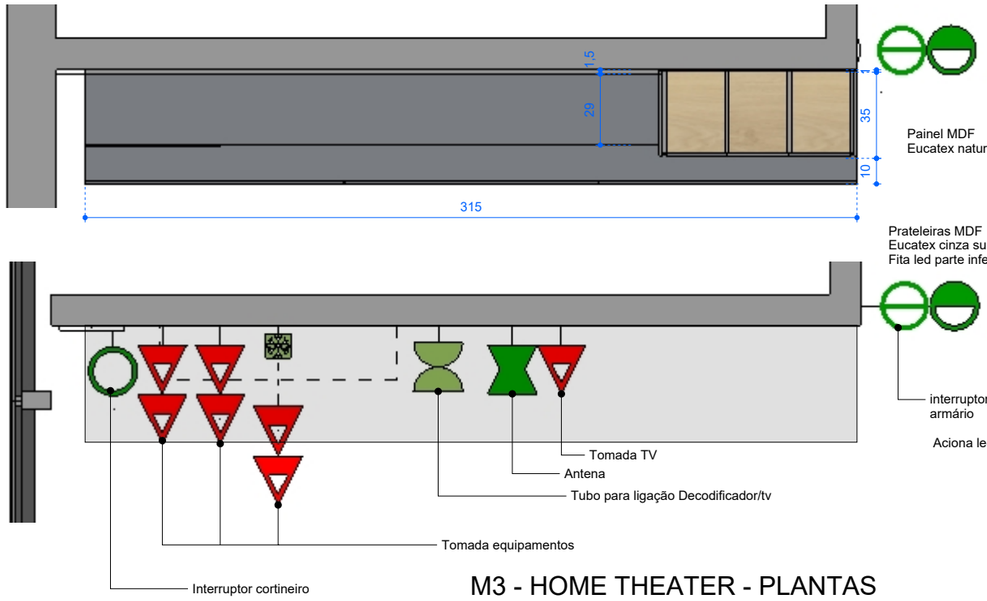

M3 - HOME THEATER - PLANTAS

ESCALA 1:25

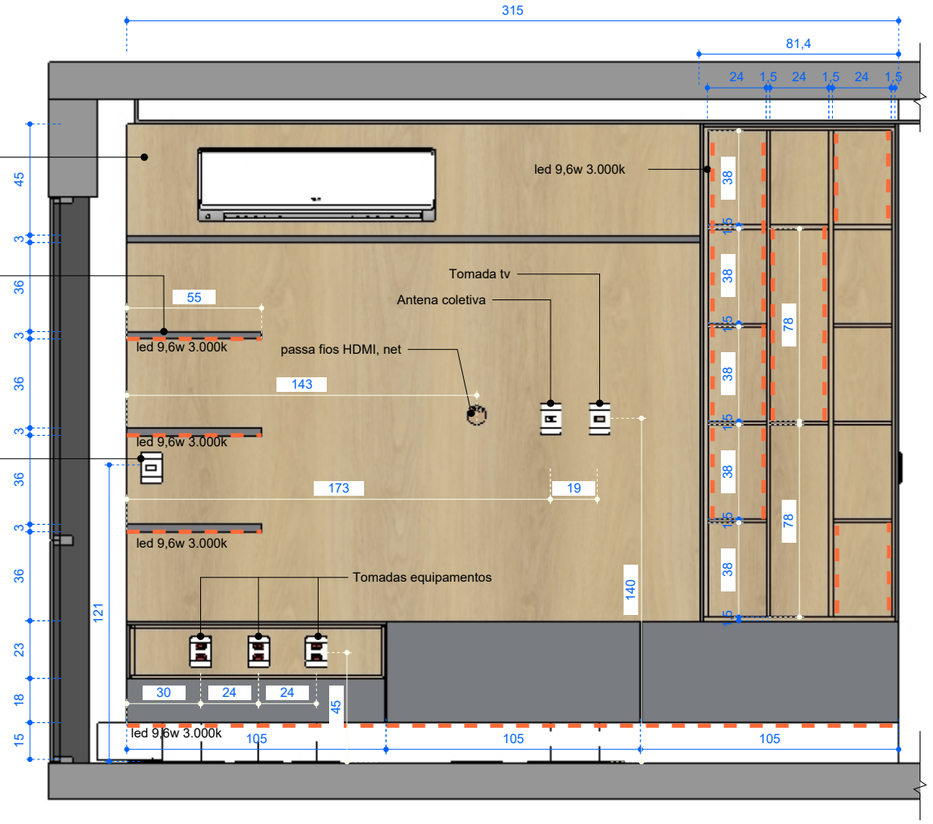


M3 - HOME THEATER - ELEV. FRONTAL

ESCALA 1:25



M3 - HOME THEATER - ELEV. FRONTAL

ESCALA 1:25

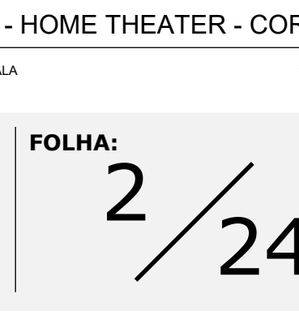

M3 - HOME THEATER - CORTE

ESCALA 1:25

EMPÓRIO HASS ambientes planejados

contato.emporiohass@gmail.com
(61)99303-3151/98274-3709
Instagram: @emporiohass

ARQUITETO RESPONSÁVEL:
José Adalberto Meuren
CAU Nº 000A487848
(61)98274-3709
jmeuren@gmail.com

CONTEÚDO DA PRANCHA:
M3 - HOME THEATER

ESCALA:
Indicada na Prancha


CLIENTE:
Gisele Landim de Souza

ENDEREÇO:
SGCV LT 20 COND. NEW YORK
BLOCO A APT 101
Brasília

ARQUIVO:
Arq_Int_Gis_Park_Sul
REVISÃO Nº:
R00
DATA REVISÃO:
23-10-2024


OBSERVAÇÕES:
Consultar arquiteto em caso de dúvida e/ou alteração;
Conferir medidas no local;
Medidas em cota prevalecem sobre o desenho

FOLHA:
2/24

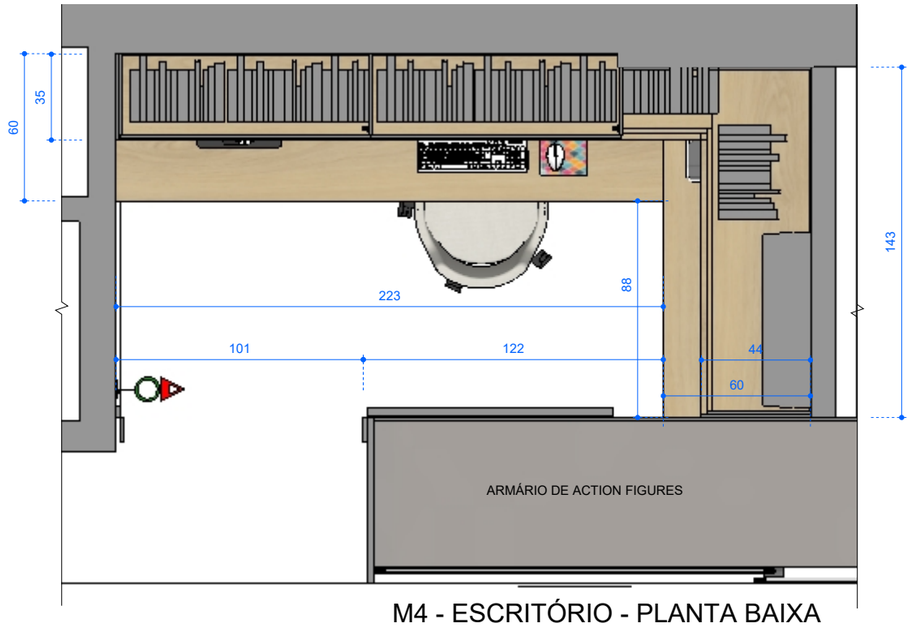

M4 - ESCRITÓRIO - PLANTA BAIXA


ESCALA 1:25

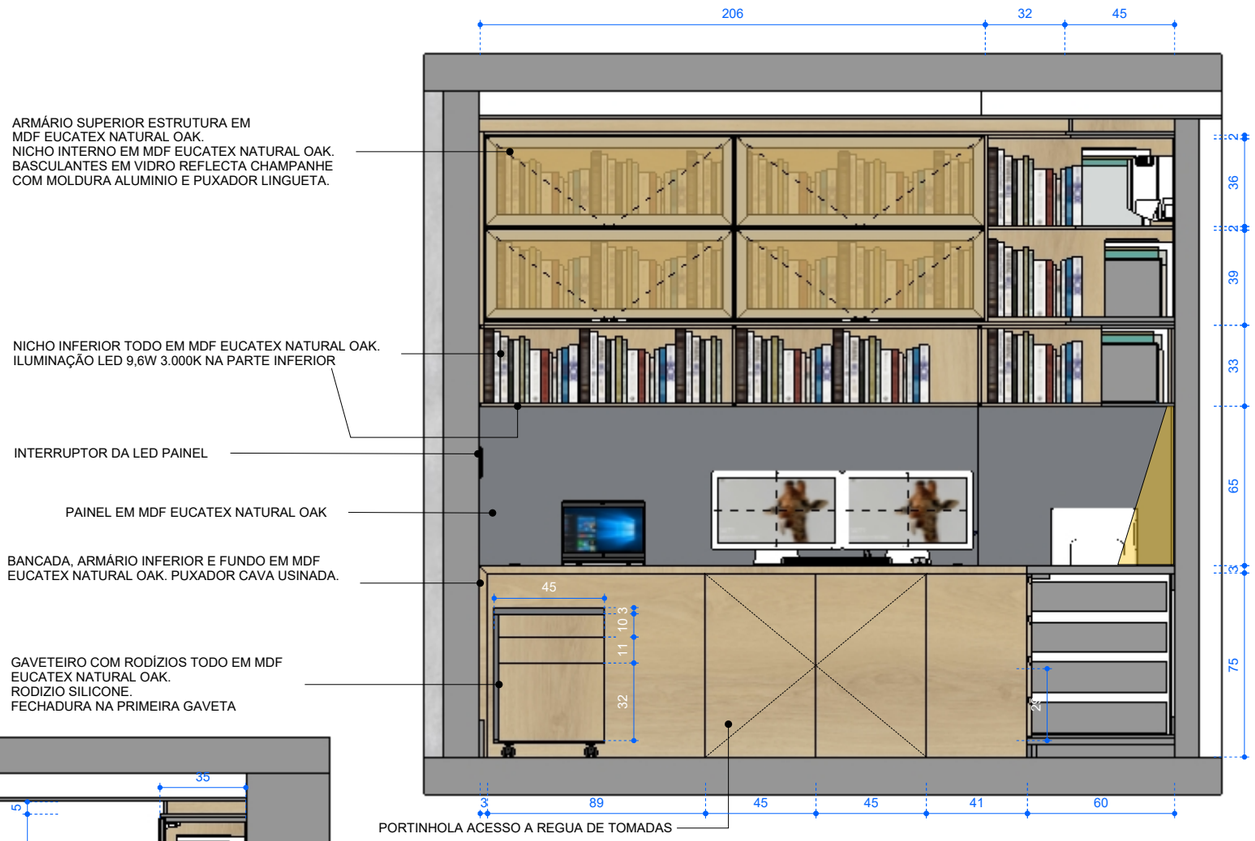

M4 - ESCRITÓRIO - ELEV. FRONTAL


ESCALA 1:25



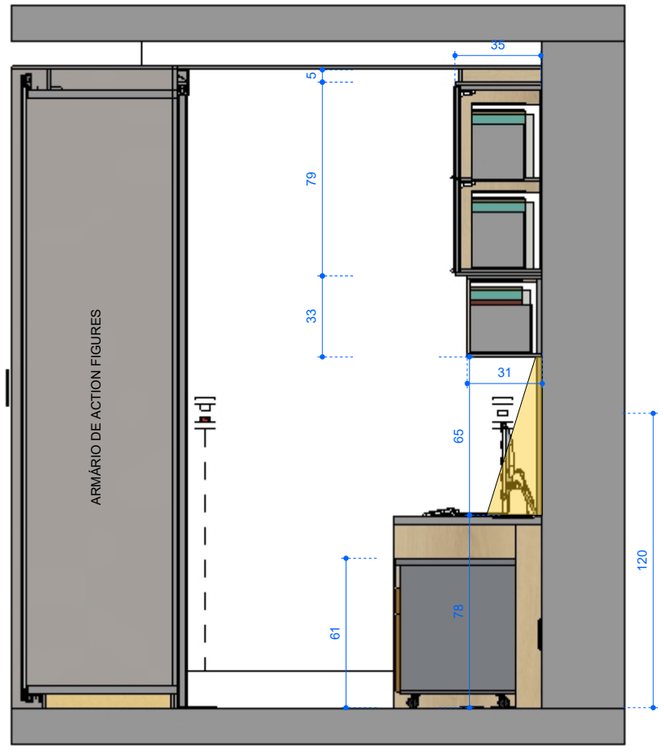

M4- ESCRITÓRIO - ELEV. LATERAL

ESCALA 1:25

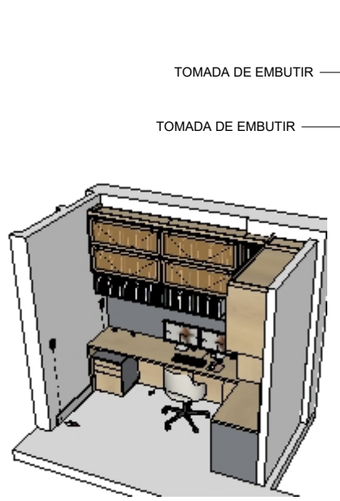

EMPÓRIO HASS ambientes planejados

contato.emporiohass@gmail.com
(61)99303-3151/98274-3709
Instagram: @emporiohass

ARQUITETO RESPONSÁVEL:
José Adalberto Meuren
CAU Nº 000A487848
(61)98274-3709
jmeuren@gmail.com

CONTEÚDO DA PRANCHA:
M4 - ESCRITÓRIO

ESCALA:
Indicada na Prancha


CLIENTE:
Gisele Landim de Souza

ENDEREÇO:
SGCV LT 20 COND. NEW YORK
BLOCO A APT 101
Brasília

ARQUIVO:
Arq_Int_Gis_Park_Sul
REVISÃO Nº:
R00
DATA REVISÃO:
23-10-2024

OBSERVAÇÕES:
Consultar arquiteto em caso de dúvida e/ou alteração;
Conferir medidas no local;
Medidas em cota prevalecem sobre o desenho

FOLHA:
3/24

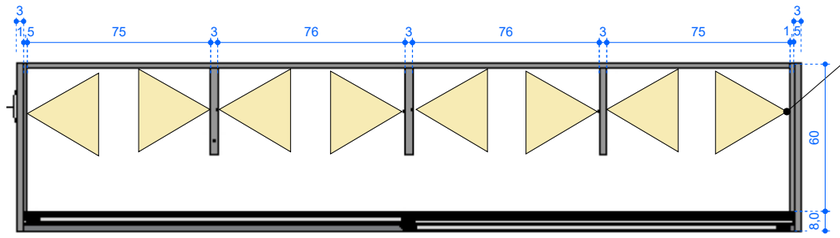


PERFIL LED INSERIDO MARCENARIA.
FITA LED 9,6WATS 3.000K

M5- ARMÁRIO ACTION FIGURES - PLANTA BAIXA

ESCALA 1:25


ARMÁRIO ESTRUTURA EM MDF EUCATEX
CINZA SUPREMO.
NICHO INTERNO EM MDF DURATEX BRANCO.
PORTAS DE CORRER EM VIDRO TRANSPARENTE
CRISTAL COM MOLDURA ALUMINIO FOSCO
PUXADOR NO PRÓPRIO PERFIL

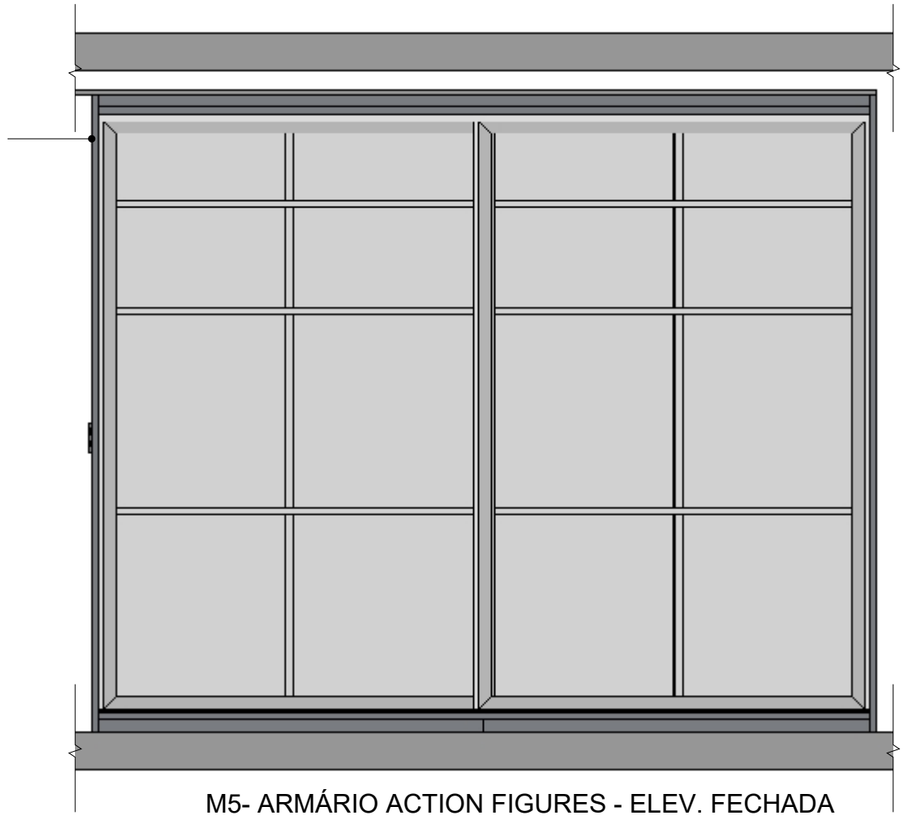

M5- ARMÁRIO ACTION FIGURES - ELEV. FECHADA

ESCALA 1:25


PERFIL LED INSERIDO MARCENARIA EM
TODAS AS LATERAIS

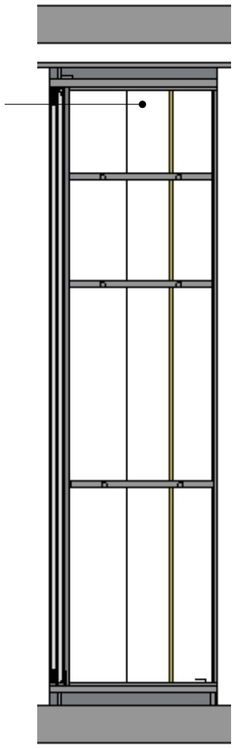

M5 - CORTE


ESCALA 1:25


PERFIL LED COM FITA 9,6W 3.000K EM TODAS
AS COLUNAS (INCLUSIVE LATERAIS DO NICHO)
OBS: COLOCAR DRIVE NO ARREMATE DO TETO

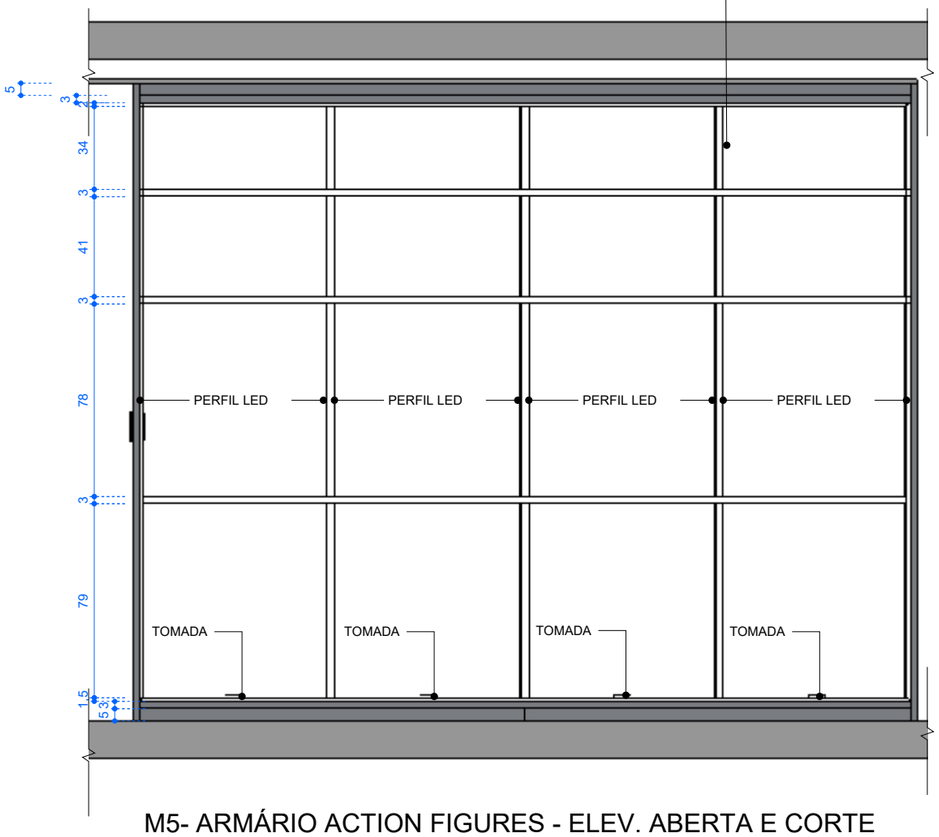

M5- ARMÁRIO ACTION FIGURES - ELEV. ABERTA E CORTE

ESCALA 1:25

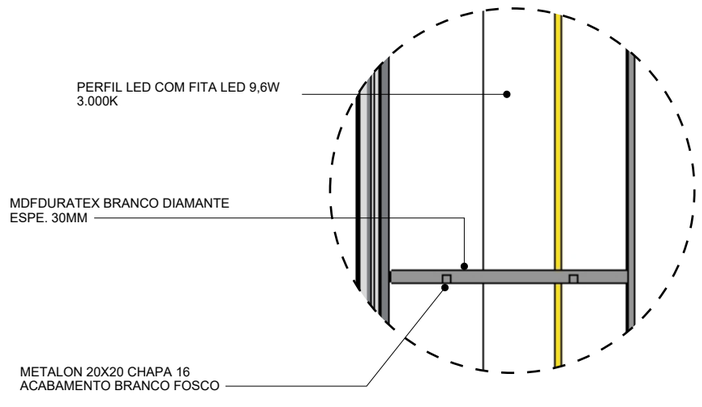

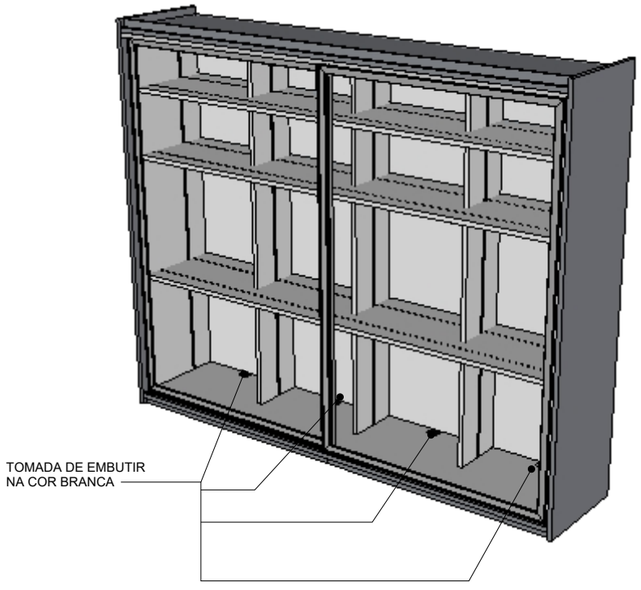

EMPÓRIO HASS ambientes planejados
contato.emporiohass@gmail.com
(61)99303-3151/98274-3709
Instagram: @emporiohass

ARQUITETO RESPONSÁVEL:
José Adalberto Meuren
CAU Nº 000A487848
(61)98274-3709
jmeuren@gmail.com

CONTEÚDO DA PRANCHA:
M5 - ARMÁRIO ACTION FIGURES

ESCALA:
Indicada na Prancha


CLIENTE:
Gisele Landim de Souza

ENDEREÇO:
SGCV LT 20 COND. NEW YORK
BLOCO A APT 101
Brasília

ARQUIVO:
Arq_Int_Gis_Park_Sul
REVISÃO Nº:
R00
DATA REVISÃO:
23-10-2024


OBSERVAÇÕES:
Consultar arquiteto em caso de dúvida e/ou alteração;
Conferir medidas no local;
Medidas em cota prevalecem sobre o desenho


FOLHA:

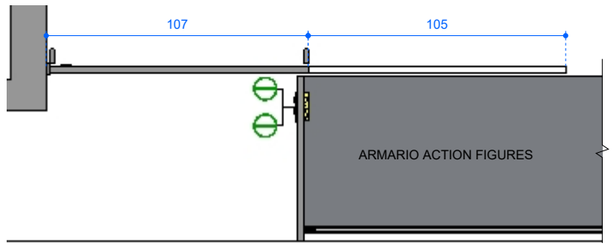

M6 - PORTA CORRER - PLANTA


ESCALA 1:25

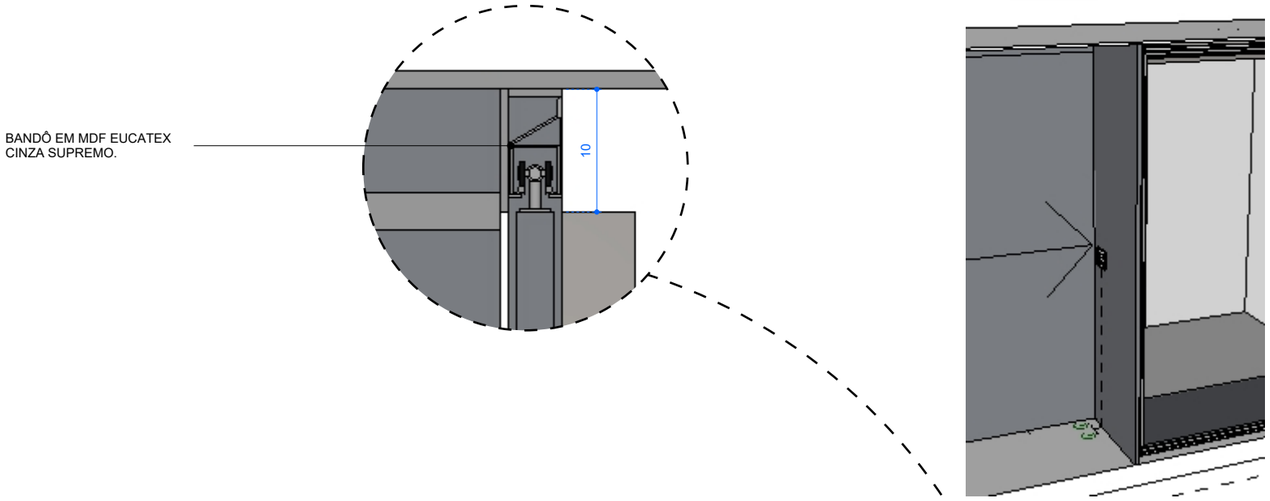

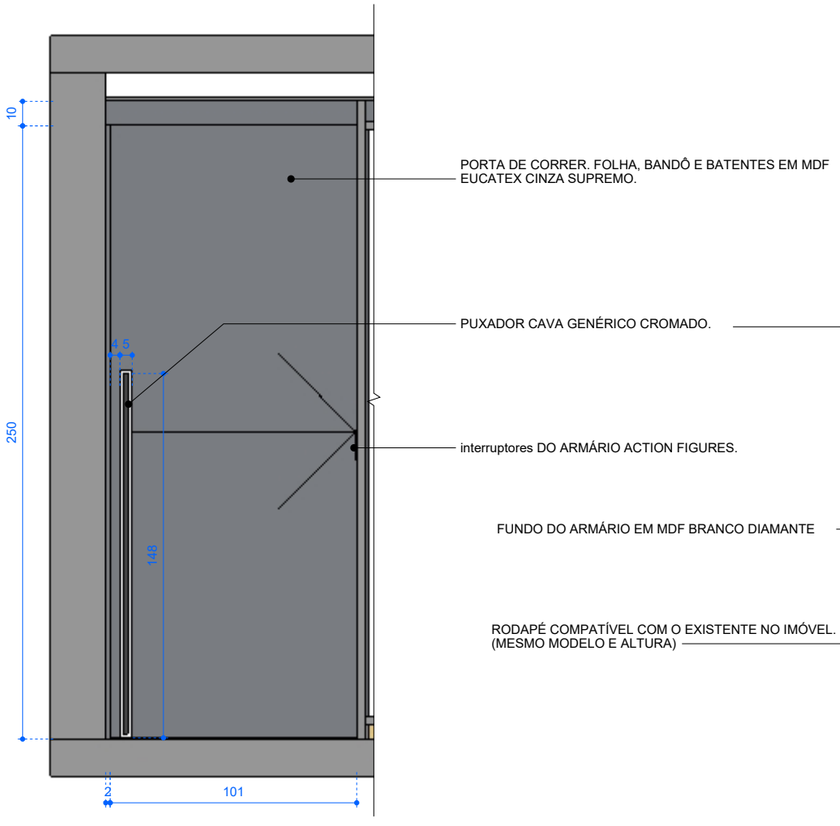


M6 - PORTA CORRER - ELEVAÇÃO

ESCALA 1:25

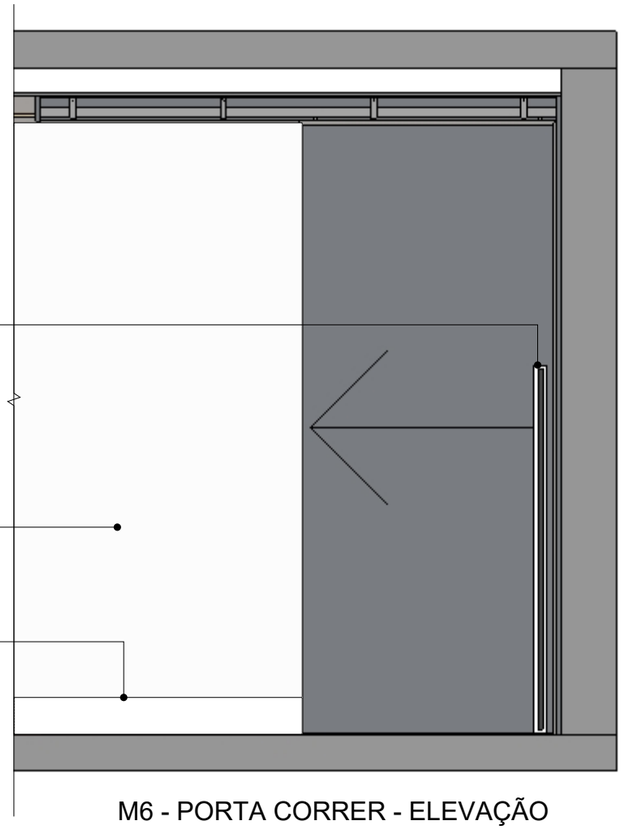

M6 - PORTA CORRER - ELEVAÇÃO

ESCALA 1:25

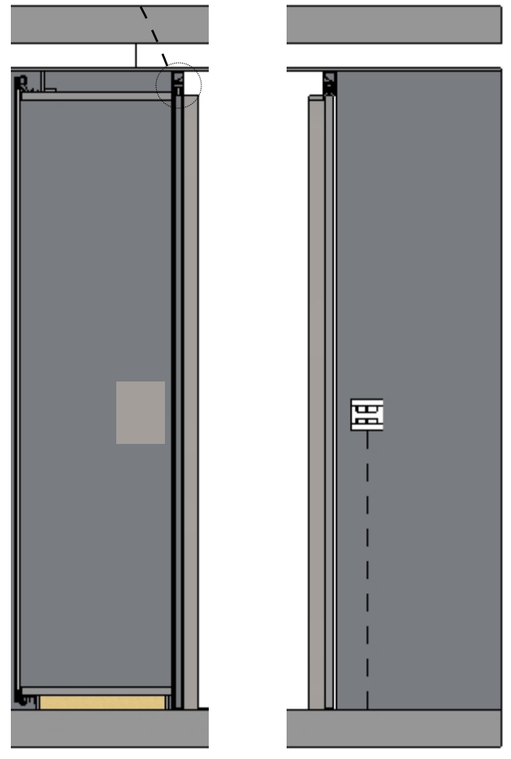

M6 - PORTA CORRER - CORTES

ESCALA 1:25

EMPÓRIO HASS ambientes planejados

contato.emporiohass@gmail.com
(61)99303-3151/98274-3709
Instagram: @emporiohass

ARQUITETO RESPONSÁVEL:
José Adalberto Meuren
CAU Nº 000A487848
(61)98274-3709
jmeuren@gmail.com

CONTEÚDO DA PRANCHA:
M6 - PORTA ACESSO ESCRITÓRIO

ESCALA:
Indicada na Prancha


CLIENTE:
Gisele Landim de Souza

ENDEREÇO:
SGCV LT 20 COND. NEW YORK
BLOCO A APT 101
Brasília

ARQUIVO:
Arq_Int_Gis_Park_Sul
REVISÃO Nº:
R00
DATA REVISÃO:
23-10-2024


OBSERVAÇÕES:
Consultar arquiteto em caso de dúvida e/ou alteração;
Conferir medidas no local;
Medidas em cota prevalecem sobre o desenho

FOLHA:

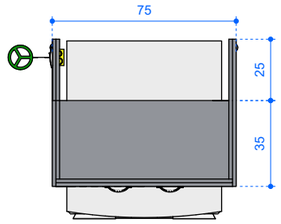


M7 - ARMÁRIO FREEZER- PLANTA


ESCALA 1:25

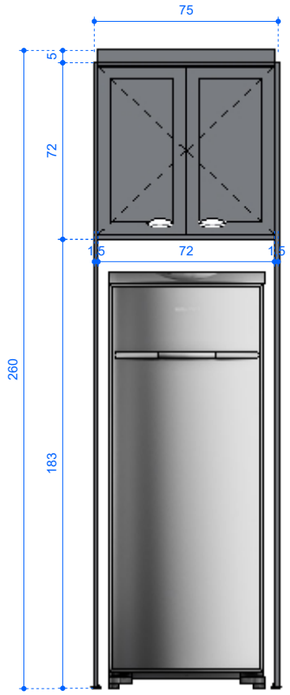

M7 - ARMÁRIO FREEZER- ELEVAÇÃO FRONTAL


ESCALA 1:25

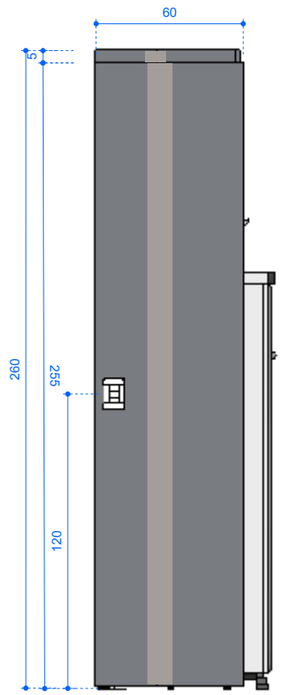

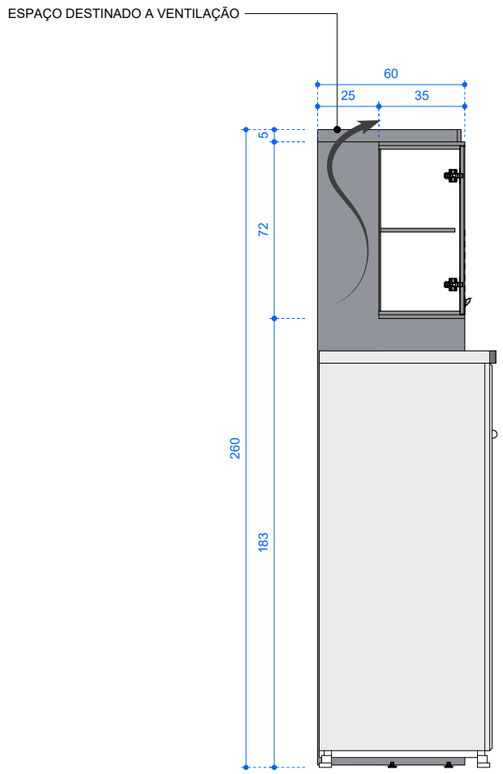

M7 - ARMÁRIO FREEZER- ELEVAÇÃO LATERAL

ESCALA 1:25

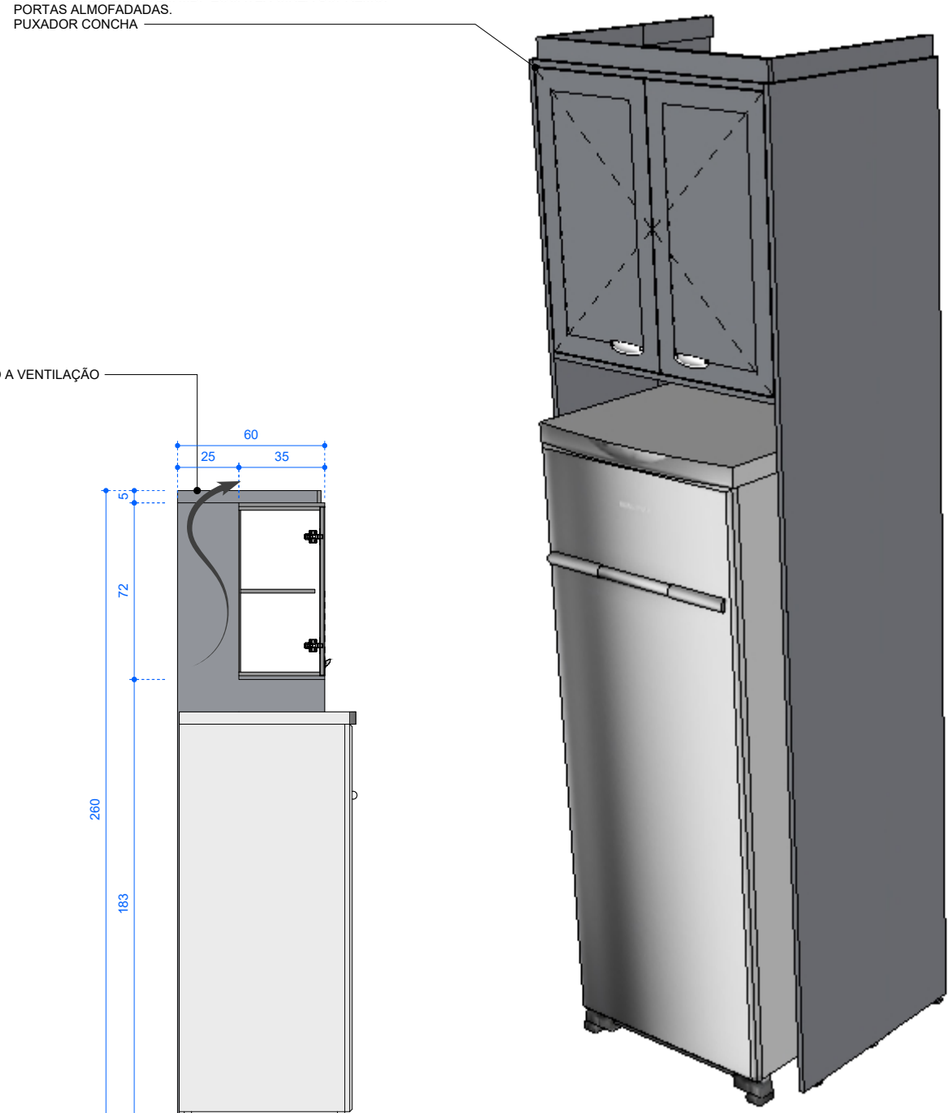

EMPÓRIO HASS ambientes planejados

contato.emporiohass@gmail.com
(61)99303-3151/98274-3709
Instagram: @emporiohass

ARQUITETO RESPONSÁVEL:
José Adalberto Meuren
CAU Nº 000A487848
(61)98274-3709
jmeuren@gmail.com

CONTEÚDO DA PRANCHA:
M7 - ARMÁRIO FREEZER

ESCALA:
Indicada na Prancha


CLIENTE:
Gisele Landim de Souza

ENDEREÇO:
SGCV LT 20 COND. NEW YORK
BLOCO A APT 101
Brasília

ARQUIVO:
Arq_Int_Gis_Park_Sul
REVISÃO Nº:
R00
DATA REVISÃO:
23-10-2024


OBSERVAÇÕES:
Consultar arquiteto em caso de dúvida e/ou alteração;
Conferir medidas no local;
Medidas em cota prevalecem sobre o desenho


FOLHA:

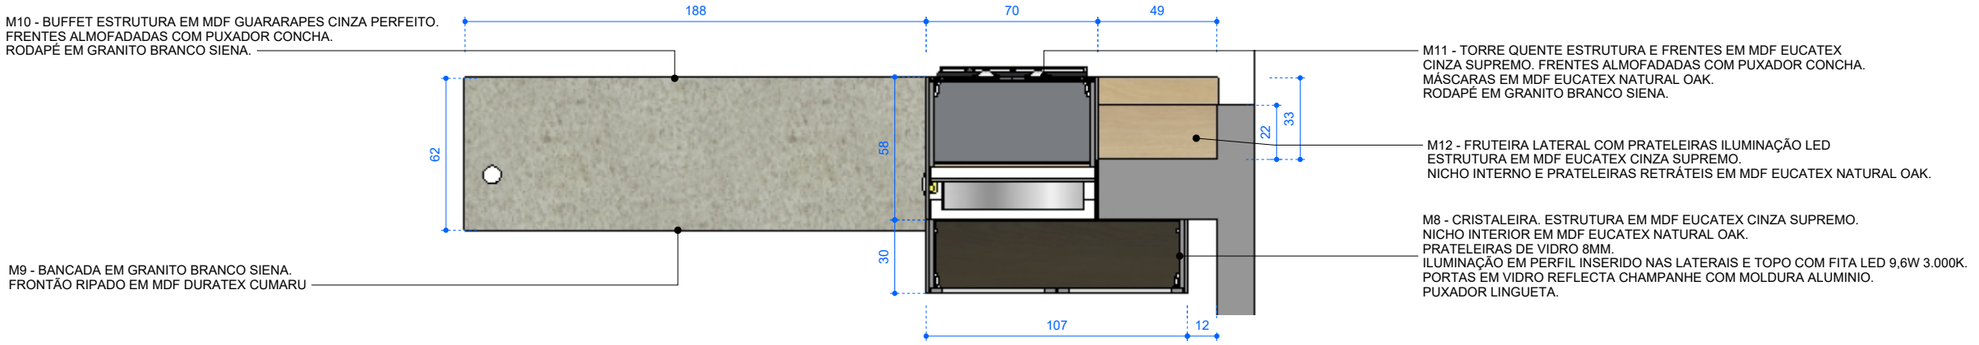


CRISTALEIRA - ILHA - TORRE QUENTE - FRUTEIRA - PLANTA

ESCALA 1:25

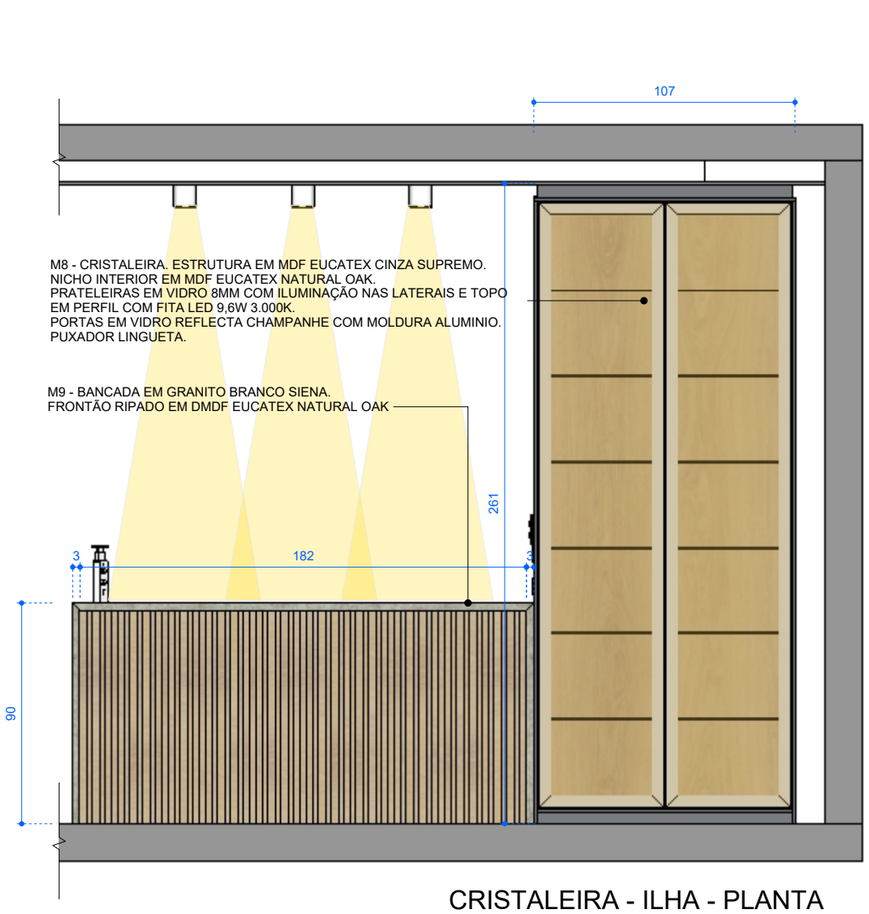

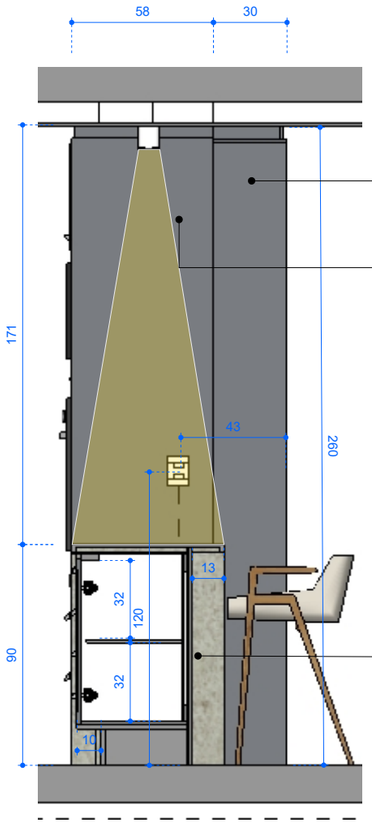

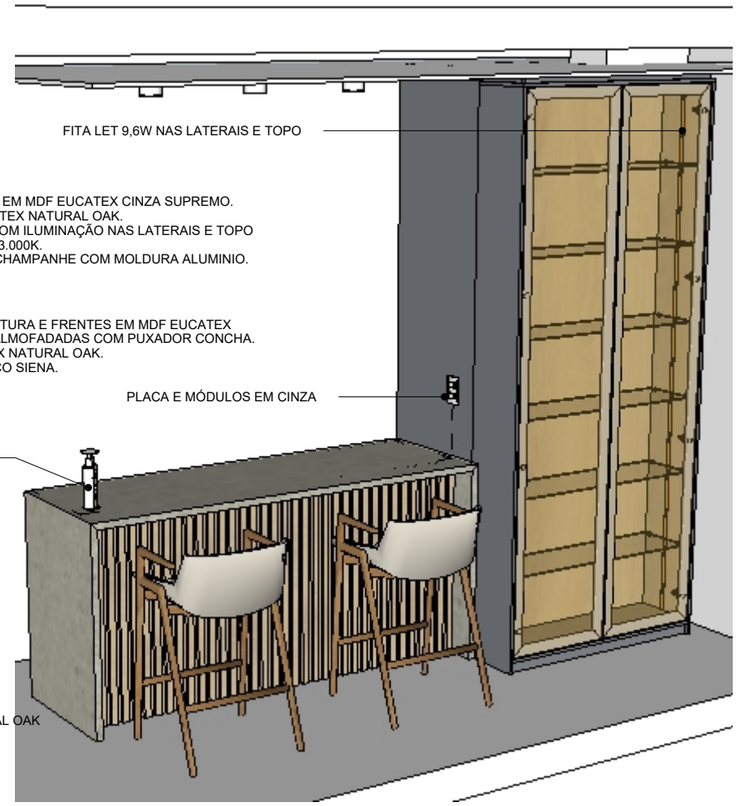

CRISTALEIRA - ILHA - PLANTA

ESCALA 1:25

EMPÓRIO HASS ambientes planejados

contato.emporiohass@gmail.com
(61)99303-3151/98274-3709
Instagram: @emporiohass

ARQUITETO RESPONSÁVEL:
José Adalberto Meuren
CAU Nº 000A487848
(61)98274-3709
jmeuren@gmail.com

CONTEÚDO DA PRANCHA:
M8/11 - SALA/COZINHA - VÁRIOS

ESCALA:
Indicada na Prancha


CLIENTE:
Gisele Landim de Souza

ENDEREÇO:
SGCV LT 20 COND. NEW YORK
BLOCO A APT 101
Brasília

ARQUIVO:
Arq_Int_Gis_Park_Sul
REVISÃO Nº:
R00
DATA REVISÃO:
23-10-2024


OBSERVAÇÕES:
Consultar arquiteto em caso de dúvida e/ou alteração;
Conferir medidas no local;
Medidas em cota prevalecem sobre o desenho


FOLHA:

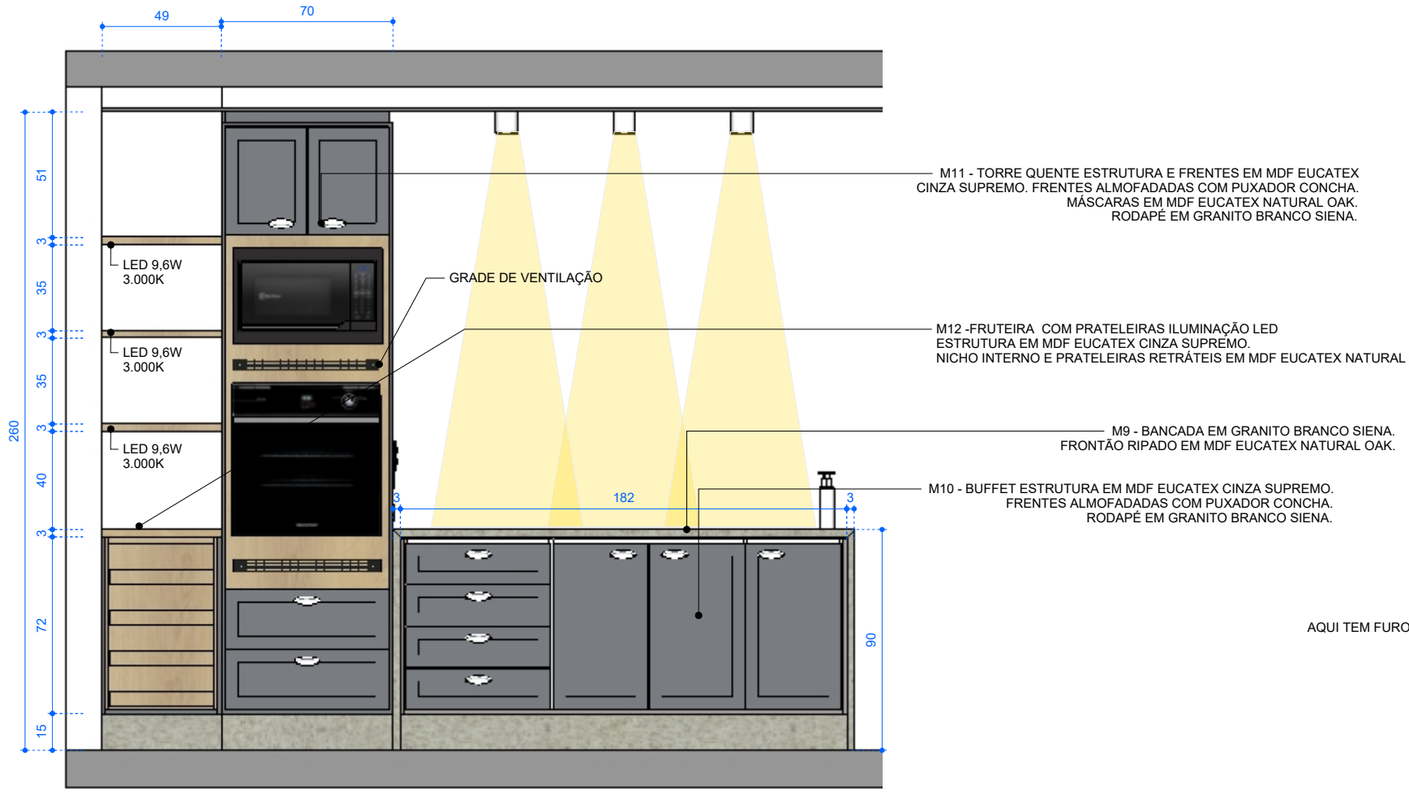

FRUTEIRA - TORRE QTE - BUFFET - ELEVAÇÃO

ESCALA 1:25

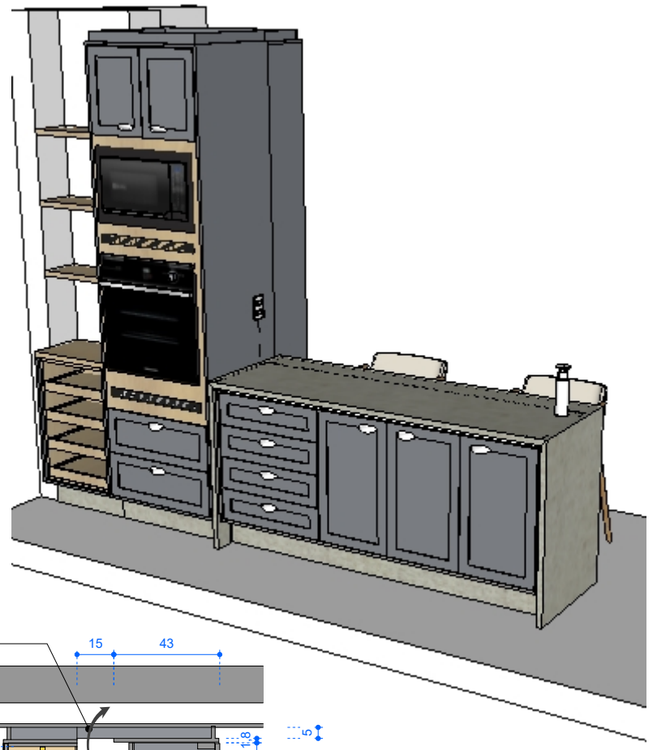

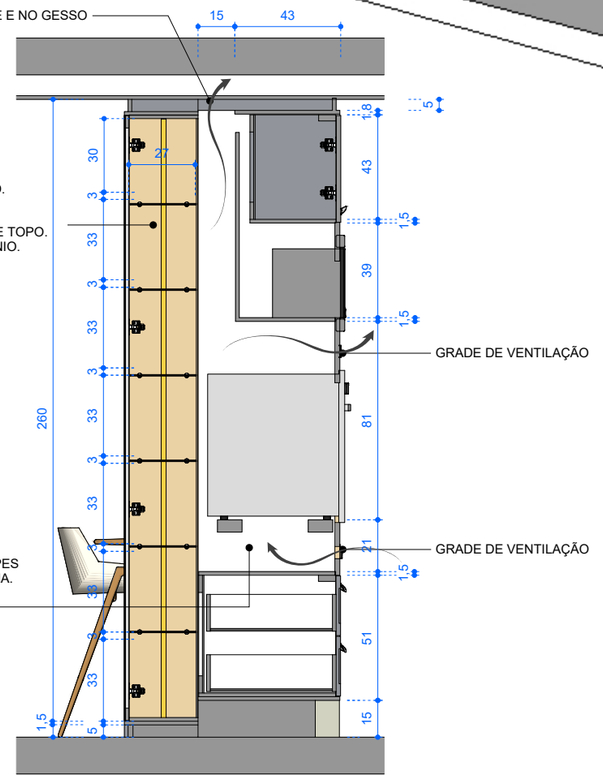

M8 - CRISTALEIRA. ESTRUTURA EM MDF EUCATEX CINZA SUPREMO.
NICHO INTERIOR EM MDF EUCATEX NATURAL OAK.
PRATELEIRAS DE VIDRO 8MM.
ILUMINAÇÃO EM PERFIL COM FITA LED 9,6W 3.000K NAS LATERAIS E TOPO.
PORTAS EM VIDRO REFLECTA CHAMPANHE COM MOLDURA ALUMINIO.
PUXADOR LINGUETA.

M11 - TORRE QUENTE ESTRUTURA E FRENTES EM MDF GUARARAPES
CINZA PERFEITO. FRENTES ALMOFADADAS COM PUXADOR CONCHA.
MÁSCARAS EM MDF DURATEX CUMARU.
RODAPÉ EM GRANITO BRANCO SIENA.

CRISTALEIRA - TORRE QTE - CORTE

ESCALA 1:25

EMPÓRIO HASS ambientes planejados

contato.emporiohass@gmail.com
(61)99303-3151/98274-3709
Instagram: @emporiohass

ARQUITETO RESPONSÁVEL:
José Adalberto Meuren
CAU Nº 000A487848
(61)98274-3709
jmeuren@gmail.com

CONTEÚDO DA PRANCHA:
M8/12 - SALA/COZINHA - VÁRIOS

ESCALA:
Indicada na Prancha


CLIENTE:
Gisele Landim de Souza

ENDEREÇO:
SGCV LT 20 COND. NEW YORK
BLOCO A APT 101
Brasília

ARQUIVO:
Arq_Int_Gis_Park_Sul
REVISÃO Nº:
R00
DATA REVISÃO:
23-10-2024


OBSERVAÇÕES:
Consultar arquiteto em caso de dúvida e/ou alteração;
Conferir medidas no local;
Medidas em cota prevalecem sobre o desenho


FOLHA:
8/24

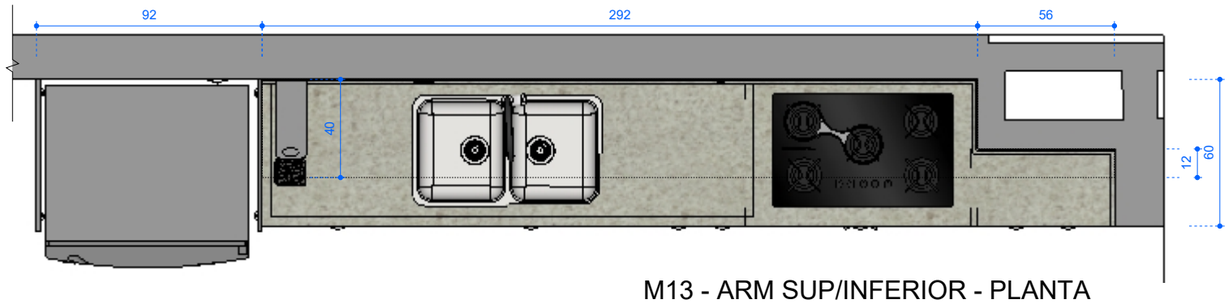

M13 - ARM SUP/INFERIOR - PLANTA


ESCALA 1:25

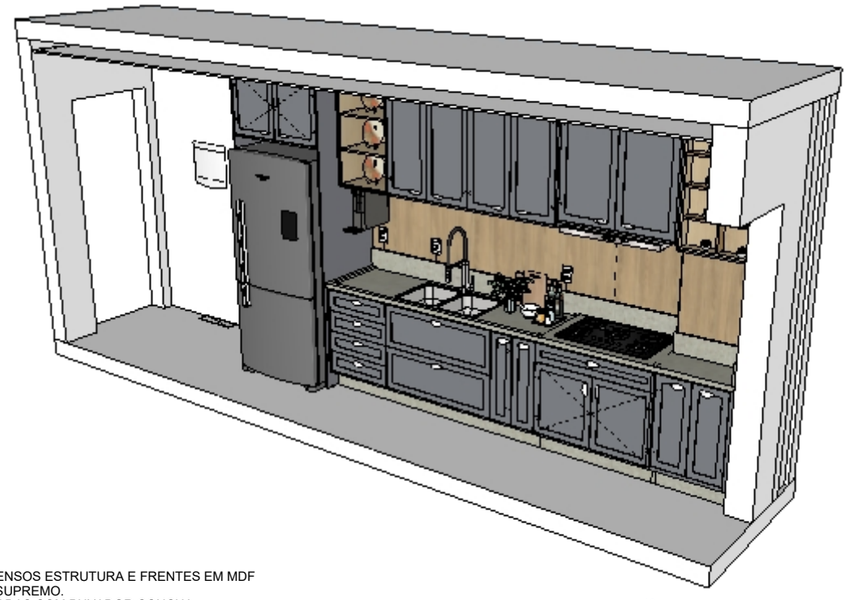

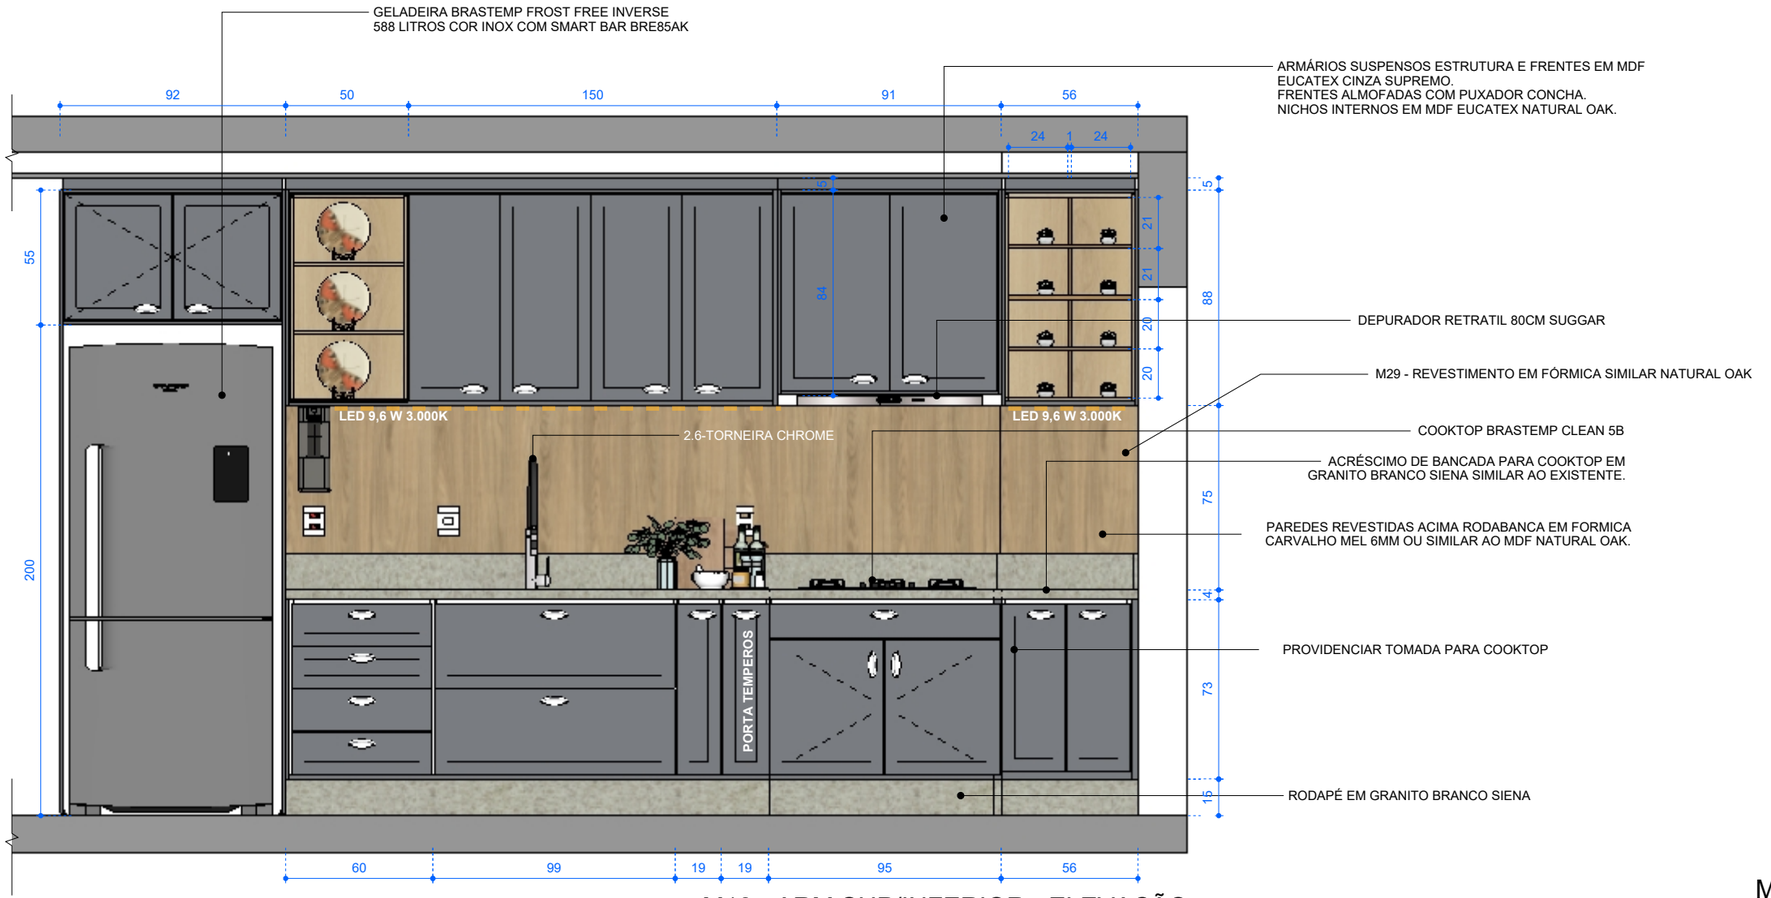

M13 - ARM SUP/INFERIOR - ELEVAÇÃO

ESCALA 1:25

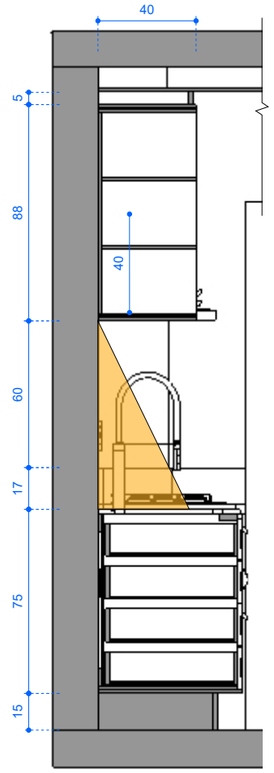

M13- ARM SUP/INFERIOR - CORTE

ESCALA 1:25

EMPÓRIO HASS ambientes planejados

contato.emporiohass@gmail.com
(61)99303-3151/98274-3709
Instagram: @emporiohass

ARQUITETO RESPONSÁVEL:
José Adalberto Meuren
CAU Nº 000A487848
(61)98274-3709
jmeuren@gmail.com

CONTEÚDO DA PRANCHA:
M13 - COZINHA - VÁRIOS

ESCALA:
Indicada na Prancha


CLIENTE:
Gisele Landim de Souza

ENDEREÇO:
SGCV LT 20 COND. NEW YORK
BLOCO A APT 101
Brasília

ARQUIVO:
Arq_Int_Gis_Park_Sul
REVISÃO Nº:
R00
DATA REVISÃO:
23-10-2024

OBSERVAÇÕES:
Consultar arquiteto em caso de dúvida e/ou alteração;
Conferir medidas no local;
Medidas em cota prevalecem sobre o desenho

FOLHA:
9/24

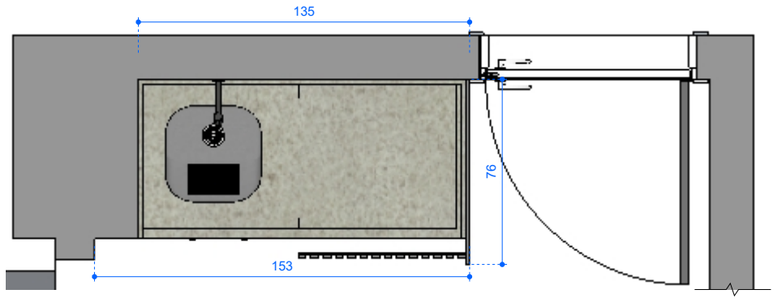

M14 - ARMÁRIO TANQUE E ML - PLANTA


ESCALA 1:25


VARAL DE TETO

ARMÁRIO SUSPENSO ESTRUTURA EM MDF EUCATEX CINZA SUPREMO.
PORTAS ALMOFADADAS COM PUXADOR CONCHA.
ARARA CROMADA NA PARTE INFERIOR

PORTA DE CORRER RIPADA PARCIALMENTE VAZADA - 01 FOLHA EM MDF EUCATEX NATURAL OAK.

ARMÁRIO INFERIOR ESTRUTURA E FRENTES EM MDF EUCATEX CINZA SUPREMO.
PORTAS ALMOFADADAS E PUXADOR CONCHA.
RODAPÉ EM GRANITO BRANCO SIENA.

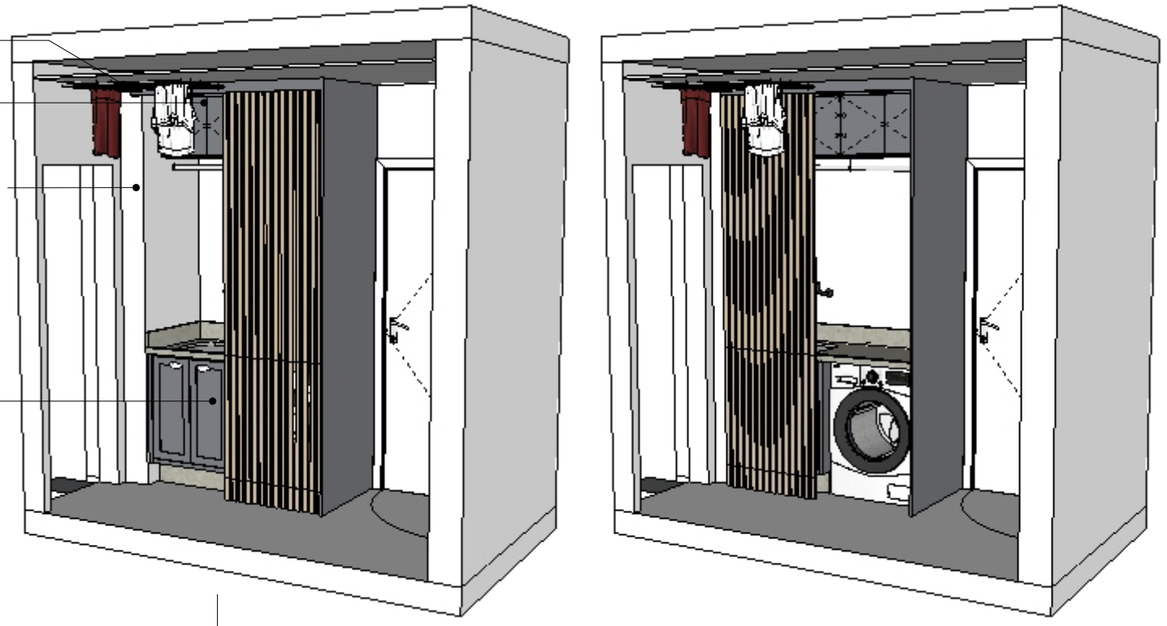


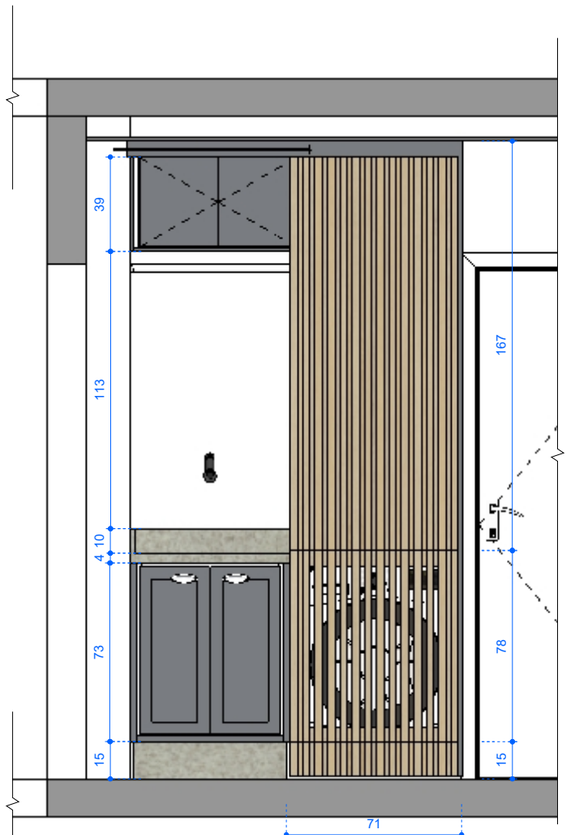

M14 - ARMÁRIO TANQUE E ML - ELEVAÇÃO


ESCALA 1:25


BANDÔ EM MDF EUCATEX CINZA SUPREMO

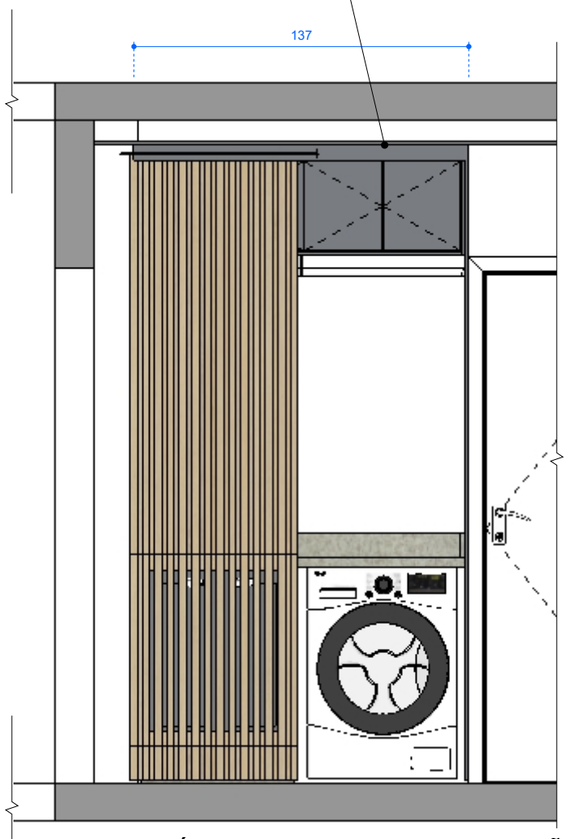

M14 - ARMÁRIO TANQUE E ML - ELEVAÇÃO

ESCALA 1:25

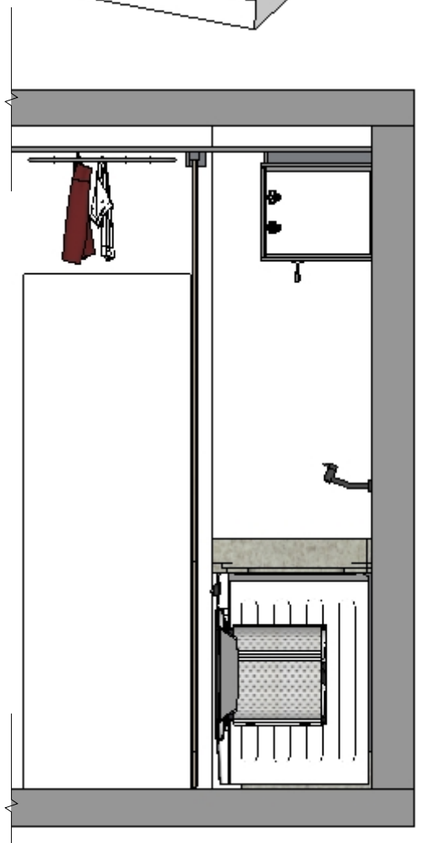

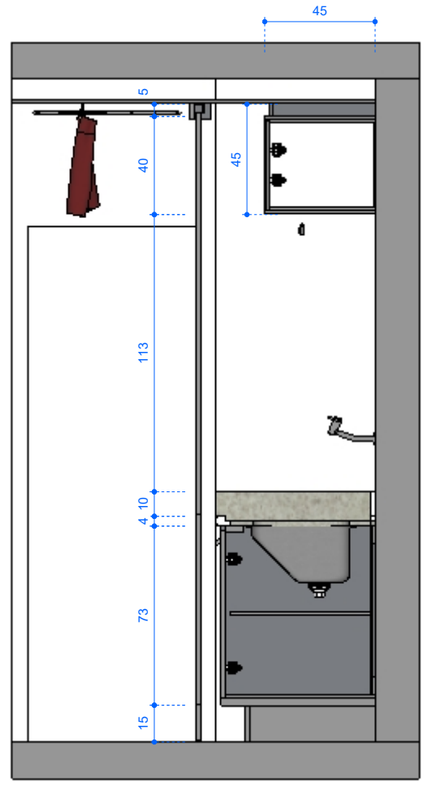

M14 - ARMÁRIO TANQUE E ML - CORTE

ESCALA 1:25

EMPÓRIO HASS ambientes planejados

contato.emporiohass@gmail.com
(61)99303-3151/98274-3709
Instagram: @emporiohass

ARQUITETO RESPONSÁVEL:
José Adalberto Meuren
CAU Nº 000A487848
(61)98274-3709
jmeuren@gmail.com

CONTEÚDO DA PRANCHA:
M14 - SERVIÇO - ARMÁRIO TANQUE E ML

ESCALA:
Indicada na Prancha


CLIENTE:
Gisele Landim de Souza

ENDEREÇO:
SGCV LT 20 COND. NEW YORK
BLOCO A APT 101
Brasília

ARQUIVO:
Arq_Int_Gis_Park_Sul
REVISÃO Nº:
R00
DATA REVISÃO:
23-10-2024


OBSERVAÇÕES:
Consultar arquiteto em caso de dúvida e/ou alteração;
Conferir medidas no local;
Medidas em cota prevalecem sobre o desenho

FOLHA:
10/24

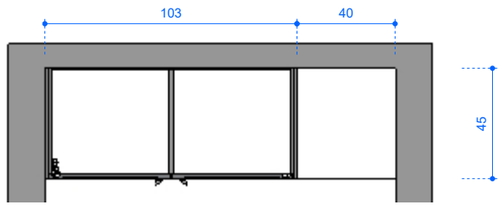

M16 - ARMÁRIO DESPENSA - PLANTA

ESCALA 1:25

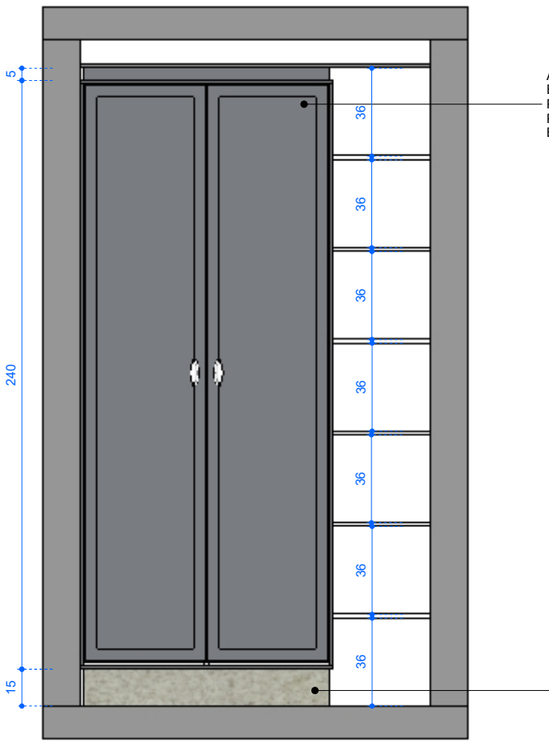


ARMÁRIO VASSOUREIRO ESTRUTURA E FRENTES EM MDF EUCATEX CINZA SUPREMO.
PORTAS ALMOFADADAS COM PUXADOR CONCHA.
PRATELEIRAS LATERAIS EM MDF DURATEX BRANCO DIAMANTE.

RODAPÉ EM GRANITO BRANCO SIENA

M16 - ARMÁRIO DESPENSA - ELEVAÇÃO

ESCALA 1:25

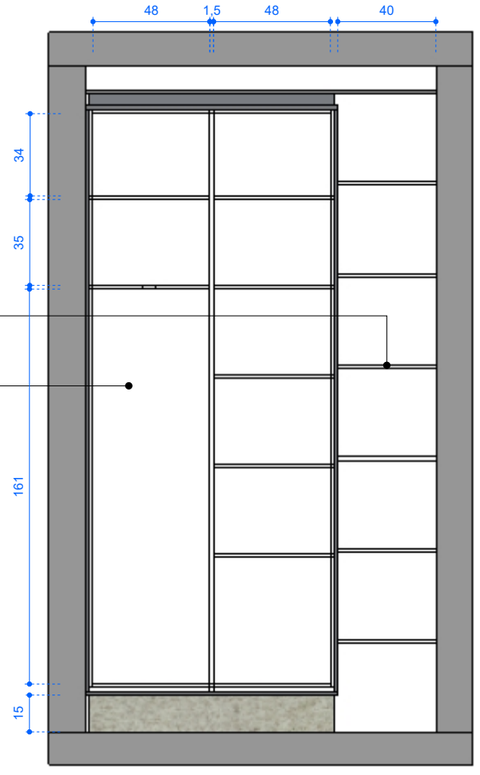

PRATELEIRAS PARA DESPENSA

VÃO PARA VASSOURAS, ESCADA E TÁBOA DE PASSAR


M16 - ARMÁRIO DESPENSA - ELEVAÇÃO

ESCALA 1:25

ARMÁRIO VASSOUREIRO ESTRUTURA E PORTAS EM MDF EUCATEX CINZA SUPREMO.
PORTAS ALMOFADADAS COM PUXADOR CONCHA

PRATELEIRAS EM MDF DURATEX BRANCO DIAMANTE

RODAPÉ EM GRANITO BRANCO SIENA

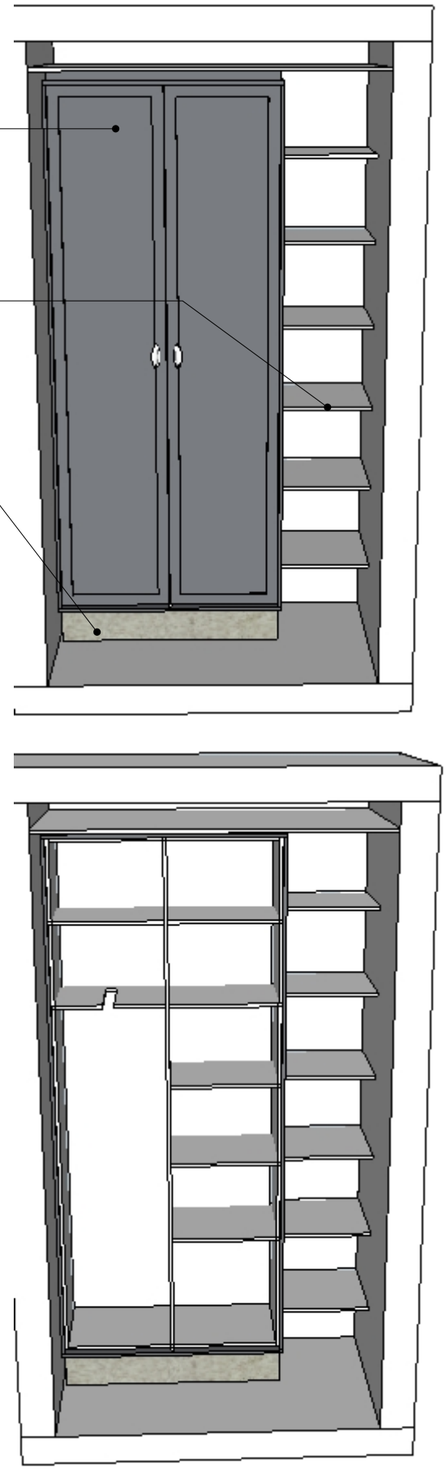

EMPÓRIO HASS ambientes planejados

contato.emporiohass@gmail.com
(61)99303-3151/98274-3709
Instagram: @emporiohass

ARQUITETO RESPONSÁVEL:
José Adalberto Meuren
CAU Nº 000A487848
(61)98274-3709
jmeuren@gmail.com

CONTEÚDO DA PRANCHA:
M16- SERVIÇO - ARMÁRIO DESPENSA

ESCALA:
Indicada na Prancha

CLIENTE:
Gisele Landim de Souza

ENDEREÇO:
SGCV LT 20 COND. NEW YORK
BLOCO A APT 101
Brasília


ARQUIVO:
Arq_Int_Gis_Park_Sul

REVISÃO Nº:
R00

DATA REVISÃO:
23-10-2024


OBSERVAÇÕES:
Consultar arquiteto em caso de dúvida e/ou alteração;
Conferir medidas no local;
Medidas em cota prevalecem sobre o desenho


FOLHA:
11/24

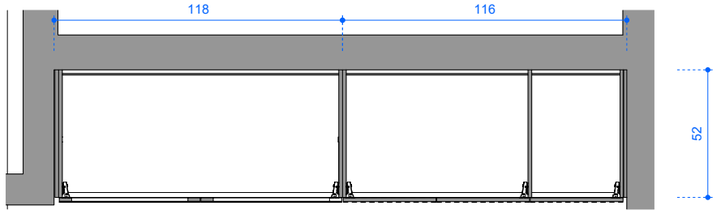

M15- ARMÁRIO CORREDOR - PLANTA

ESCALA 1:25

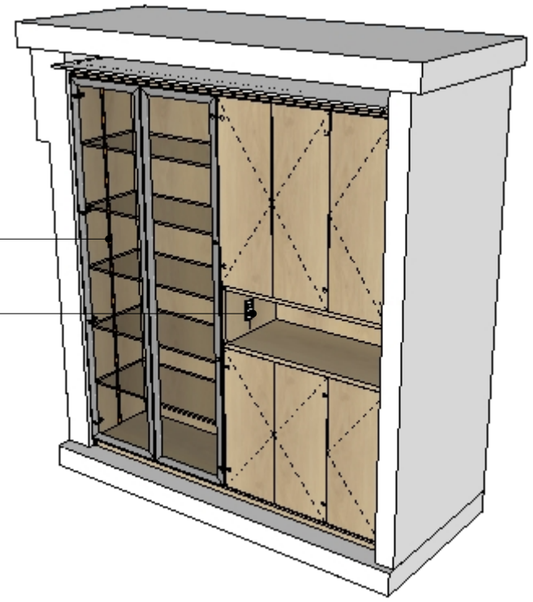

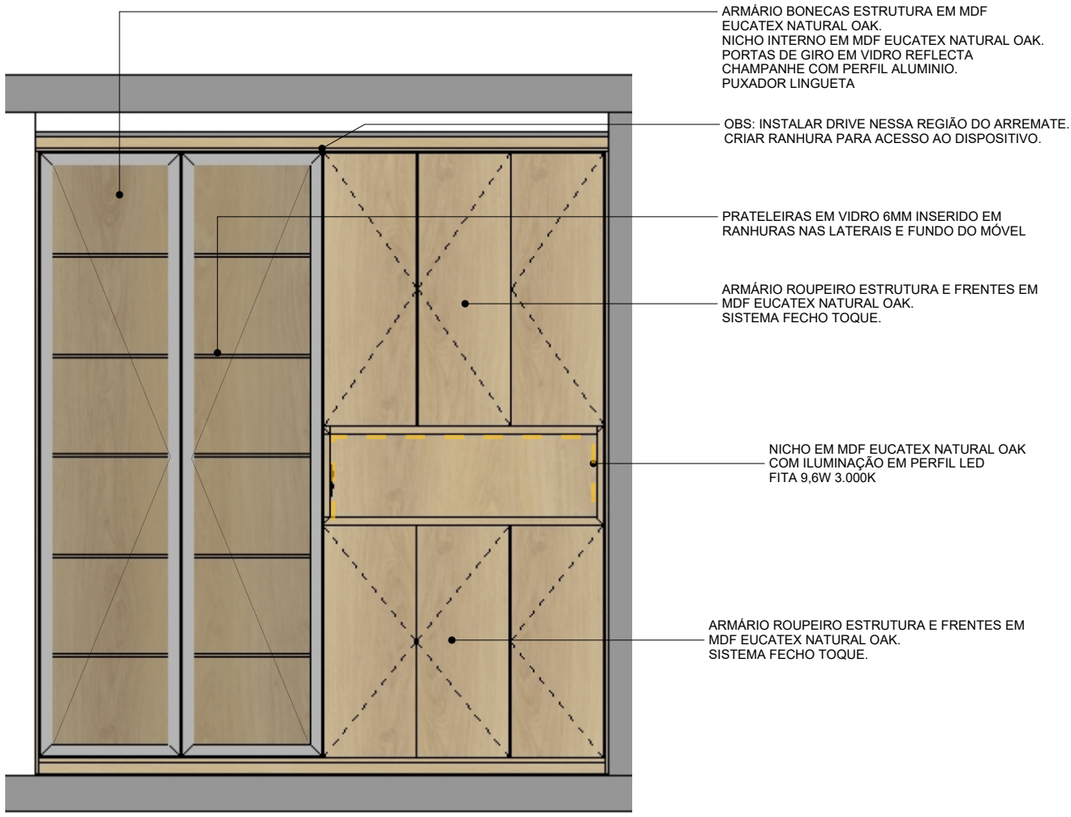


M15- ARMÁRIO CORREDOR - ELEVAÇÃO FECHADA

ESCALA 1:25



M15- ARMÁRIO CORREDOR - ELEVAÇÃO ABERTA

ESCALA 1:25

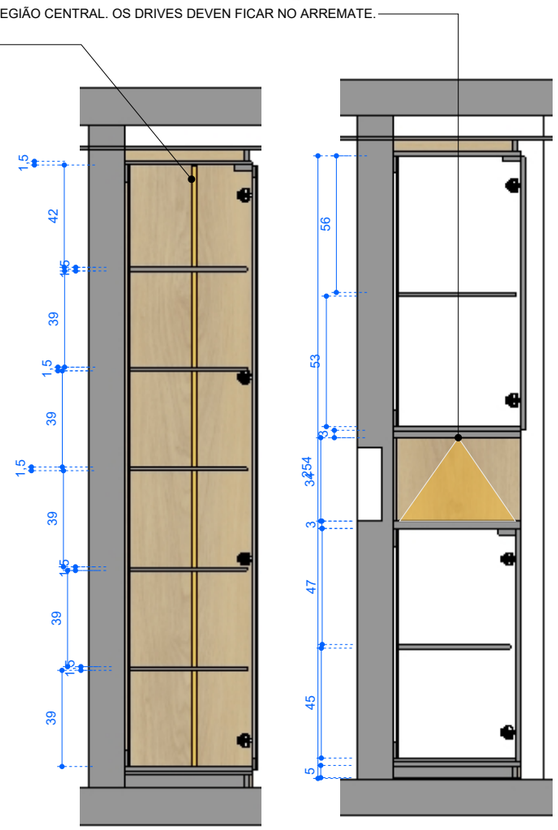

M15- ARMÁRIO CORREDOR - CORTES

ESCALA 1:25

EMPÓRIO HASS ambientes planejados
contato.emporiohass@gmail.com
(61)99303-3151/98274-3709
Instagram: @emporiohass

ARQUITETO RESPONSÁVEL:
José Adalberto Meuren
CAU Nº 000A487848
(61)98274-3709
jmeuren@gmail.com

CONTEÚDO DA PRANCHA:
M15 - ARMÁRIO CORREDOR

ESCALA:
Indicada na Prancha


CLIENTE:
Gisele Landim de Souza

ENDEREÇO:
SGCV LT 20 COND. NEW YORK
BLOCO A APT 101
Brasília

ARQUIVO:
Arq_Int_Gis_Park_Sul
REVISÃO Nº:
R00
DATA REVISÃO:
23-10-2024

OBSERVAÇÕES:
Consultar arquiteto em caso de dúvida e/ou alteração;
Conferir medidas no local;
Medidas em cota prevalecem sobre o desenho

FOLHA:
12/24

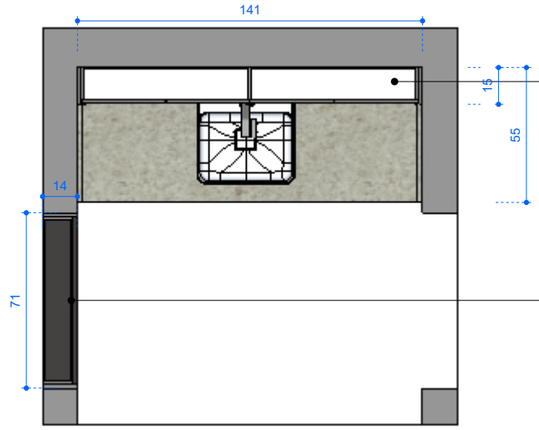



M21 - ARMÁRIO SUPERIOR ESTRUTURA EM MDF GUARARAPES NEBLINA.
PORTAS DE GIRO ESPELHADAS COM PUXADOR SOBRA INFERIOR.

M20 - NICHO ESTRUTURA E PRATELEIRAS EM MDF GUARARAPES NEBLINA.
FUNDO ESPELHADO.

WC ANTÔNIO - PLANTA

ESCALA 1:25

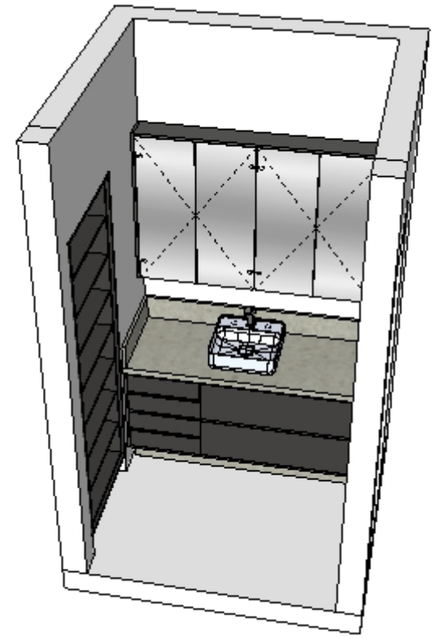

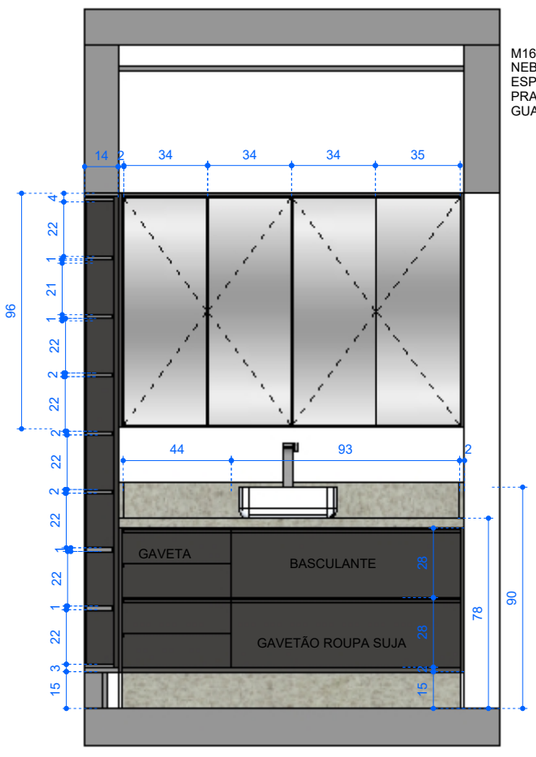

M16 - NICHO EM MDF GUARARAPES NEBLINA COM FUNDO ESPELHADO.
PRATELEIRAS EM MDF GUARARAPES NEBLINA


M17- ARMÁRIO SUSPENSO ESTRUTURA EM MDF GUARARAPES NEBLINA.
PORTAS DE GIRO ESPELHADAS COM PUXADOR SOBRA INFERIOR

M18 - ARMÁRIO INFERIOR ESTRUTURA EM MDF GUARARAPES NEBLINA.
FRENTES EM MDF GUARARAPES NOITE
PUXADOR CAVA USINADA

RODAPÉ EM GRANITO BRANCO SIENA

WC ANTÔNIO - ELEV. FECHADA

ESCALA 1:25

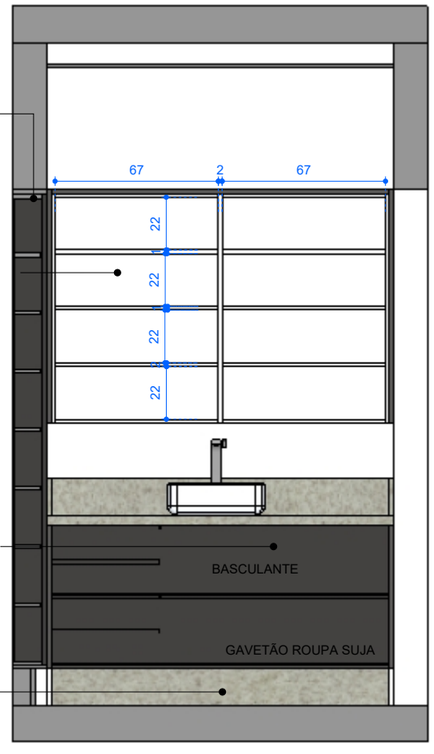

WC ANTÔNIO - ELEV. ABERTA


ESCALA 1:25

M16 - NICHO EM MDF GUARARAPES NEBLINA COM FUNDO ESPELHADO.
PRATELEIRAS EM MDF GUARARAPES NEBLINA.

M17- ARMÁRIO SUSPENSO ESTRUTURA EM MDF GUARARAPES NEBLINA.
PORTAS DE GIRO ESPELHADAS COM PUXADOR SOBRA INFERIOR

M18 - ARMÁRIO INFERIOR ESTRUTURA EM MDF GUARARAES NEBLINA.
FRENTES EM MDF GUARARAPES NOITE.
PUXADOR CAVA USINADA.

RODAPÉ EM GRANITO BRANCO SIENA

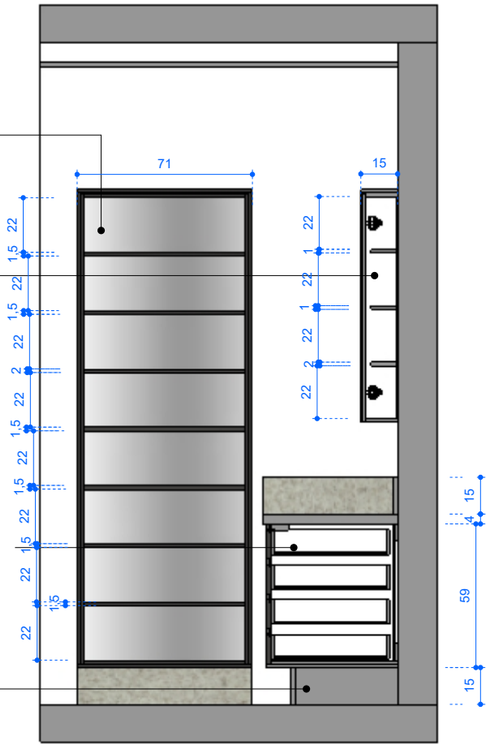

WC ANTÔNIO - CORTE

ESCALA 1:25

EMPÓRIO HASS ambientes planejados

contato.emporiohass@gmail.com
(61)99303-3151/98274-3709
Instagram: @emporiohass

ARQUITETO RESPONSÁVEL:
José Adalberto Meuren
CAU Nº 000A487848
(61)98274-3709
jmeuren@gmail.com

CONTEÚDO DA PRANCHA:
M16/18 - WC ANTONIO

ESCALA:
Indicada na Prancha


CLIENTE:
Gisele Landim de Souza

ENDEREÇO:
SGCV LT 20 COND. NEW YORK
BLOCO A APT 101
Brasília

ARQUIVO:
Arq_Int_Gis_Park_Sul
REVISÃO Nº:
R00
DATA REVISÃO:
23-10-2024

OBSERVAÇÕES:
Consultar arquiteto em caso de dúvida e/ou alteração;
Conferir medidas no local;
Medidas em cota prevalecem sobre o desenho


FOLHA:
13/24

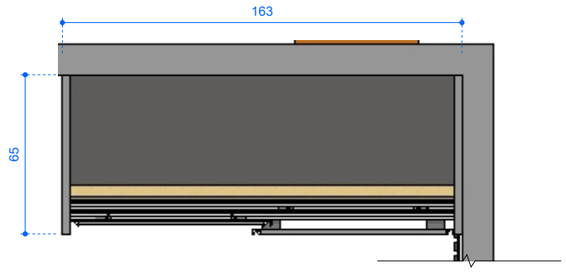


M19 - ARMÁRIO ANTÔNIO

ESCALA 1:25


M19 - ARMÁRIO ROUPEIRO ESTRUTURA EM MDF GUARARAPES NEBLINA.
PORTAS DE CORRER SENDO 01 LISA EM MDF GUARARAPES NOITE E 01 ESPELHADA.
PUXADOR ESTILO COLEGATTO

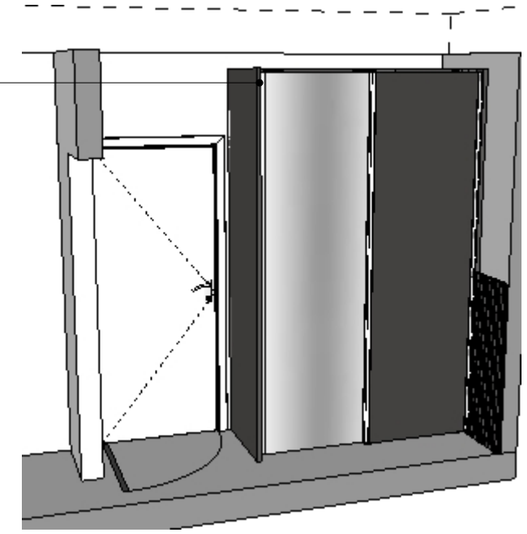

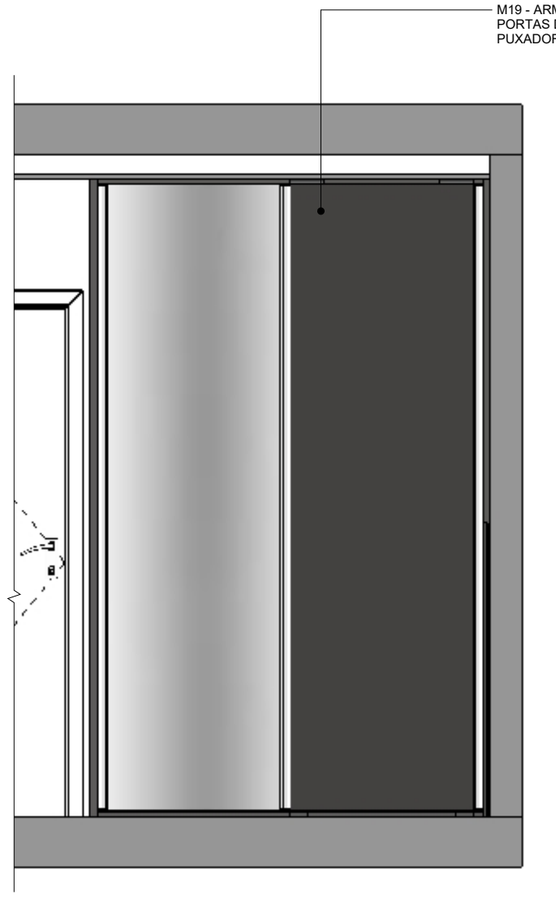


M19 - ARMÁRIO ANTÔNIO - ELEVAÇÃO FECHADA

ESCALA 1:25

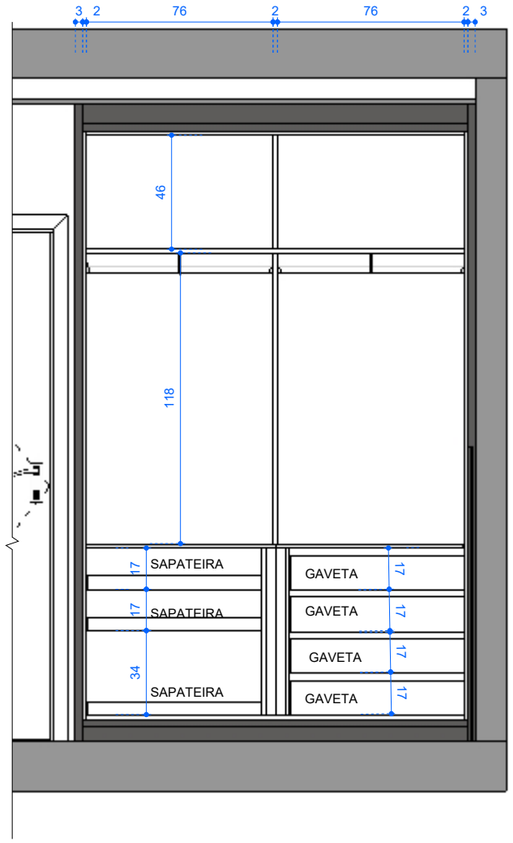

M19 - ARMÁRIO ANTÔNIO - ELEVAÇÃO ABERTA

ESCALA 1:25

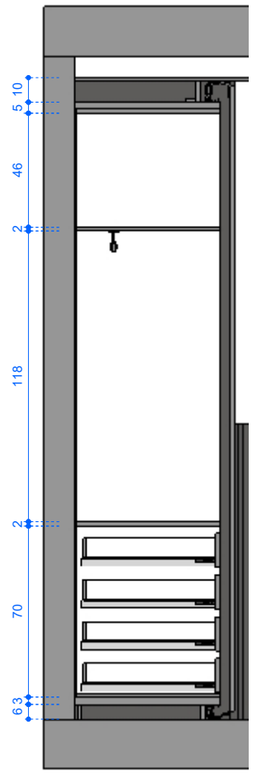

M19 - ARMÁRIO ANTÔNIO - CORTE

ESCALA 1:25

EMPÓRIO HASS ambientes planejados

contato.emporiohass@gmail.com
(61)99303-3151/98274-3709
Instagram: @emporiohass

ARQUITETO RESPONSÁVEL:
José Adalberto Meuren
CAU Nº 000A487848
(61)98274-3709
jmeuren@gmail.com

CONTEÚDO DA PRANCHA:
M19- QTO ANTÔNIO - ARMÁRIO

ESCALA:
Indicada na Prancha

CLIENTE:
Gisele Landim de Souza

ENDEREÇO:
SGCV LT 20 COND. NEW YORK
BLOCO A APT 101
Brasília


ARQUIVO:
Arq_Int_Gis_Park_Sul

REVISÃO Nº:
R00

DATA REVISÃO:
23-10-2024


OBSERVAÇÕES:
Consultar arquiteto em caso de dúvida e/ou alteração;
Conferir medidas no local;
Medidas em cota prevalecem sobre o desenho

FOLHA:
14/24

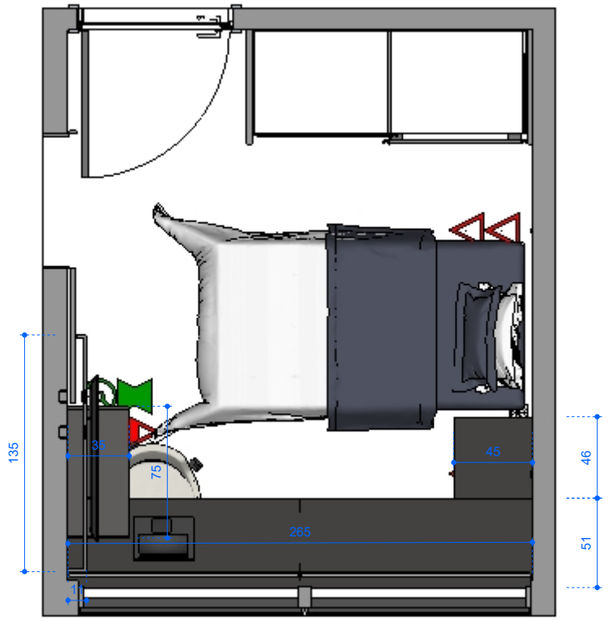


QUARTO ANTÔNIO - PLANTA

ESCALA 1:50

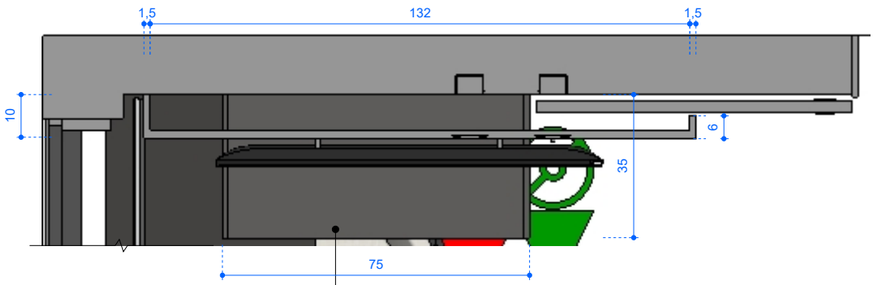

M21 - PAINEL TV E NICHO EM MDF GUARARAPES NEBLINA.

M21 - PAINEL TV E NICHO EM MDF GUARARAPES NEBLINA

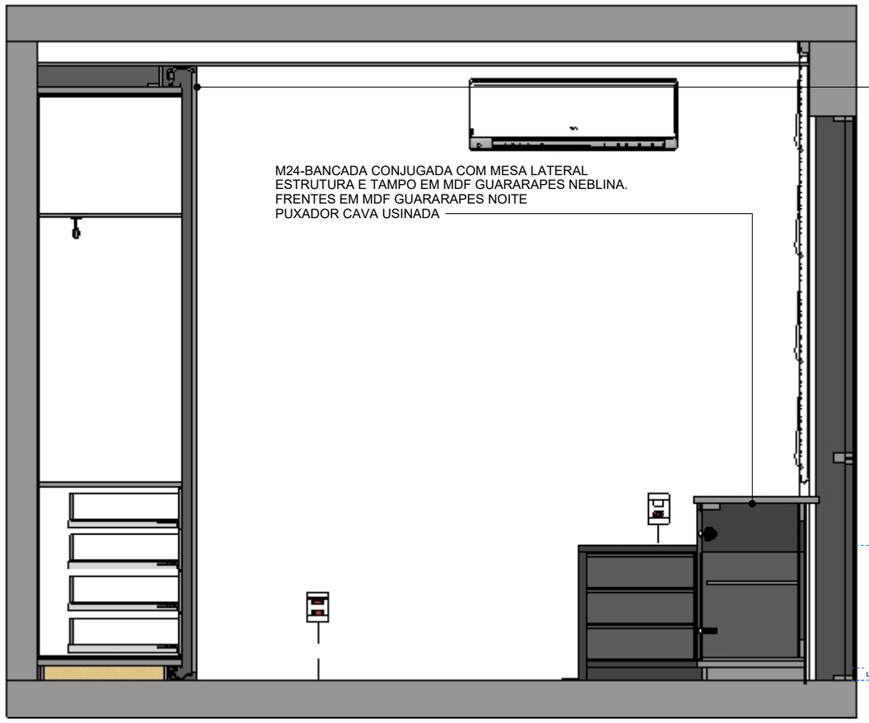

CABECEIRA - ELEVAÇÃO

ESCALA 1:25



BANCADA - ELEVAÇÃO

ESCALA 1:25

EMPÓRIO HASS ambientes planejados

contato.emporiohass@gmail.com
(61)99303-3151/98274-3709
Instagram: @emporiohass

ARQUITETO RESPONSÁVEL:
José Adalberto Meuren
CAU Nº 000A487848
(61)98274-3709
jmeuren@gmail.com

CONTEÚDO DA PRANCHA:
M19/20/21 - QTO ANTÔNIO - VÁRIOS

ESCALA:
Indicada na Prancha

CLIENTE:
Gisele Landim de Souza

ENDEREÇO:
SGCV LT 20 COND. NEW YORK
BLOCO A APT 101
Brasília


ARQUIVO:
Arq_Int_Gis_Park_Sul

REVISÃO Nº:
R00

DATA REVISÃO:
23-10-2024


OBSERVAÇÕES:
Consultar arquiteto em caso de dúvida e/ou alteração;
Conferir medidas no local;
Medidas em cota prevalecem sobre o desenho

FOLHA:
15/24

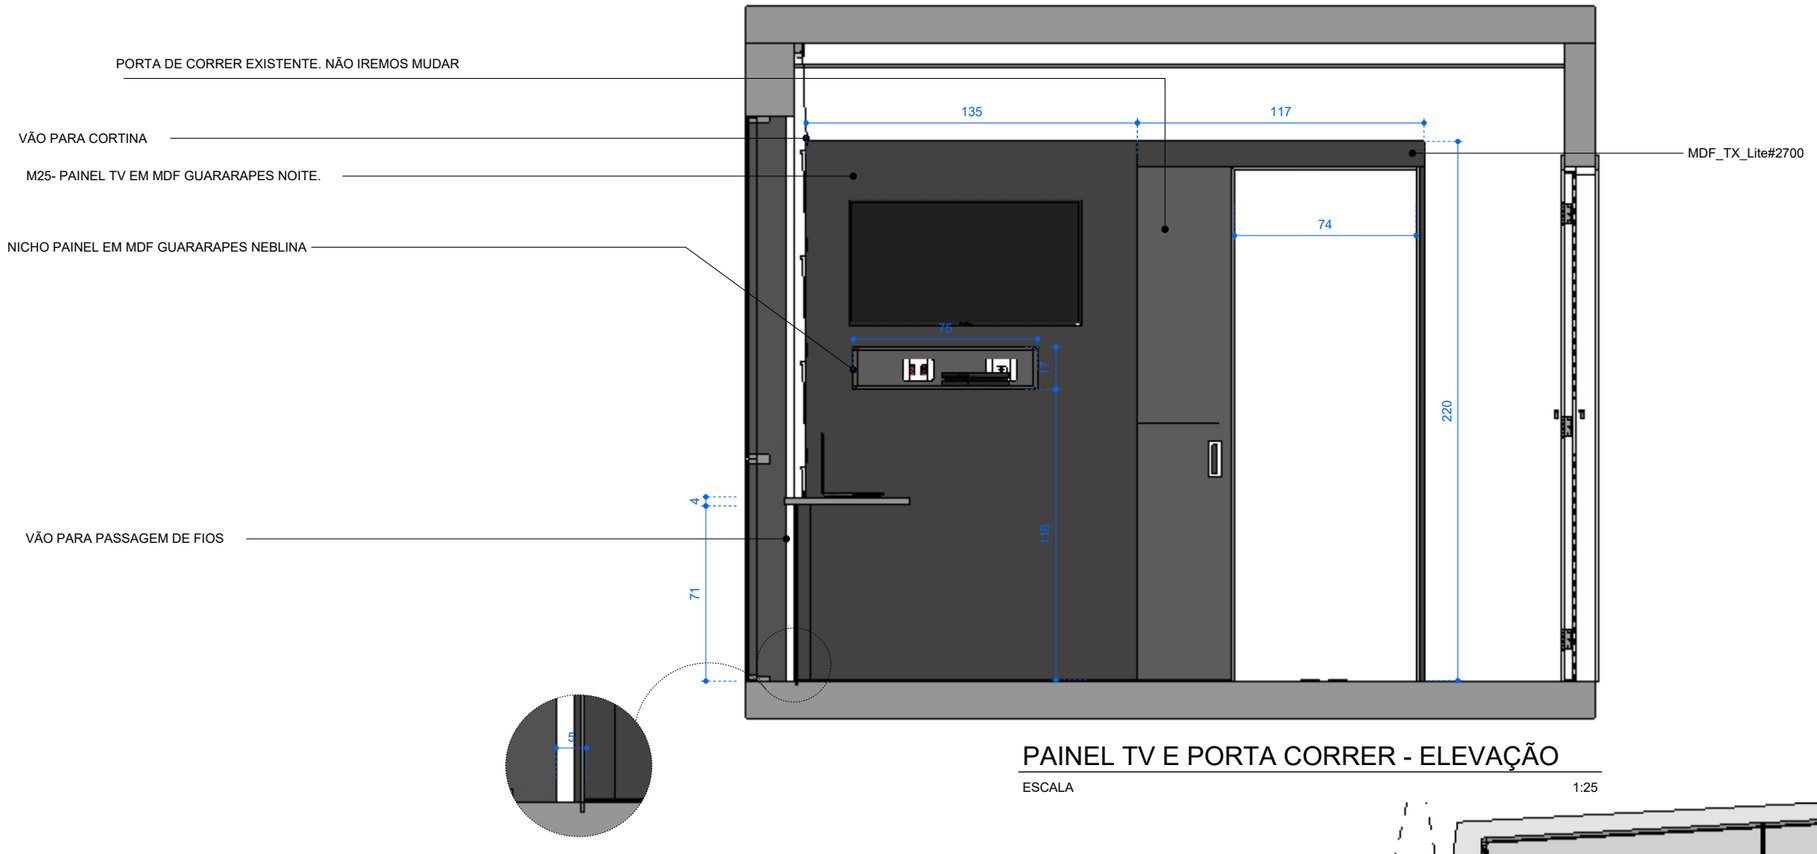

PAINEL TV E PORTA CORRER - ELEVAÇÃO

ESCALA 1:25

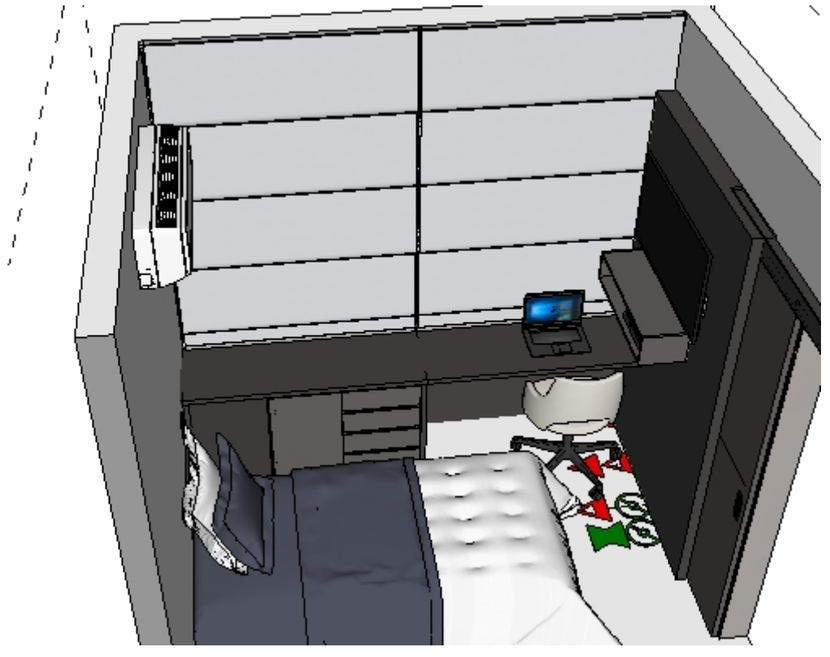

EMPÓRIO HASS ambientes planejados

contato.emporiohass@gmail.com
(61)99303-3151/98274-3709
Instagram: @emporiohass

ARQUITETO RESPONSÁVEL:
José Adalberto Meuren
CAU Nº 000A487848
(61)98274-3709
jmeuren@gmail.com

CONTEÚDO DA PRANCHA:
M21 - QTO ANTÔNIO - PAINEL

ESCALA:
Indicada na Prancha


CLIENTE:
Gisele Landim de Souza

ENDEREÇO:
SGCV LT 20 COND. NEW YORK
BLOCO A APT 101
Brasília

ARQUIVO:
Arq_Int_Gis_Park_Sul
REVISÃO Nº:
R00
DATA REVISÃO:
23-10-2024

OBSERVAÇÕES:
Consultar arquiteto em caso de dúvida e/ou alteração;
Conferir medidas no local;
Medidas em cota prevalecem sobre o desenho

FOLHA:
16/24

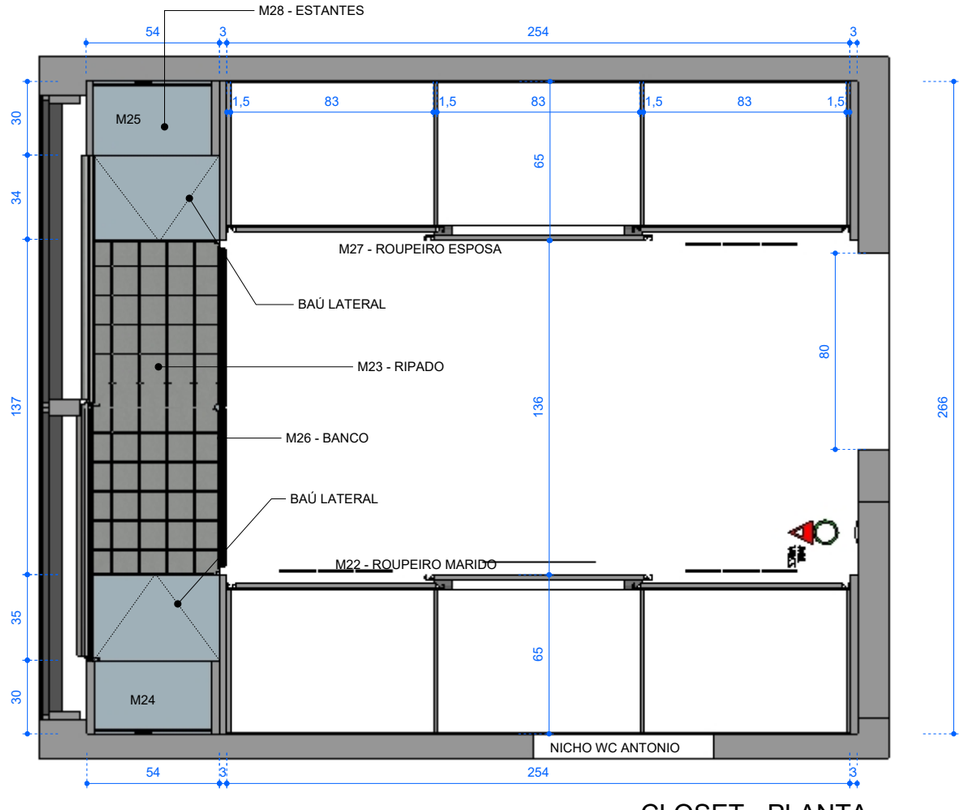

CLOSET - PLANTA

ESCALA 1:25




M22- ARMÁRIO ROUPEIRO ESTRUTURA EM MDF
DURATEX AZUL ASTRAL.
PORTAS DE CORRER LISAS COM TRILHO EMBUTIDO
SENDO 02 EM MDF EUCATEX NATURAL OAK E 01 ESPELHADA.
PUXADOR ESTILO COLEGATTO

M23 - RIPADO EM DURATEX AZUL ASTRAL COM 01 PERFIL LED
FITA LED 9,6W 3.000K


M24 - ESTANTE ESTRUTURA E PRATELEIRAS
EM MDF DURATEX AZUL ASTRAL
FUNDO EM MDF EUCATEX NATURAL OAK

M26 - BANCO TODO EM MDF DURATEX AZUL ASTRAL
COM BAU NAS LATERAIS E GAVETÕES NA FRENTE.
PUXADOR EM CAVA USINADA.
ALMOFADA EM FUTTON A ESCOLHER

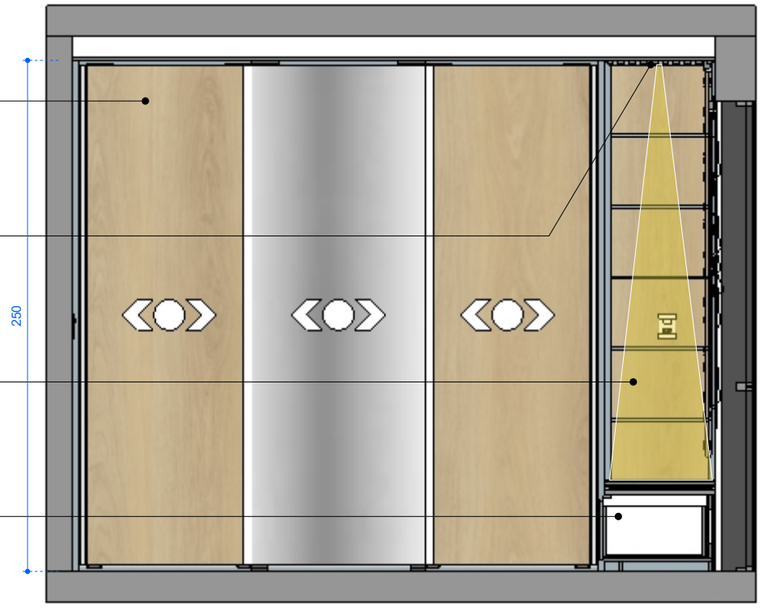

CLOSET - ROUPEIRO MARIDO - ELEVAÇÃO FECHADA

ESCALA 1:25

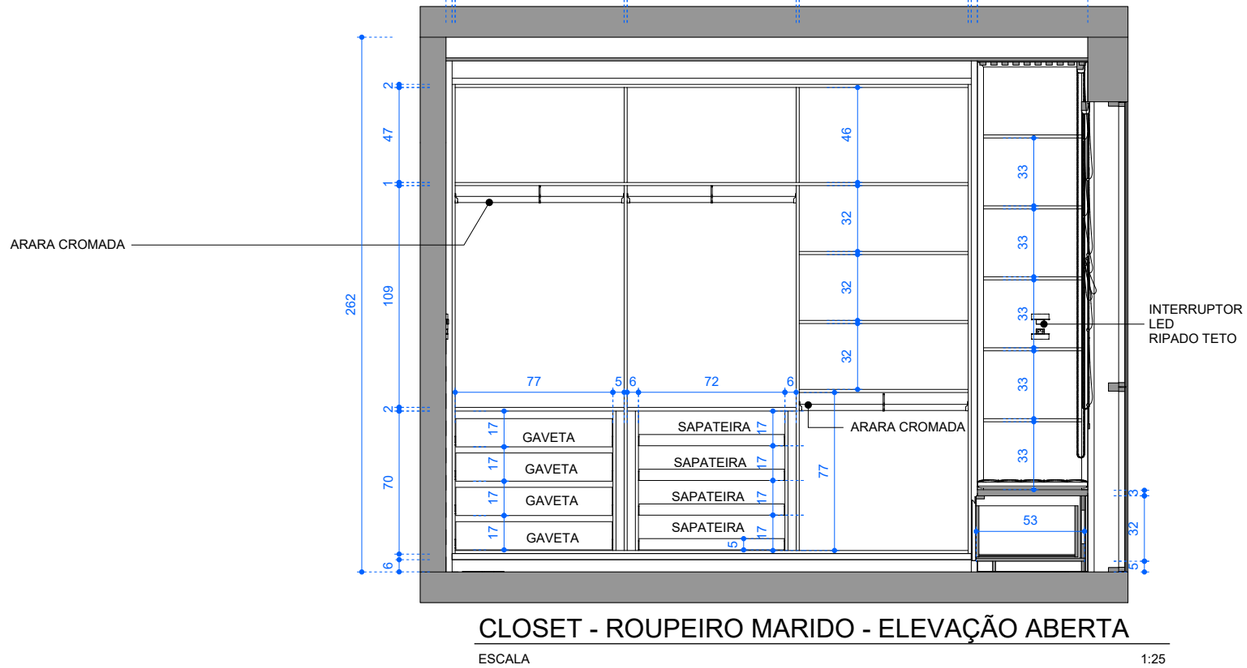

CLOSET - ROUPEIRO MARIDO - ELEVAÇÃO ABERTA

ESCALA 1:25

EMPÓRIO HASS ambientes planejados

contato.emporiohass@gmail.com
(61)99303-3151/98274-3709
Instagram: @emporiohass

ARQUITETO RESPONSÁVEL:
José Adalberto Meuren
CAU Nº 000A487848
(61)98274-3709
jmeuren@gmail.com

CONTEÚDO DA PRANCHA:
M22/M26 - CLOSET

ESCALA:
Indicada na Prancha


CLIENTE:
Gisele Landim de Souza

ENDEREÇO:
SGCV LT 20 COND. NEW YORK
BLOCO A APT 101
Brasília

ARQUIVO:
Arq_Int_Gis_Park_Sul
REVISÃO Nº:
R00
DATA REVISÃO:
23-10-2024


OBSERVAÇÕES:
Consultar arquiteto em caso de dúvida e/ou alteração;
Conferir medidas no local;
Medidas em cota prevalecem sobre o desenho

FOLHA:
17/24

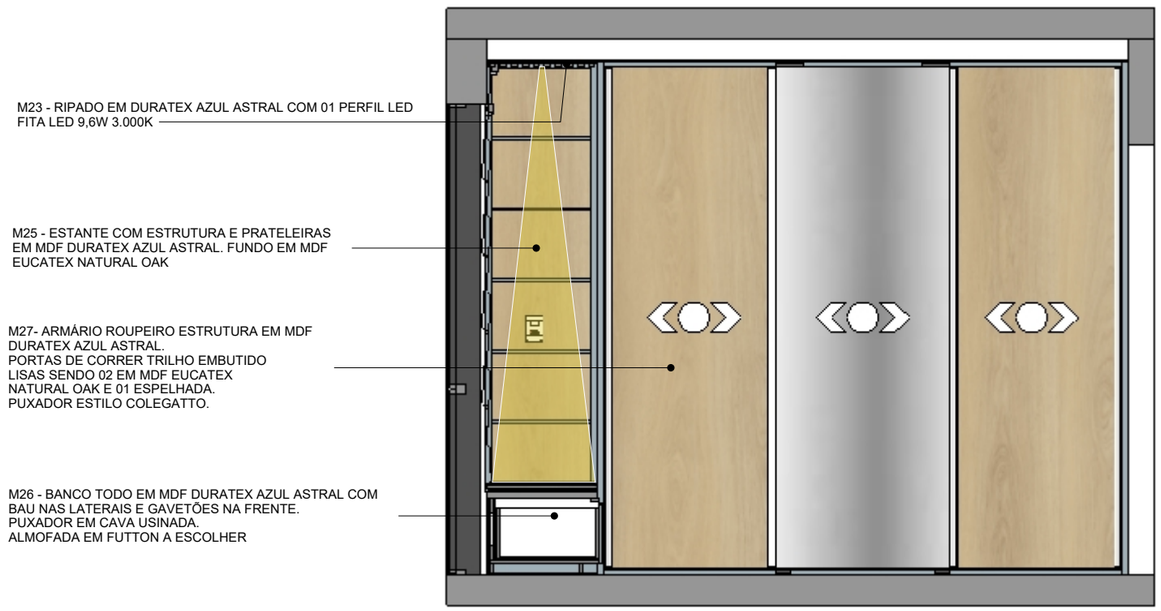


CLOSET - ROUPEIRO ESPOSA - ELEVAÇÃO FECHADA

ESCALA 1:30

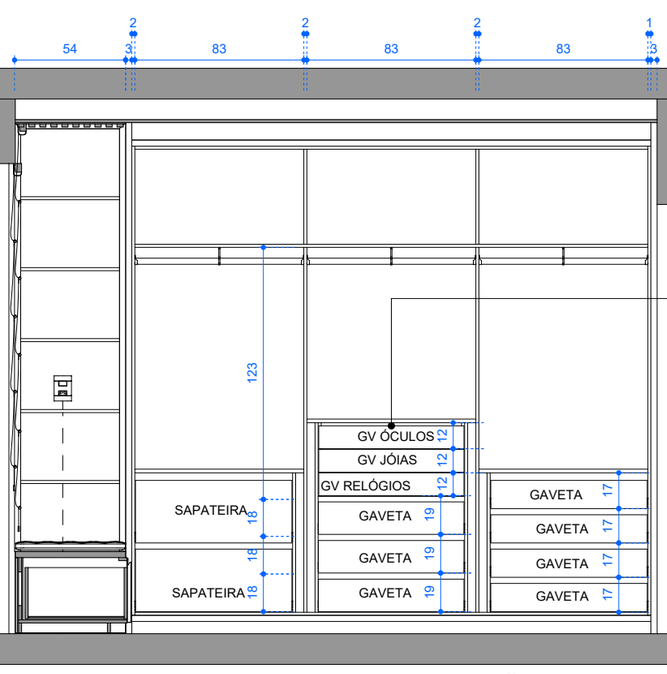


CLOSET - ROUPEIRO ESPOSA - ELEVAÇÃO ABERTA

ESCALA 1:30

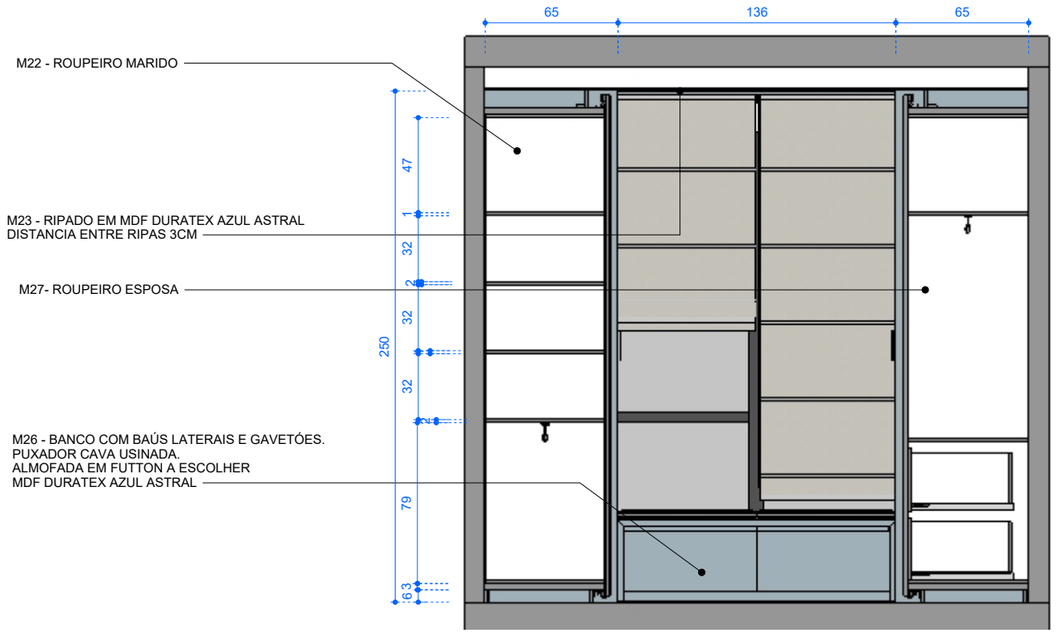

CLOSET - CORTE ARMÁRIOS

ESCALA 1:30

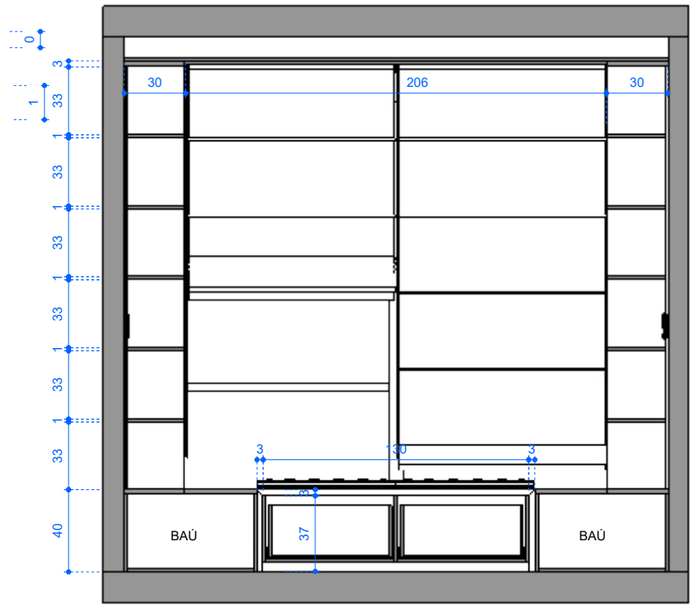

CLOSET - CORTE PRATELEIRAS ESTANTES E BANCO

ESCALA 1:30

EMPÓRIO HASS ambientes planejados

contato.emporiohass@gmail.com
(61)99303-3151/98274-3709
Instagram: @emporiohass

ARQUITETO RESPONSÁVEL:
José Adalberto Meuren
CAU Nº 000A487848
(61)98274-3709
jmeuren@gmail.com

CONTEÚDO DA PRANCHA:
M22/M27 - CLOSET

ESCALA:
Indicada na Prancha


CLIENTE:
Gisele Landim de Souza

ENDEREÇO:
SGCV LT 20 COND. NEW YORK
BLOCO A APT 101
Brasília

ARQUIVO:
Arq_Int_Gis_Park_Sul
REVISÃO Nº:
R00
DATA REVISÃO:
23-10-2024


OBSERVAÇÕES:
Consultar arquiteto em caso de dúvida e/ou alteração;
Conferir medidas no local;
Medidas em cota prevalecem sobre o desenho


FOLHA:
18/24

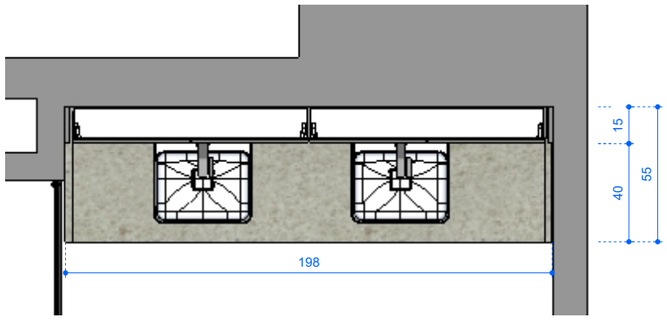

M28/M29 - WC CASAL - PLANTA


ESCALA 1:25

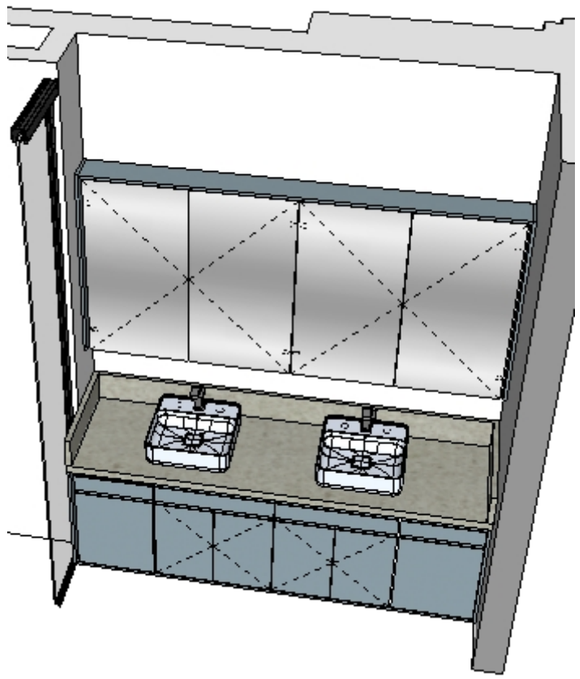

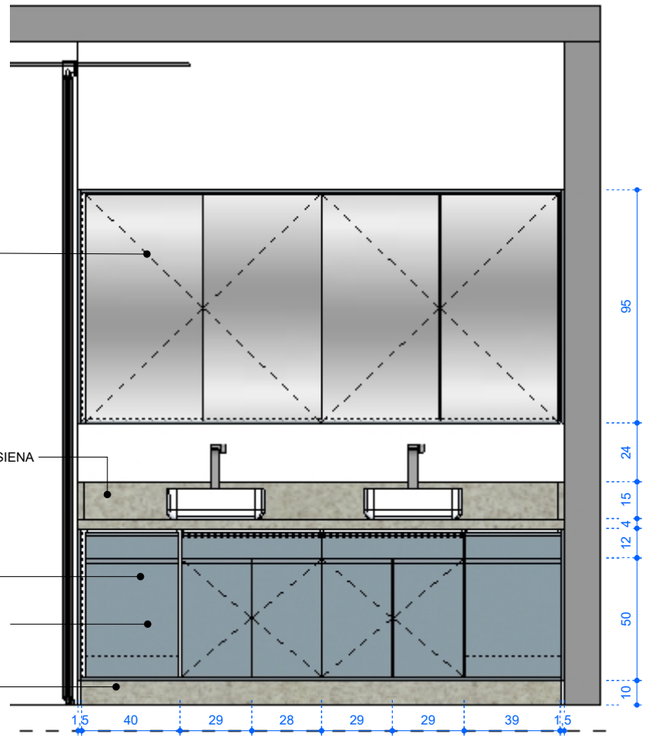


M28/M29 - WC CASAL - ELEVAÇÃO FECHADA

ESCALA 1:25

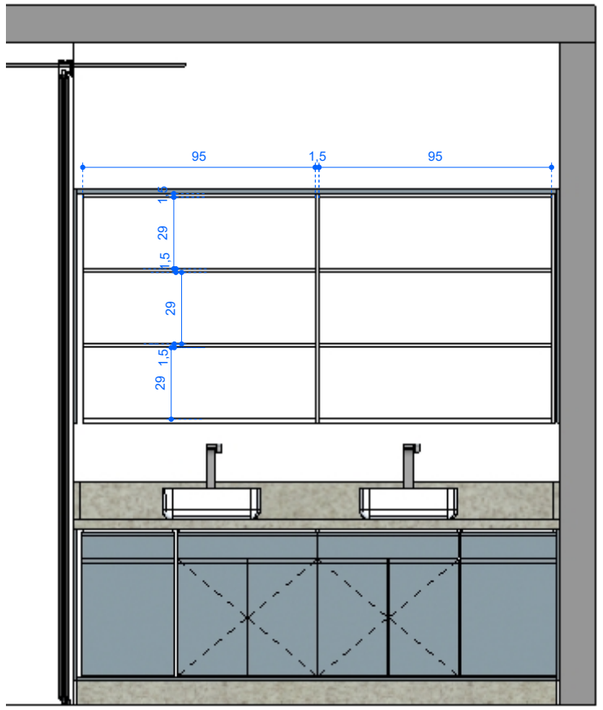

M28/M29 - WC CASAL - ELEVAÇÃO ABERTA

ESCALA 1:25

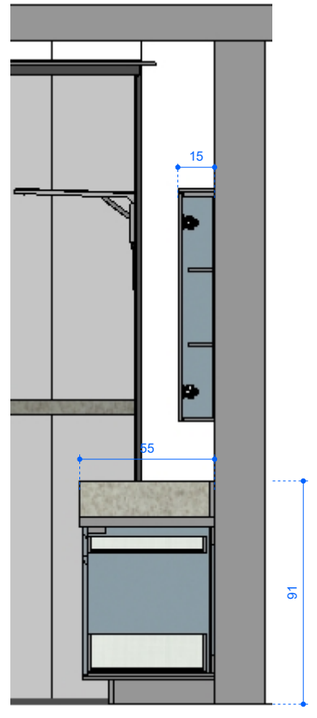

M28/M29 - WC CASAL - CORTE

ESCALA 1:25

EMPÓRIO HASS ambientes planejados

contato.emporiohass@gmail.com
(61)99303-3151/98274-3709
Instagram: @emporiohass

ARQUITETO RESPONSÁVEL:
José Adalberto Meuren
CAU Nº 000A487848
(61)98274-3709
jmeuren@gmail.com

CONTEÚDO DA PRANCHA:
M28/M29 - WC CASAL

ESCALA:
Indicada na Prancha

CLIENTE:
Gisele Landim de Souza


ENDEREÇO:
SGCV LT 20 COND. NEW YORK
BLOCO A APT 101
Brasília

ARQUIVO:
Arq_Int_Gis_Park_Sul
REVISÃO Nº:
R00
DATA REVISÃO:
23-10-2024

OBSERVAÇÕES:
Consultar arquiteto em caso de dúvida e/ou alteração;
Conferir medidas no local;
Medidas em cota prevalecem sobre o desenho


FOLHA:
19/24


OBS: O ITEM M31 ESTÁ DESCRITO NA PRANCHA Nº 09

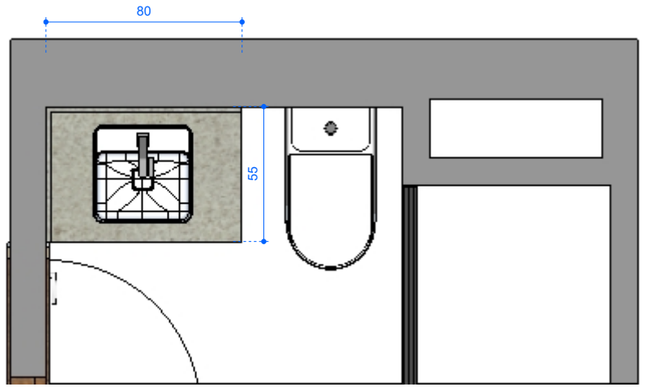

M31/32- ARMÁRIOS WC ARTHUR - PLANTA


ESCALA 1:25

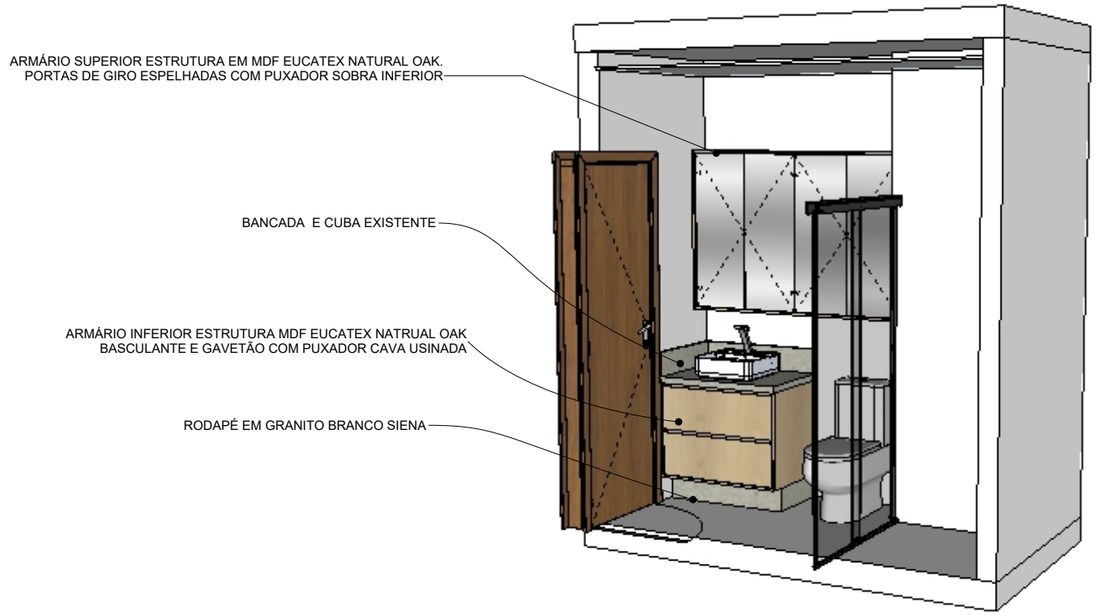

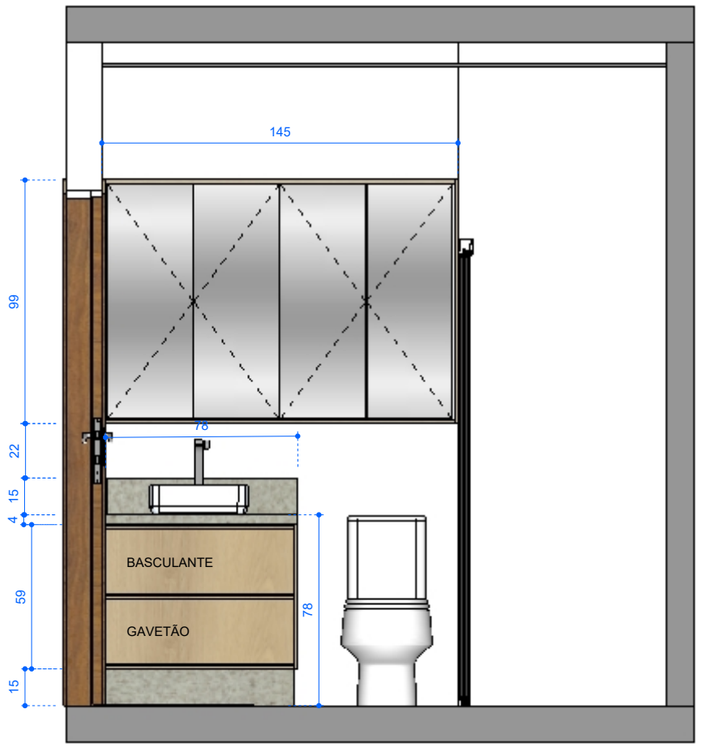


M31/32- ARMÁRIOS WC ARTHUR - ELEVAÇÃO

ESCALA 1:25

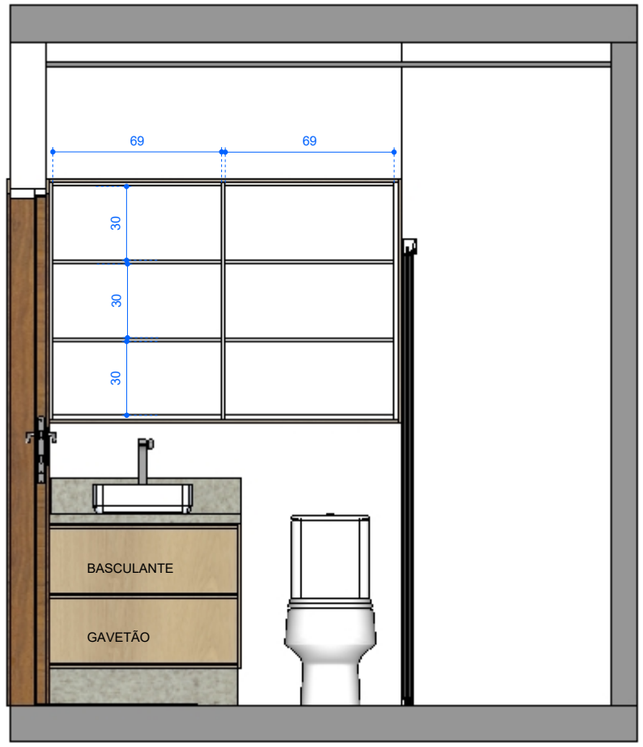

M31/32- ARMÁRIOS WC ARTHUR - ELEVAÇÃO

ESCALA 1:25

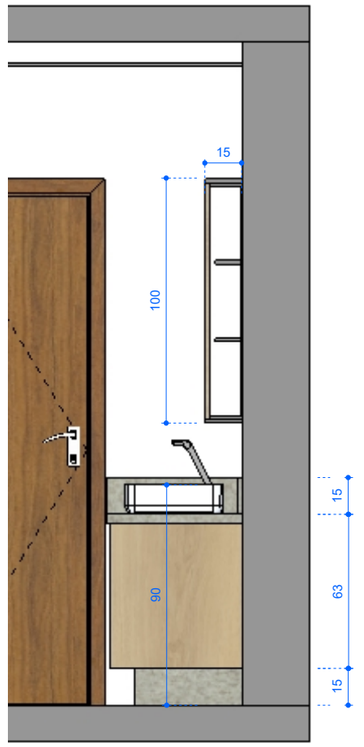

M31/32- ARMÁRIOS WC ARTHUR - CORTE

ESCALA 1:25

EMPÓRIO HASS ambientes planejados

contato.emporiohass@gmail.com
(61)99303-3151/98274-3709
Instagram: @emporiohass

ARQUITETO RESPONSÁVEL:
José Adalberto Meuren
CAU Nº 000A487848
(61)98274-3709
jmeuren@gmail.com

CONTEÚDO DA PRANCHA:
M30/31/32 - COZINHA E WC ARTHUR

ESCALA:
Indicada na Prancha

CLIENTE:
Gisele Landim de Souza

ENDEREÇO:
SGCV LT 20 COND. NEW YORK
BLOCO A APT 101
Brasília

ARQUIVO:
Arq_Int_Gis_Park_Sul

REVISÃO Nº:
R00

DATA REVISÃO:
23-10-2024

OBSERVAÇÕES:
Consultar arquiteto em caso de dúvida e/ou alteração;
Conferir medidas no local;
Medidas em cota prevalecem sobre o desenho

FOLHA:
20/24