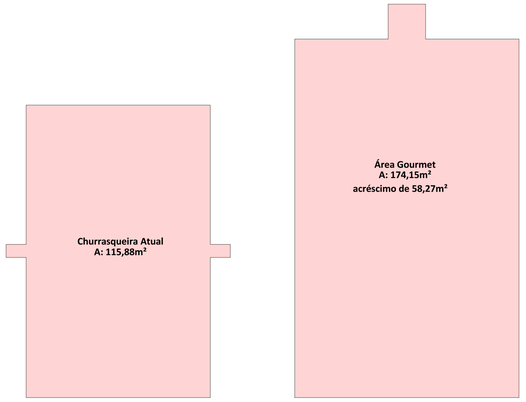


Demonstrativo acréscimo de área construída

Escala: 1:100

TAXA OCUPAÇÃO

Edificação	Área	T.O %
Área Gourmet	174,14	2,17
Bloco A	233,20	2,91
Bloco B	233,20	2,91
Bloco C	233,20	2,91
Bloco D	261,63	3,27
Bloco E	261,60	3,27
Bloco F	233,20	2,91
Bloco G	233,20	2,91
Bloco H	233,20	2,91
CEB	4,80	0,06
Portaria	44,21	0,55
	2.145,58 m²	**26,78**

ÁREA PERMEÁVEL

	Área
Jardim 01	24,50
Jardim 01	177,91
Jardim 02	16,16
Jardim 03	24,50
Jardim 04	21,84
Jardim 05	21,84
Jardim 06	2,54
Jardim 07	2,54
Jardim 08	2,54
Jardim 09	2,54
Jardim 10	532,89
Jardim 11	1.206,67
	2.036,47 m²

Estacionamento Permeável

	Área (m²)
Estacionamento	131,77
Estacionamento	132,00
Estacionamento permeável	220,32
Estacionamento Permeável	96,00
Estacionamento Permeável	96,00
Estacionamento Permeável	183,59
Estacionamento Permeável	183,60
Estacionamento Permeável	208,08
	1.251,36 m²


QUADRO DE ÁREAS

2 QUARTOS: BLOCOS A, B, C, F, G, H
PAVIMENTO — ÁREA CONSTRUÍDA (m²)
TÉRREO 233,16
1º PAVIMENTO 223,77
2º PAVIMENTO 223,77
3º PAVIMENTO 223,77
SUBTOTAL DE ÁREA CONSTRUÍDA 904,47
QUANTIDADE DE BLOCOS 6,00
ÁREA TOTAL CONSTRUÍDA – 2 QUARTOS 5.426,82
3 QUARTOS: BLOCOS D, E
PAVIMENTO — ÁREA CONSTRUÍDA (m²)
TÉRREO 276,33
1º PAVIMENTO 267,22
2º PAVIMENTO 267,22
3º PAVIMENTO 267,22
SUBTOTAL DE ÁREA CONSTRUÍDA 1.077,99
QUANTIDADE DE BLOCOS 2,00
ÁREA TOTAL CONSTRUÍDA – 3 QUARTOS 2.155,98
QUADRA QS-03, CONJUNTO 7, LOTE 2
EDIFICAÇÕES — ÁREA CONSTRUÍDA (m²)
BLOCOS DE APARTAMENTOS 2 UQARTOS 5.426,82
BLOCOS DE APARTAMENTOS 3 QUARTOS 2.155,98
ÁREA GOURMET (ANTIGA CHURRASQUEIRA) 174,15
PORTARIA 44,20
ÁREA TOTAL CONSTRUÍDA (ATC) 7.801,15
ÁREA DO LOTE 8.007,93
A ÁREA DO CÔMODO DA CEB É DE 4,8 m² (ÁREA NÃO COMPUTÁVEL)

CIU	00183I5d0001
Projeto	URB 031/2012
Norma Vigente	LC 948/2019 alterada pela LC 1007/2022
Código Parâmetro	2.102,00
UOS Parâmetro	Re 3
Coef. Aproveitamento básico/Máximo	1,30
Taxa Ocupação	0,50
Taxa Permeabilidade	0,30

Notas:

- Legislação: O projeto está de acordo com o código de obras do distrito federal;
- O profissional responsável pela execução da obra, juntamente com o proprietário se comprometem a construir a calçada de sua responsabilidade, adequando-a com as vizinhas existentes, atendendo a acessibilidade a todos com rampas e outros itens nos termos do código de edificações do DF;
- Os corrimãos devem ser calculados para resistir a uma carga de 900N aplicada em qualquer ponto deles, verticalmente de cima para baixo e horizontalmente em ambos os sentidos;
- Todas as escadas serão executadas em piso anti-derrapante;
- Todas as rampas serão executadas em piso anti-derrapante;
- Todas as esquadrias com vidro inferior a 90cm de altura, voltadas para o exterior, serão em vidro de segurança;
- Os vãos de acesso da edificação, para permitir a acessibilidade às pessoas com dificuldade de locomoção, atenderão ao seguinte:
  - Largura mínima de oitenta centímetros, soleira com bordas arredondadas ou chanfradasa com altura máxima de 1,5cm;
  - trilhos de embutir em portas de correr;
  - A Altura de interruptores e tomadas nas áreas comuns serão de acordo com a NBR 9050.

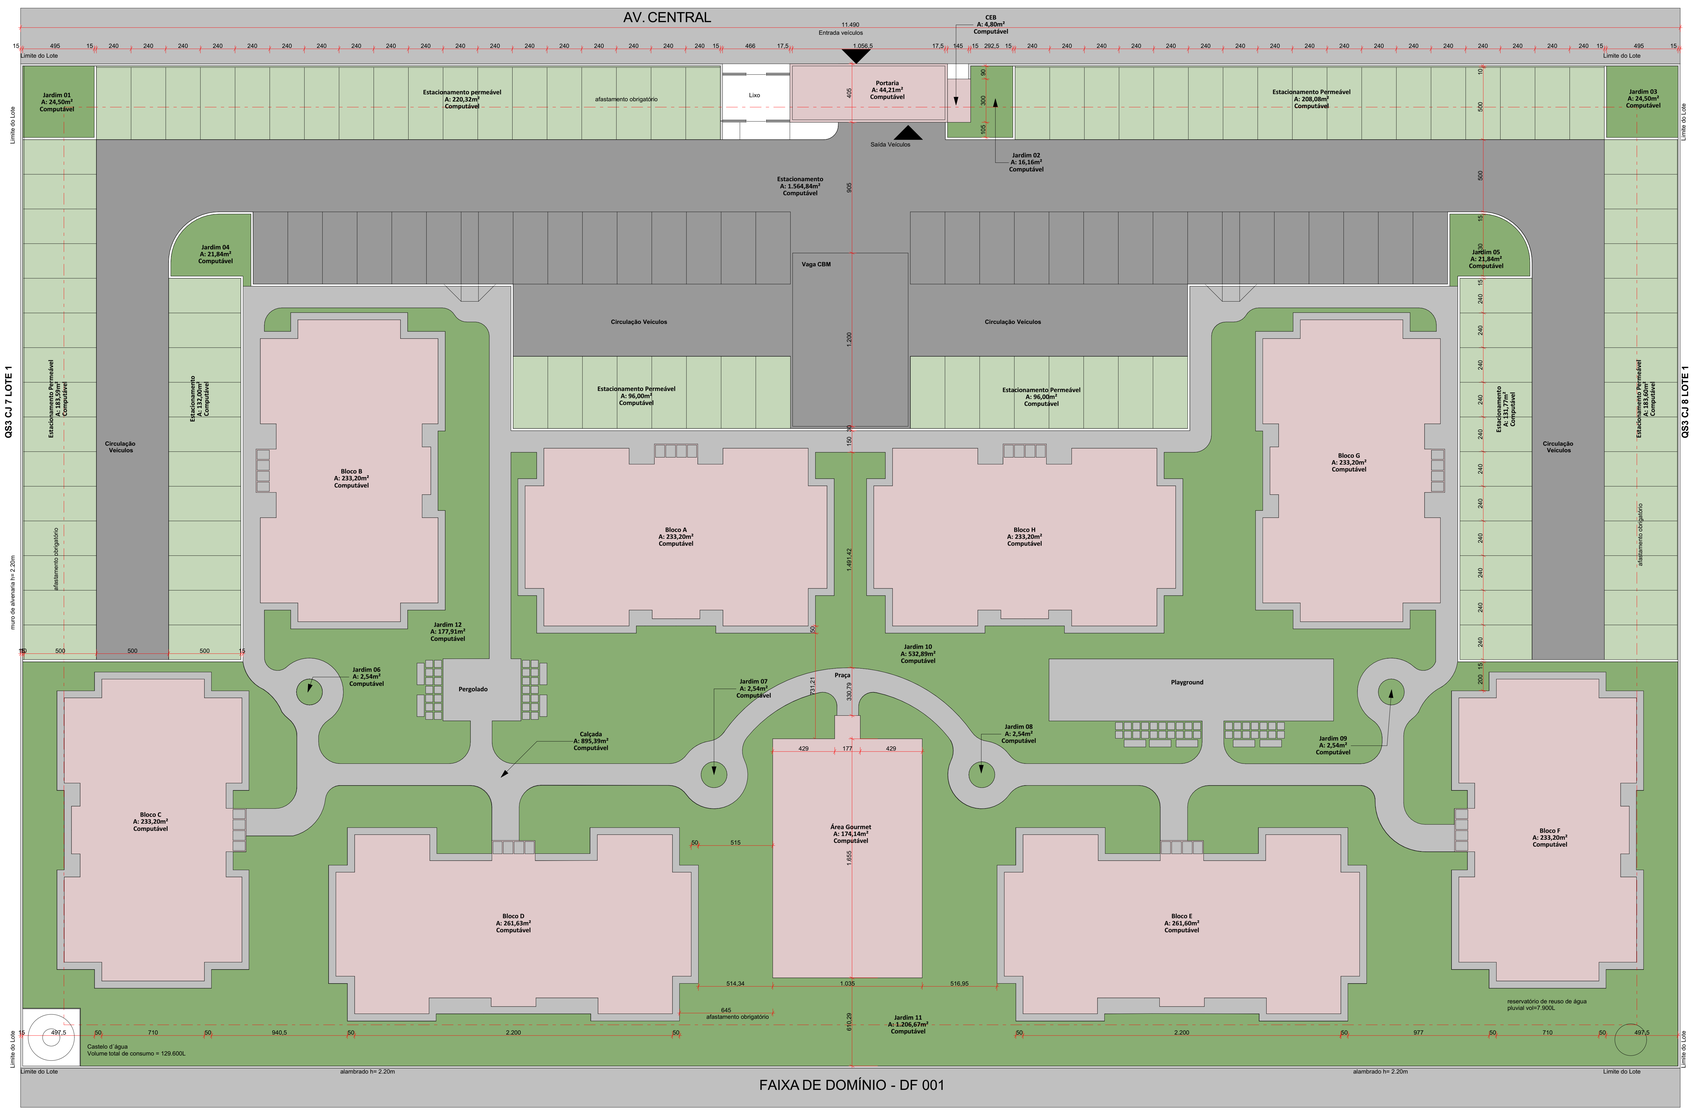

Planta de Implantação

Escala: 1:150


ÍNDICES URBANÍSTICOS

INFORMAÇÕES DO LOTE

INSCRIÇÃO IMOBILIÁRIA	000.000.000.000
ÁREA DO TERRENO	8.007,93m²
TESTADA DO TERRENO	114,90 m

ÍNDICES URBANÍSTICOS

ZONEAMENTO	RE3
CATEGORIA DE USO	8112-5/00
TAXA DE OCUPAÇÃO	98,55%
COEFICIENTE DE APROVEITAMENTO DO LOTE	0,99
GABARITO	4,5m (Churrasqueira)
TAXA DE PERMEABILIDADE	25,42%

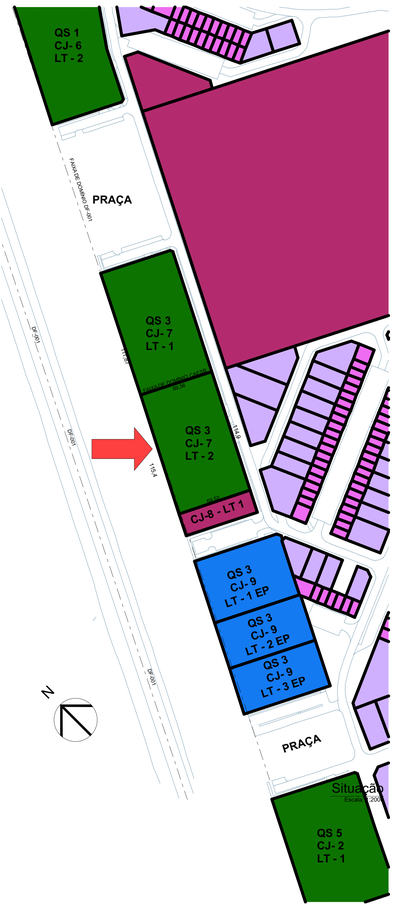

Situação

Escala: 1:2000

REV.	DESCRIÇÃO	MODIFICADO POR	DATA

ESPAÇO CHURRASQUEIRA - REFORMA COM ACRÉSCIMO DE ÁREA

ENDEREÇO:	Quadra QS-03, Conjunto 07, Lote 02 - Riacho Fundo II Brasília DF 71.844-032
PROPRIETÁRIO:	Condomínio Parque do Riacho 26
AUTORIA DO PROJETO:	José Adalberto Meuren
RESPONSÁVEL TÉCNICO:	José Adalberto Meuren

PROPRIETÁRIO: Condomínio Parque do Riacho 26 CPF/CNPJ nº 24.802.190/0001-29

Documento assinado digitalmente
gov.br JOSÉ ADALBERTO MEUREN
Data: 16/07/2026 10:08:37-0300
Verifique em https://validar.iti.gov.br

AUTORIA DO PROJETO: José Adalberto Meuren CAU nº A48784-8/DF

RESPONSÁVEL TÉCNICO: José Adalberto Meuren CAU nº A48784-8/DF

PROJETO DE ARQUITETURA


Situação - Implantação - Demonstrativo aumento de área - tabelas

PL | 01

DATA: Julho/2026

ETAPA DO PROJETO: Projeto Legal	EQUIPE TÉCNICA: José Adalberto Meuren CAU/CREA: A48784-8/DF	AREA TERRENO: 8.007,93m²
ESCALA: 1:2000, 1:150, 1:100, 1:1		AREA CONSTRUIDA: 7.801,15 m²

ARQUIVO: Condomínio Parque Riacho 26 x - Churrasqueira - Reforma - 25.07.2026.pln

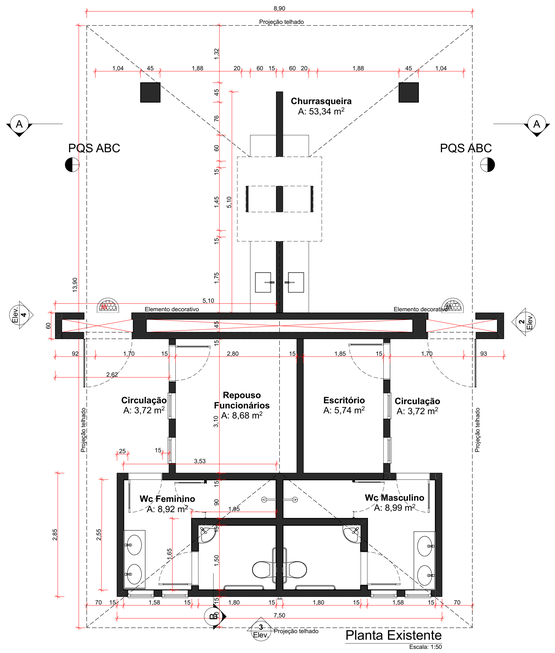


Planta Existente

Escala: 1:50

MAPA AMBIENTES LEVANTAMENTO

nº Zona	Nome Zona	Área
01	Churrasqueira	53,34
02	Repouso Funcionários	8,68
03	Escritório	5,74
04	Wc Feminino	8,92
07	Wc Masculino	8,99
08	Circulação	3,72
09	Circulação	3,72
		93,11 m²

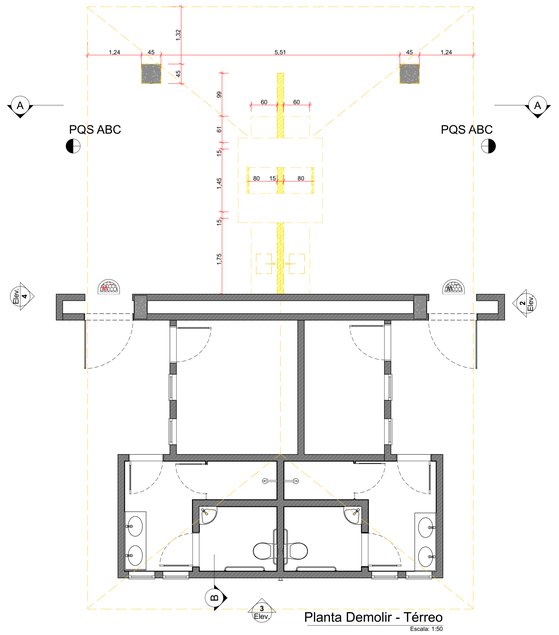


Planta Demolir - Térreo

Escala: 1:50


LEGENDA DEMOLIR CONSTRUIR

	Área
A Construir	154,29
A Demolir	43,77
Existente	227,32

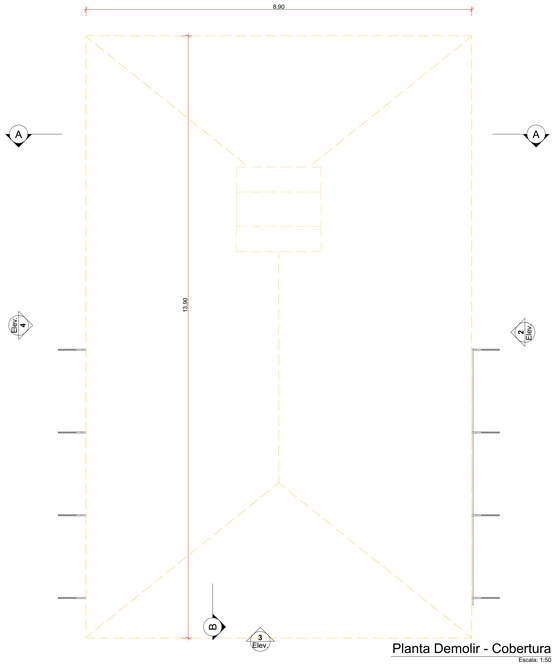


Planta Demolir - Cobertura

Escala: 1:50

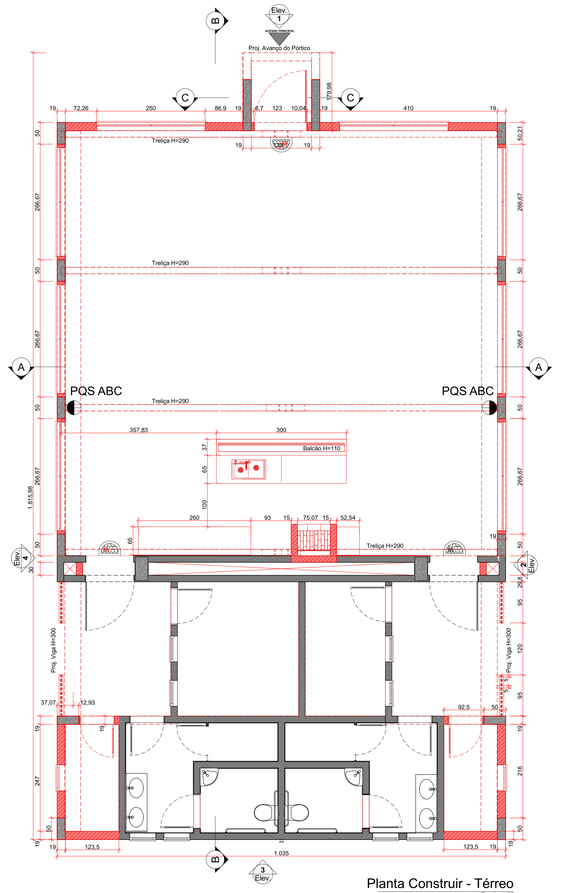


Planta Construir - Térreo

Escala: 1:50

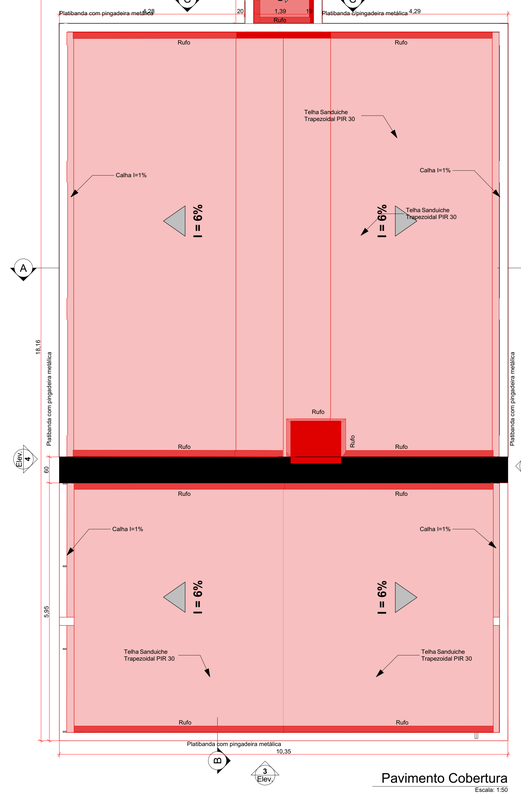


Pavimento Cobertura

Escala: 1:50

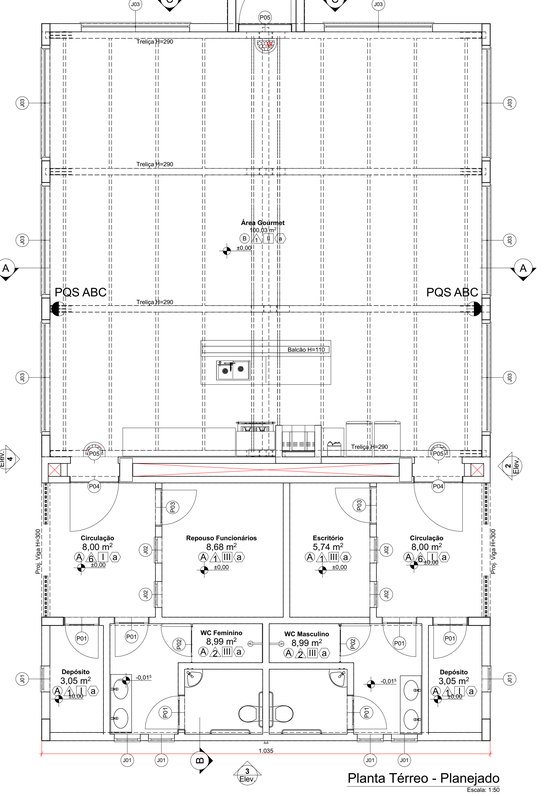

Planta Térreo - Planejado

Escala: 1:50

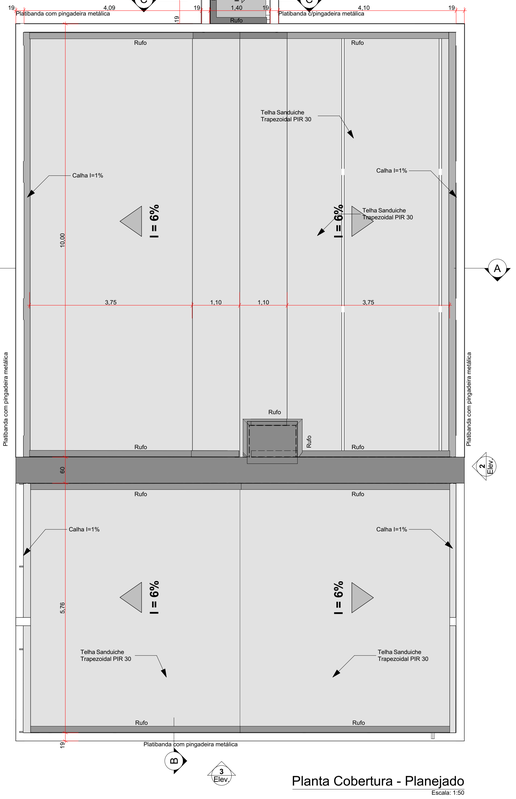

Planta Cobertura - Planejado

Escala: 1:50

QUADRO DE ESQUADRIAS - ADICIONAR

	ID	L x A	P	Tipo de Abertura	Material	Q.
Porta						
	P01	80×210	0	Abrir Simples	Alumínio	2
	P05	120×280	0	Abrir Simples	Alumínio; Vidro	1
Janela						
	J01	60×30	183	Maxim-Ar	Alumínio	2
	J03	250×180	100	Correr 2 Folhas	Alumínio; Vidro	8

QUADRO DE ESQUADRIAS - EXISTENTES

	ID	L x A	P	Tipo de Abertura	Material	Q.
Porta						
	P01	0,80×2,10	0,00	Abrir Simples	Alumínio	4
	P02	0,82×2,10	0,00	Abrir Simples	Alumínio	2
	P03	0,80×2,10	0,00	Abrir Simples	Alumínio; Vidro	2
	P04	1,10×2,10	0,00	Abrir Simples	Alumínio; Vidro	2
Janela						
	J01	0,60×0,30	1,83	Maxim-Ar	Alumínio	4

MAPA AMBIENTES PLANEJADO

nº Zona	Nome Zona	Área
01	Área Gourmet	100,03
02	Circulação	8,00
03	Repouso Funcionários	8,68
04	Escritório	5,74
05	Circulação	8,00
06	Depósito	3,05
07	WC Feminino	8,99
08	WC Masculino	8,99
09	Depósito	3,05
		154,53 m²

REV.	DESCRIÇÃO	MODIFICADO POR	DATA

ESPAÇO CHURRASQUEIRA - REFORMA COM ACRÉSCIMO DE ÁREA

ENDEREÇO: Quadra QS-03, Conjunto 07, Lote 02 - Riacho Fundo II Brasília DF 71.844-032

PROPRIETÁRIO: Condomínio Parque do Riacho 26

AUTORIA DO PROJETO: José Adalberto Meuren

RESPONSÁVEL TÉCNICO: José Adalberto Meuren

PROPRIETÁRIO: Condomínio Parque do Riacho 26 CPF/CNPJ nº 24.802.190/0001-29

gov.br Documento assinado digitalmente
JOSE ADALBERTO MEUREN
Data: 16/07/2026 10:08:37-0300
Verifique em https://validar.iti.gov.br

AUTORIA DO PROJETO: José Adalberto Meuren CAU nº A48784-8/DF

RESPONSÁVEL TÉCNICO: José Adalberto Meuren CAU nº A48784-8/DF

ARQUITETURA & INTERIORES j.m

PROJETO DE ARQUITETURA


Plantas Baixas Demolir/Construir/Planejado

PL | 02

DATA: Julho/2026

ETAPA DO PROJETO:	EQUIPE TÉCNICA:	ÁREA TERRENO:
Projeto Legal	José Adalberto Meuren	8.007,93m²
ESCALA:	CAU/DFA: A48784-8/DF	ÁREA CONSTRUÍDA:
1:50, 1:1		7.801,15 m²

ARQUIVO: Condomínio Parque Riacho 26 e 1- Churrasqueira - Reforma - 03-07-2026.pln

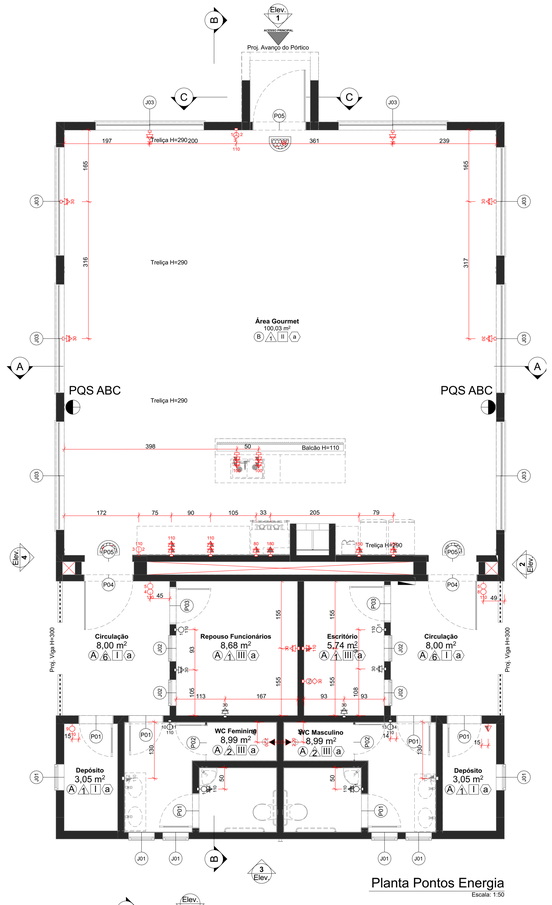


Planta Pontos Energia

Escala: 1:50

MIE-PE-06 LEGENDA PONTOS ELÉTRICOS

	Interruptor	Internet	Tomada 220v 10A	Tomada 220v 20A	TV	Estado
	0	0	1	0	0	A Construir
	0	0	1	0	0	A Construir
	0	0	1	0	0	A Construir
	0	0	1	0	0	A Construir
	0	0	1	0	0	A Construir
	0	0	1	0	0	A Construir
	0	0	1	0	0	A Construir
	0	0	1	0	0	A Construir
	0	0	1	0	0	A Construir
	0	0	1	0	0	A Construir
	0	0	1	0	0	A Construir
	0	0	1	1	0	A Construir
	0	0	1	1	0	A Construir
	0	0	2	0	0	A Construir
	0	0	2	0	0	A Construir
	0	1	0	0	1	A Construir
	0	**1**	**18**	**2**	**1**	

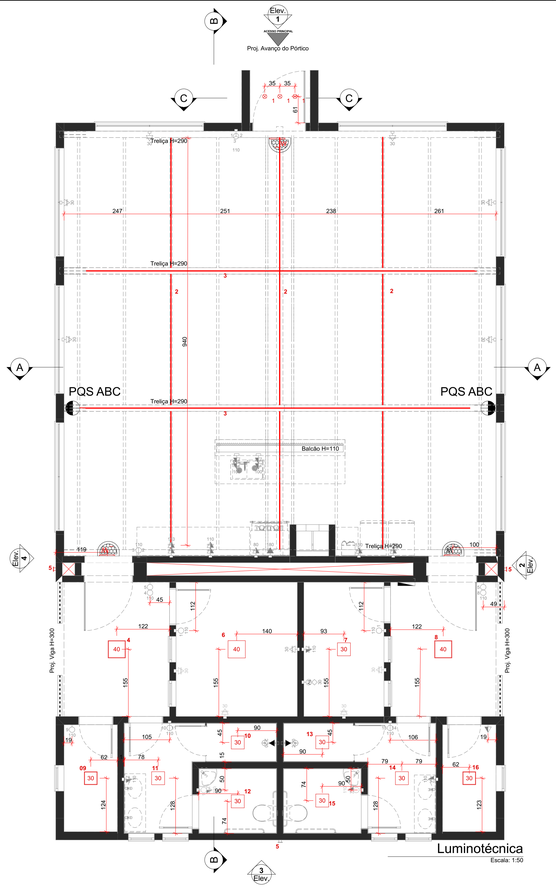

Luminotécnica

Escala: 1:50

QUADRO DE LUMINÁRIAS

Modelo	Legenda	Tipo de Lâmpada	Potência	Fluxo Luminoso	Temp.	Tipo de Fonte	IP (Proteção)	Q.	Estado
Arandela retangular duplo facho									
		LED	3W	320	3.000 K	inclusa	65	1	A Construir
Embutido ou Placa de Led 30x30cm									
	30	LED	32 W	2.500	3.000 k	Inclusa	20	2	A Construir
Embutido ou Placa de Led 40x40cm									
	40	LED	32 W	2.400	3.000 K	Inclusa	20	2	Existente
Sobrepor 30x30cm									
	30	LED	32 W	2.500	3.000 K	Inclusa	20	7	Existente
Sobrepor 40x40cm									
	40	LED	32 W	2.500	3.000 k	Inclusa	20	1	Existente
Spot Embutir									
		LED AR111	12 W	720	3000	Inclusa	20	3	A Construir


QUADRO DE PERFIS LED

Modelo	Legenda	Tipo de Lâmpada	Potência	Fluxo Luminoso	Temp.	Fonte	IP	Comp.	Quantidade	Estado
Fita Led Alto Brilho										
		LED	18 W/m	1.800	3.000 K	2 drivers 24v 150W	20	9,00	2	A Construir
		LED	18 W/m	1.800	3.000 K	2 drivers 24v 150W	20	9,50	3	A Construir
									46,50 m	

MEMORIAL ACABAMENTOS

Ambiente	Especificação Piso	Código Piso	Especificação Parede	Código Parede	Especificação Rodapé	Código Rodapé	Especificação Teto	Código Teto
Pavimento Térreo								
Área Gourmet	Porcelanato 72x72 ART 2096 Metropole Cement Acetinado - Via Rosa	B	Pintura Branco Acetinato	1	Porcelanato 72x72 ART2096 Metropole Cement Acetinado - Via Rosa	a	Telha Trapezoidal com fundo acabamento madeirado	II
Circulação	Porcelanato 72x72 ART 2096 Metropole Cement Acetinado - Via Rosa	A	Textura lisa elegance Ibratim	6	Porcelanato 72x72 ART2096 Metropole Cement Acetinado - Via Rosa	a	Forro de Gesso Acartonado acabamento Branco Fosco	I
Depósito	Porcelanato 72x72 ART 2096 Metropole Cement Acetinado - Via Rosa	A	Pintura Branco Acetinato	1	Porcelanato 72x72 ART2096 Metropole Cement Acetinado - Via Rosa	a	Forro de Gesso Acartonado acabamento Branco Fosco	I
Escritório	Porcelanato 72x72 ART 2096 Metropole Cement Acetinado - Via Rosa	A	Pintura Branco Acetinato	1	Porcelanato 72x72 ART2096 Metropole Cement Acetinado - Via Rosa	a	Laje com acabamento em gesso cola branco fosco	III
Repouso Funcionários	Porcelanato 72x72 ART 2096 Metropole Cement Acetinado - Via Rosa	A	Pintura Branco Acetinato	1	Porcelanato 72x72 ART2096 Metropole Cement Acetinado - Via Rosa	a	Laje com acabamento em gesso cola branco fosco	III
WC Feminino	Porcelanato 72x72 ART 2096 Metropole Cement Acetinado - Via Rosa	A	Porcelanato 72x72 ART2096 Metropole Cement Acetinado - Via Rosa	2	Porcelanato 72x72 ART2096 Metropole Cement Acetinado - Via Rosa	a	Laje com acabamento em gesso cola branco fosco	III
WC Masculino	Porcelanato 72x72 ART 2096 Metropole Cement Acetinado - Via Rosa	A	Porcelanato 72x72 ART2096 Metropole Cement Acetinado - Via Rosa	2	Porcelanato 72x72 ART2096 Metropole Cement Acetinado - Via Rosa	a	Laje com acabamento em gesso cola branco fosco	III

Nota:
- As alvenarias externas, pilares e vigas terão acabamento Textura Lisa elegance Ibratim;
- A alvenaria do elemento decorativo,churrasqueira, platibanda e pilaretes de amarração da platibanda terão acabamento em Tinta Pva preto fosco;
- Todas as peças metálicas da estrutura do telhado bem como dos brises laterais terão acabamento em Tinsta esmalte preto fosco;
- O pórtico de entrada terá acabamento em tinta pva preto fosco.

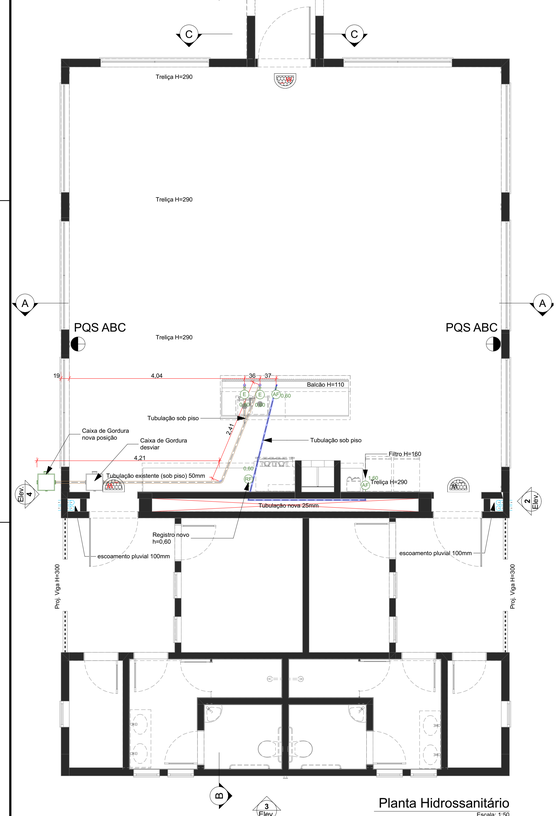


Planta Hidrossanitário

Escala: 1:50


LEGENDA PONTOS HIDROSSANITÁRIOS

	Modelo	Estado	Q.
CG	Caixa de Gordura	A Construir	1
07 QV	Ponto de Água Fria	A Construir	2
09 3 0,60	Ponto de Esgoto	A Construir	2
RG	Ponto de Registro	A Construir	1

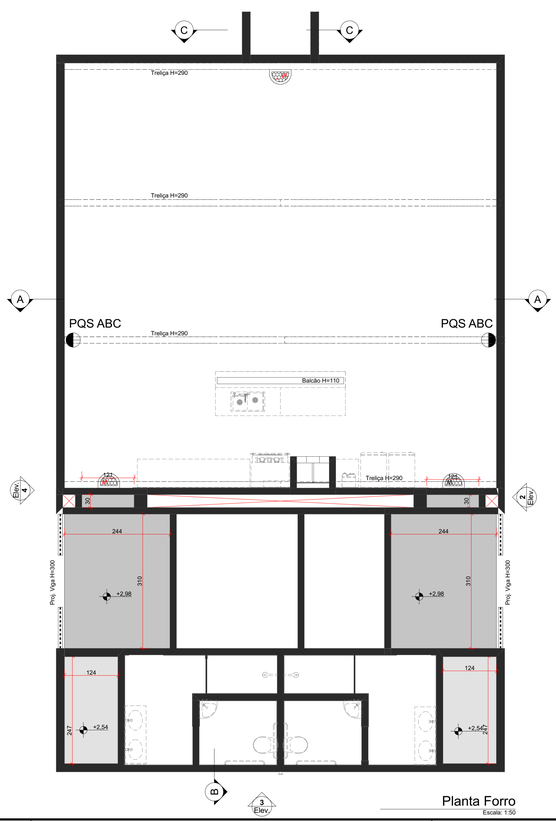

Planta Forro

Escala: 1:50

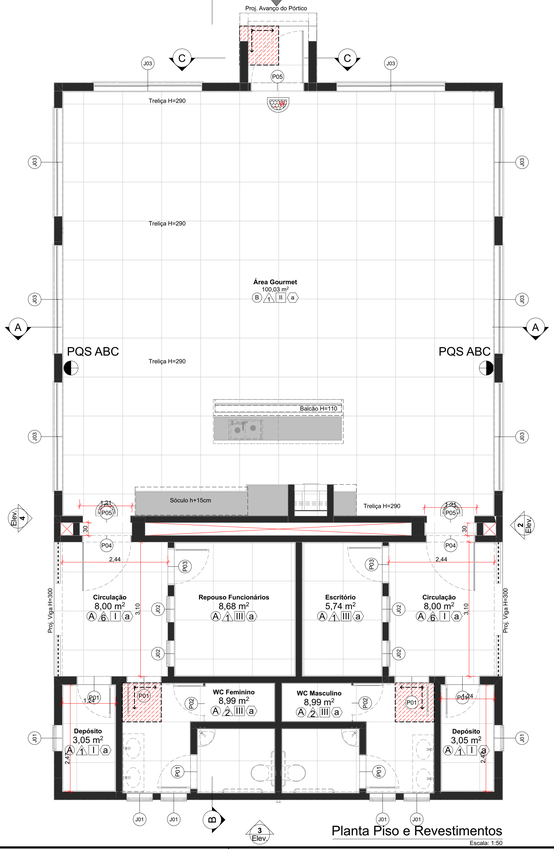

Planta Piso e Revestimentos

Escala: 1:50

REV.	DESCRIÇÃO	MODIFICADO POR	DATA

ESPAÇO CHURRASQUEIRA - REFORMA COM ACRÉSCIMO DE ÁREA

ENDEREÇO: Quadra QS-03, Conjunto 07, Lote 02 - Riacho Fundo II Brasília DF 71.844-032

PROPRIETÁRIO: Condomínio Parque do Riacho 26

AUTORIA DO PROJETO: José Adalberto Meuren

RESPONSÁVEL TÉCNICO: José Adalberto Meuren

PROPRIETÁRIO: Condomínio Parque do Riacho 26 CPF/CNPJ nº 24.802.190/0001-29

gov.br Documento assinado digitalmente
JOSÉ ADALBERTO MEUREN
Data: 16/07/2026 10:08:37-0300
Verifique em https://validar.iti.gov.br

AUTORIA DO PROJETO: José Adalberto Meuren CAU nº A48784-8/DF

RESPONSÁVEL TÉCNICO: José Adalberto Meuren CAU nº A48784-8/DF

ARQUITETURA & INTERIORES j.m

PROJETO DE ARQUITETURA


Pontos Energia, Luminotécnica, hidrossanitário, Forro, Piso e Revestimentos

PL | 03

DATA: Julho/2026

ETAPA DO PROJETO:	EQUIPE TÉCNICA:	ÁREA TERRENO:
Projeto Legal	José Adalberto Meuren	8.007,93m²
ESCALA:	CAU/DFA: A48784-8/DF	ÁREA CONSTRUÍDA:
1:50, 1:1		7.801,15 m²


ARQUIVO: Condomínio Parque Riacho 26 e. Churrasqueira - Reforma - 23-07-2026.pln

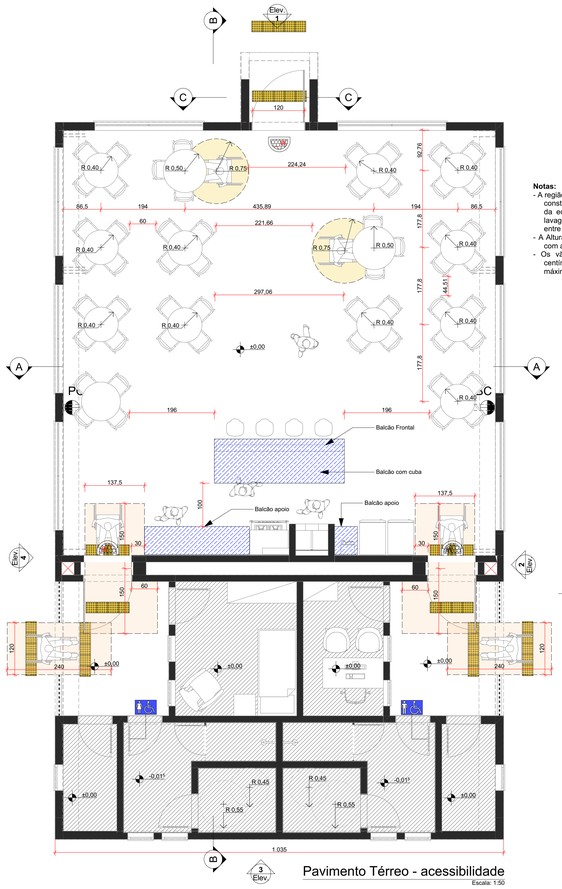

Pavimento Térreo - acessibilidade

Escala: 1:50


Notas:
- A região que compreende as bancadas , fogão, churrasqueira e geladeiras constitui área operacional de serviço (back-of-house), de uso exclusivo da equipe de cozinha e serviço. Sua função é permitir o preparo, a lavagem, o deslocamento interno e a passagem de pratos e bebidas entre os equipamentos;
- A Altura de interruptores e tomadas nas áreas comuns serão de acordo com a NBR 9050;
- Os vãos de acesso da edificação terão largura mínima de oitenta centímetros, soleira com bordas arredondadas ou chanfradas com altura máxima de 1,5cm.

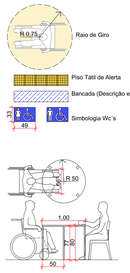

mesa acessibilidade


Escala: 1:50

ÁREA	FUNÇÃO	QUEM USA
Balcão frontal (1,10m)	Apoio para consumação de banquetas	Condôminos
Balcão com cuba (0,90m)	Lavagem de utensílios, passagem de pratos/bebidas	Equipe de cozinha/serviço
Balcão ao fundo	apoio e preparo de alimentos para cocção	Equipe cozinha
Freezer+geladeira	Armazenamento de insumos	Equipe cozinha
Salão principal	Mesas e circulação	Condôminos

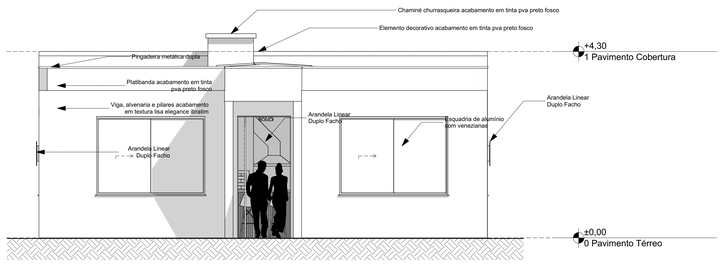


Elevação 1

Escala: 1:50

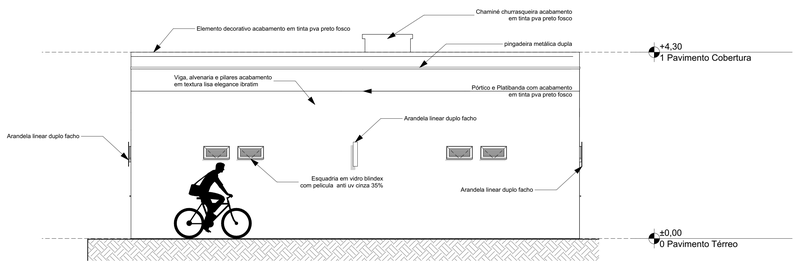


Elevação 3

Escala: 1:50

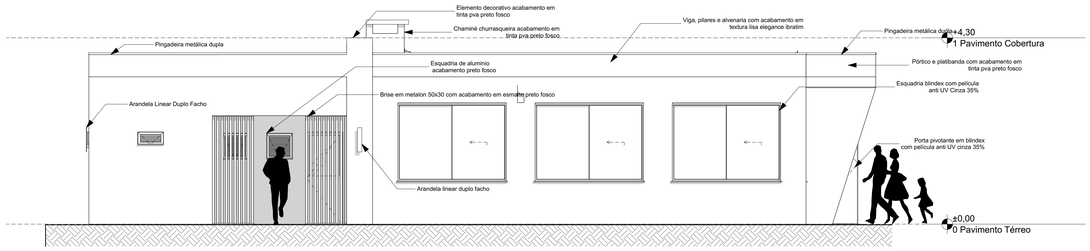


Elevação 2

Escala: 1:50

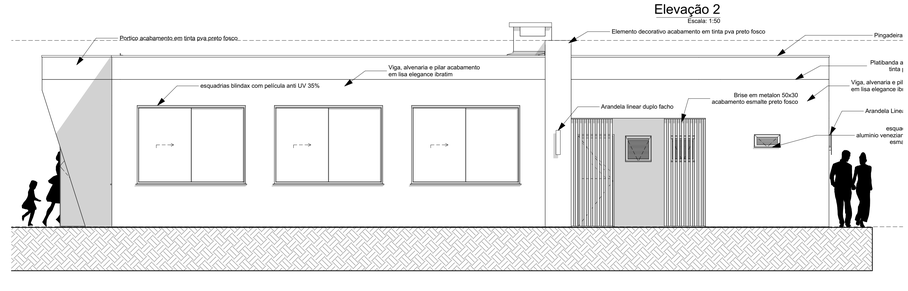


Elevação 4

Escala: 1:50

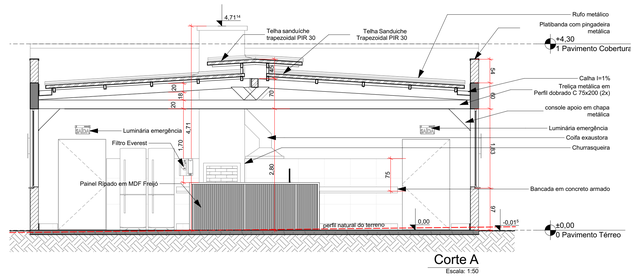


Corte A

Escala: 1:50

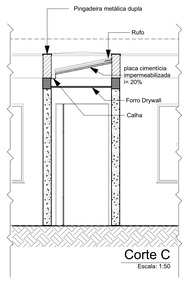


Corte C

Escala: 1:50

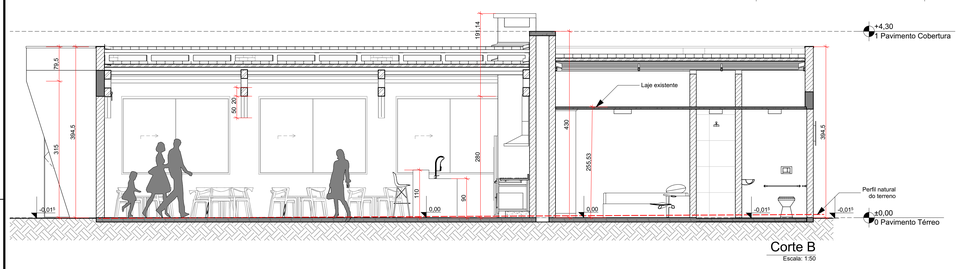


Corte B


Escala: 1:50

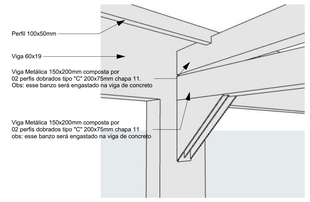

Obs: Todas as peças metálicas terão acabamento em esmalte a base d´água preto fosco.

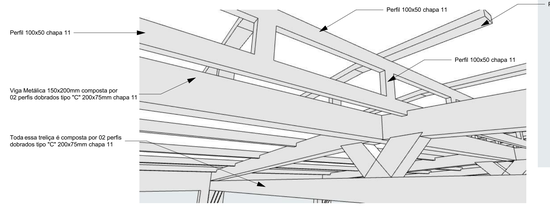

Obs: Todas as peças metálicas terão acabamento em esmalte a base d´água preto fosco.

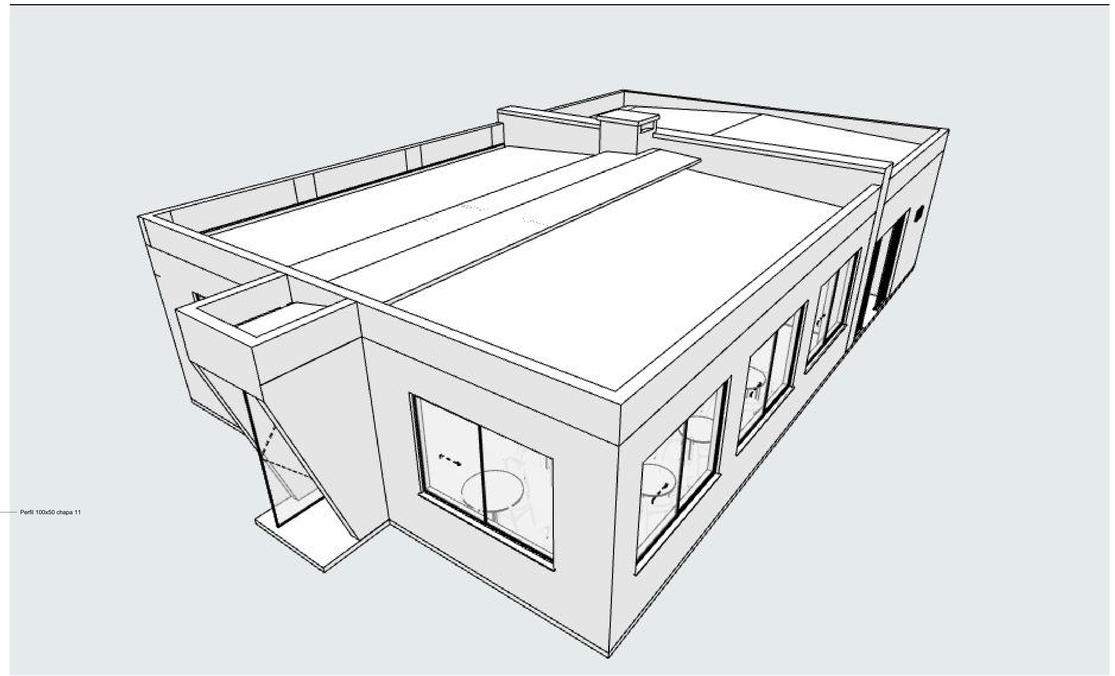

REV.	DESCRIÇÃO	MODIFICADO POR	DATA

ESPAÇO CHURRASQUEIRA - REFORMA COM ACRÉSCIMO DE ÁREA

ENDEREÇO: Quadra QS-03, Conjunto 07, Lote 02 - Riacho Fundo II Brasília DF 71.844-032

PROPRIETÁRIO: Condomínio Parque do Riacho 26

AUTORIA DO PROJETO: José Adalberto Meuren

RESPONSÁVEL TÉCNICO: José Adalberto Meuren

PROPRIETÁRIO: Condomínio Parque do Riacho 26 CPF/CNPJ nº 24.802.190/0001-29

Documento assinado digitalmente
gov.br
JOSÉ ADALBERTO MEUREN
Data: 16/01/2026 10:08:38-0300
Verifique em https://validar.iti.gov.br

AUTORIA DO PROJETO: José Adalberto Meuren CAU nº A48784-8/DF

RESPONSÁVEL TÉCNICO: José Adalberto Meuren CAU nº A48784-8/DF

PROJETO DE ARQUITETURA

Acessibilidade, Cortes e Elevações

PL | 04

DATA: Julho/2026

ETAPA DO PROJETO: Projeto Legal

EQUIPE TÉCNICA: José Adalberto Meuren CAU/CREA: A48784-8/DF

ESCALA: 1:50, 1:76,21, 1:85,71, 1:1, 1:32,18

ÁREA TERRENO: 8.007,93m²

ÁREA CONSTRUÍDA: 7.801,15 m²

ARQUIVO: Condomínio Parque Riacho 26 b. Churrasqueira - Reforma - 15-07-2026.pln