
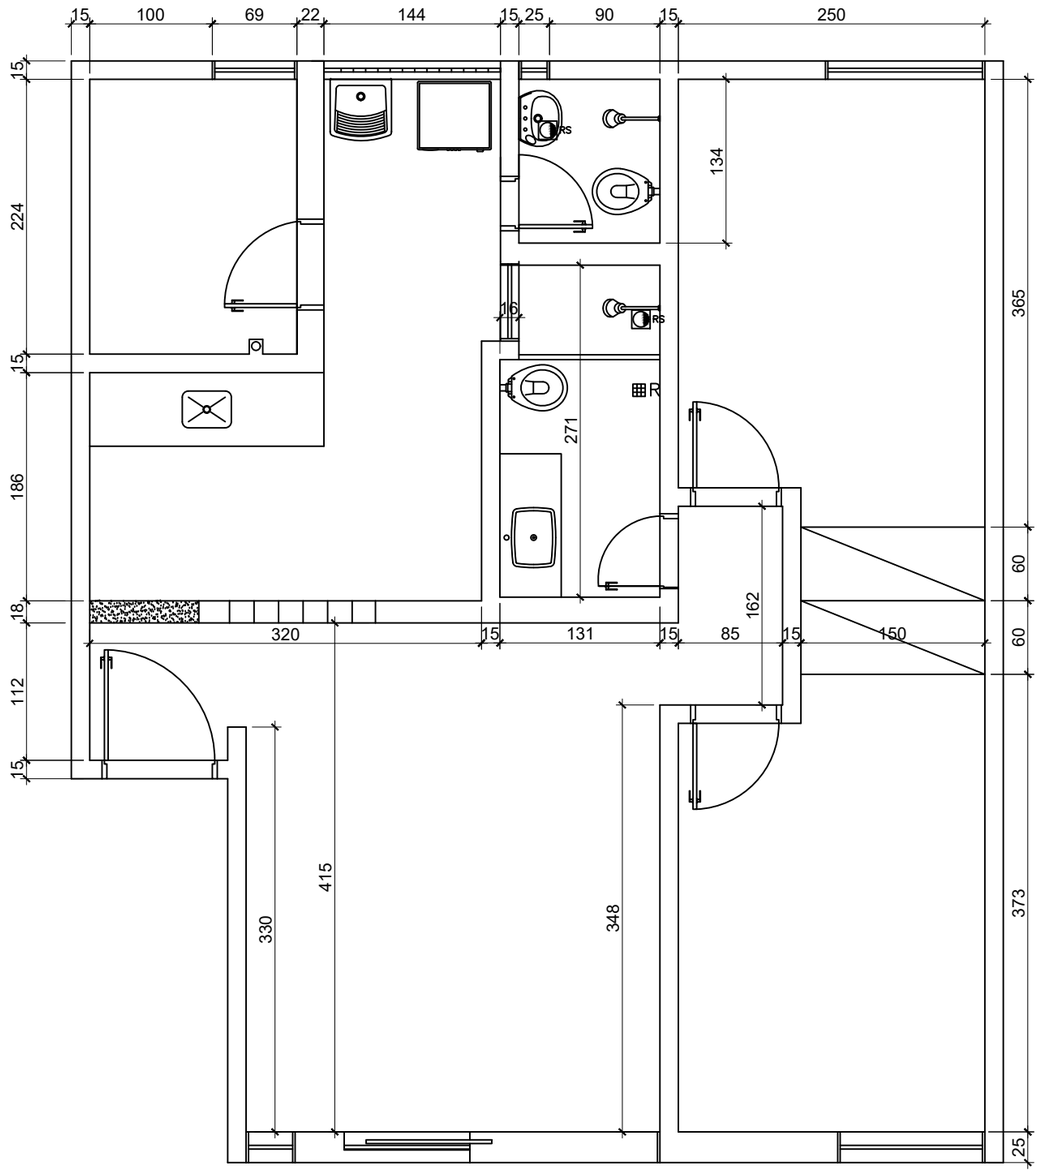


PLANTA BAIXA ORIGINAL
escala - 1/50

LEGENDA:


- demolir
- construir
- existente
- concreto

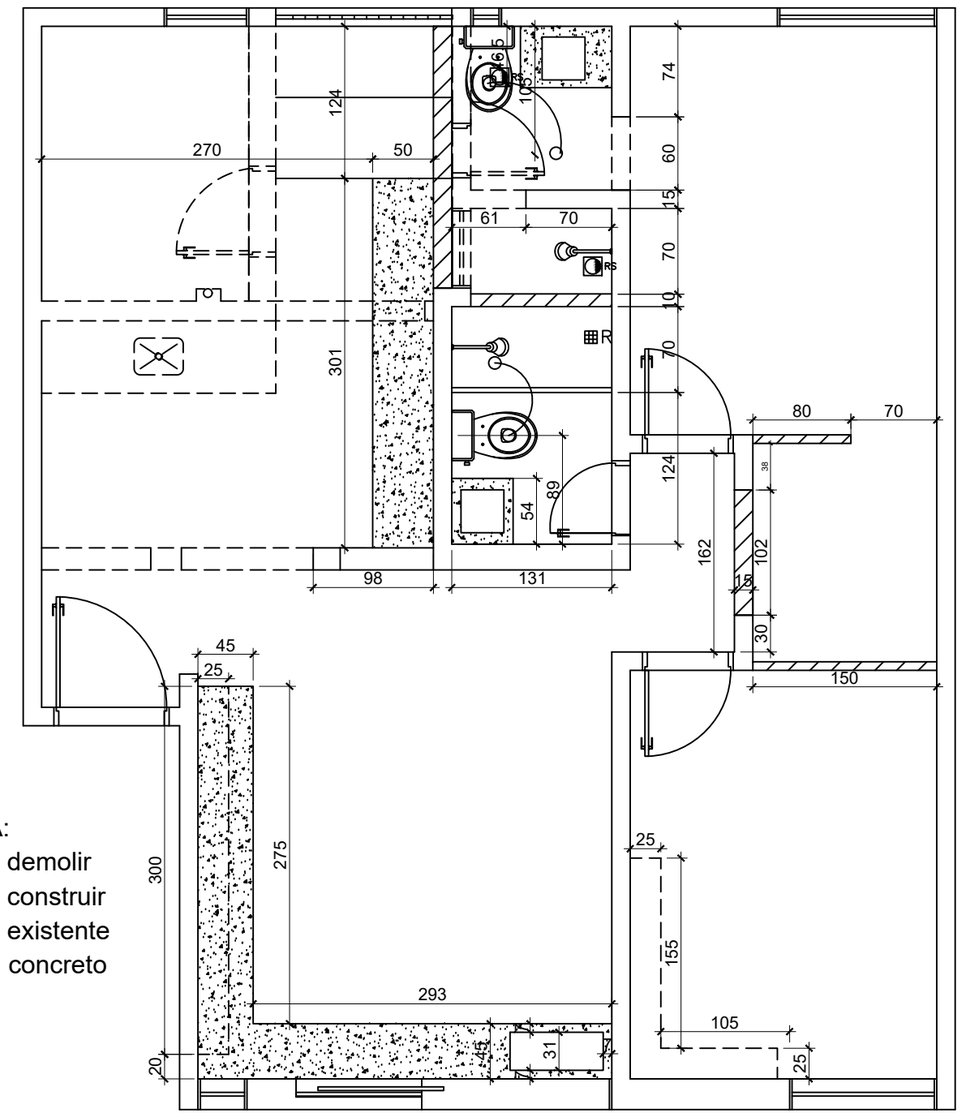

PLANTA DEMOLIR/CONSTRUIR
escala - 1/50

Obs: As intervenções propostas só serão executadas se não interferirem em nenhuma peça estrutural (Viga/Pilar) ou instalação que não possa sofrer derivações.


JMEUREN 98274-3709	PROJETO: REFORMA DE APARTAMENTO AUTOR: jmeuren@gmail.com CAU/DF 000A487848	CLIENTE: MURIEL GUEDES & HENRIQUE MEUREN ENDEREÇO: SQN 409 BLOCO C aptº 206	PRANCHA: 01 Data: Dez/2020

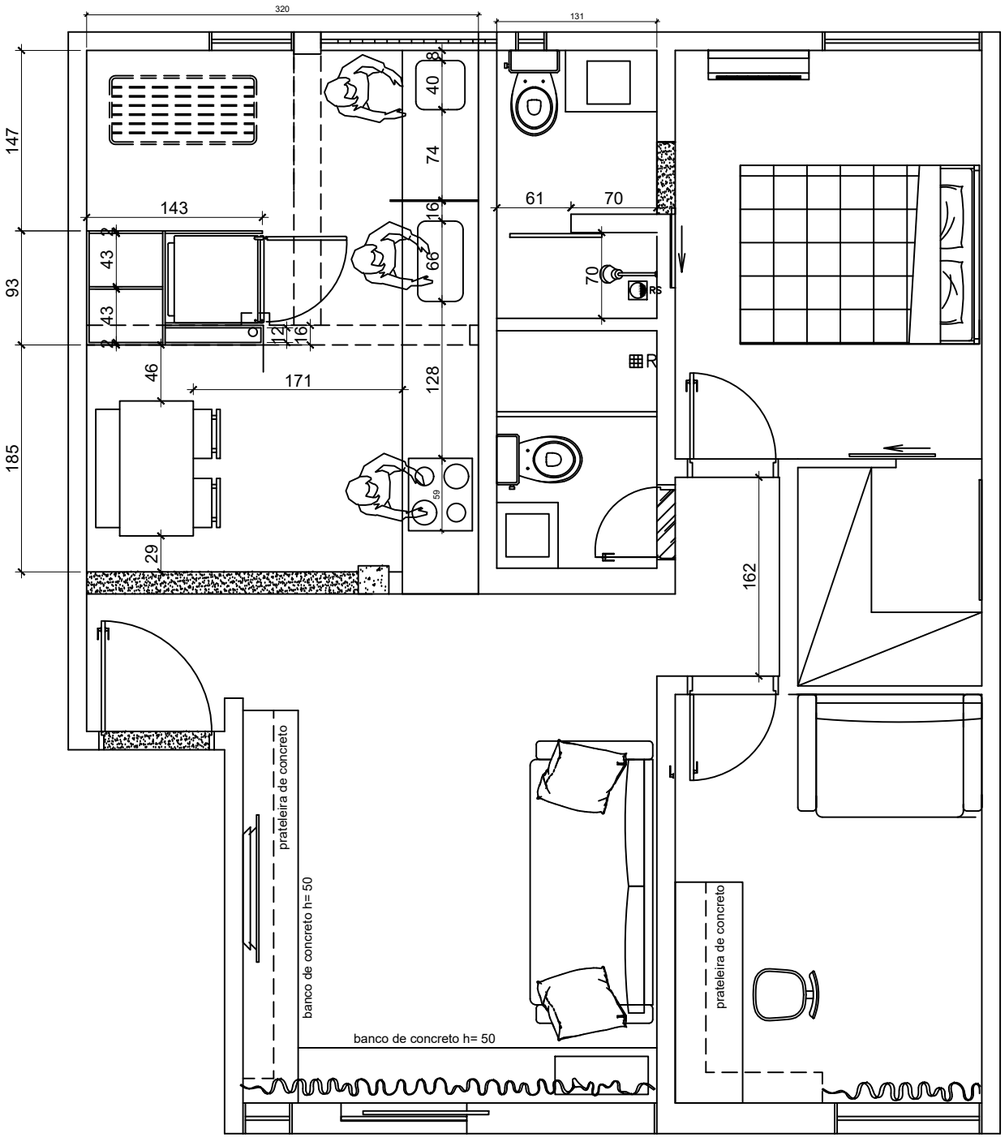

LAYOUT SUGERIDO
escala - 1/50


LEGENDA

Lum. Led Quad. de Embutir Acab. Branco tipo mini dicroica - cor 3.000k	◆
Painel Led Quad. de Embutir Acab. Bco - 20x20 - 25watts cor 3.000k	■
Painel Led Quad. de sobrepor Acab. Bco - 30x30 - 25 watts cor 3.000k	⊞
Painel Led Quad. de Embutir Acab. Bco - 30x30 - 25 watts cor 3.000k	■
SPOT sob trilhos acabamento preto cor 3.000k	
Ponto de Antena 30 cm do piso	
Tomada baixa 30cm do piso	
Tomada média a 130 cm do piso	
Tomada Alta a 200 cm do piso	
Ponto de Telefone a 30cm do piso	
Interruptor e tomada a 130cm do pixo	

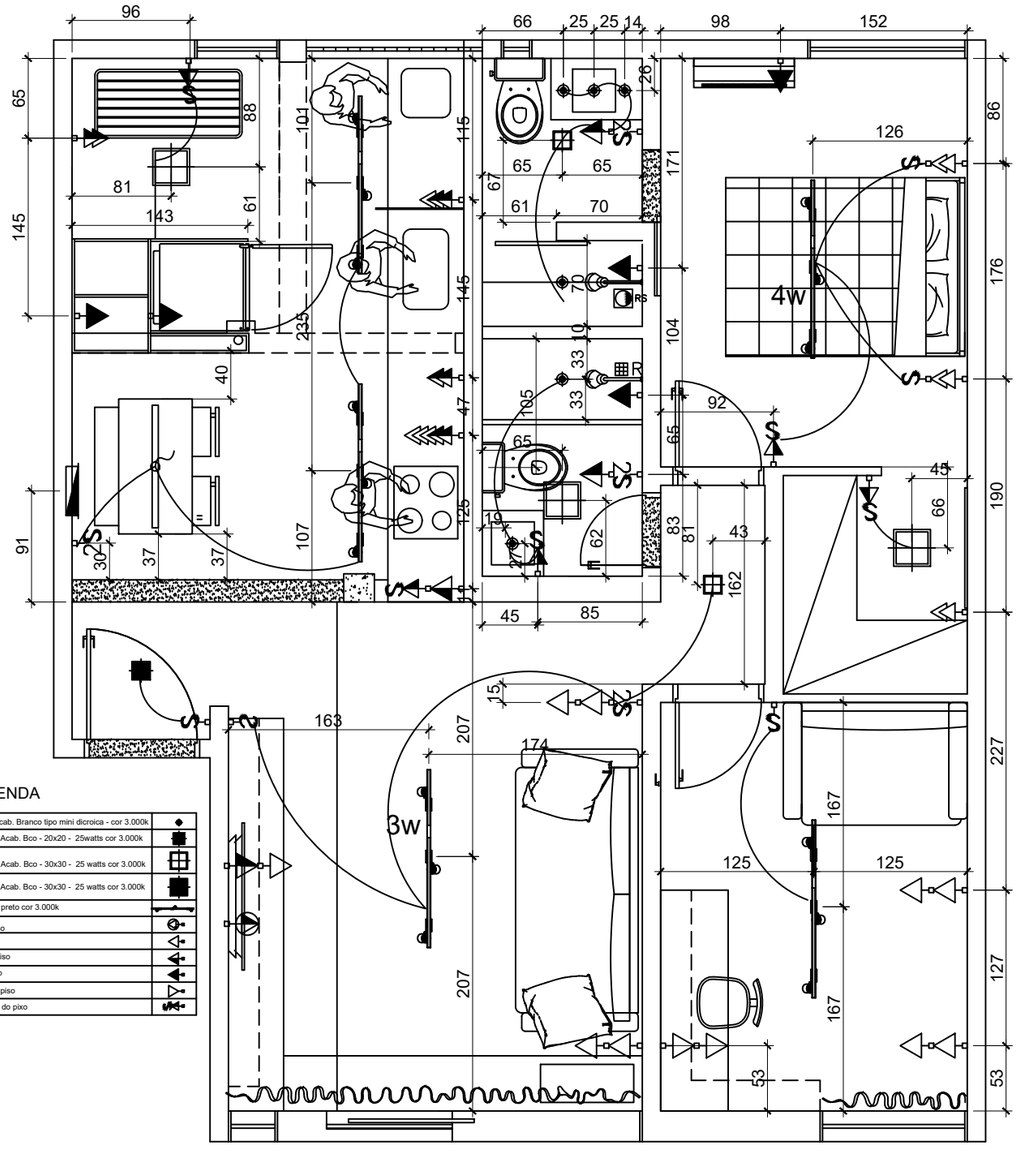


PONTOS DE LUZ E ENERGIA
escala - 1/50

PROJETO: JMEUREN	REFORMA DE APARTAMENTO	CLIENTE: MURIEL GUEDES & HENRIQUE MEUREN	PRANCHA: 02
AUTOR: 98274-3709	jmeuren@gmail.com CAU/DF 000A487848	ENDEREÇO: SQN 409 BLOCO C aptº 206	Data: Dez/2020

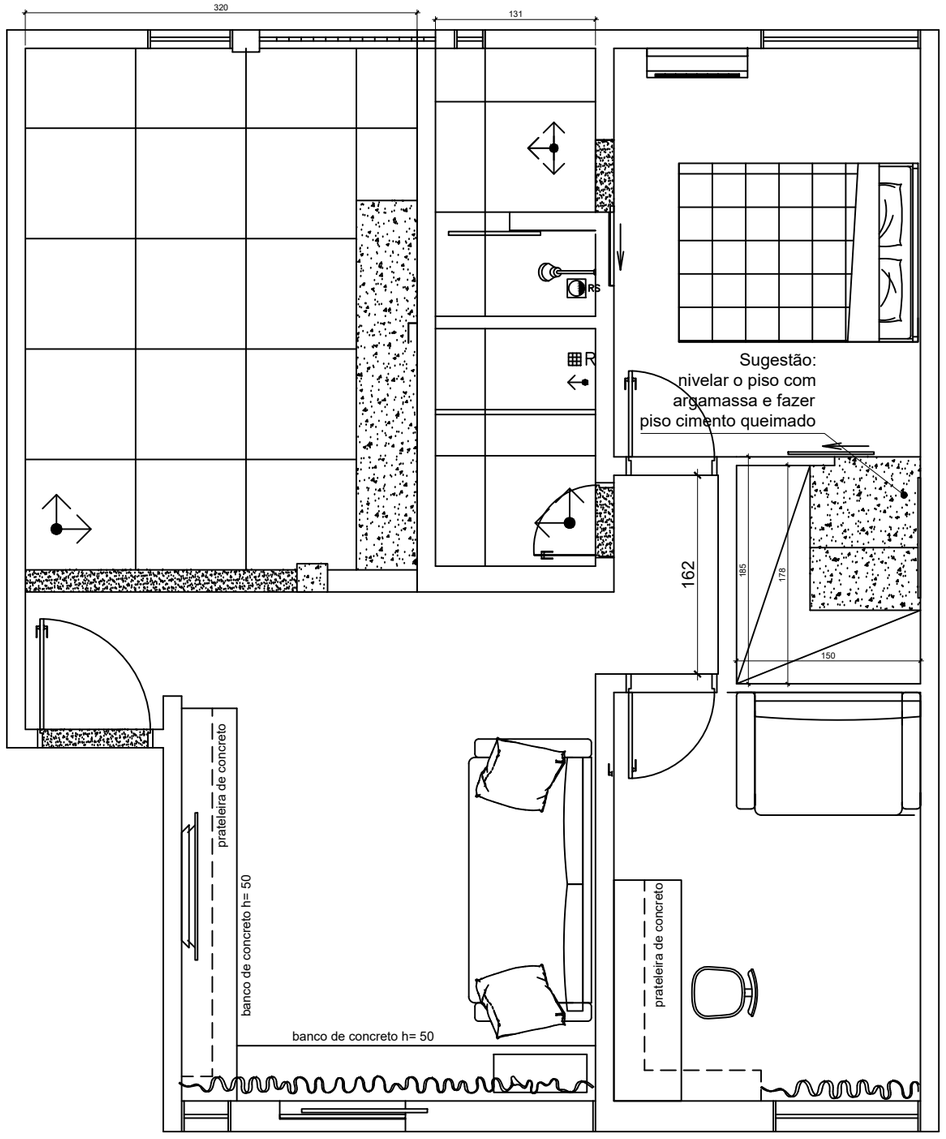


PLANTA PISO
escala - 1/50

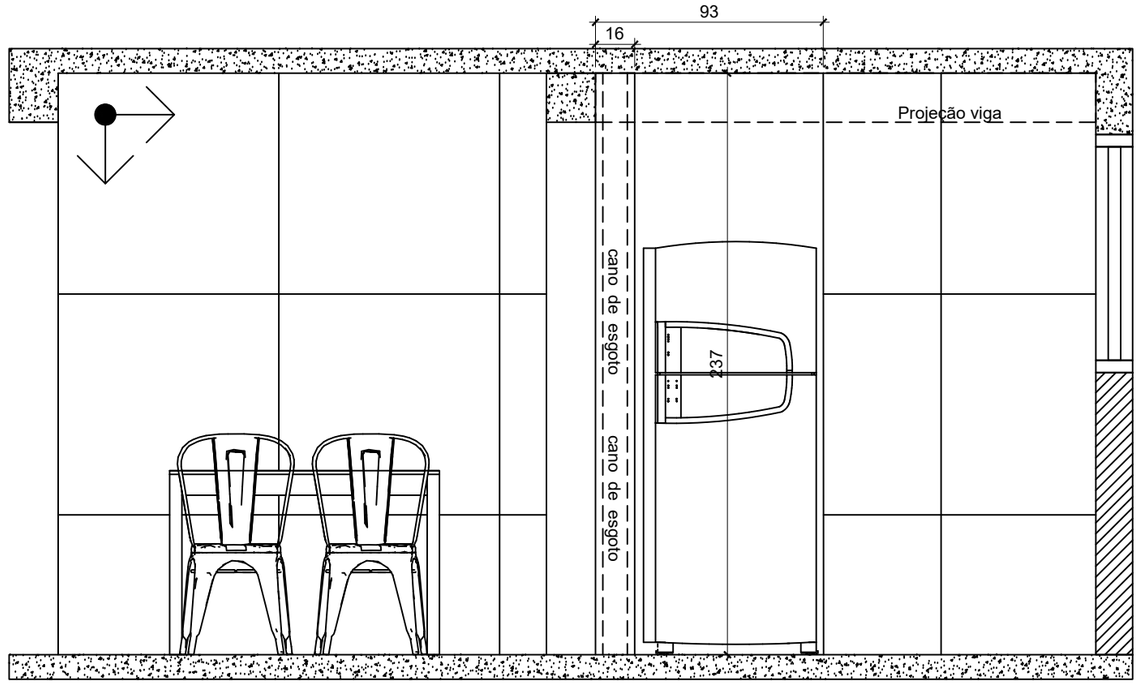


ELEVAÇÃO COZINHA
escala - 1/25


JMEUREN 98274-3709	PROJETO: REFORMA DE APARTAMENTO AUTOR: jmeuren@gmail.com CAU/DF 000A487848	CLIENTE: MURIEL GUEDES & HENRIQUE MEUREN ENDEREÇO: SQN 409 BLOCO C aptº 206	PRANCHA: 03 Data: Dez/2020

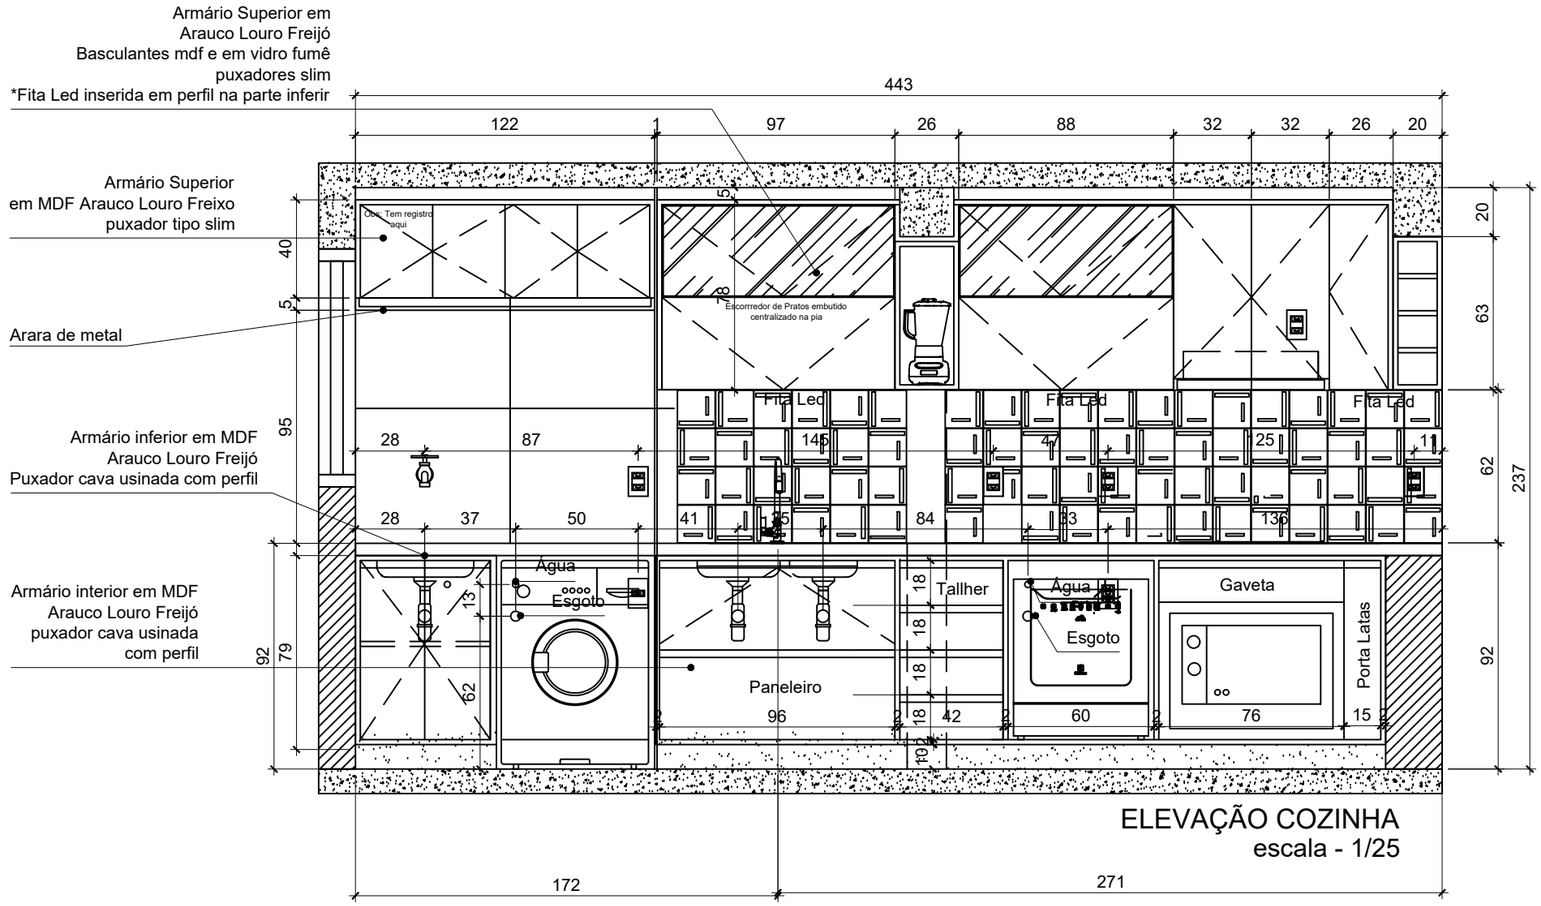

JMEUREN 98274-3709	PROJETO: REFORMA DE APARTAMENTO AUTOR: jmeuren@gmail.com CAU/DF 000A487848	CLIENTE: MURIEL GUEDES & HENRIQUE MEUREN ENDEREÇO: SQN 409 BLOCO C aptº 206	PRANCHA: 04 Data: Dez/2020

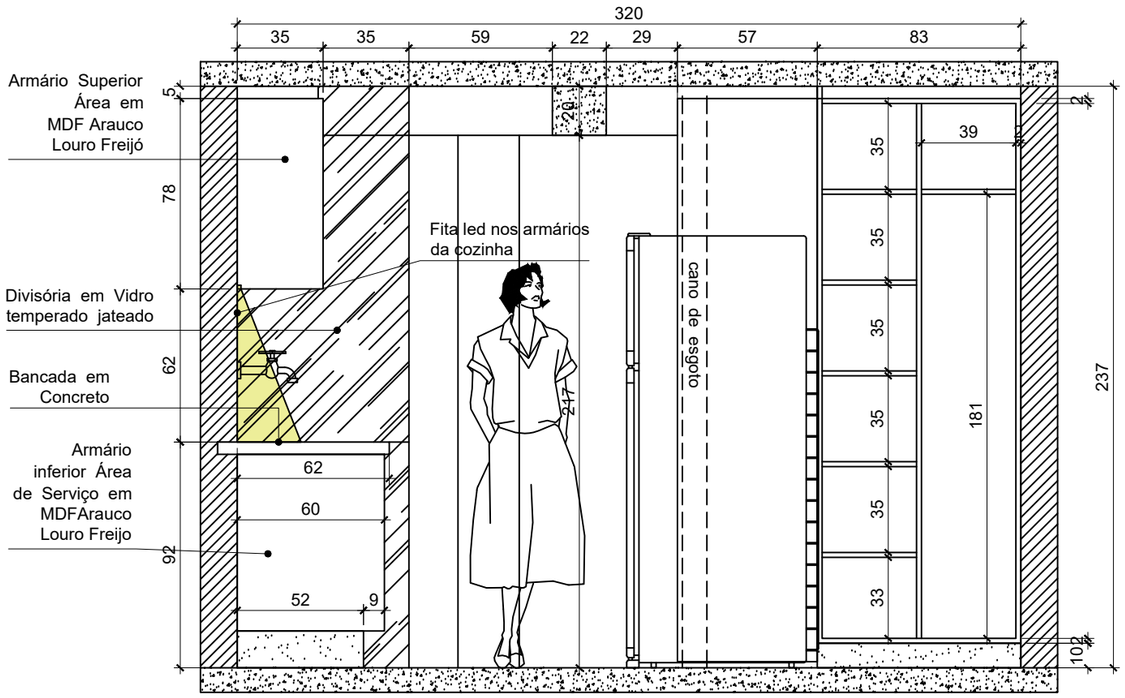


ELEVAÇÃO COZINHA
escala - 1/25

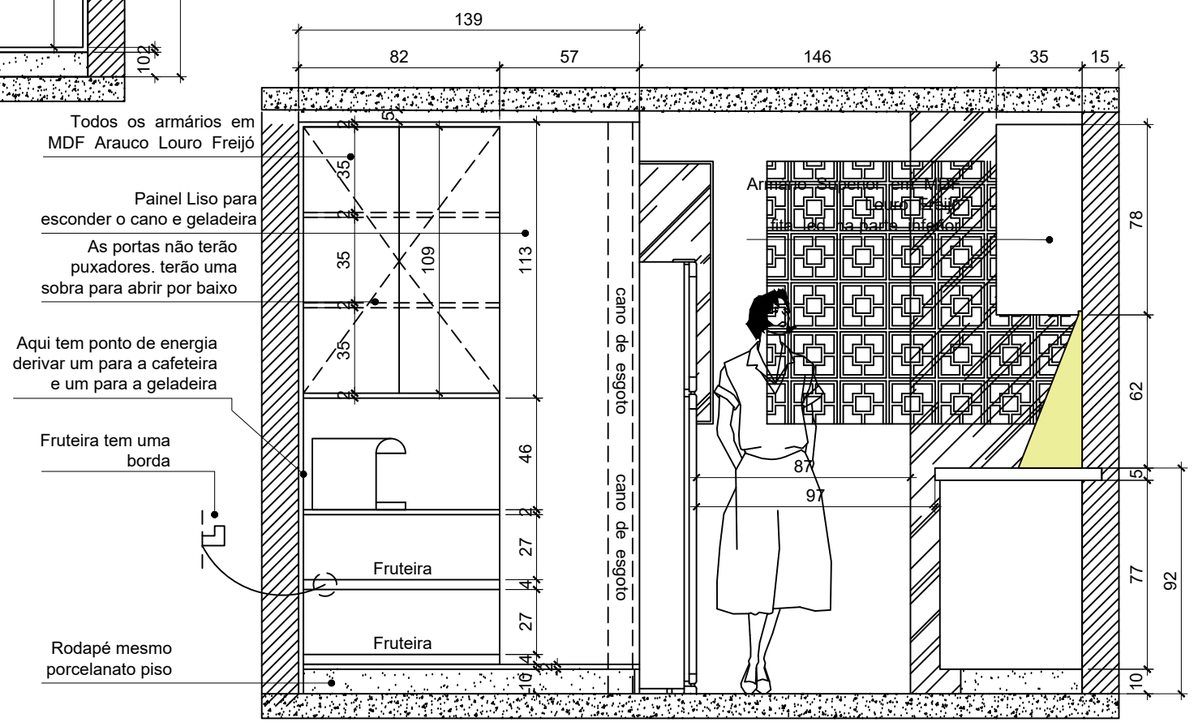


ELEVAÇÃO COZINHA
escala - 1/25


JMEUREN 98274-3709	PROJETO: REFORMA DE APARTAMENTO AUTOR: jmeuren@gmail.com CAU/DF 000A487848	CLIENTE: MURIEL GUEDES & HENRIQUE MEUREN ENDEREÇO: SQN 409 BLOCO C aptº 206	PRANCHA: 05 Data: Dez/2020

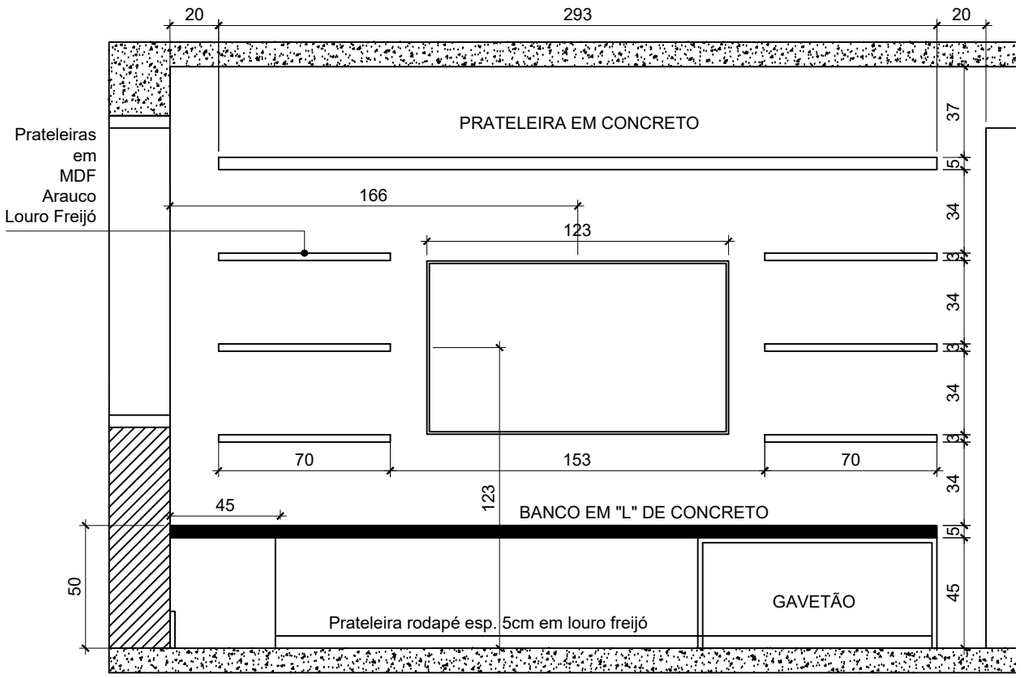

ELEVAÇÃO SALA
escala - 1/25

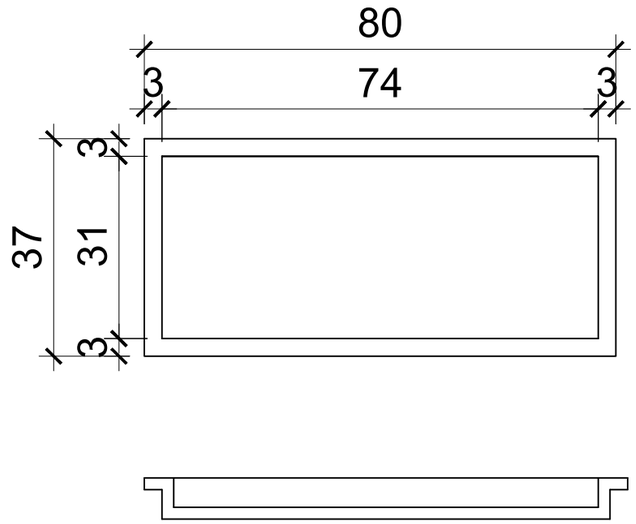

BANDEJA/TAMPA BAÚ
EM MDF LOURO FREIJÓ

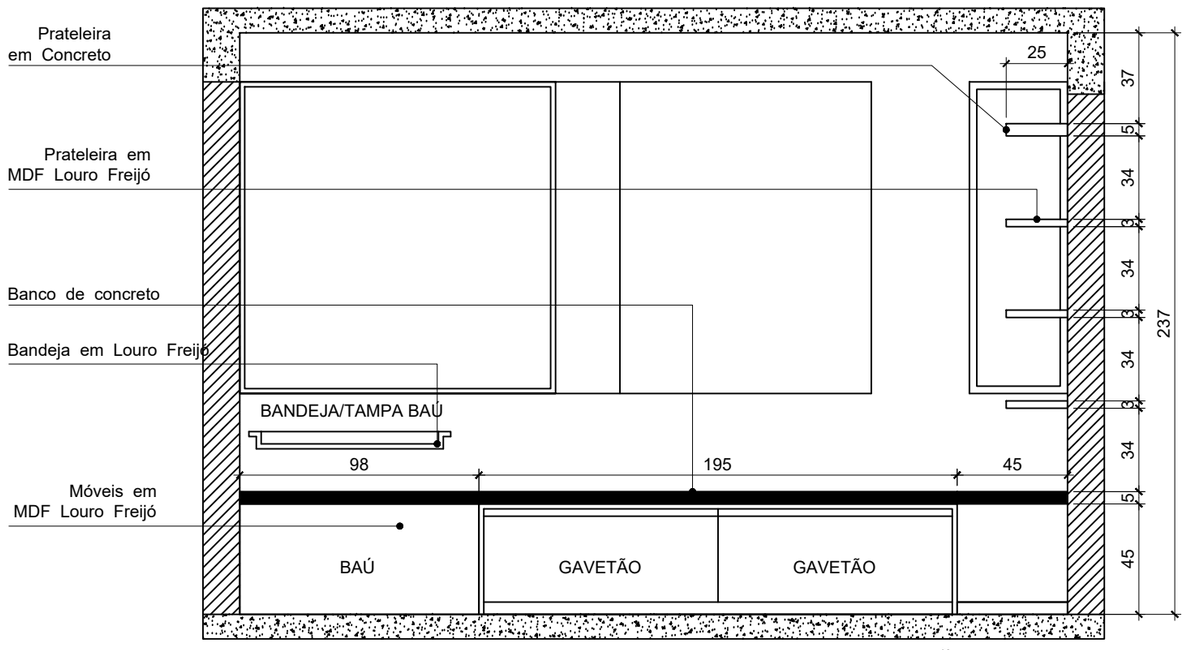

ELEVAÇÃO SALA
escala - 1/25

JMEUREN

98274-3709

PROJETO:

REFORMA DE APARTAMENTO

AUTOR:
jmeuren@gmail.com
CAU/DF 000A487848

CLIENTE:

MURIEL GUEDES & HENRIQUE MEUREN

ENDEREÇO:


SQN 409 BLOCO C aptº 206

PRANCHA:


06

Data:


Dez/2020

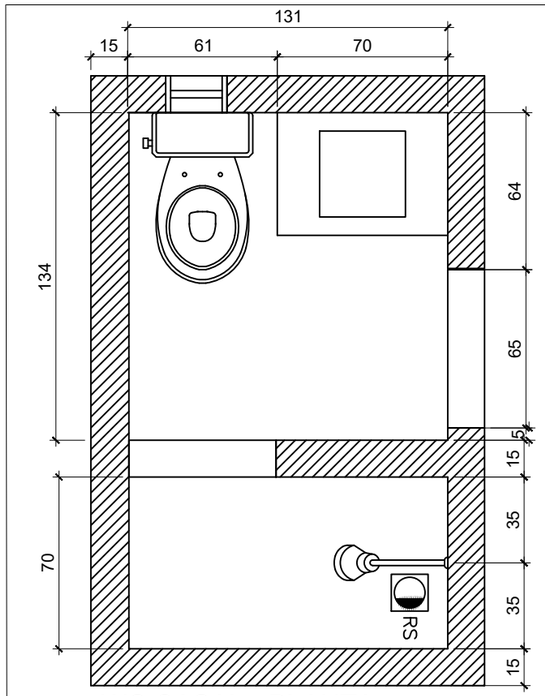


WC CASAL - PLANTA
escala - 1/25

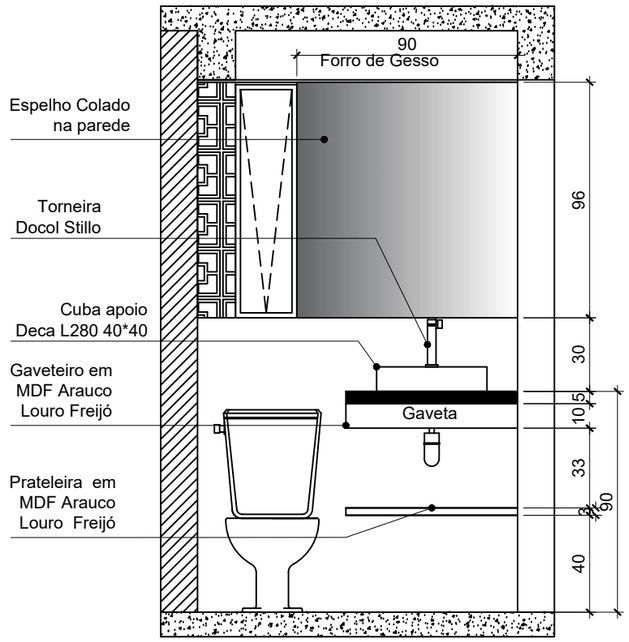


WC CASAL - ELEV. BANCADA
escala - 1/25

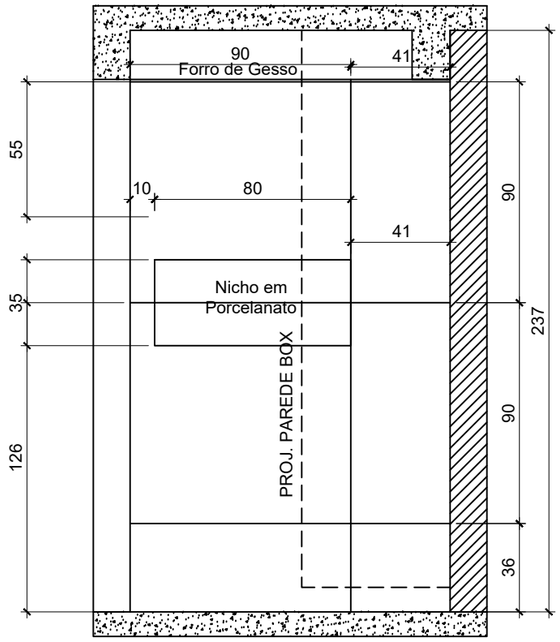

WC CASAL - ELEV. BOX
escala - 1/25

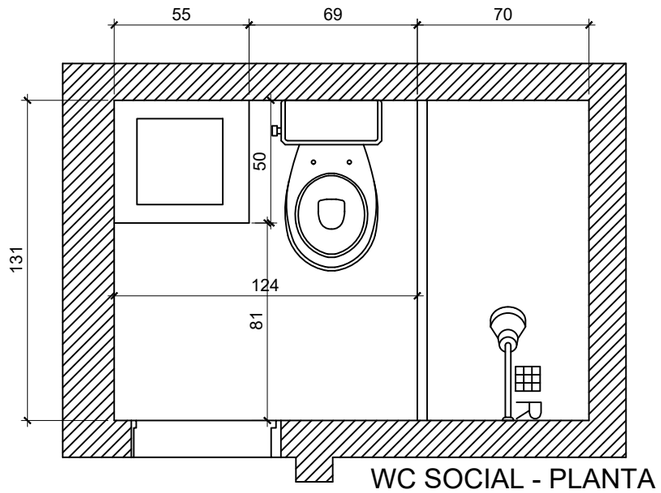


WC SOCIAL - PLANTA
escala - 1/25

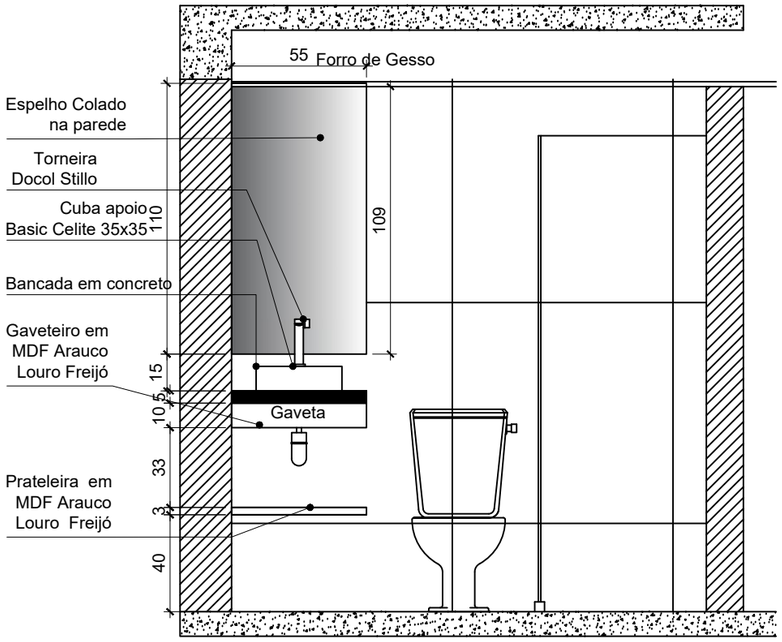


WC SOCIAL - ELEV. BOX
escala - 1/25


JMEUREN 98274-3709	PROJETO: REFORMA DE APARTAMENTO AUTOR: jmeuren@gmail.com CAU/DF 000A487848	CLIENTE: MURIEL GUEDES & HENRIQUE MEUREN ENDEREÇO: SQN 409 BLOCO C aptº 206	PRANCHA: 07 Data: Dez/2020

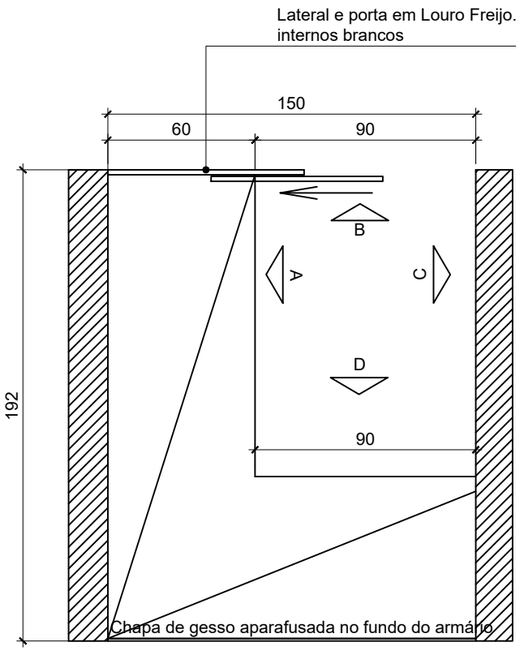

CLOSET - PLANTA
escala - 1/25

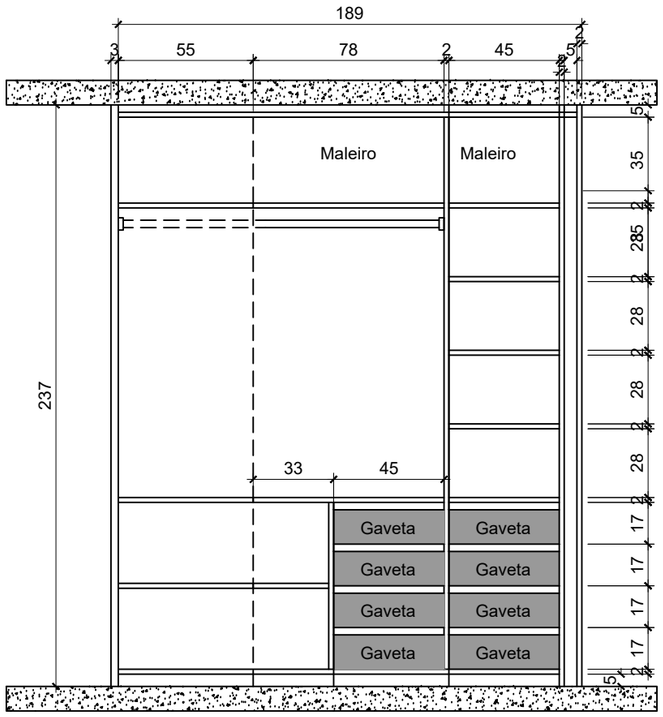


CLOSET - VISTA A
escala - 1/25

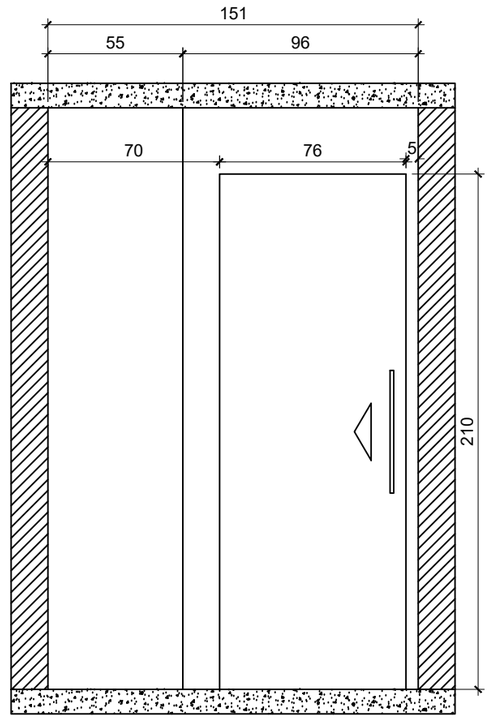


CLOSET - VISTA B
escala - 1/25


JMEUREN 98274–3709	PROJETO: REFORMA DE APARTAMENTO AUTOR: jmeuren@gmail.com CAU/DF 000A487848	CLIENTE: MURIEL GUEDES & HENRIQUE MEUREN ENDEREÇO: SQN 409 BLOCO C aptº 206	PRANCHA: 08 Data: Dez/2020

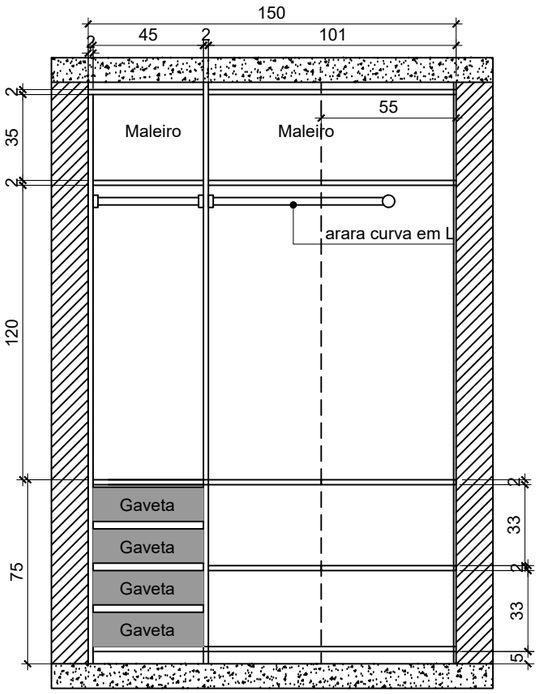

CLOSET - VISTA C
escala - 1/25

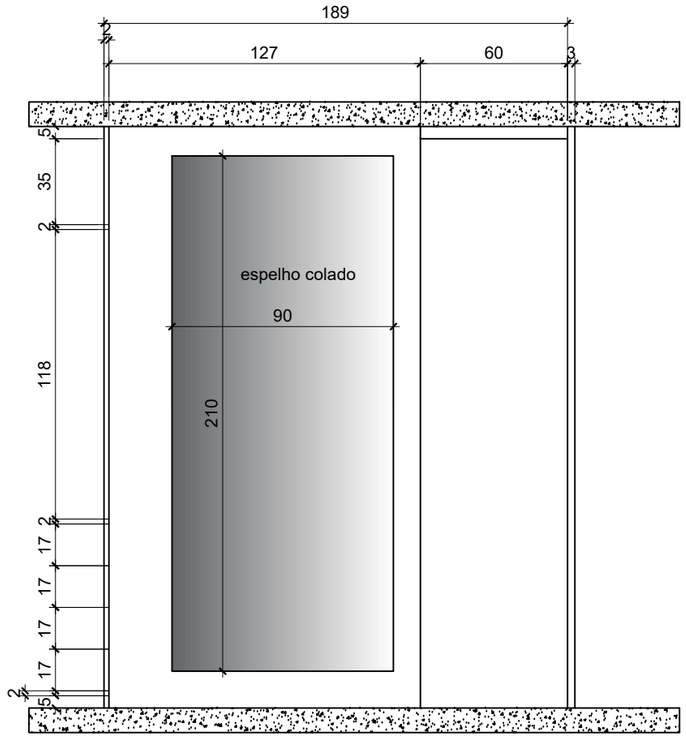


CLOSET - VISTA D
escala - 1/25

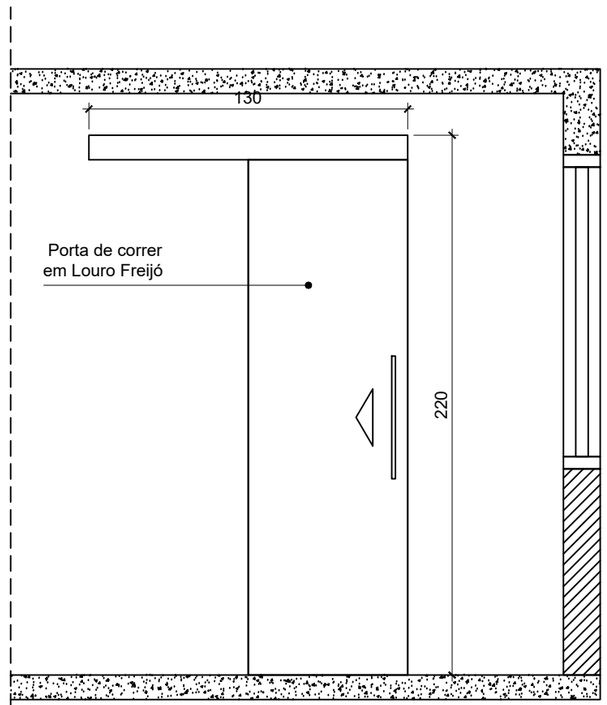

PORTA DE CORRER WC CASAL
escala - 1/25

JMEUREN 98274-3709	PROJETO: REFORMA DE APARTAMENTO AUTOR: jmeuren@gmail.com CAU/DF 000A487848	CLIENTE: MURIEL GUEDES & HENRIQUE MEUREN ENDEREÇO: SQN 409 BLOCO C aptº 206	PRANCHA: 09 Data: Dez/2020

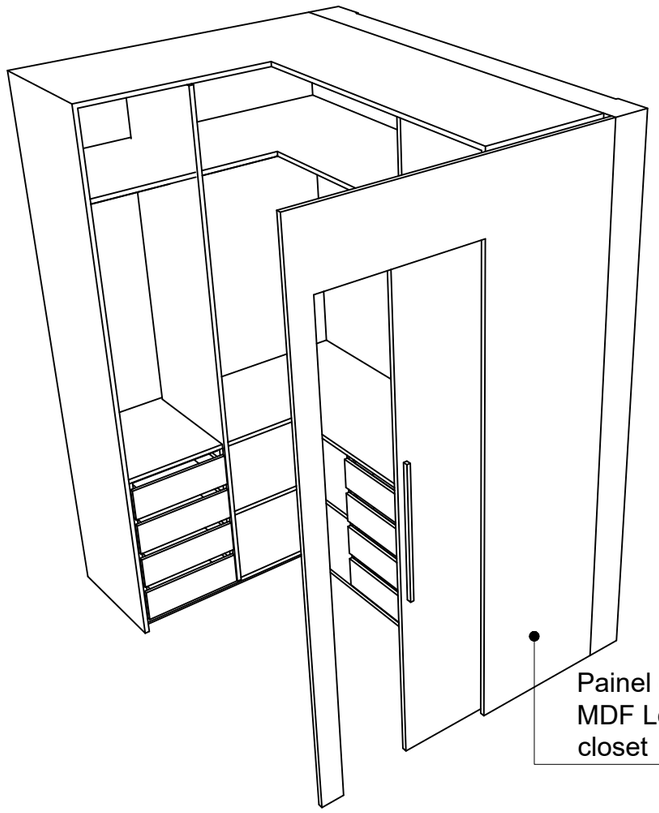

Painel e porta em
MDF Louro Freijó.
closet interno branco



CLOSET - PERSPECTIVA EXTERNA E INTERNA
s/escala

JMEUREN 98274–3709	PROJETO: REFORMA DE APARTAMENTO AUTOR: jmeuren@gmail.com CAU/DF 000A487848	CLIENTE: MURIEL GUEDES & HENRIQUE MEUREN ENDEREÇO: SQN 409 BLOCO C aptº 206	PRANCHA: 10 Data: Dez/2020