

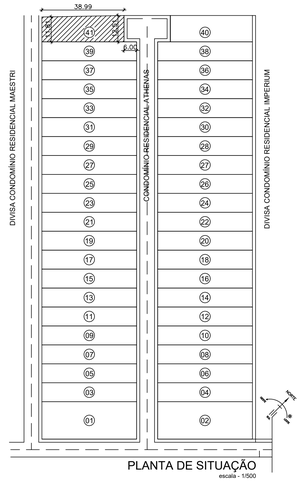



PLANTA DE SITUAÇÃO
escala - 1/500

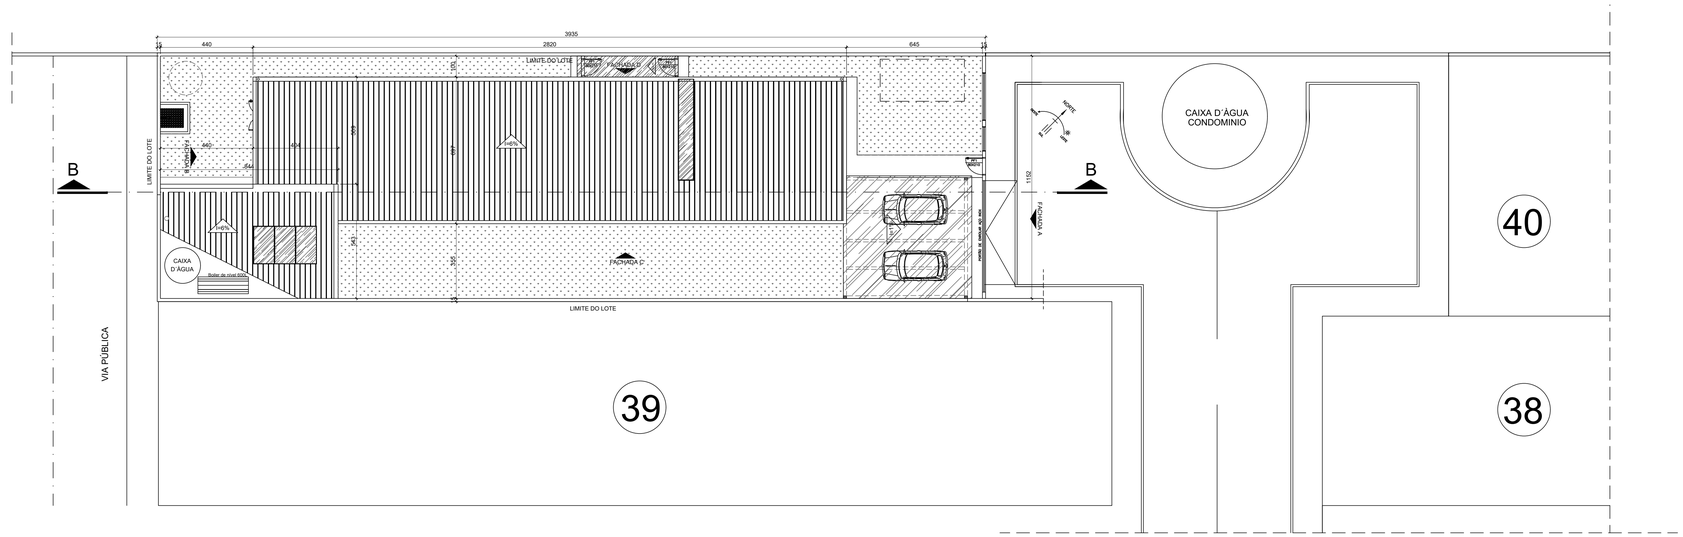


PLANTA DE COBERTURA / LOCAÇÃO
escala - 1/50

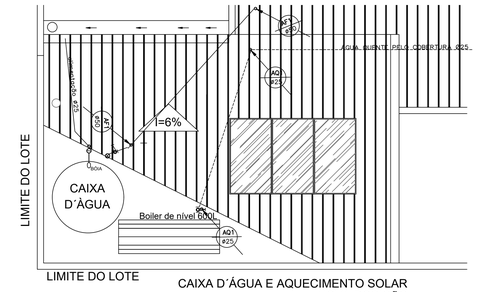

CAIXA D'ÁGUA E AQUECIMENTO SOLAR
NOVA POSIÇÃO
escala - 1/50

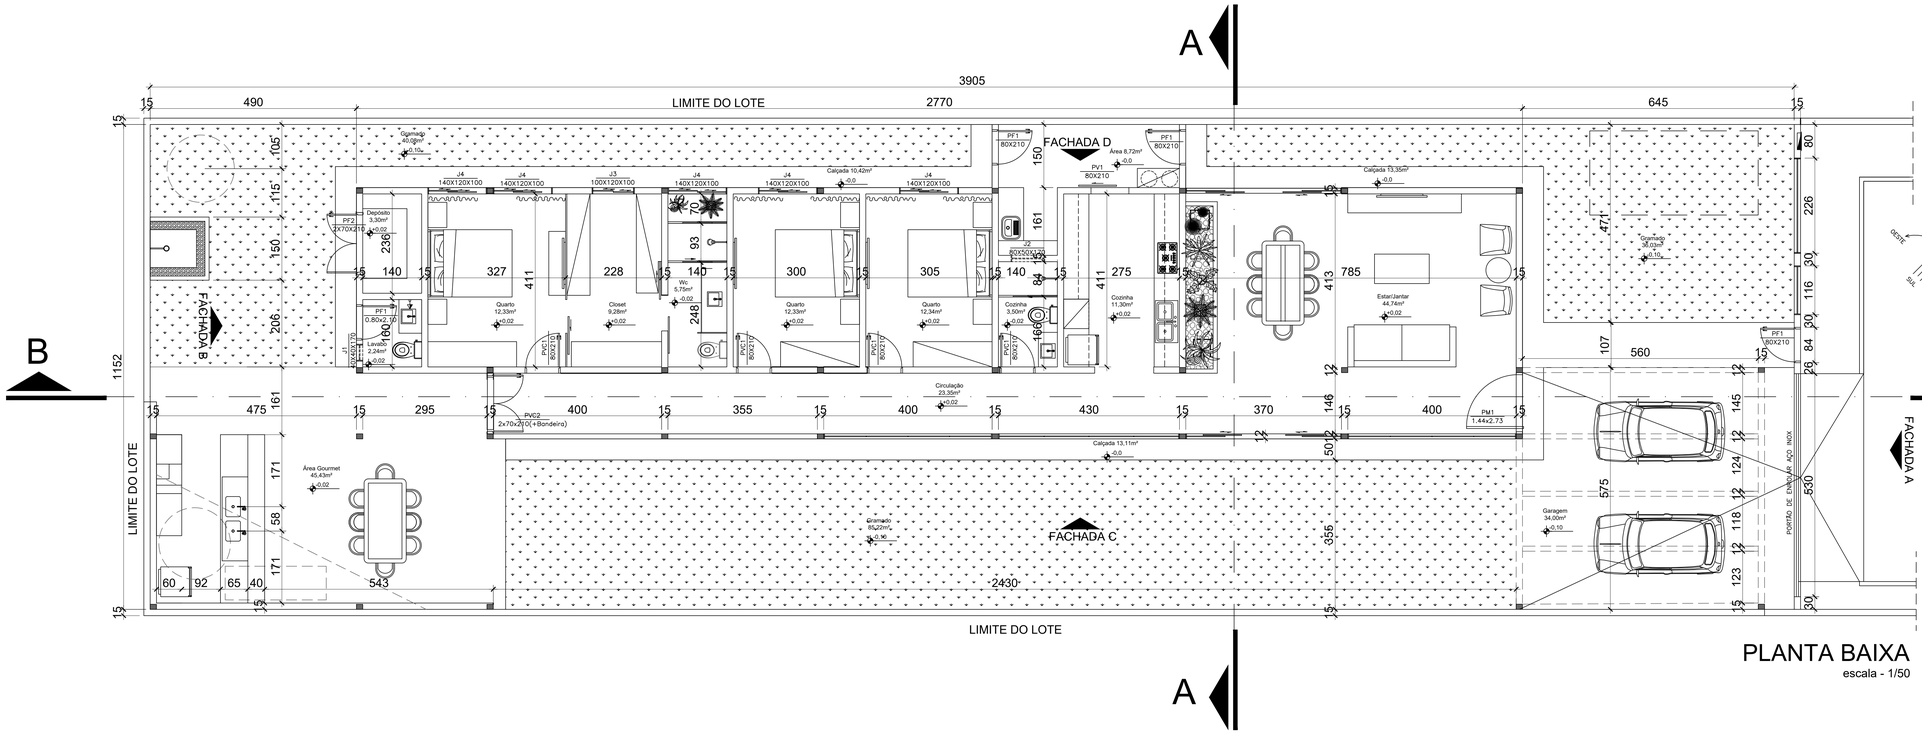

PLANTA BAIXA
escala - 1/50

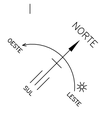

PROJETO ARQUITETURA – RESIDÊNCIA UNIFAMILIAR

ENDEREÇO: N. Rural Ponte Alta Norte Gleba B Rua Rodobelo – Chácara 50 – Cond. Res. Athenas – Lt 41

PROPRIETARIO: LUCIENE BARRETO SANTOS – CPF 279.818.351-00

AUTOR DO PROJETO: JOSÉ ADALBERTO MEUREN – CAU A48784-8

RESPONSAVEL TECNICO: JOSÉ ADALBERTO MEUREN – CAU A48784-8

PROPRIETARIO

AUTOR DO PROJETO

RESP. TÉCNICO


DLFO

DLFO

CREA


PROJETO DE ARQUITETURA

DESENHO Nº:				REVISÃO
01/03	VISTA E CORTE			02
	DATA	ESCALA	AUTOR PROJ.	EXT. ARQ.
	Dezembro/2021	No Poncho	JAM	VISTO	DWG

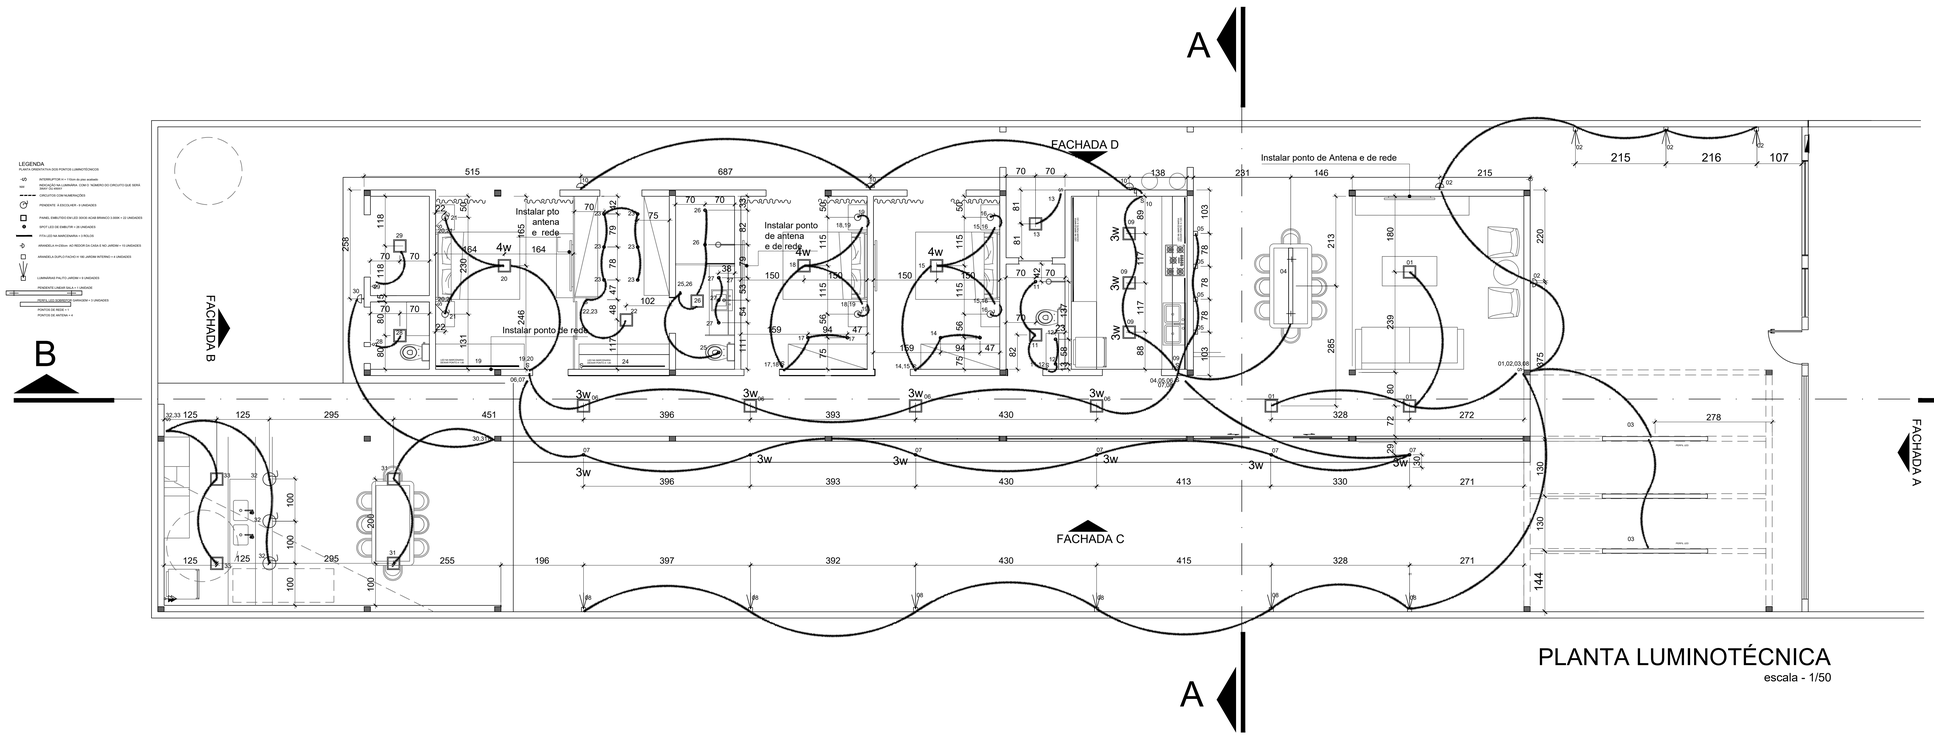

PLANTA LUMINOTÉCNICA

escala - 1/50

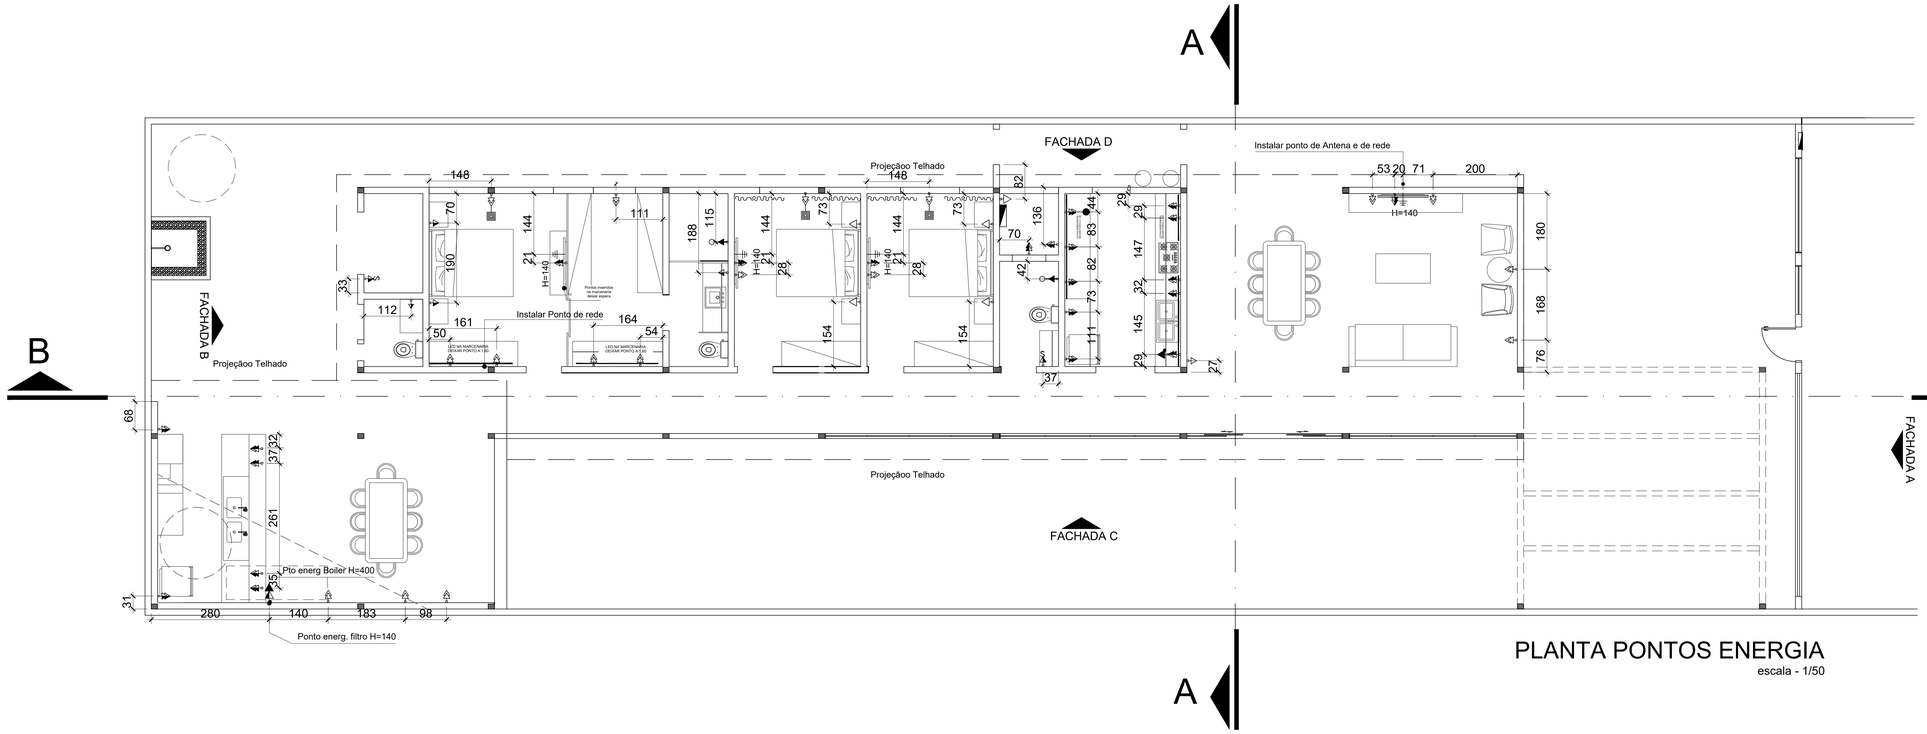

PLANTA PONTOS ENERGIA

escala - 1/50

LEGENDA INSTALAÇÕES

- Tomada Baixa (h=30cm)
- Tomada Média (h=1.10)
- Caixa de passagem para fiação tv plasma
- Ponto de Telefone (h=tomada próxima)
- Tomada Alta (h=220cm) – Deitada
- Ar Condicionado Tipo SPLIT –verificar altura e posição c/fornecedor
- Interfone/Porteiro Eletrônico –verificar altura e posição c/fornecedor
- Ponto antena TV (h=tomada próxima)
- QFL H=140 do piso

PROJETO ARQUITETURA – RESIDÊNCIA UNIFAMILIAR

ENDERECO: N. Rural Ponte Alta Norte Gleba B Rua Rodobelo – Chácara 50 – Cond. Res. Athenas – Lt 41

PROPRIETARIO: LUCIENE BARRETO SANTOS – CPF 279.818.351-00

AUTOR DO PROJETO: JOSÉ ADALBERTO MEUREN – CAU A48784-8

RESPONSAVEL TECNICO: JOSÉ ADALBERTO MEUREN – CAU A48784-8

PROPRIETARIO

AUTOR DO PROJETO

RESP. TÉCNICO


DLFO

DLFO


CREA

PROJETO DE ARQUITETURA


DESENHO Nº:				REVISÃO
02/03				02
DATA	ESCALA	AUTOR PROJ.		EXT. ARQ.
Dezembro/2021	No Prancha	JAM	VISTO	DWG

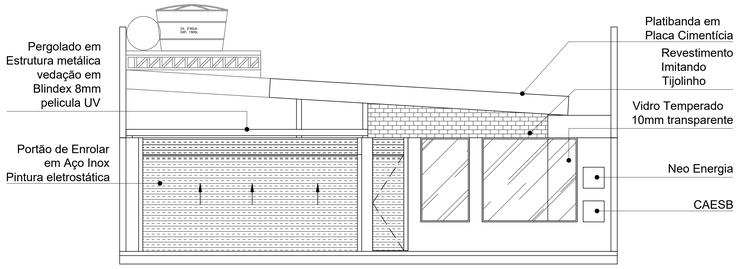

FACHADA A
escala - 1/50

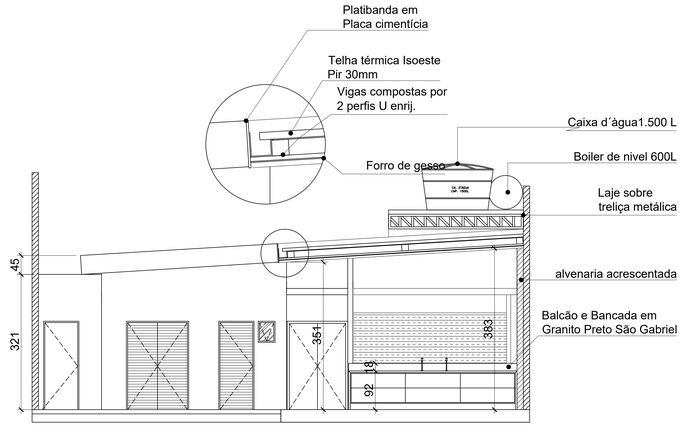

FACHADA B
escala - 1/50

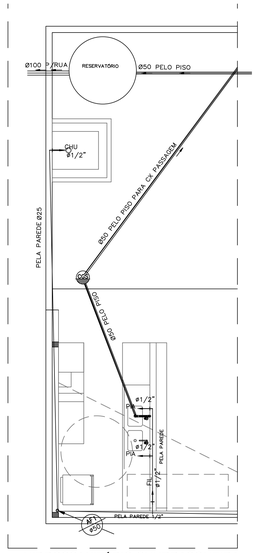

HIDROSSANITÁRIO CHURRASQUEIRA
NOVA POSIÇÃO
escala - 1/50


LEGENDA

- Tubulação de água fria
- Tubulação de água quente
- Ponto de Consumo
- Registro de gaveta (planta e vista) — Planta: RG; Vista: RG
- Registro de pressão (vista) — Vista: RP
- Torneira para jardim
- VCR — Válvula com registro (VCR)
- Conexões (Te, Joelho)
- Cruzamento não conectado
- Tubulação que sobe, continua e desce
- AX X — Indica o tipo e o número da coluna de água (quente/fria))
- ø XX — Indica o diâmetro da coluna de água


CONVENÇÕES

CH – Chuveiro	DCH – Ducha higiênica	MLR – Máquina de lavar roupa
LAV – Lavatório	PIA – Pia de cozinha	CxD – Caixa de descarga
TJ - Torneira de Jardim	MLL – Máquina de lavar louça	TQ – Tanque
VCR – Válvula c. registro	FIL – Filtro	B.HID. – Banheira Hidromassagem


FACHADA C
escala - 1/50

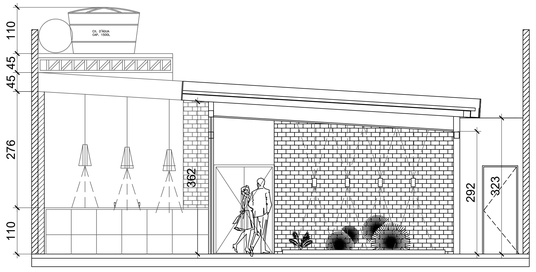

CORTE AA
escala - 1/50

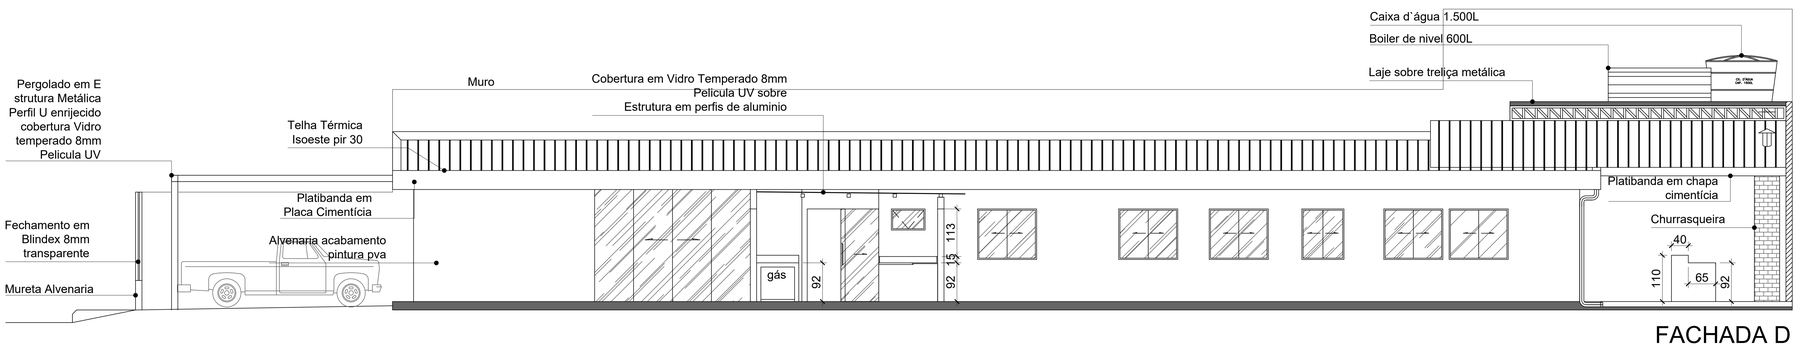

FACHADA D
escala - 1/50

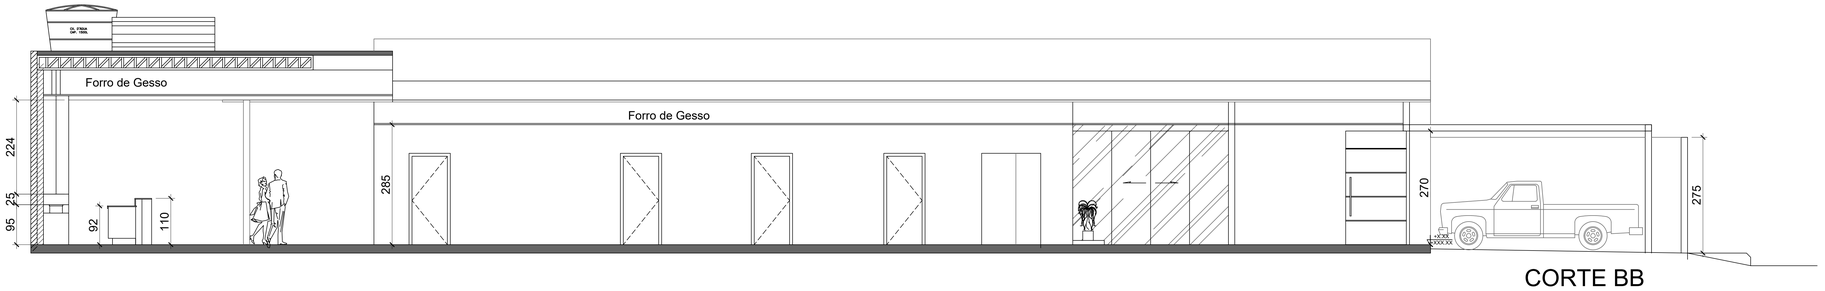

CORTE BB
escala - 1/50

PROJETO ARQUITETURA – RESIDÊNCIA UNIFAMILIAR

ENDEREÇO: N. Rural Ponte Alta Norte Gleba B Rua Rodobelo – Chácara 50 – Cond. Res. Athenas – Lt 4

PROPRIETÁRIO: LUCIENE BARRETO SANTOS – CPF 279.818.351-00

AUTOR DO PROJETO: JOSÉ ADALBERTO MEUREN – CAU A48784-8

RESPONSÁVEL TÉCNICO: JOSÉ ADALBERTO MEUREN – CAU A48784-8

PROPRIETÁRIO

AUTOR DO PROJETO

RESP. TÉCNICO

DLFO

DLFO

CREA

PROJETO DE ARQUITETURA

DESENHO Nº:				REVISÃO
03/03				02
DATA	ESCALA	AUTOR PROJ.		EXT. ARQ.
Dezembro/2021	No Poncho	JAM	VISTO	DWG