CADERNO DE INTERIORES

Projetos Residenciais
Projetos Comerciais
Projetos Interiores

ARQUITETO RESPONSÁVEL:
José Adalberto Meuren
CAU Nº 000A487848
(61)98274-3709
jmeuren@gmail.com


CONTEÚDO DA PRANCHA:
Capa

ESCALA:
Indicada na Prancha

CLIENTE:
Caetana Juracy Rezende Silva
CPF: 576.328.801-78

ENDEREÇO:
SQN 403 Bl N Aptº 306
Brasília

ARQUIVO:
Arq_Int_descrição
REVISÃO Nº:
R00
DATA REVISÃO:
14-11-2025

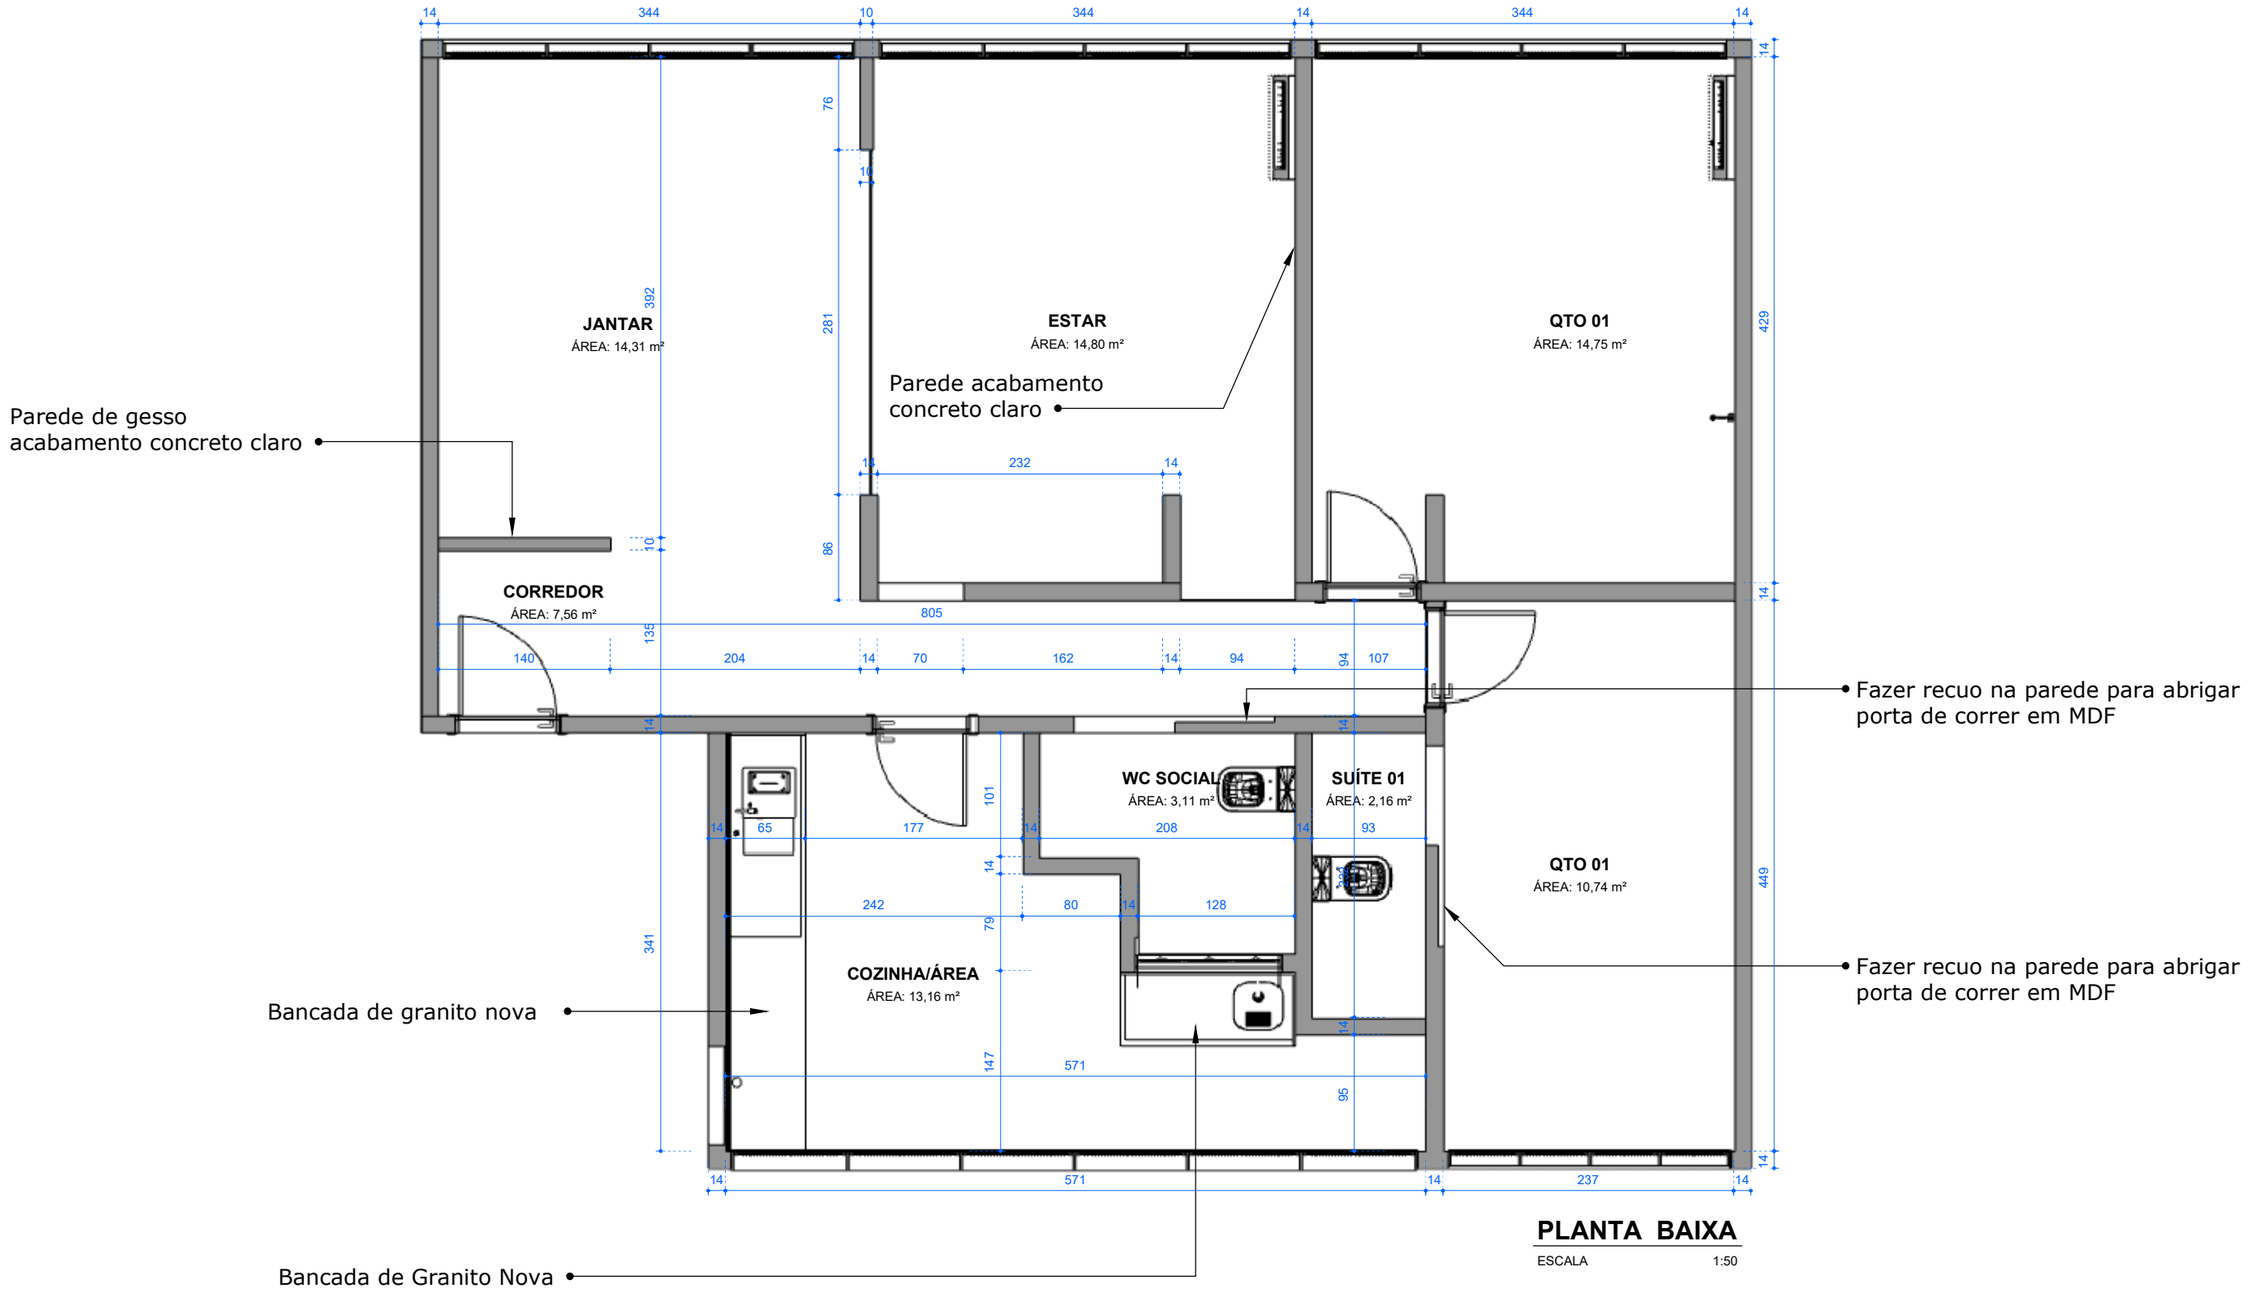

Projetos Residenciais
Projetos Comerciais
Projetos Interiores

ARQUITETO RESPONSÁVEL:
José Adalberto Meuren
CAU Nº 000A487848
(61)98274-3709
jmeuren@gmail.com

CONTEÚDO DA PRANCHA:
Planta Baixa

ESCALA:
Indicada na Prancha

CLIENTE:
Caetana Juracy Rezende Silva
CPF: 576.328.801-78

ENDEREÇO:
SQN 403 Bl N Aptº 306
Brasília


ARQUIVO:
Arq_Int_descrição

REVISÃO Nº:
R00

DATA REVISÃO:
14-11-2025

OBSERVAÇÕES:
Consultar arquiteto em caso de dúvida e/ou alteração;
Conferir medidas no local;
Medidas em cota prevalecem sobre o desenho

FOLHA:
01/11

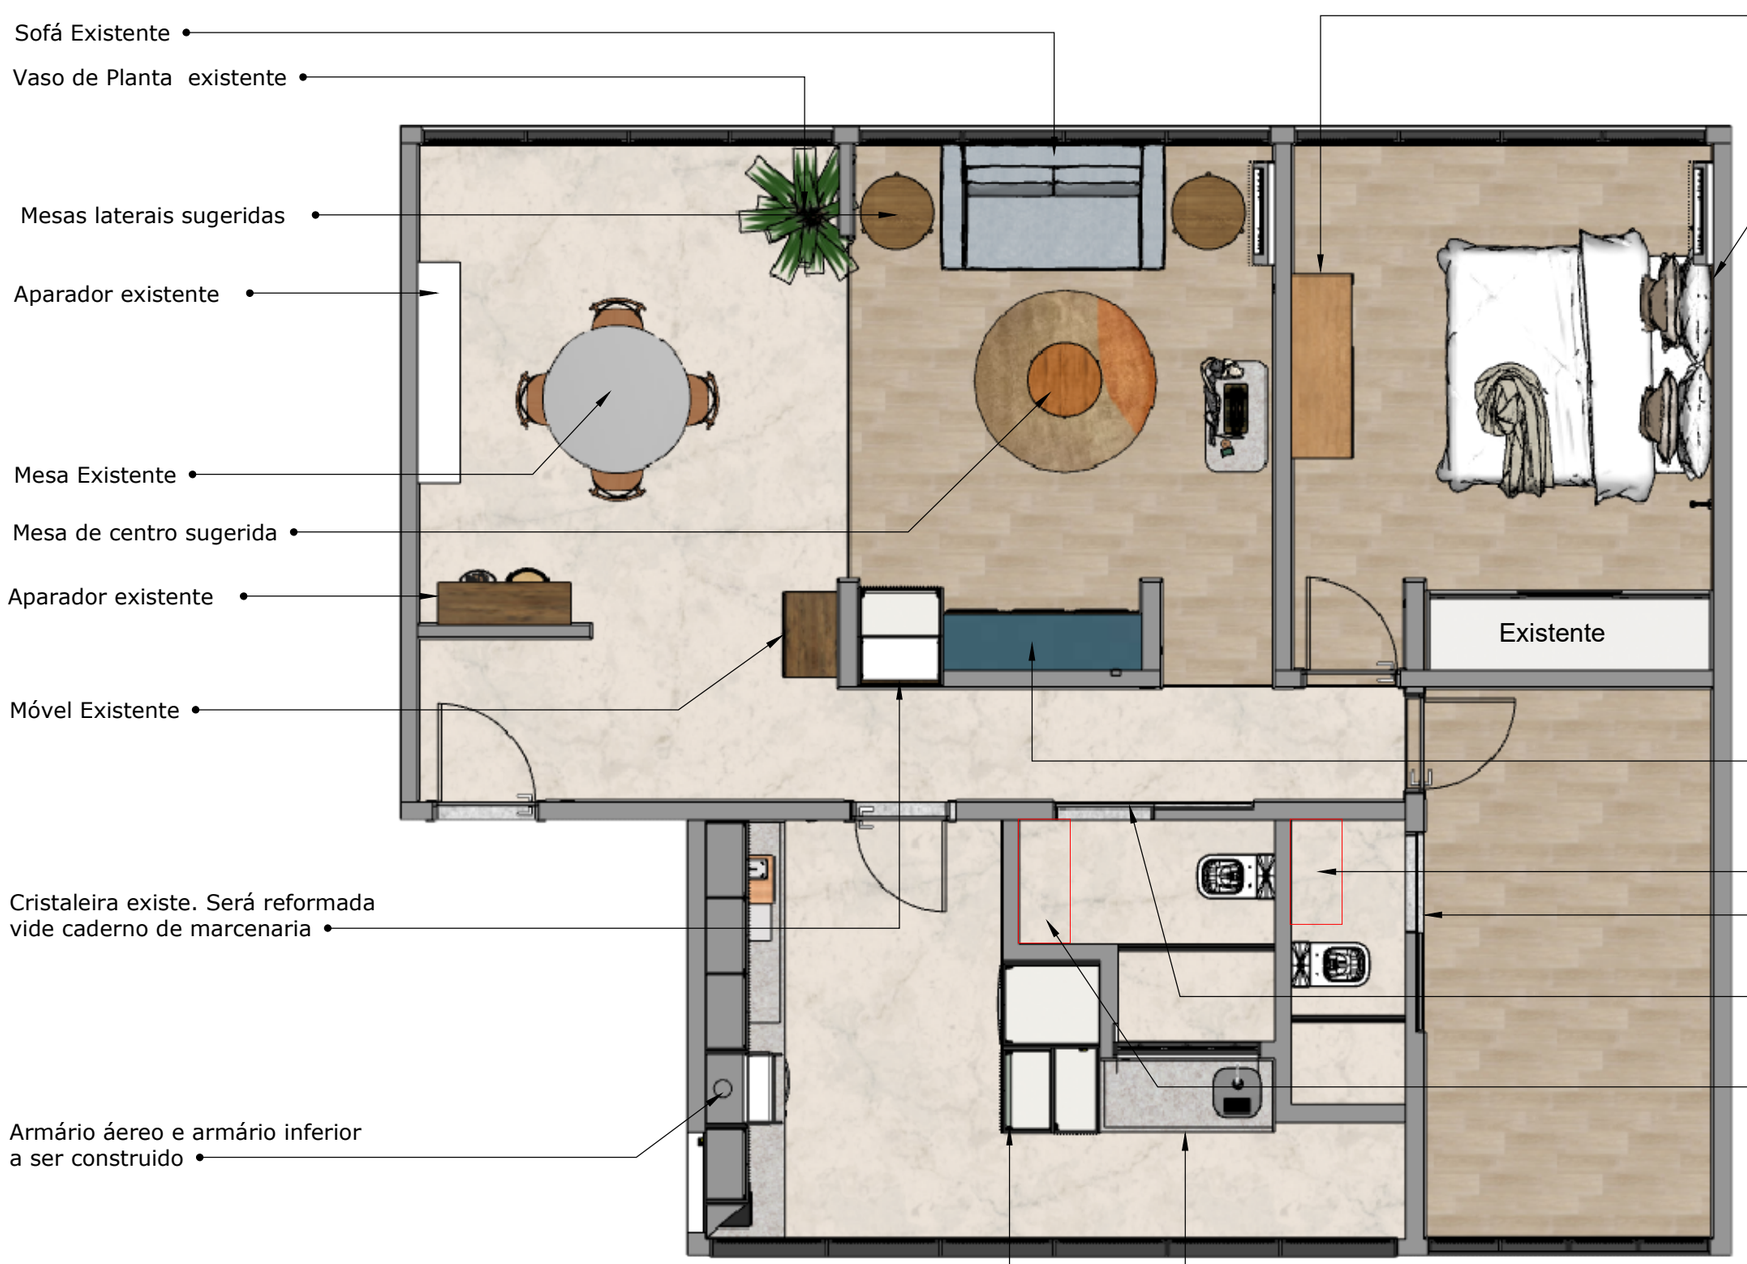

PLANTA LAYOUT

ESCALA 1:50

Projetos Residenciais
Projetos Comerciais
Projetos Interiores

ARQUITETO RESPONSÁVEL:
José Adalberto Meuren
CAU Nº 000A487848
(61)98274-3709
jmeuren@gmail.com

CONTEÚDO DA PRANCHA:
Planta LayOut

ESCALA:
Indicada na Prancha

CLIENTE:
Caetana Juracy Rezende Silva
CPF: 576.328.801-78

ENDEREÇO:
SQN 403 Bl N Aptº 306
Brasília

ARQUIVO:
Arq_Int_descrição

REVISÃO Nº:
R00

DATA REVISÃO:
14-11-2025

OBSERVAÇÕES:
Consultar arquiteto em caso de dúvida e/ou alteração;
Conferir medidas no local;
Medidas em cota prevalecem sobre o desenho

FOLHA:
02/11

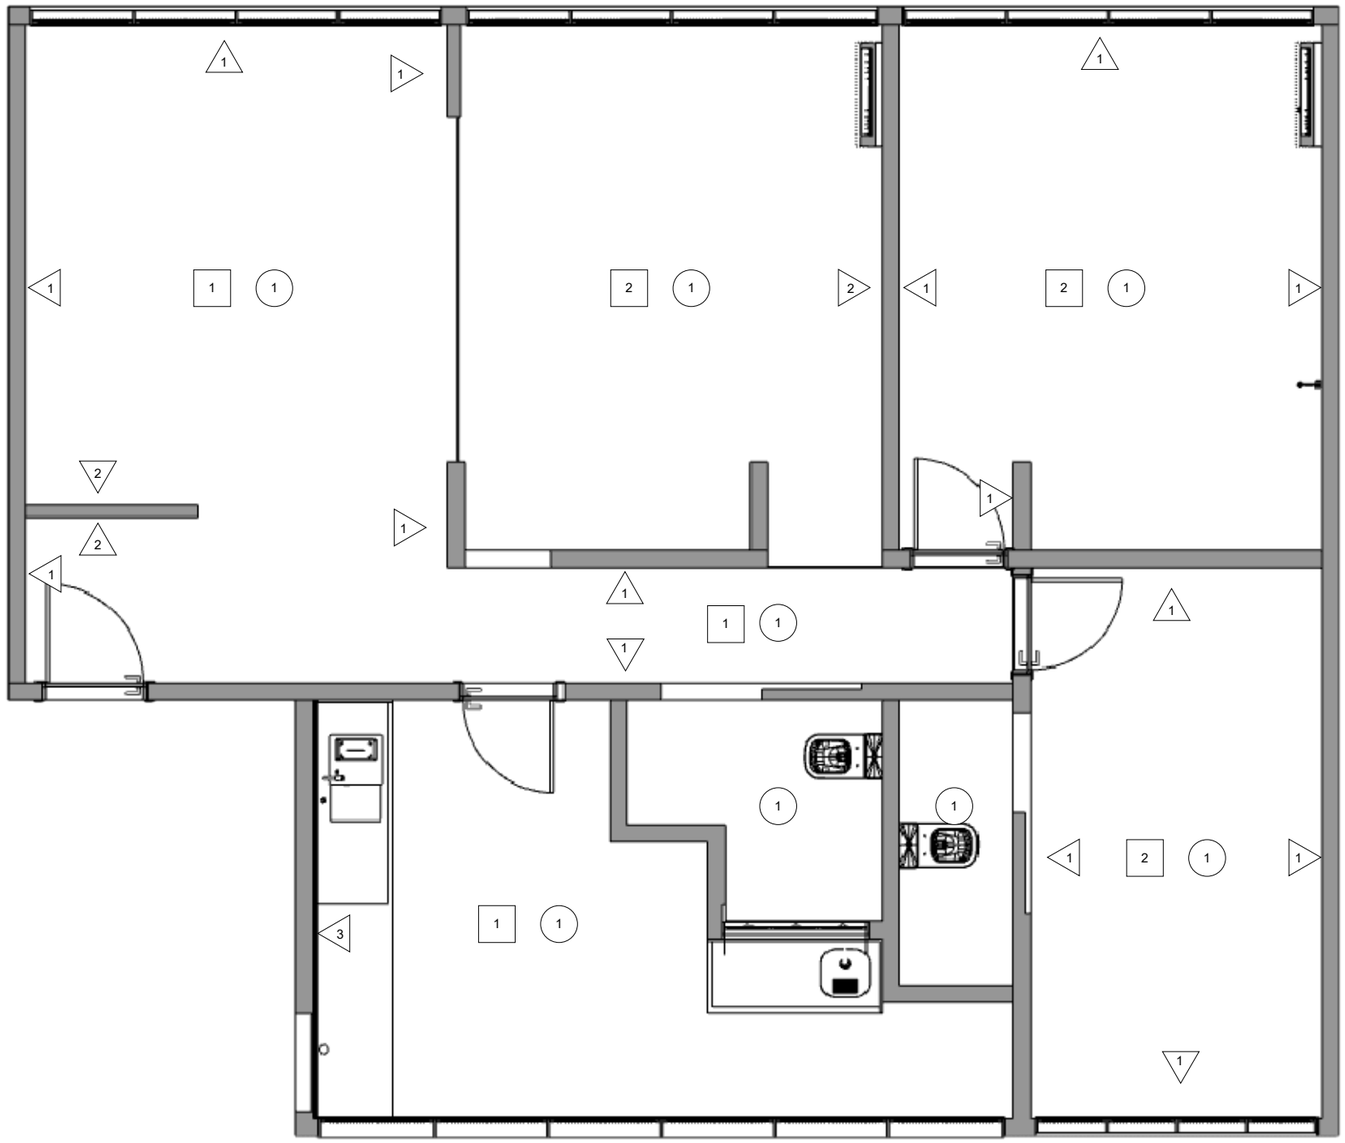


TABELA DE REVESTIMENTOS - PISOS (N)

CÓD	DESCRIÇÃO
01	PORCENALATO EXISTENTE
02	VINÍLICO TARKETT AMBIENTA CEDRO 20,8X123CM

TABELA DE REVESTIMENTOS - PAREDE (A)

CÓD	DESCRIÇÃO
01	SUVINIL PAPEL PICADO ACETINADO
02	MASSA ACABAMENTO CONCRETO CLARO
03	REV. LADRILAR ANDORINHA - TURQ/BRANCO

TABELA DE REVESTIMENTOS - TETO (N)

CÓD	DESCRIÇÃO
01	SUVINIL BRANCO NEVE FOSCO

PLANTA ACABAMENTOS

ESCALA 1:50

ARQUITETURA & INTERIORES

Projetos Residenciais
Projetos Comerciais
Projetos Interiores

ARQUITETO RESPONSÁVEL:
José Adalberto Meuren
CAU Nº 000A487848
(61)98274-3709
jmeuren@gmail.com

CONTEÚDO DA PRANCHA:
Planta Acabamentos

ESCALA:
Indicada na Prancha

CLIENTE:
Caetana Juracy Rezende Silva
CPF: 576.328.801-78

ENDEREÇO:
SQN 403 Bl N Aptº 306
Brasília

ARQUIVO:
Arq_Int_descrição

REVISÃO Nº:
R00

DATA REVISÃO:
14-11-2025

OBSERVAÇÕES:
Consultar arquiteto em caso de dúvida e/ou alteração;
Conferir medidas no local;
Medidas em cota prevalecem sobre o desenho

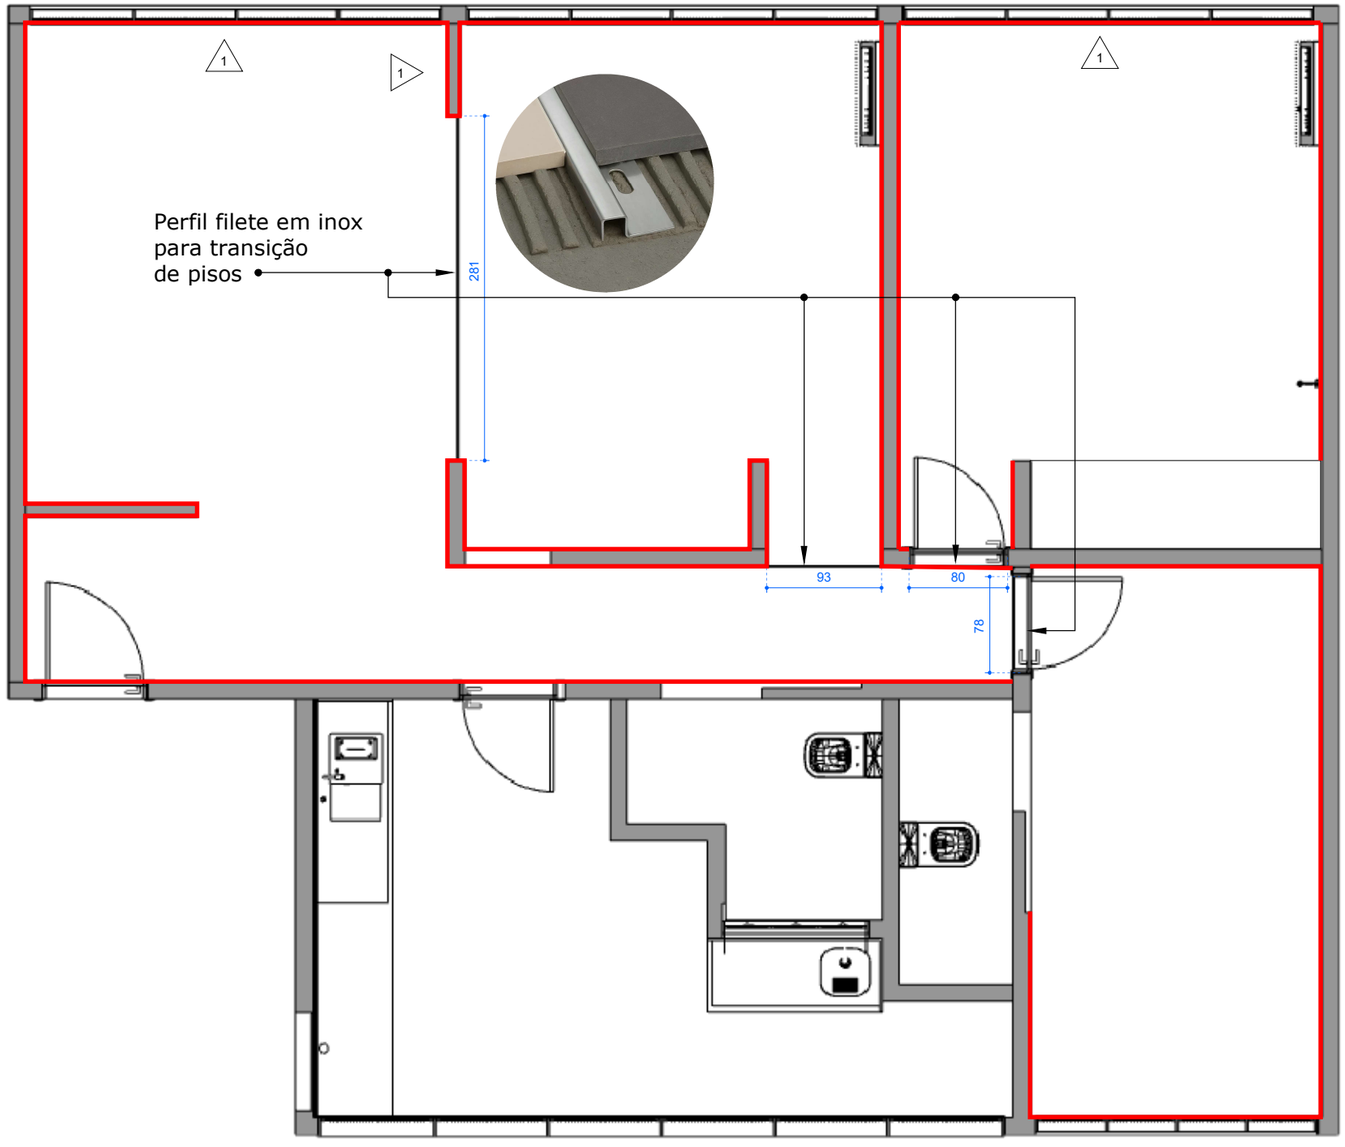


TABELA DE REVESTIMENTOS - RODAPÉ

N

CÓD	DESCRIÇÃO
01	RODAPÉ SANTA LUZIA H=15CM

PLANTA RODAPÉ E FILETES

ESCALA 1:50

ARQUITETURA & INTERIORES j.m

Projetos Residenciais
Projetos Comerciais
Projetos Interiores

ARQUITETO RESPONSÁVEL:
José Adalberto Meuren
CAU Nº 000A487848
(61)98274-3709
jmeuren@gmail.com

CONTEÚDO DA PRANCHA:
Planta Rodapé

ESCALA:
Indicada na Prancha

CLIENTE:
Caetana Juracy Rezende Silva
CPF: 576.328.801-78

ENDEREÇO:
SQN 403 Bl N Aptº 306
Brasília


ARQUIVO:
Arq_Int_descrição

REVISÃO Nº:
R00

DATA REVISÃO:
14-11-2025

OBSERVAÇÕES:
Consultar arquiteto em caso de dúvida e/ou alteração;
Conferir medidas no local;
Medidas em cota prevalecem sobre o desenho

FOLHA:
04/11

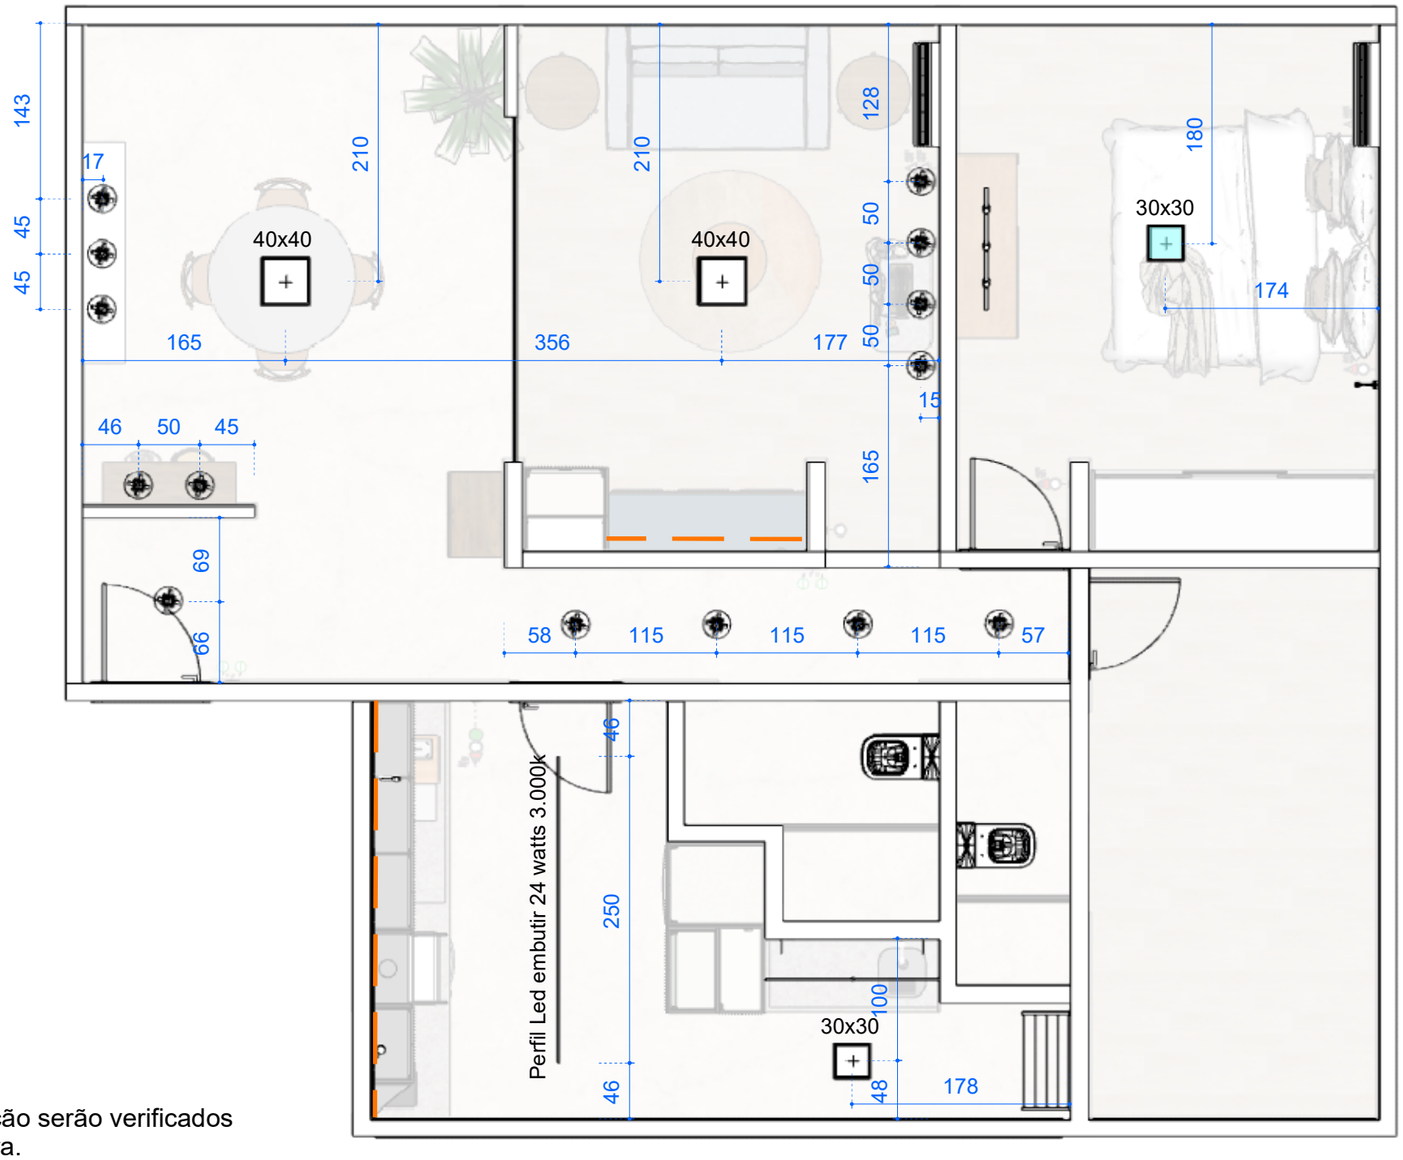

LEGENDA

- Interruptor Simples
- Interruptor de 2 Seções
- Interruptor de 3 Seções
- Interruptor Paralelo
- Interruptor Intermediário
- Plafon de Sobrepor
- Plafon de Embutir
- Mini dicróica quad. direc. emb. 3.000k

Fita led 9watts emb. marcenaria 3.000k

OBS:
Os circuitos de iluminação serão verificados no local no inicio da obra.

PLANTA LUMINÁRIAS

ESCALA 1:50

Projetos Residenciais
Projetos Comerciais
Projetos Interiores

ARQUITETO RESPONSÁVEL:
José Adalberto Meuren
CAU Nº 000A487848
(61)98274-3709
jmeuren@gmail.com

CONTEÚDO DA PRANCHA:
Planta Luminárias

ESCALA:
Indicada na Prancha

CLIENTE:
Caetana Juracy Rezende Silva
CPF: 576.328.801-78


ENDEREÇO:
SQN 403 Bl N Aptº 306
Brasília

ARQUIVO:
Arq_Int_descrição

REVISÃO Nº:
R00

DATA REVISÃO:
14-11-2025

OBSERVAÇÕES:
Consultar arquiteto em caso de dúvida e/ou alteração;
Conferir medidas no local;
Medidas em cota prevalecem sobre o desenho

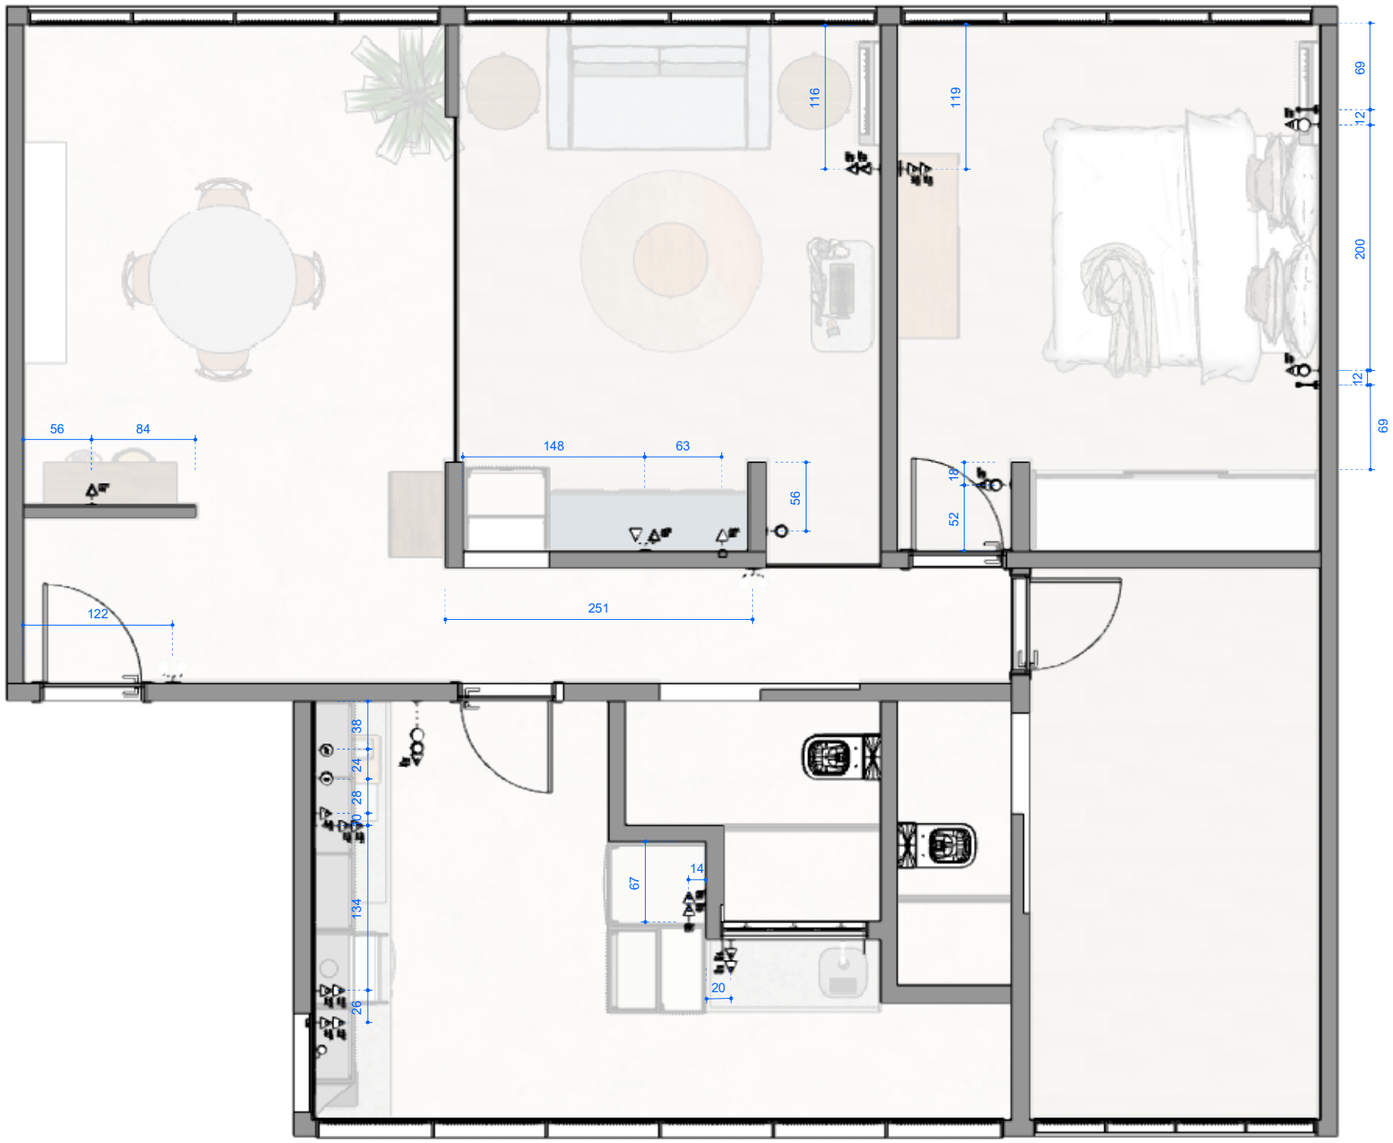

LEGENDA

- Interruptor Simples
- Interruptor de 2 Seções
- Interruptor de 3 Seções
- Interruptor Paralelo
- Interruptor Intermediário
- Tomada Baixa
- Tomada Média
- Tomada Alta
- Tomada Alt. Personalizada
- Módulo Furo
- Módulo Cego
- RJ-11 Telefone
- RJ-11 Interfone
- RJ-45
- Campainha Cigarra
- Campainha Pulsador
- Dimmer
- Sensor
- Ventilador Dimmer
- Ventilador Variador
- Antena Baixa
- Antena Média
- Antena Alta
- Água Fria
- Esgoto

PLANTA PONTOS

ESCALA 1:50

ARQUITETURA & INTERIORES

Projetos Residenciais
Projetos Comerciais
Projetos Interiores

ARQUITETO RESPONSÁVEL:
José Adalberto Meuren
CAU Nº 000A487848
(61)98274-3709
jmeuren@gmail.com

CONTEÚDO DA PRANCHA:
Planta Pontos

ESCALA:
Indicada na Prancha

CLIENTE:
Caetana Juracy Rezende Silva
CPF: 576.328.801-78

ENDEREÇO:
SQN 403 Bl N Aptº 306
Brasília

ARQUIVO:
Arq_Int_descrição

REVISÃO Nº:
R00

DATA REVISÃO:
14-11-2025

OBSERVAÇÕES:
Consultar arquiteto em caso de dúvida e/ou alteração;
Conferir medidas no local;
Medidas em cota prevalecem sobre o desenho

Paredes em acabamento
Suvinil Papel Picado

Parede de Gesso revestida em
acabamento concreto claro


Cristaleira existente. Reformar adicionando portas em vidro canelado, iluminação em fita led nas laterais e interior em Freijó, conforme caderno de marcenaria



VISTA 1
ESCALA 1:50

Paredes em acabamento
Suvinil Papel Picado

Parede de Gesso revestida em
acabamento concreto claro

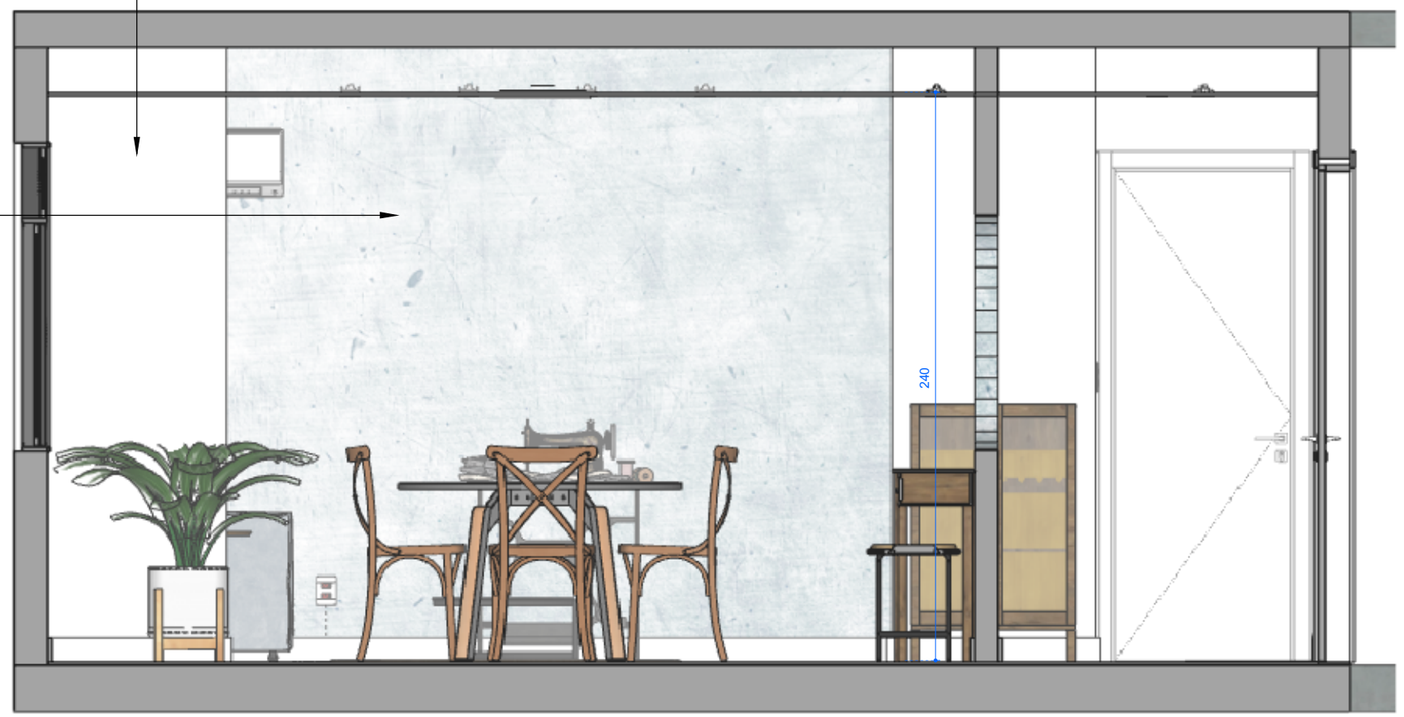

VISTA 2
ESCALA 1:50

ARQUITETURA & INTERIORES

Projetos Residenciais
Projetos Comerciais
Projetos Interiores

ARQUITETO RESPONSÁVEL:
José Adalberto Meuren
CAU Nº 000A487848
(61)98274-3709
jmeuren@gmail.com

CONTEÚDO DA PRANCHA:
Vistas 1 e 2

ESCALA:
Indicada na Prancha

CLIENTE:
Caetana Juracy Rezende Silva
CPF: 576.328.801-78

ENDEREÇO:
SQN 403 Bl N Aptº 306
Brasília

ARQUIVO:
Arq_Int_descrição
REVISÃO Nº:
R00
DATA REVISÃO:
14-11-2025

OBSERVAÇÕES:
Consultar arquiteto em caso de dúvida e/ou alteração;
Conferir medidas no local;
Medidas em cota prevalecem sobre o desenho

FOLHA:



VISTA 3

ESCALA 1:50



VISTA 4

ESCALA 1:50

Projetos Residenciais
Projetos Comerciais
Projetos Interiores

ARQUITETO RESPONSÁVEL:
José Adalberto Meuren
CAU Nº 000A487848
(61)98274-3709
jmeuren@gmail.com

CONTEÚDO DA PRANCHA:
Vistas 3 e 4

ESCALA:
Indicada na Prancha

CLIENTE:
Caetana Juracy Rezende Silva
CPF: 576.328.801-78

ENDEREÇO:
SQN 403 Bl N Aptº 306
Brasília


ARQUIVO:
Arq_Int_descrição

REVISÃO Nº:
R00

DATA REVISÃO:
14-11-2025


OBSERVAÇÕES:
Consultar arquiteto em caso de dúvida e/ou alteração;
Conferir medidas no local;
Medidas em cota prevalecem sobre o desenho

FOLHA:
08/11

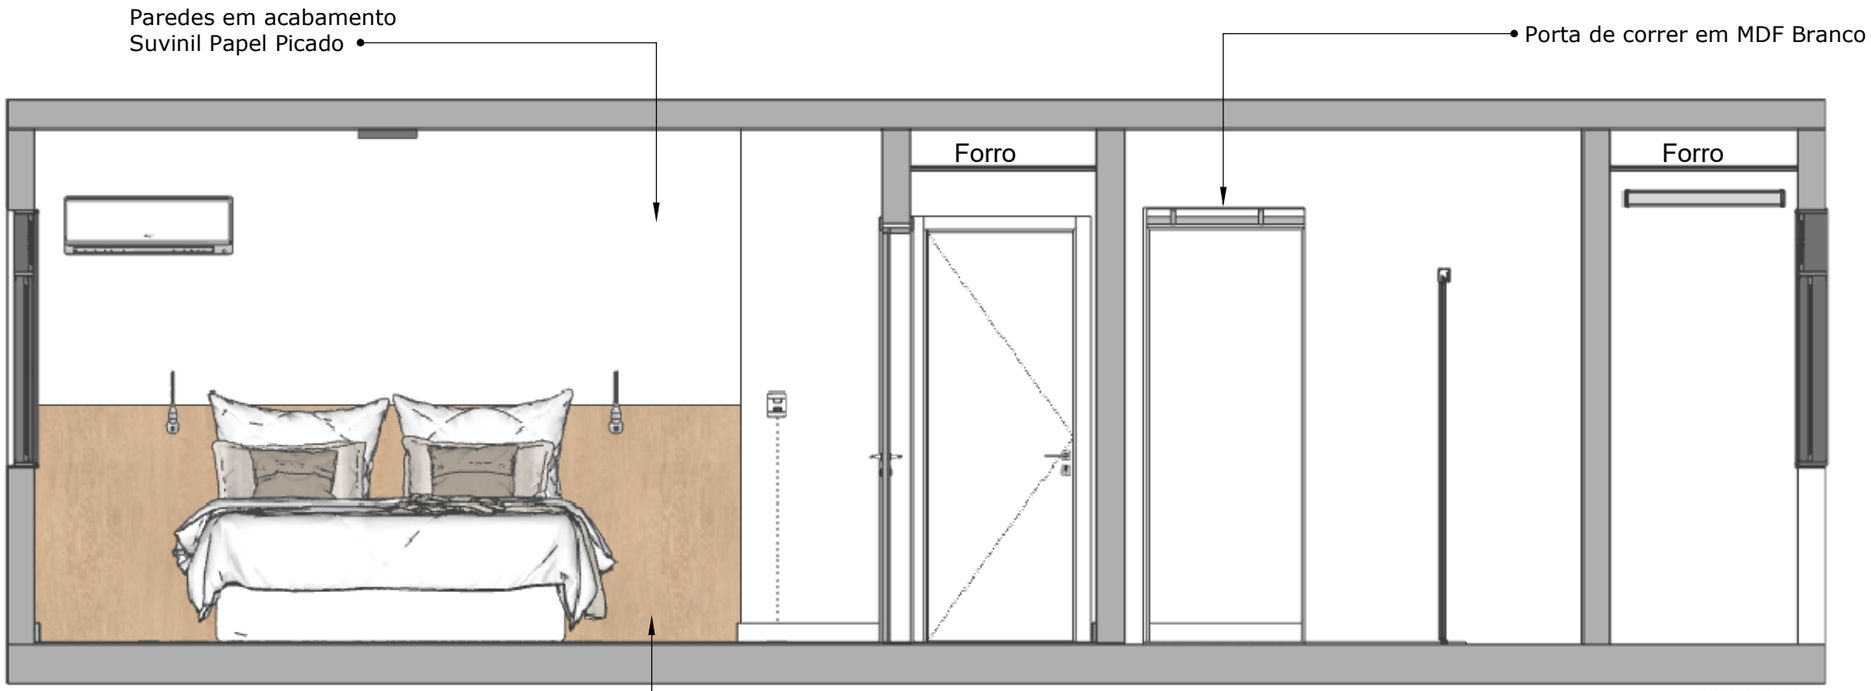

VISTA 5

ESCALA 1:50

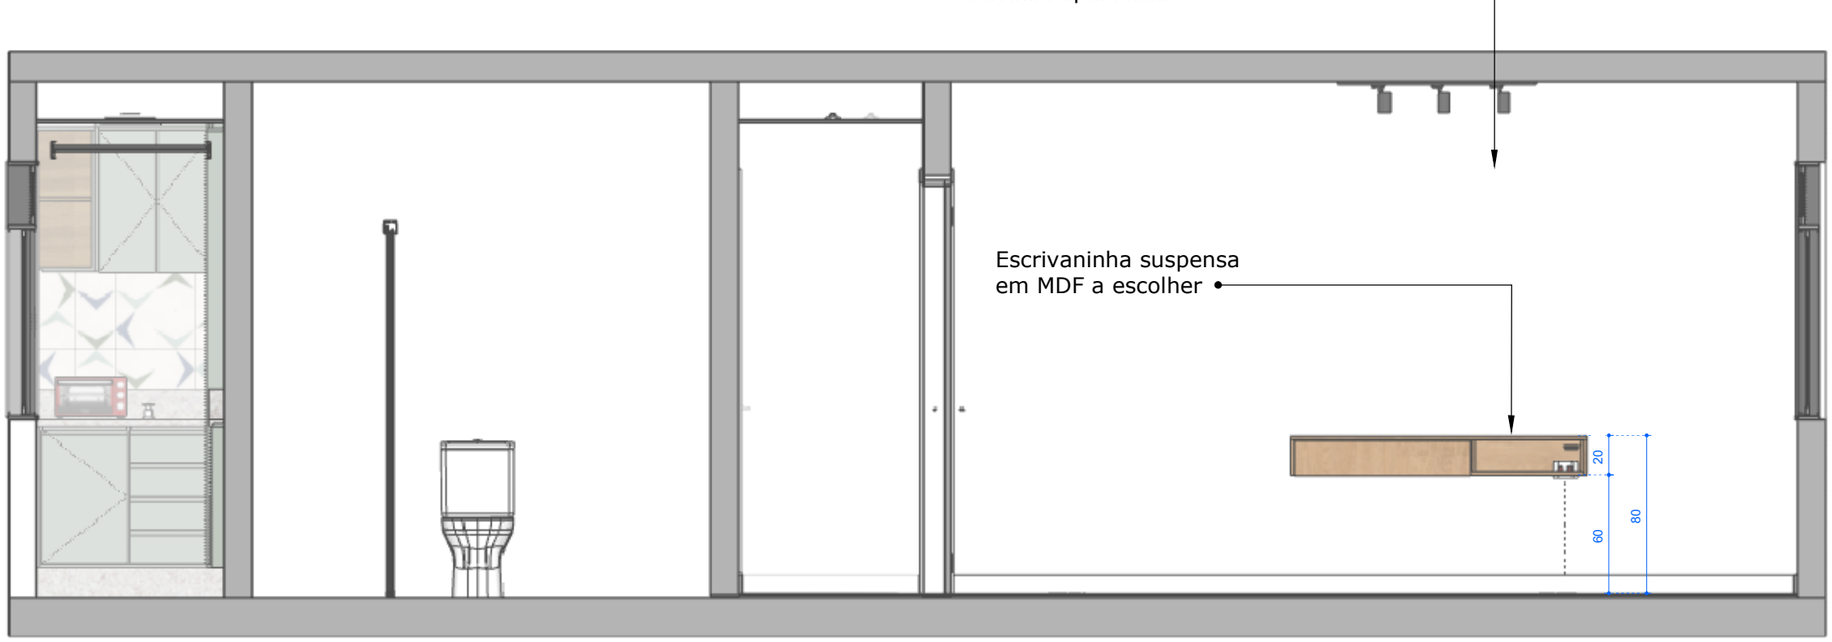

VISTA 6

ESCALA 1:50

ARQUITETURA & INTERIORES

Projetos Residenciais
Projetos Comerciais
Projetos Interiores

ARQUITETO RESPONSÁVEL:
José Adalberto Meuren
CAU Nº 000A487848
(61)98274-3709
jmeuren@gmail.com

CONTEÚDO DA PRANCHA:
Vistas 5 e 6

ESCALA:
Indicada na Prancha

CLIENTE:
Caetana Juracy Rezende Silva
CPF: 576.328.801-78

ENDEREÇO:
SQN 403 Bl N Aptº 306
Brasília

ARQUIVO:
Arq_Int_descrição

REVISÃO Nº:
R00

DATA REVISÃO:
14-11-2025


OBSERVAÇÕES:
Consultar arquiteto em caso de dúvida e/ou alteração;
Conferir medidas no local;
Medidas em cota prevalecem sobre o desenho

FOLHA:
09/11



VISTA 7

ESCALA 1:50

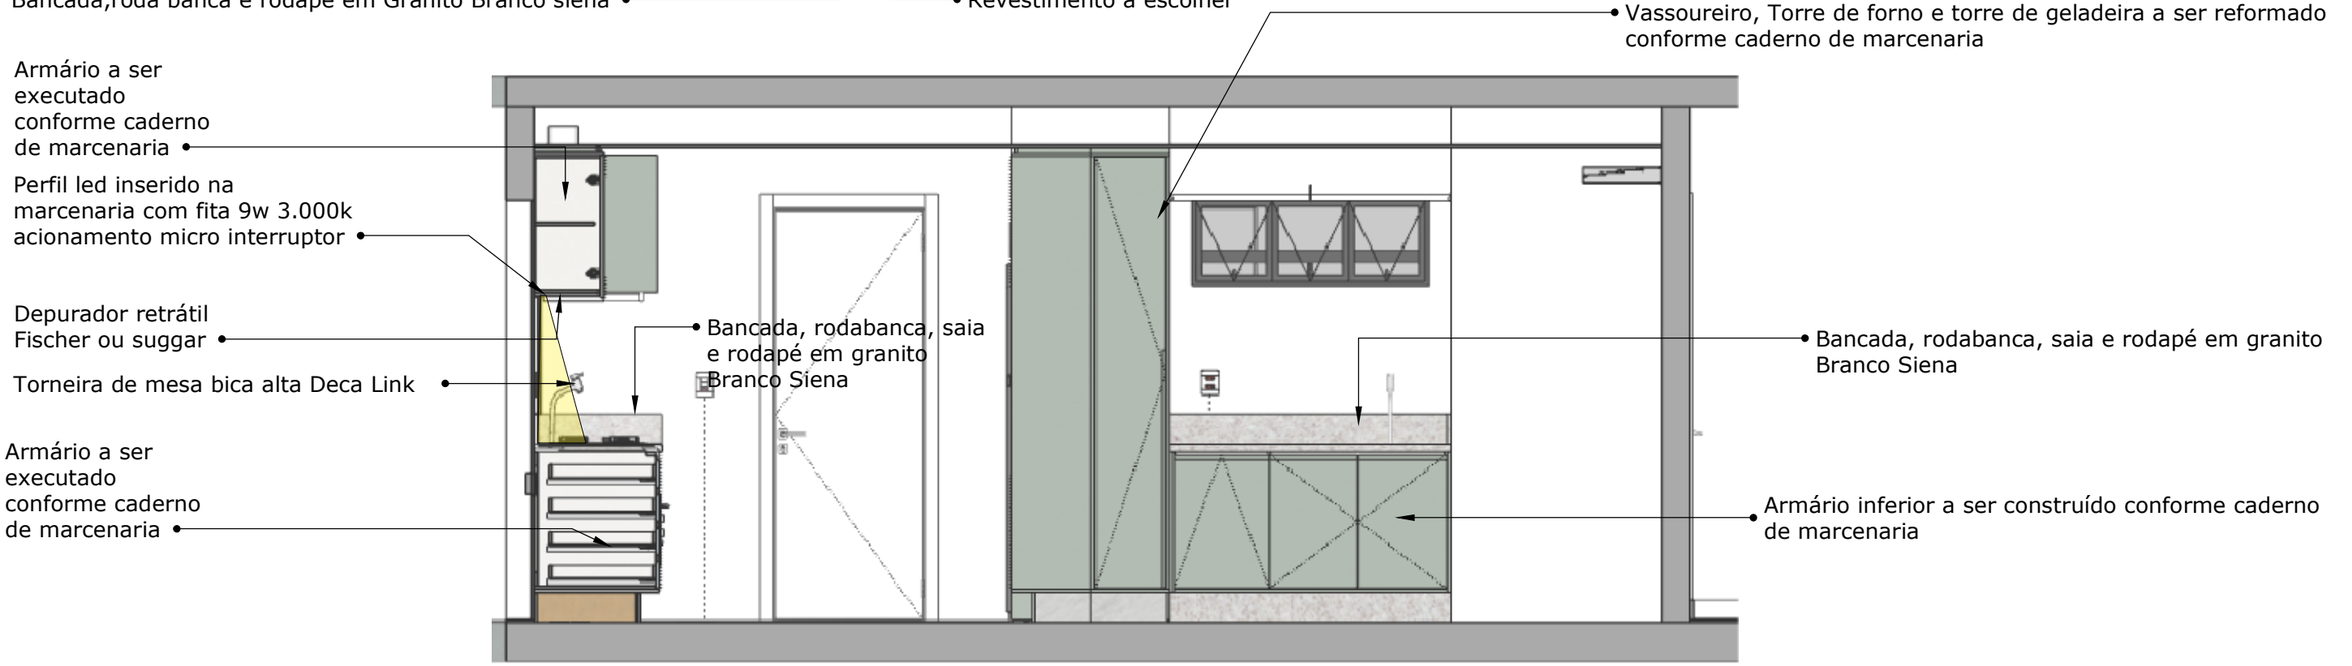

VISTA 8

ESCALA 1:50

ARQUITETURA & INTERIORES j.m

Projetos Residenciais
Projetos Comerciais
Projetos Interiores

ARQUITETO RESPONSÁVEL:
José Adalberto Meuren
CAU Nº 000A487848
(61)98274-3709
jmeuren@gmail.com

CONTEÚDO DA PRANCHA:
Vistas 7 e 8

ESCALA:
Indicada na Prancha

CLIENTE:
Caetana Juracy Rezende Silva
CPF: 576.328.801-78


ENDEREÇO:
SQN 403 Bl N Aptº 306
Brasília

ARQUIVO:
Arq_Int_descrição

REVISÃO Nº:
R00


DATA REVISÃO:
14-11-2025


OBSERVAÇÕES:
Consultar arquiteto em caso de dúvida e/ou alteração;
Conferir medidas no local;
Medidas em cota prevalecem sobre o desenho

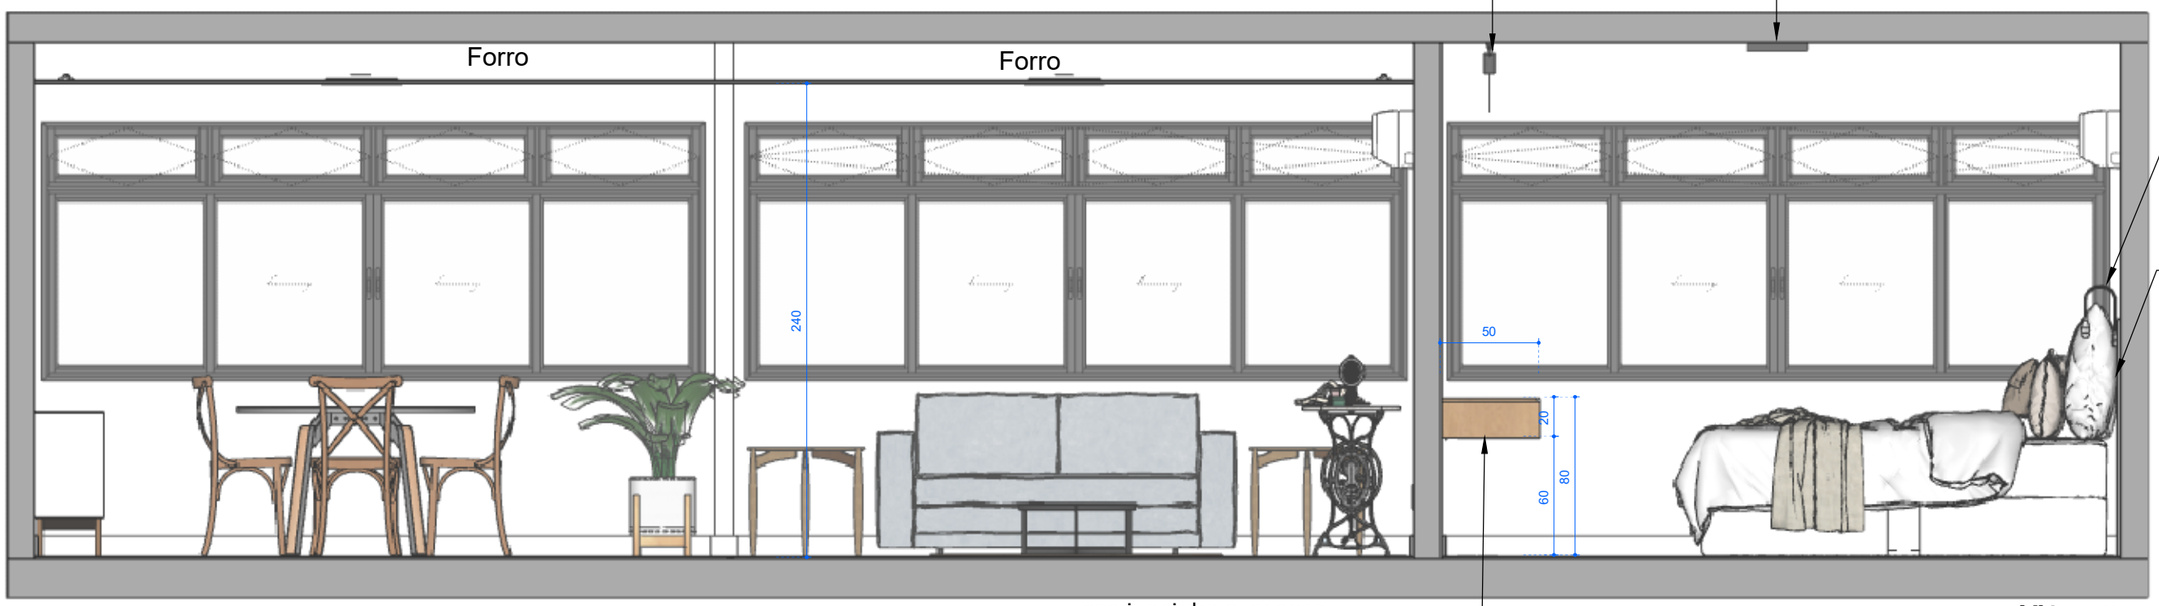


VISTA 9


ESCALA 1:50

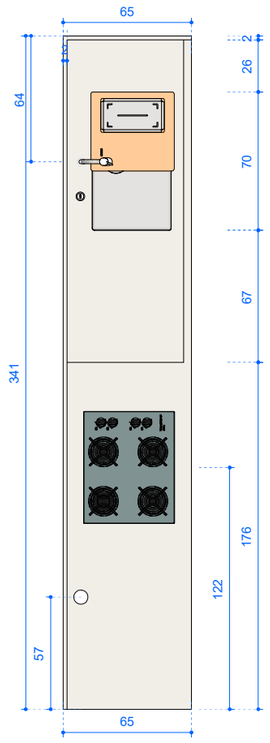

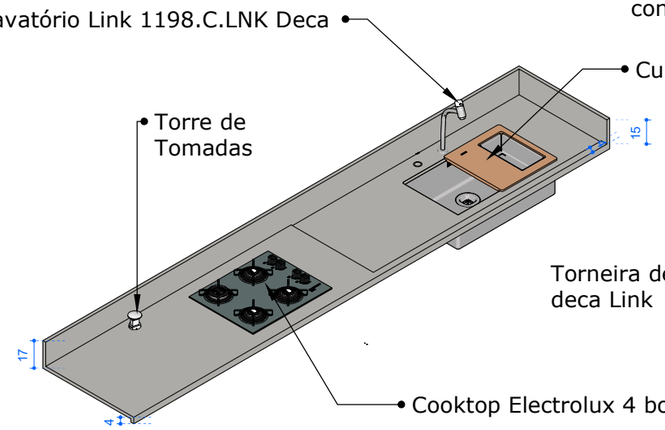


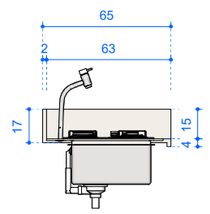

BANCADA COZINHA

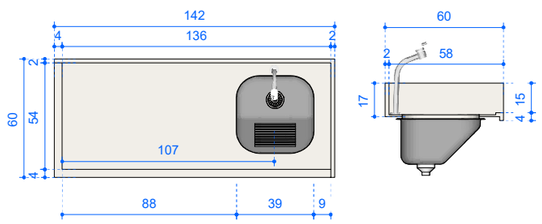

BANCADA TANQUE

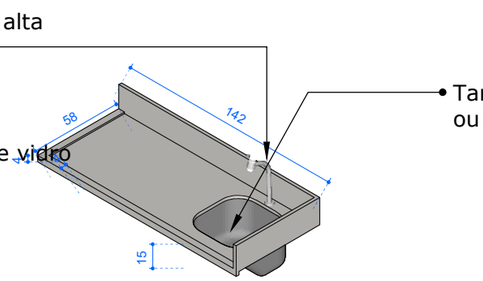

Armário Inferior Cuba/Fogão	341x15	Só frontal
Armário Inferior Tanque+ Lateral Torre Microondas	213x15	45º na esquerda
Torre Microndas	60x15	Frontal

Projetos Residenciais
Projetos Comerciais
Projetos Interiores

ARQUITETO RESPONSÁVEL:
José Adalberto Meuren
CAU Nº 000A487848
(61)98274-3709
jmeuren@gmail.com

CONTEÚDO DA PRANCHA:
Vista 9

ESCALA:
Indicada na Prancha

CLIENTE:
Caetana Juracy Rezende Silva
CPF: 576.328.801-78

ENDEREÇO:
SQN 403 Bl N Aptº 306
Brasília

ARQUIVO:
Arq_Int_descrição
REVISÃO Nº:
R00
DATA REVISÃO:
14-11-2025

OBSERVAÇÕES:
Consultar arquiteto em caso de dúvida e/ou alteração;
Conferir medidas no local;
Medidas em cota prevalecem sobre o desenho

FOLHA:
11/11