CADERNO DE MARCENARIA

Projetos Residenciais
Projetos Comerciais
Projetos Interiores

ARQUITETO RESPONSÁVEL:
José Adalberto Meuren
CAU Nº 000A487848
(61)98274-3709
jmeuren@gmail.com

CONTEÚDO DA PRANCHA:
Capa

ESCALA:
Indicada na Prancha

CLIENTE:
Caetana Juracy Rezende Silva
CPF: 576.328.801-78

ENDEREÇO:
SQN 403 Bl N Aptº 306
Brasília

ARQUIVO:
Marc_Caetana_SQN_403
REVISÃO Nº:
R00
DATA REVISÃO:
15-11-2025





Tubo exaustor do depurador

Armário aéreo em MDF Duratex Mint

Nicho em Duratex Freijó Puro


Perfil Led com fita 9w 3.000k acionamento via microinterruptor.

Depurador retrátil slim Fischer, Suggar ou similar

Armário Inferior em MDF Duratex Mint.
Porta Veneziana no compartimento do botijão.
Frentes com puxador cava usinada.
Nichos aberto em MDF Duratex Freijó.

Forno elétrico Fischer Fit Line 48 Litros

Lava Louças 8 serviços Brastemp ou Electrolux

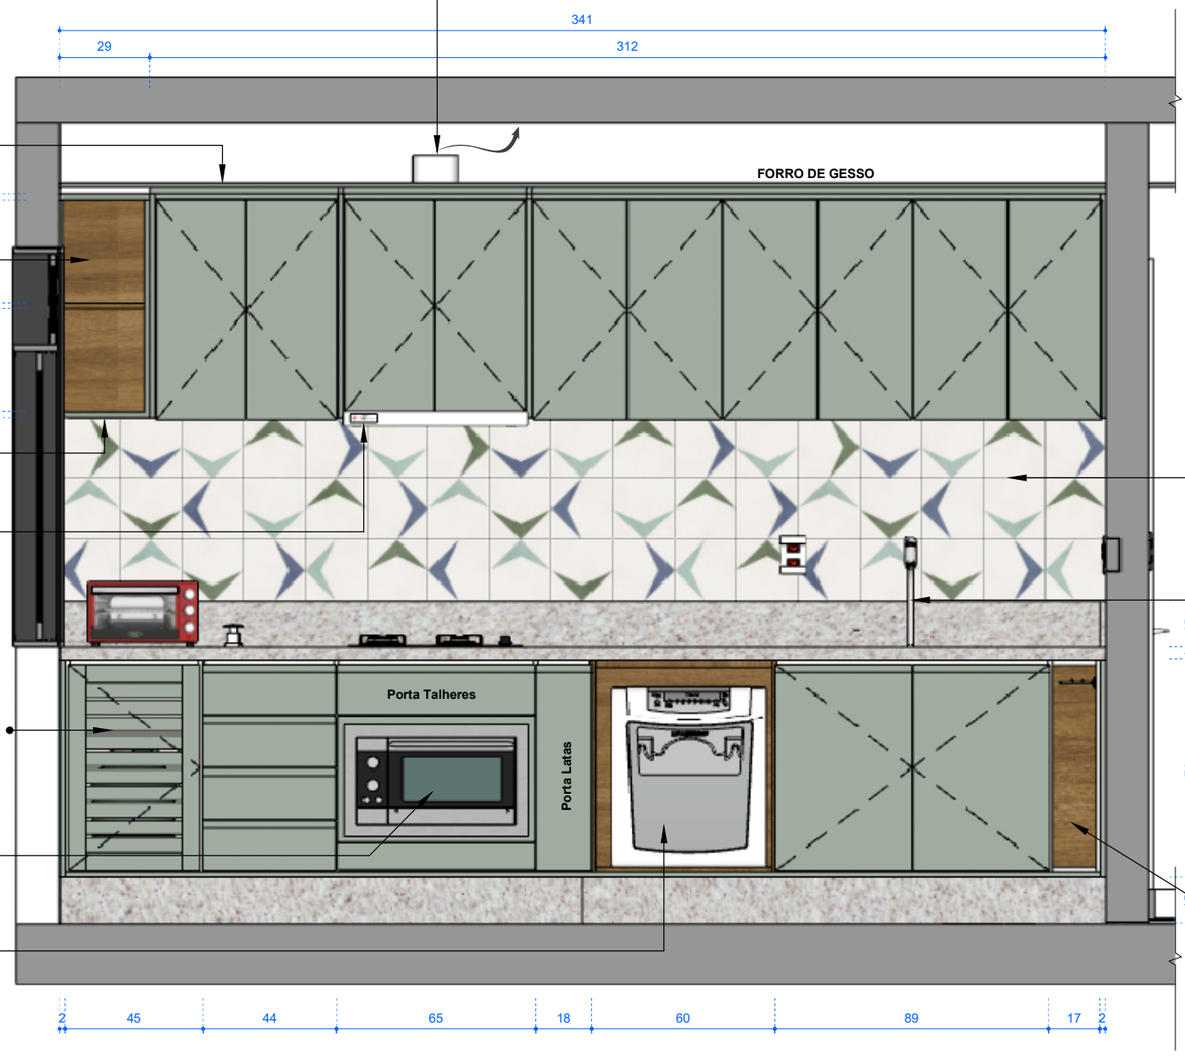






Ladrilar - Andorinha - Custom 2 - 200x200x15mm

Torneira de mesa bica alta Deca Link



Porta Pano de Prato

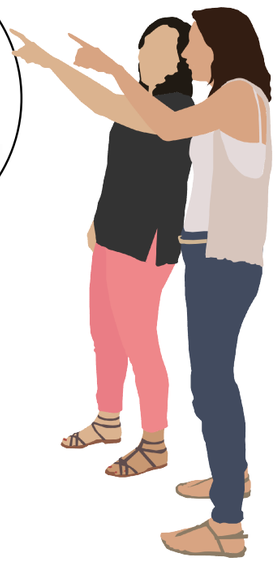

COZINHA - VISTA BANCADA - ELEVAÇÃO

ESCALA 1:20

Projetos Residenciais
Projetos Comerciais
Projetos Interiores

ARQUITETO RESPONSÁVEL:
José Adalberto Meuren
CAU Nº 000A487848
(61)98274-3709
jmeuren@gmail.com

CONTEÚDO DA PRANCHA:
Bancada Elevação Fechada

ESCALA:
Indicada na Prancha

CLIENTE:
Caetana Juracy Rezende Silva
CPF: 576.328.801-78


ENDEREÇO:
SQN 403 Bl N Aptº 306
Brasília

ARQUIVO:
Marc_Caetana_SQN_403
REVISÃO Nº:
R00
DATA REVISÃO:
15-11-2025

OBSERVAÇÕES:
Consultar arquiteto em caso de dúvida e/ou alteração;
Conferir medidas no local;
Medidas em cota prevalecem sobre o desenho

FOLHA:
01/12

Ponto de energia para alimentação do depurador e do drive da fita led

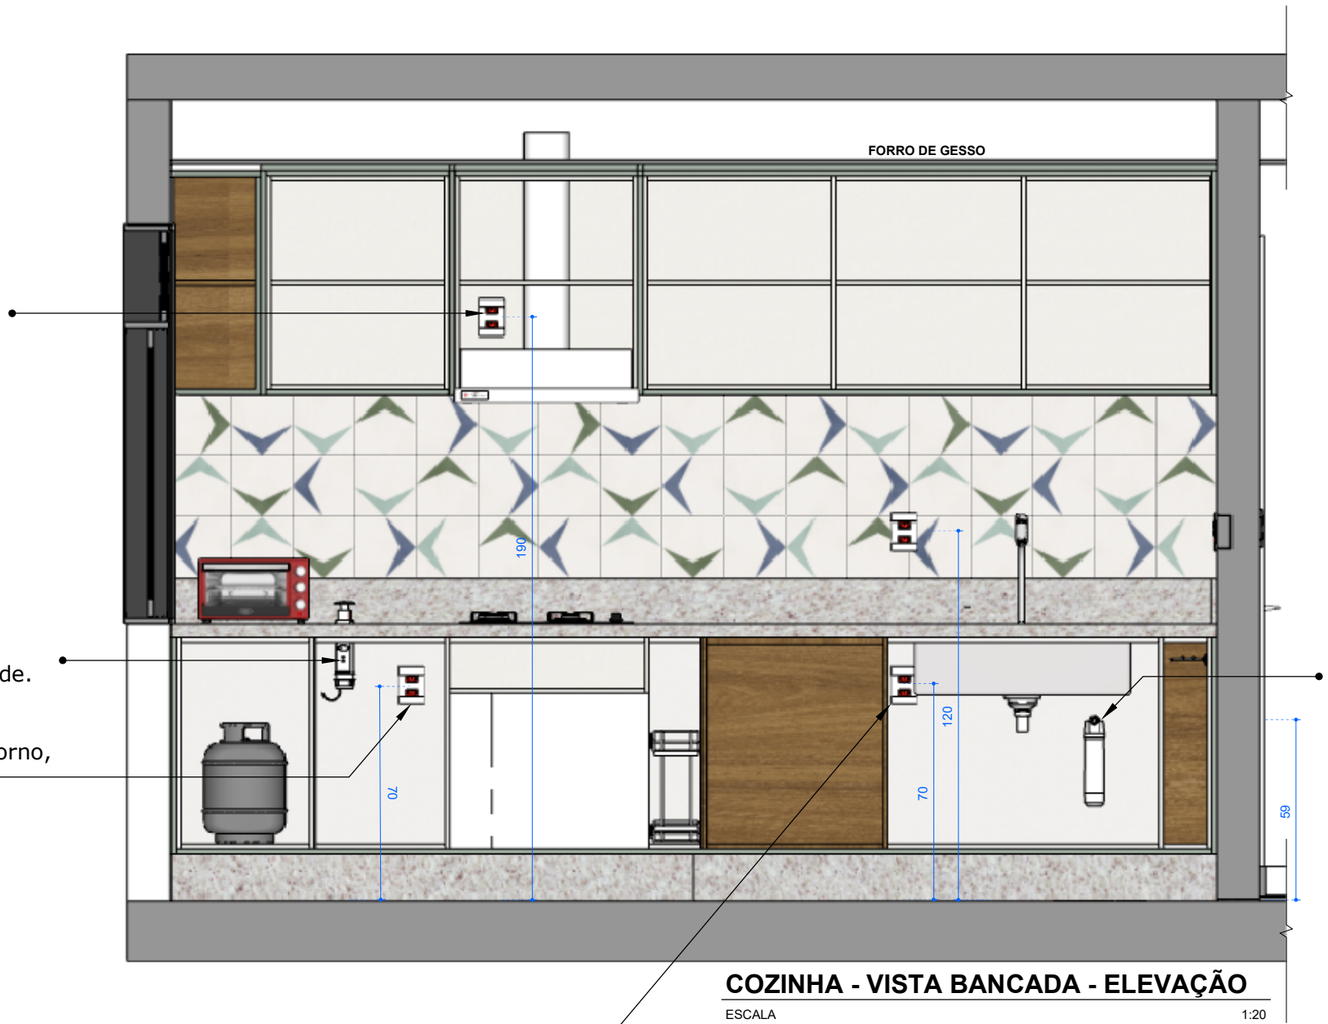

Torre de Tomadas (essa região tem a porta então não dá para ficar na parede.

Ponto de energia para alimentaçãodo Forno, cooktop e torre de tomadas

Ponto de energia para lava louças e futuro triturador

COZINHA - VISTA BANCADA - ELEVAÇÃO

ESCALA 1:20



Filtro de água embaixo da pia Pure9 ou similar.



Projetos Residenciais
Projetos Comerciais
Projetos Interiores

ARQUITETO RESPONSÁVEL:
José Adalberto Meuren
CAU Nº 000A487848
(61)98274-3709
jmeuren@gmail.com

CONTEÚDO DA PRANCHA:
Bancada Elevação Aberta


ESCALA:
Indicada na Prancha

CLIENTE:
Caetana Juracy Rezende Silva
CPF: 576.328.801-78

ENDEREÇO:
SQN 403 Bl N Aptº 306
Brasília

ARQUIVO:
Marc_Caetana_SQN_403
REVISÃO Nº:
R00
DATA REVISÃO:
15-11-2025

OBSERVAÇÕES:
Consultar arquiteto em caso de dúvida e/ou alteração;
Conferir medidas no local;
Medidas em cota prevalecem sobre o desenho

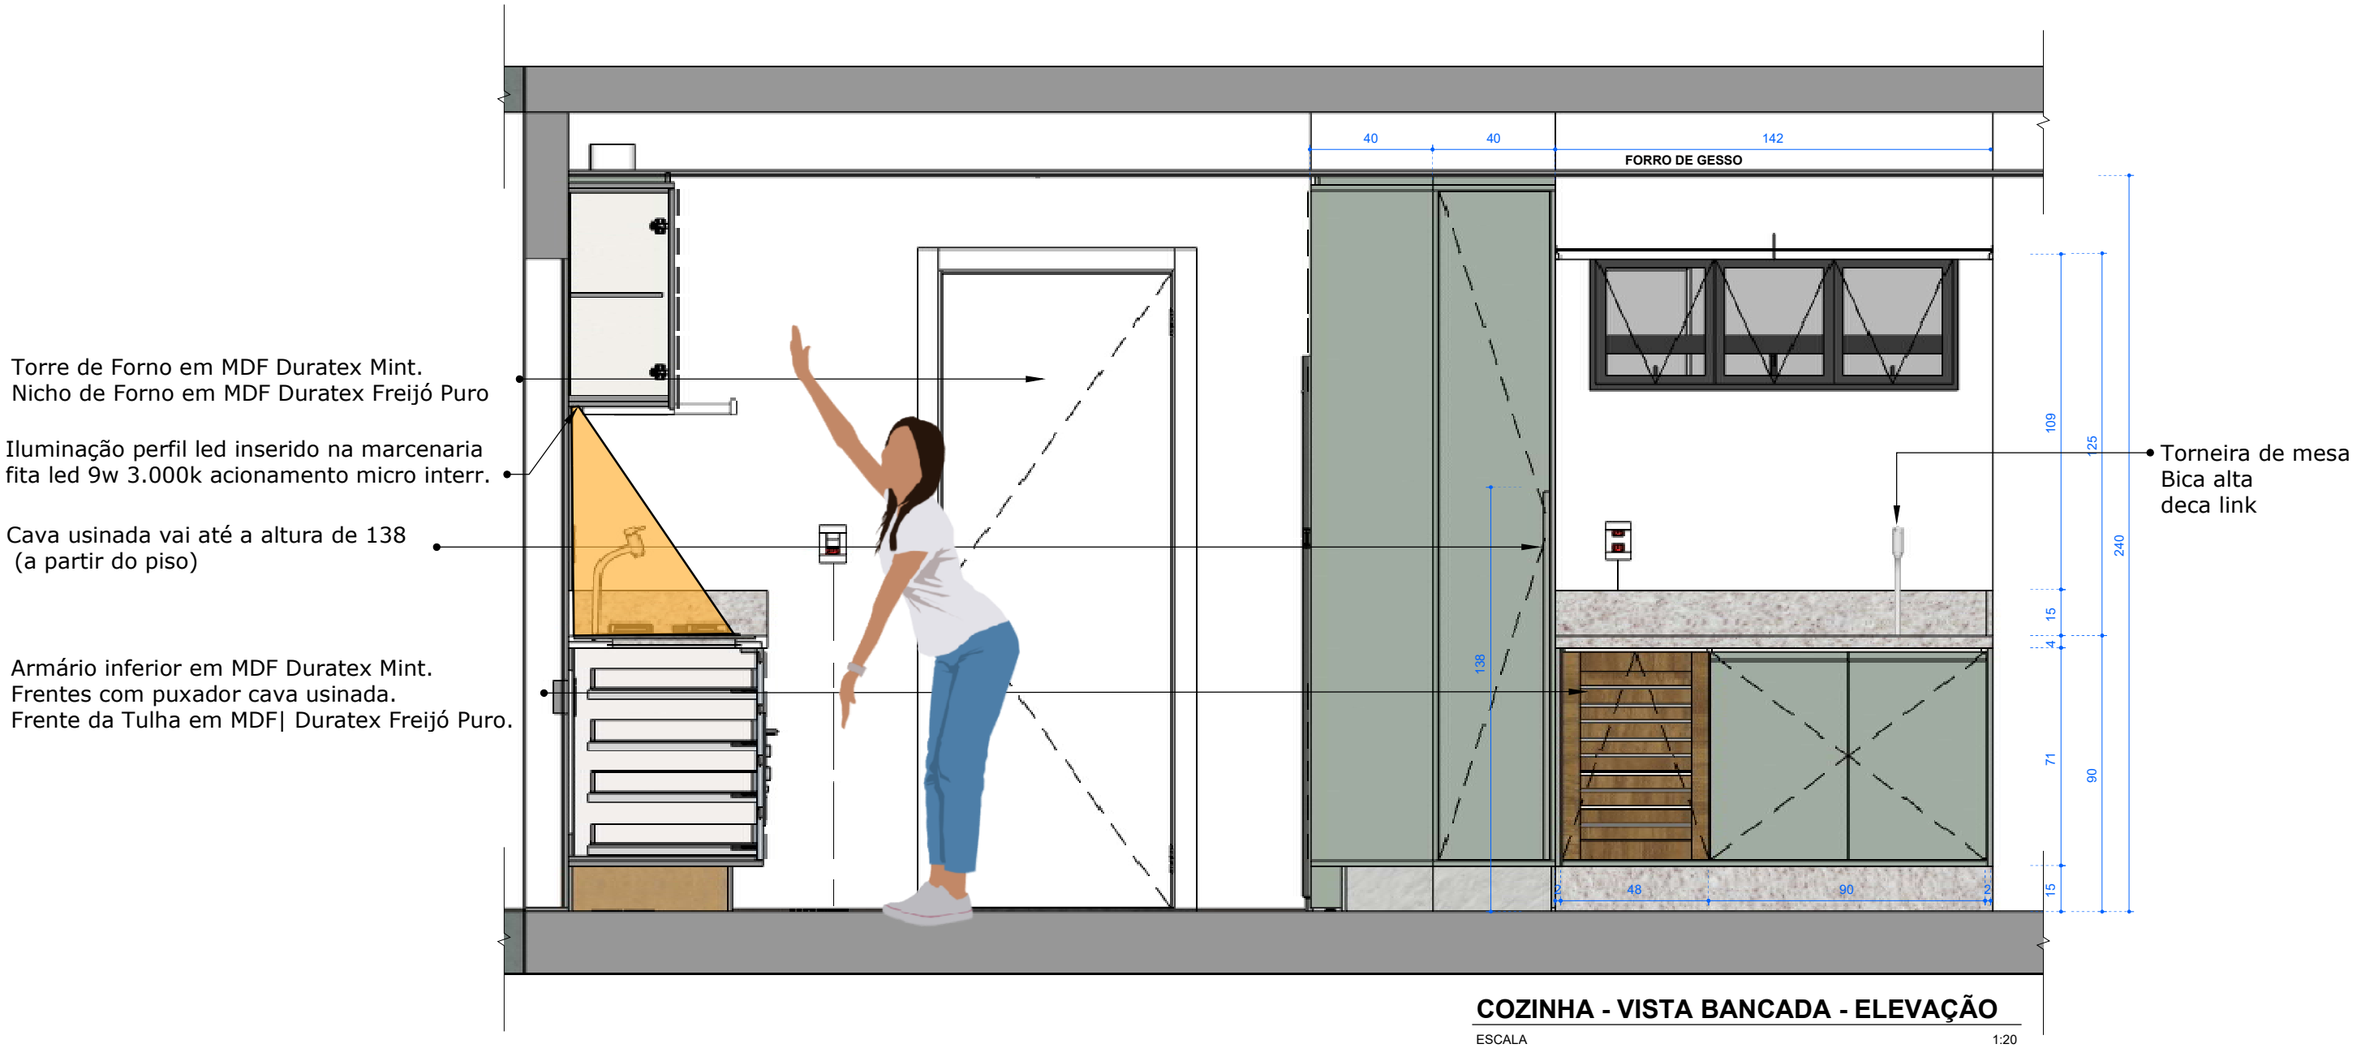

COZINHA - VISTA BANCADA - ELEVAÇÃO

ESCALA 1:20

ARQUITETURA & INTERIORES j.m

Projetos Residenciais
Projetos Comerciais
Projetos Interiores

ARQUITETO RESPONSÁVEL:
José Adalberto Meuren
CAU Nº 000A487848
(61)98274-3709
jmeuren@gmail.com

CONTEÚDO DA PRANCHA:
Torres e Armário Área - Elevação Fechada

ESCALA:
Indicada na Prancha


CLIENTE:
Caetana Juracy Rezende Silva
CPF: 576.328.801-78

ENDEREÇO:
SQN 403 Bl N Aptº 306
Brasília

ARQUIVO:
Marc_Caetana_SQN_403
REVISÃO Nº:
R00
DATA REVISÃO:
15-11-2025

OBSERVAÇÕES:
Consultar arquiteto em caso de dúvida e/ou alteração;
Conferir medidas no local;
Medidas em cota prevalecem sobre o desenho

FOLHA:

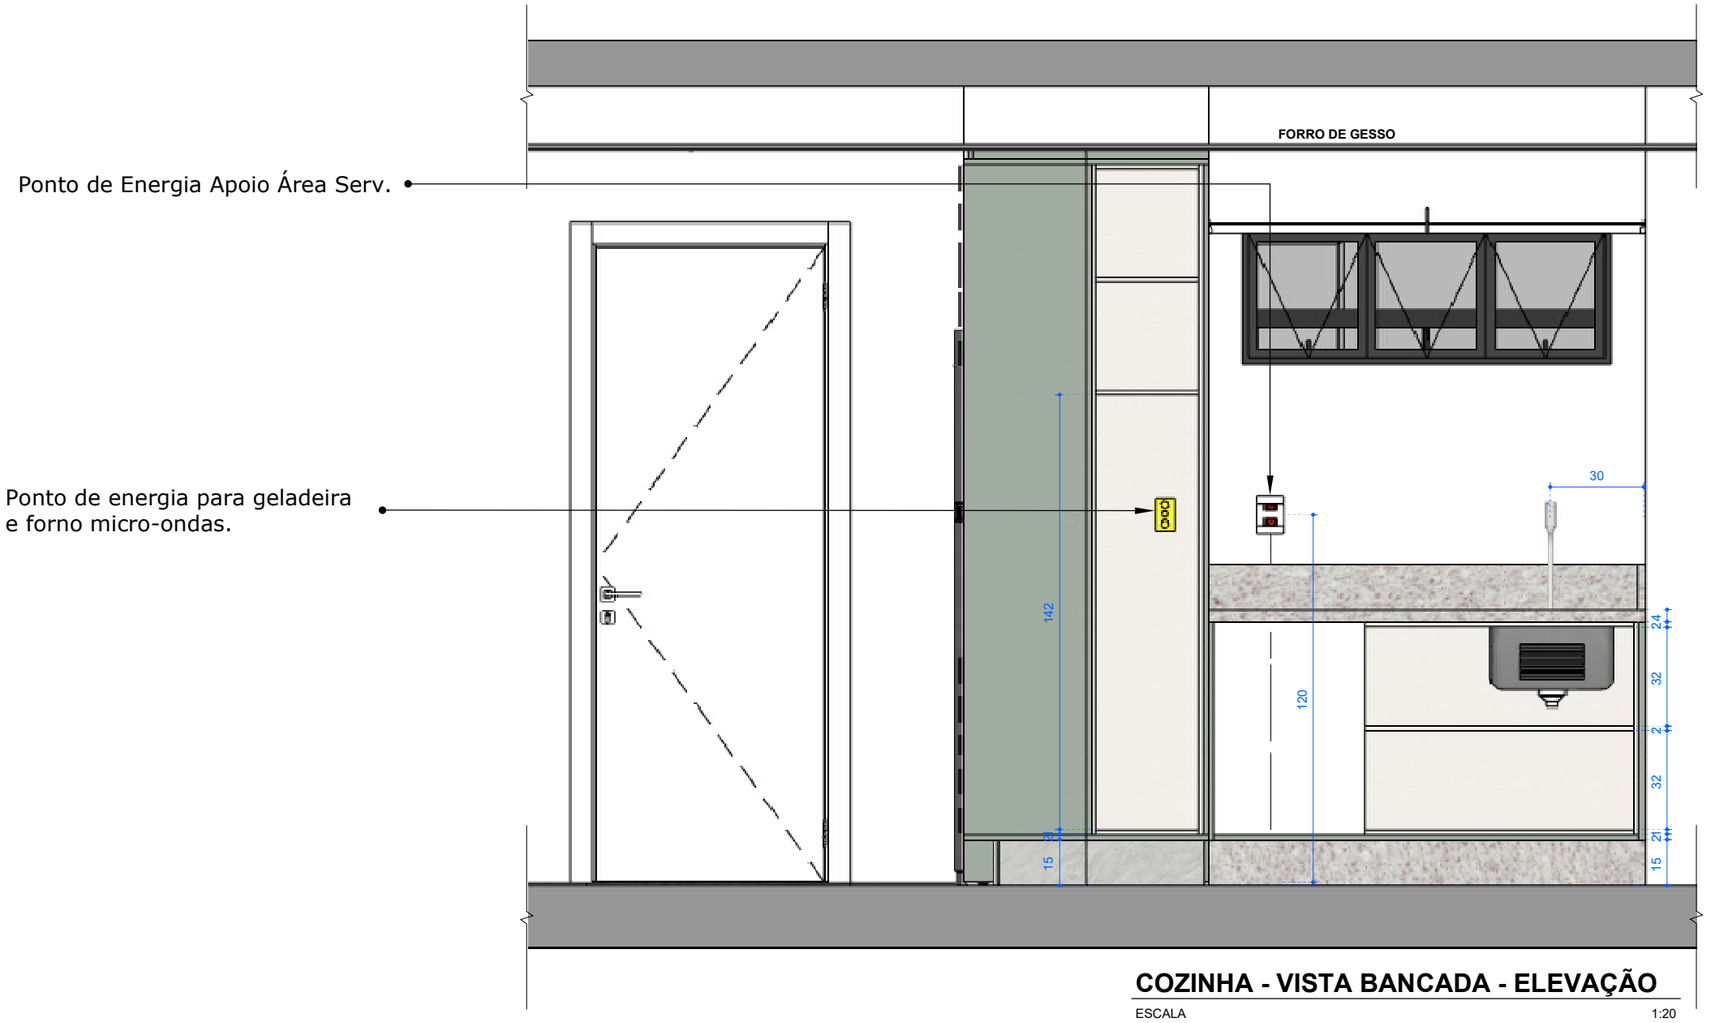

ARQUITETURA & INTERIORES
j.m
Projetos Residenciais
Projetos Comerciais
Projetos Interiores

ARQUITETO RESPONSÁVEL:
José Adalberto Meuren
CAU Nº 000A487848
(61)98274-3709
jmeuren@gmail.com

CONTEÚDO DA PRANCHA:
Torres e Armário Área - Elevação Aberta

ESCALA:
Indicada na Prancha

CLIENTE:
Caetana Juracy Rezende Silva
CPF: 576.328.801-78


ENDEREÇO:
SQN 403 Bl N Aptº 306
Brasília

ARQUIVO:
Marc_Caetana_SQN_403
REVISÃO Nº:
R00
DATA REVISÃO:
15-11-2025

OBSERVAÇÕES:
Consultar arquiteto em caso de dúvida e/ou alteração;
Conferir medidas no local;
Medidas em cota prevalecem sobre o desenho

FOLHA:



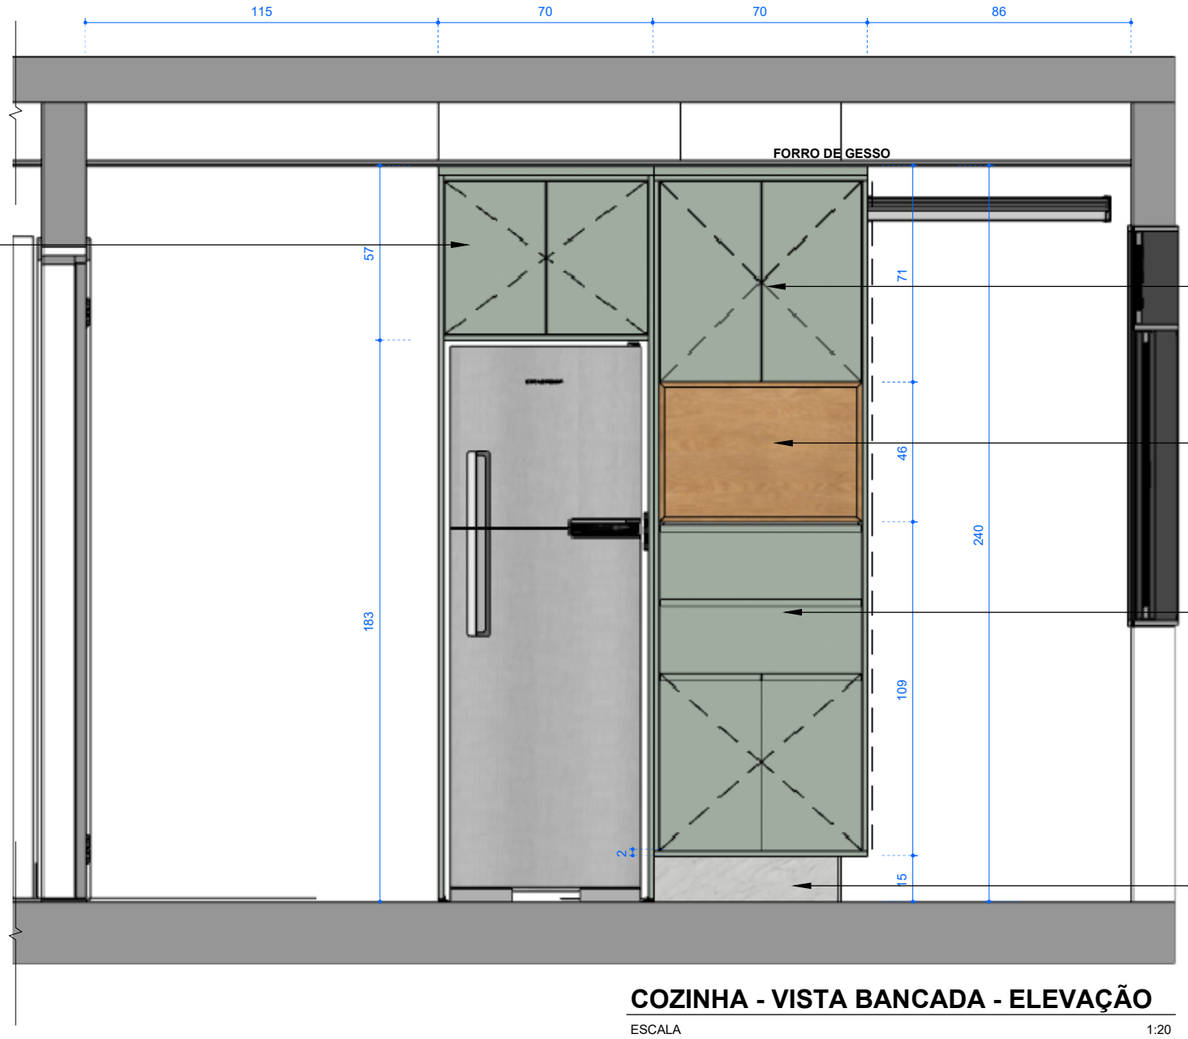

Armário Geladeira existente. Revestir com MDF Duratex Mint. Portas com puxador sobra inferior.

Torre micro-ondas em MDF Duratex Mint. Parte superior com fecho toque.

Nicho de micro-ondas em MDF Duratex Freijó Puro. Colocar Passa fios na lateral do móvel.

Gavetas e portas em MDF Duratex Mint. Puxador cava usinada.

Rodapé em Granito Branco Siena

COZINHA - VISTA BANCADA - ELEVAÇÃO

ESCALA 1:20

Projetos Residenciais
Projetos Comerciais
Projetos Interiores

ARQUITETO RESPONSÁVEL:
José Adalberto Meuren
CAU Nº 000A487848
(61)98274-3709
jmeuren@gmail.com

CONTEÚDO DA PRANCHA:
Torre Geladeira e Torre Forno - Elevação Fechada

ESCALA:
Indicada na Prancha

CLIENTE:
Caetana Juracy Rezende Silva
CPF: 576.328.801-78


ENDEREÇO:
SQN 403 Bl N Aptº 306
Brasília

ARQUIVO:
Marc_Caetana_SQN_403
REVISÃO Nº:
R00
DATA REVISÃO:
15-11-2025

OBSERVAÇÕES:
Consultar arquiteto em caso de dúvida e/ou alteração;
Conferir medidas no local;
Medidas em cota prevalecem sobre o desenho

FOLHA:



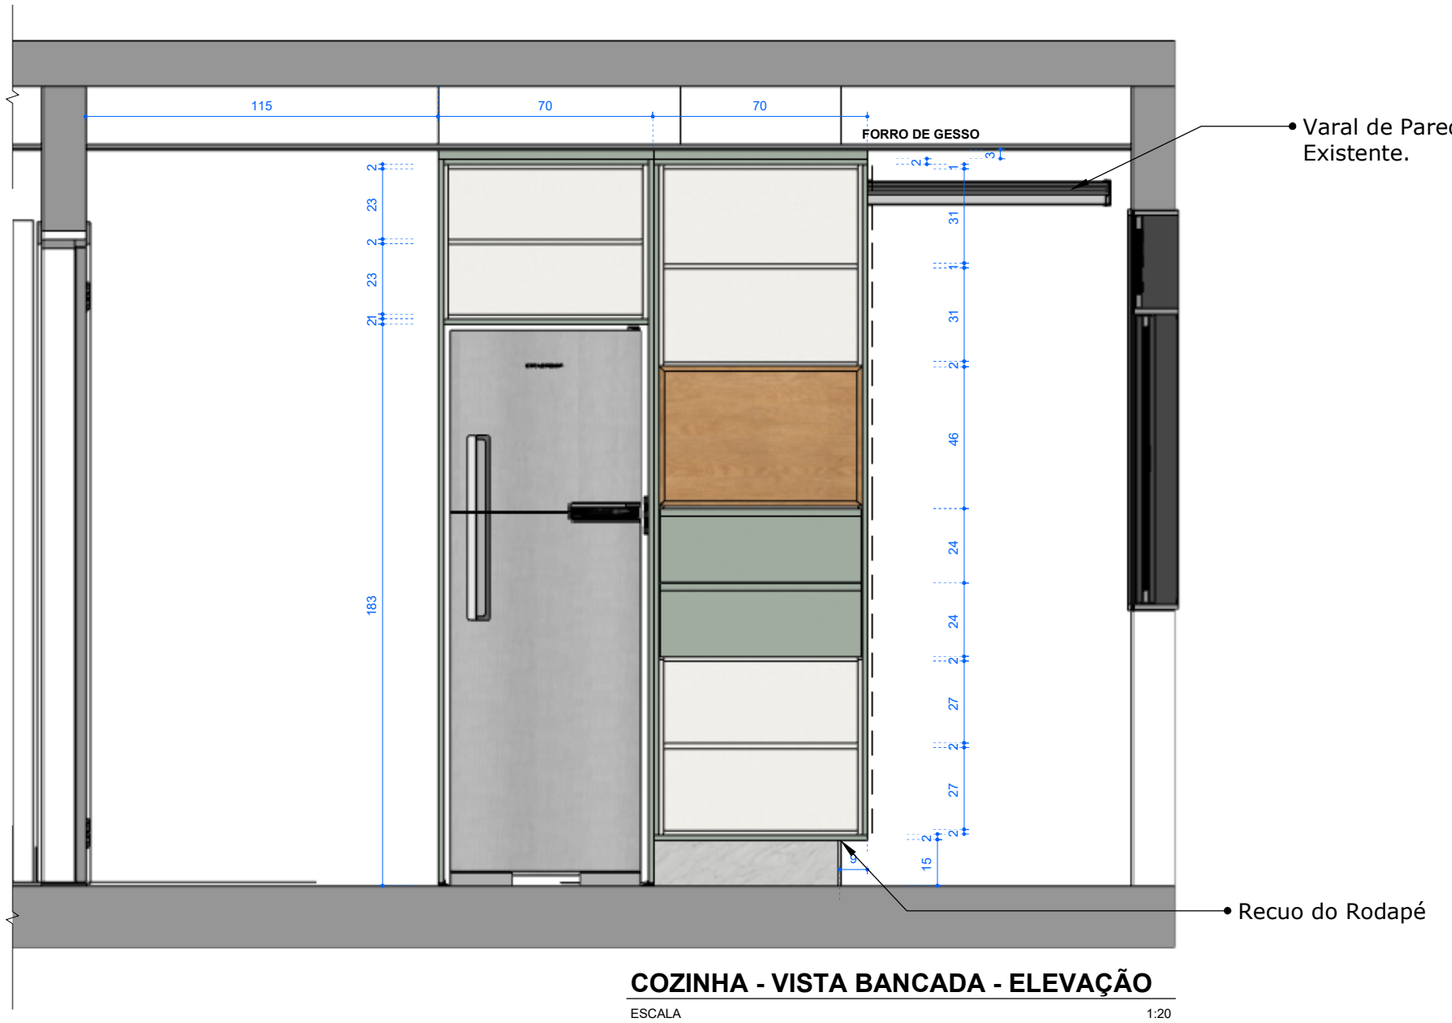

COZINHA - VISTA BANCADA - ELEVAÇÃO

ESCALA 1:20

ARQUITETURA & INTERIORES

Projetos Residenciais
Projetos Comerciais
Projetos Interiores

ARQUITETO RESPONSÁVEL:
José Adalberto Meuren
CAU Nº 000A487848
(61)98274-3709
jmeuren@gmail.com

CONTEÚDO DA PRANCHA:
Torre Geladeira e Torre Forno - Elevação Aberta

ESCALA:
Indicada na Prancha

CLIENTE:
Caetana Juracy Rezende Silva
CPF: 576.328.801-78

ENDEREÇO:
SQN 403 Bl N Aptº 306
Brasília


ARQUIVO:
Marc_Caetana_SQN_403

REVISÃO Nº:
R00

DATA REVISÃO:
15-11-2025

OBSERVAÇÕES:
Consultar arquiteto em caso de dúvida e/ou alteração;
Conferir medidas no local;
Medidas em cota prevalecem sobre o desenho



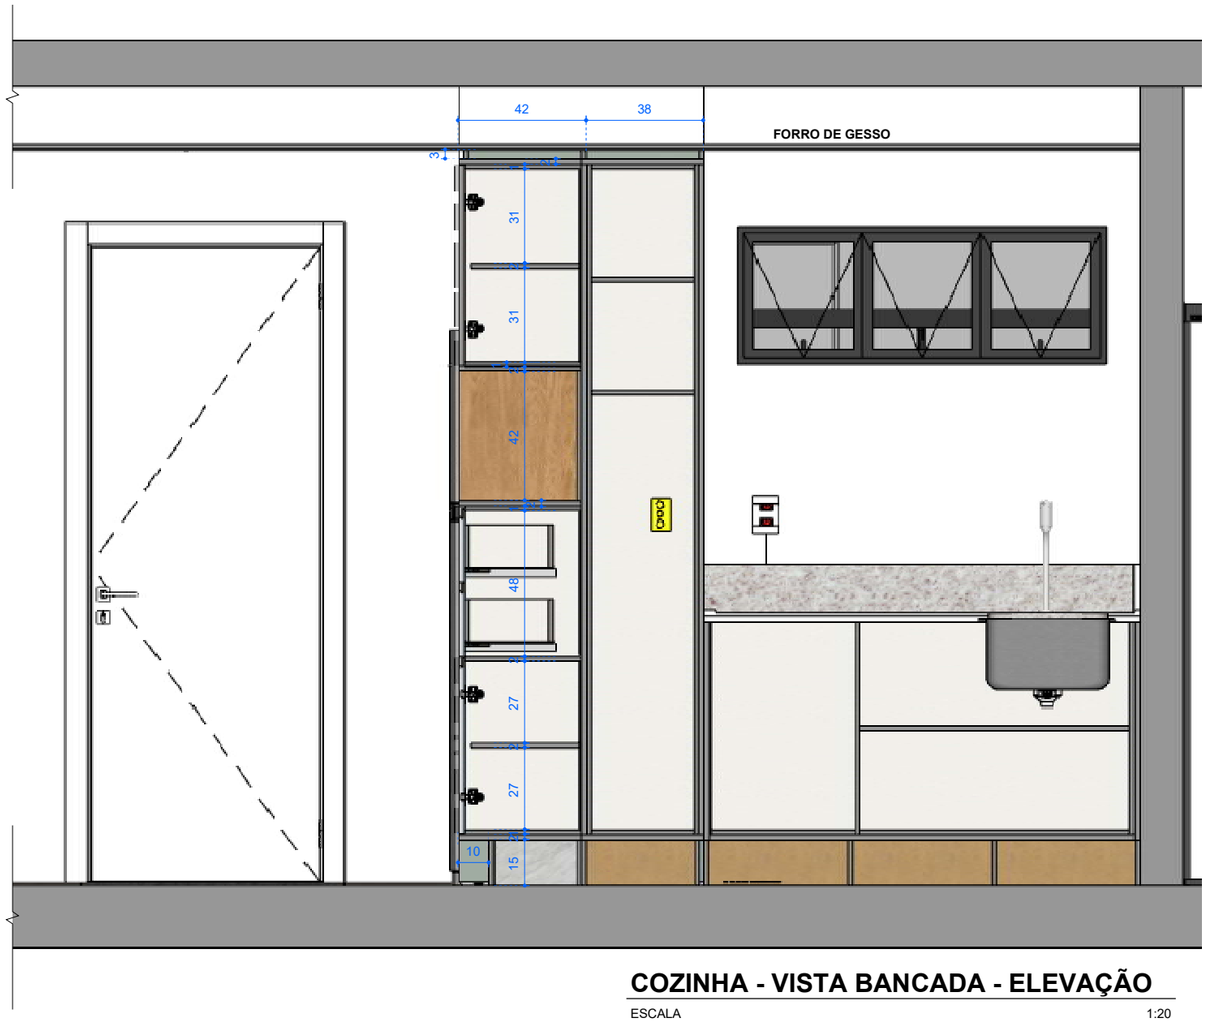

COZINHA - VISTA BANCADA - ELEVAÇÃO

ESCALA 1:20

ARQUITETURA & INTERIORES

Projetos Residenciais
Projetos Comerciais
Projetos Interiores

ARQUITETO RESPONSÁVEL:
José Adalberto Meuren
CAU Nº 000A487848
(61)98274-3709
jmeuren@gmail.com

CONTEÚDO DA PRANCHA:
Corte Torre Forno Microondas

ESCALA:
Indicada na Prancha

CLIENTE:
Caetana Juracy Rezende Silva
CPF: 576.328.801-78

ENDEREÇO:
SQN 403 Bl N Aptº 306
Brasília


ARQUIVO:
Marc_Caetana_SQN_403

REVISÃO Nº:
R00

DATA REVISÃO:
15-11-2025


OBSERVAÇÕES:
Consultar arquiteto em caso de dúvida e/ou alteração;
Conferir medidas no local;
Medidas em cota prevalecem sobre o desenho

FOLHA:

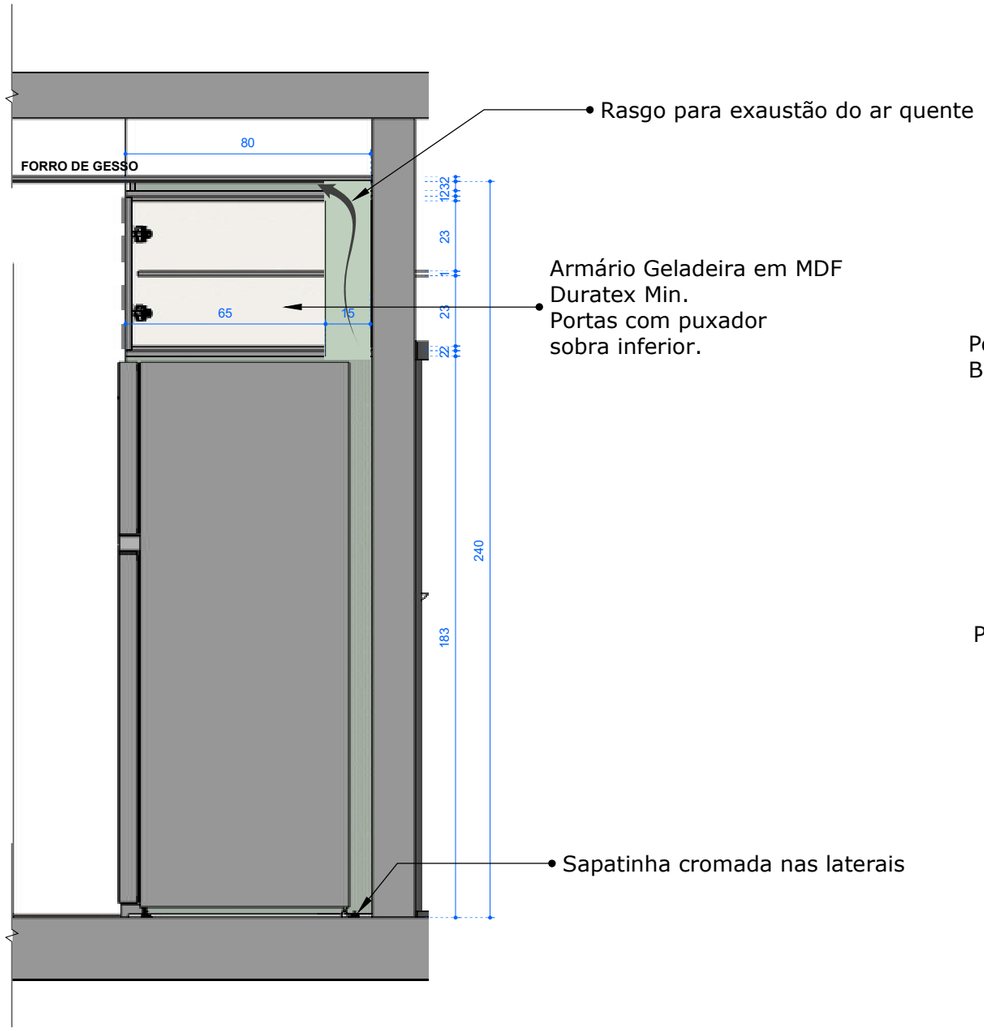

COZINHA - ARMÁRIO GELADEIRA - CORTE

ESCALA 1:20

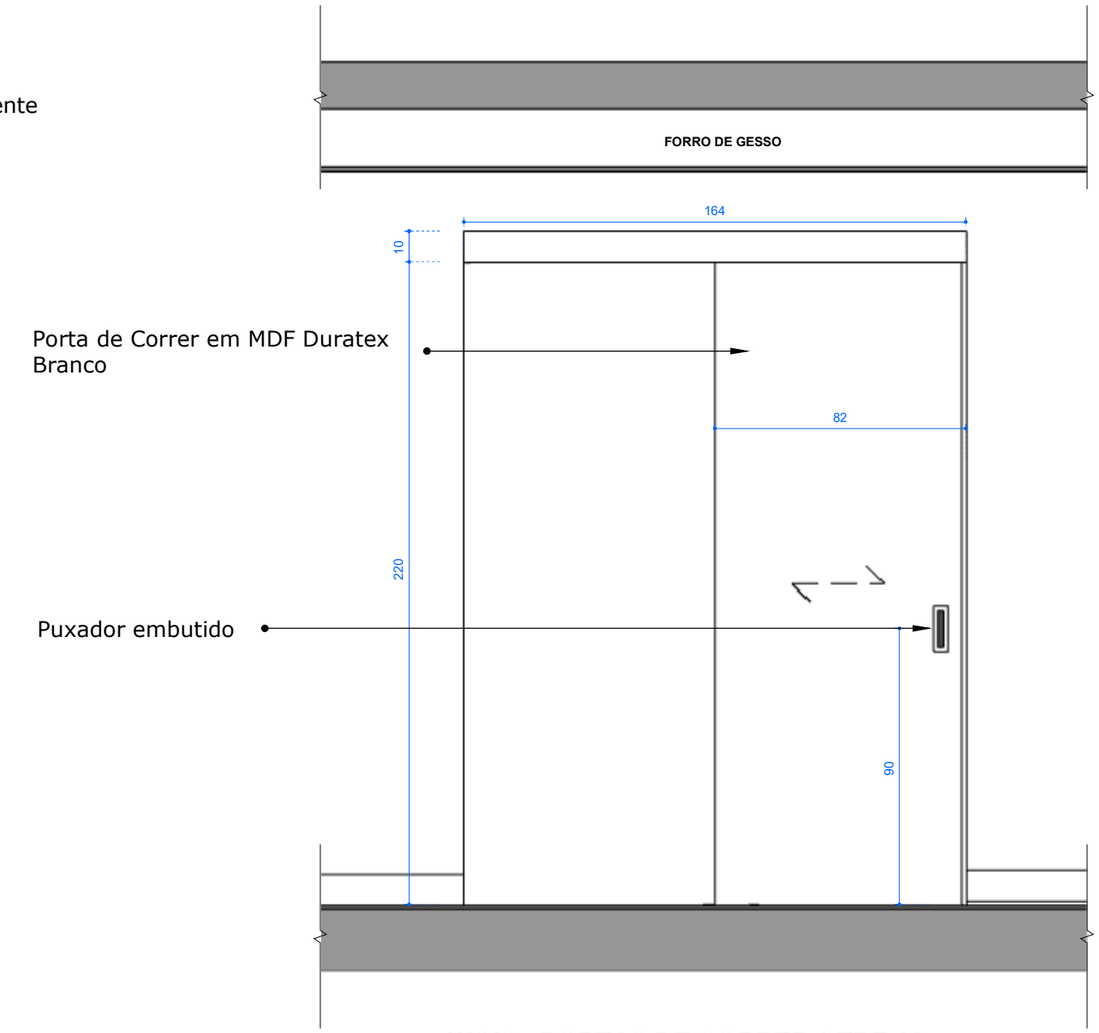

WC´S - PORTAS DE CORRER QTDE 02

ESCALA 1:20

ARQUITETURA & INTERIORES

Projetos Residenciais
Projetos Comerciais
Projetos Interiores

ARQUITETO RESPONSÁVEL:
José Adalberto Meuren
CAU Nº 000A487848
(61)98274-3709
jmeuren@gmail.com

CONTEÚDO DA PRANCHA:
Corte Armário Geladeira - Elevação portas correr

ESCALA:
Indicada na Prancha

CLIENTE:
Caetana Juracy Rezende Silva
CPF: 576.328.801-78

ENDEREÇO:
SQN 403 Bl N Aptº 306
Brasília

ARQUIVO:
Marc_Caetana_SQN_403
REVISÃO Nº:
R00
DATA REVISÃO:
15-11-2025

OBSERVAÇÕES:
Consultar arquiteto em caso de dúvida e/ou alteração;
Conferir medidas no local;
Medidas em cota prevalecem sobre o desenho


FOLHA:




Cristaleira existente.
Alizar e fitamento externo
em MDF Duratex Azul Secreto.
Interior em MDF Duratex Freijó Puro.
Portas moldura fina alumínio preto
e vidro canelado.
Puxador lingueta preto

Iluminação nas laterais com perfil
led inserido na marcenaria e fita
led 9w 3.000k.
Acionamento pelo interruptor que
está no lado direito da parede .

Prateleira em vidro incolor 6mm

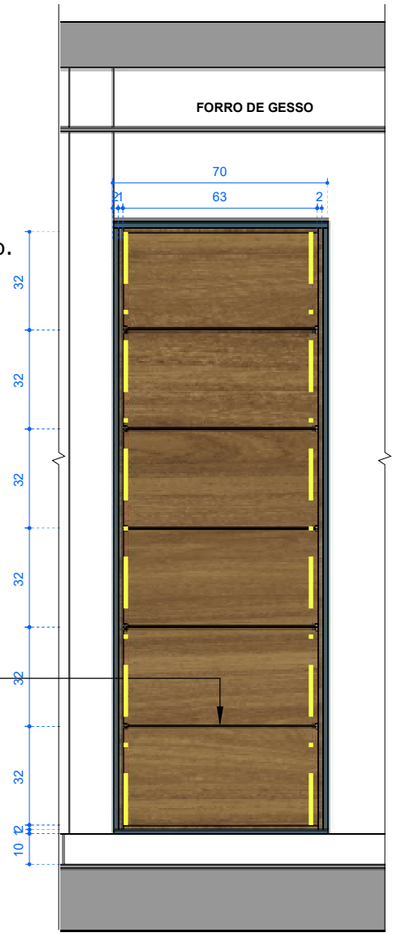

Iluminação nas laterais com perfil
led inserido na marcenaria e fita
led 9w 3.000k.
Acionamento pelo interruptor que está
no lado direito da parede.

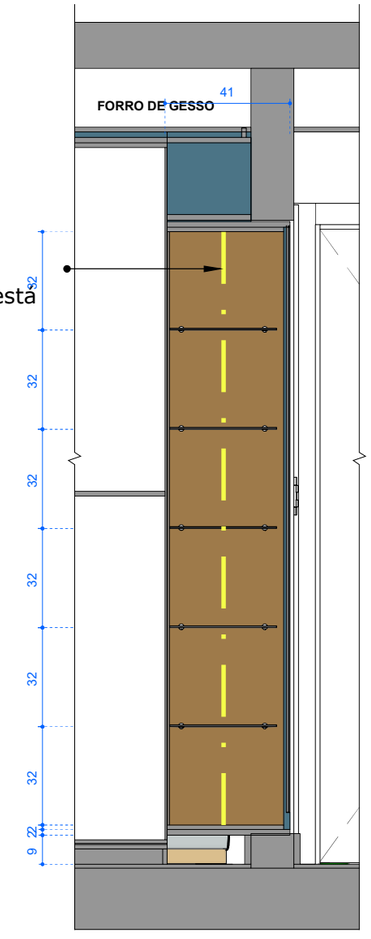

CRISTALEIRA - ELEVAÇÕES E CORTE

ESCALA 1:20

ARQUITETURA & INTERIORES
j.m
Projetos Residenciais
Projetos Comerciais
Projetos Interiores

ARQUITETO RESPONSÁVEL:
José Adalberto Meuren
CAU Nº 000A487848
(61)98274-3709
jmeuren@gmail.com

CONTEÚDO DA PRANCHA:
Cristaleira -Elevação e Cortes

ESCALA:
Indicada na Prancha


CLIENTE:
Caetana Juracy Rezende Silva
CPF: 576.328.801-78


ENDEREÇO:
SQN 403 Bl N Aptº 306
Brasília

ARQUIVO:
Marc_Caetana_SQN_403
REVISÃO Nº:
R00
DATA REVISÃO:
15-11-2025

OBSERVAÇÕES:
Consultar arquiteto em caso de dúvida e/ou alteração;
Conferir medidas no local;
Medidas em cota prevalecem sobre o desenho

FOLHA:
09/12

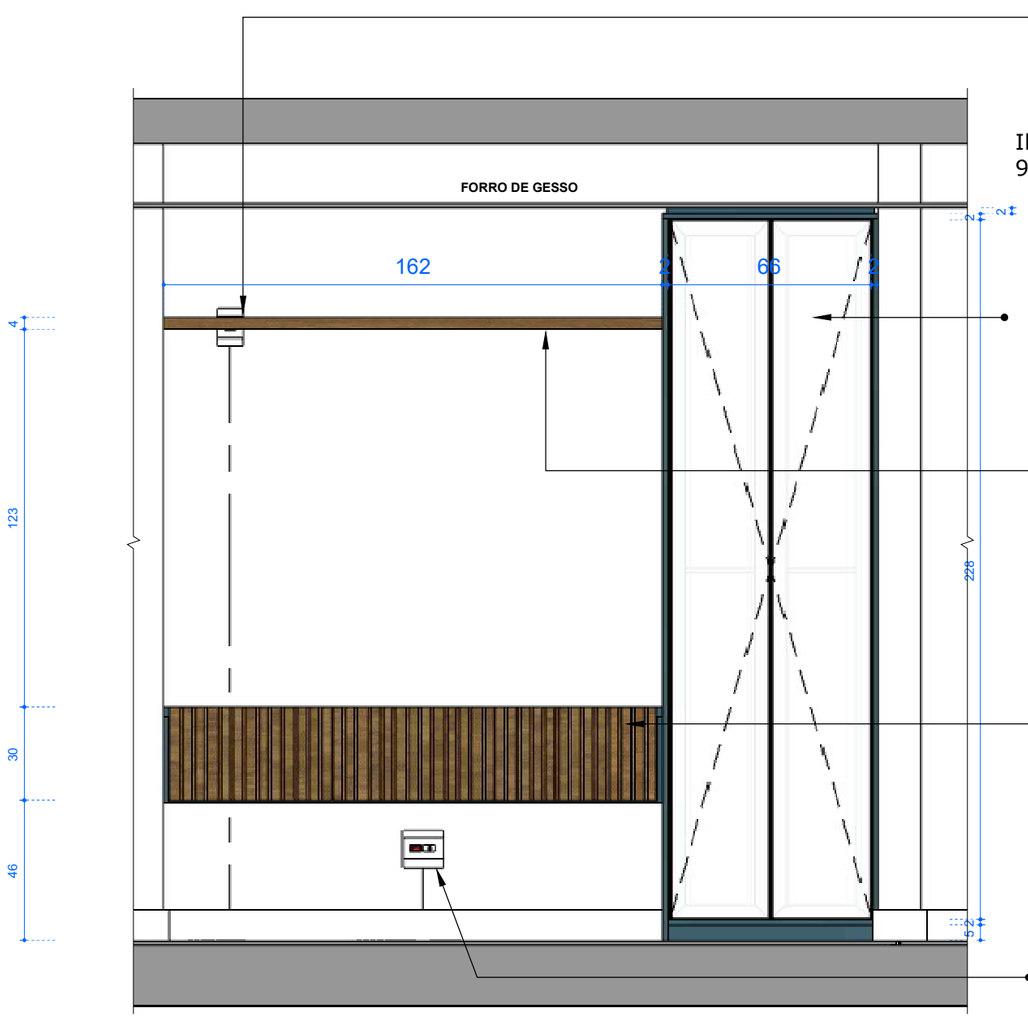

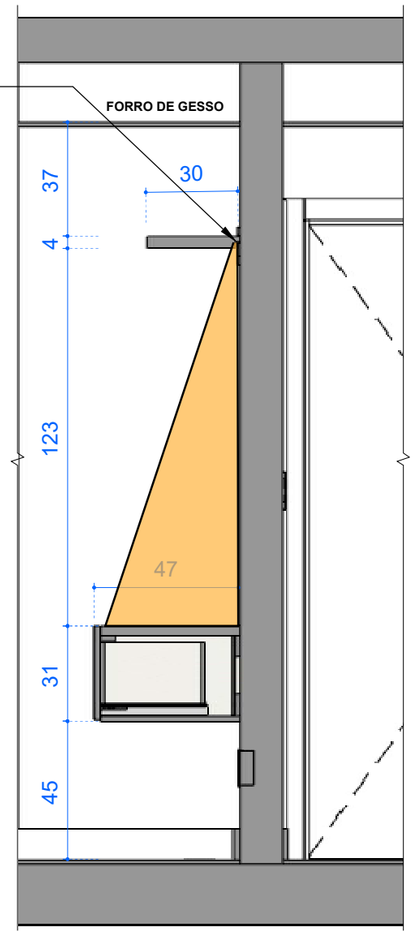

ESTANTE E RACK - EVELAÇÃO E CORTE

ESCALA 1:20

ARQUITETURA & INTERIORES j.m
Projetos Residenciais
Projetos Comerciais
Projetos Interiores

ARQUITETO RESPONSÁVEL:
José Adalberto Meuren
CAU Nº 000A487848
(61)98274-3709
jmeuren@gmail.com

CONTEÚDO DA PRANCHA:
Armário e Rack Sala

ESCALA:
Indicada na Prancha

CLIENTE:
Caetana Juracy Rezende Silva
CPF: 576.328.801-78

ENDEREÇO:
SQN 403 Bl N Aptº 306
Brasília

ARQUIVO:
Marc_Caetana_SQN_403
REVISÃO Nº:
R00
DATA REVISÃO:
15-11-2025


OBSERVAÇÕES:
Consultar arquiteto em caso de dúvida e/ou alteração;
Conferir medidas no local;
Medidas em cota prevalecem sobre o desenho

FOLHA:

Armário existente a ser reformado. todo em MDF
Duratex Branco.
Portas de correr serão aproveitadas.

Arandela de Leitura fixa na cabeceira.
Importante. Arandela tem que ter interruptor proprio

Cabeceira existente a ser reformada. Utilizar madeirado similar ao existente

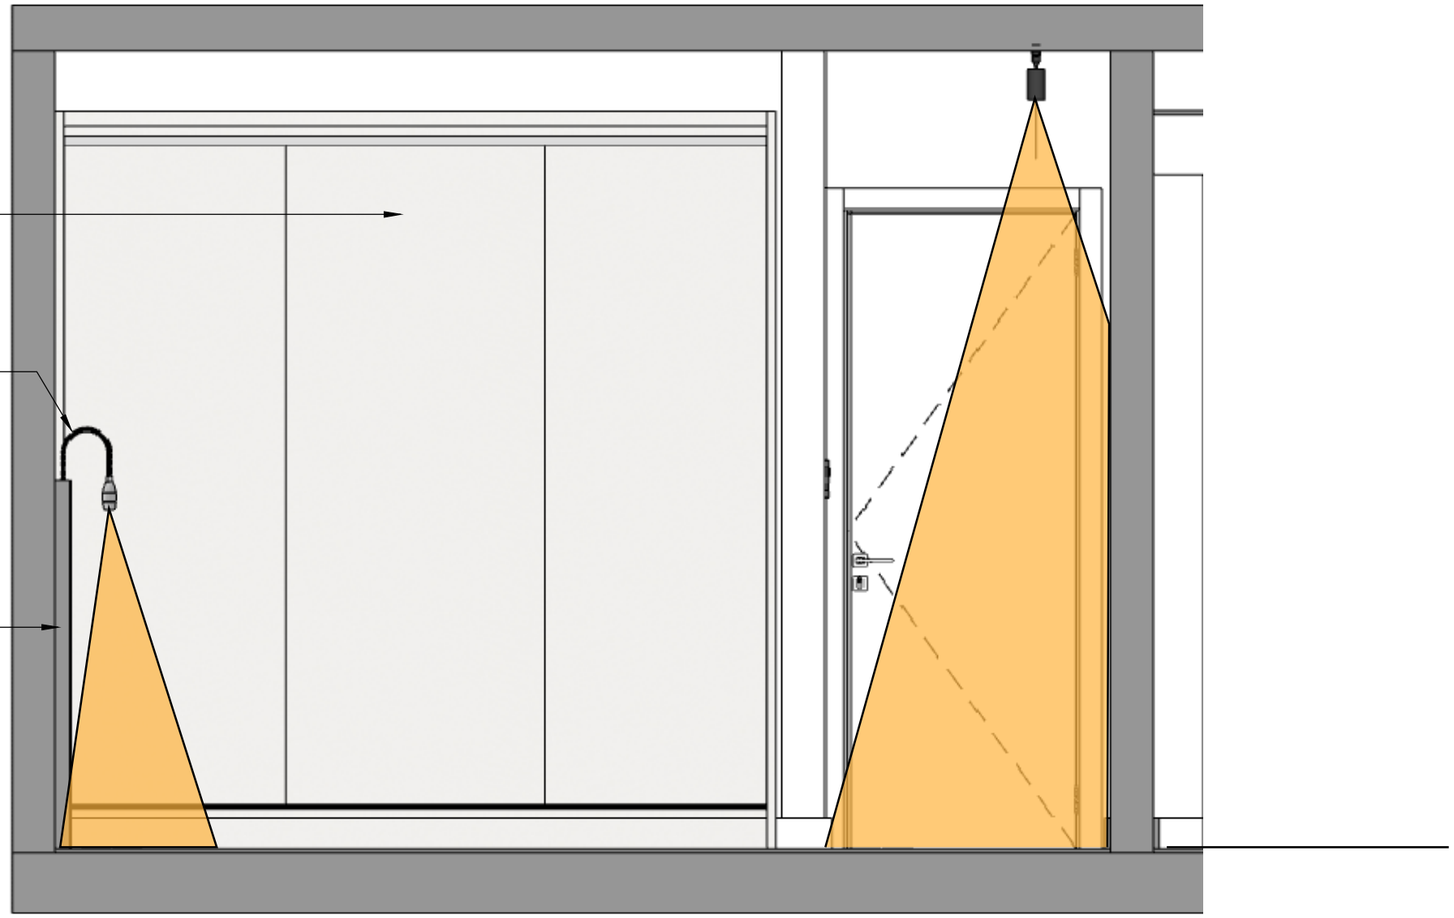

ARMÁRIO E CABECEIRA QUARTO - ELEV.

ESCALA 1:20

ARQUITETURA & INTERIORES j.m

Projetos Residenciais
Projetos Comerciais
Projetos Interiores

ARQUITETO RESPONSÁVEL:
José Adalberto Meuren
CAU Nº 000A487848
(61)98274-3709
jmeuren@gmail.com

CONTEÚDO DA PRANCHA:
Armário e Cabeceira Quarto

ESCALA:
Indicada na Prancha

CLIENTE:
Caetana Juracy Rezende Silva
CPF: 576.328.801-78


ENDEREÇO:
SQN 403 Bl N Aptº 306
Brasília

ARQUIVO:
Marc_Caetana_SQN_403
REVISÃO Nº:
R00
DATA REVISÃO:
15-11-2025

OBSERVAÇÕES:
Consultar arquiteto em caso de dúvida e/ou alteração;
Conferir medidas no local;
Medidas em cota prevalecem sobre o desenho

FOLHA:



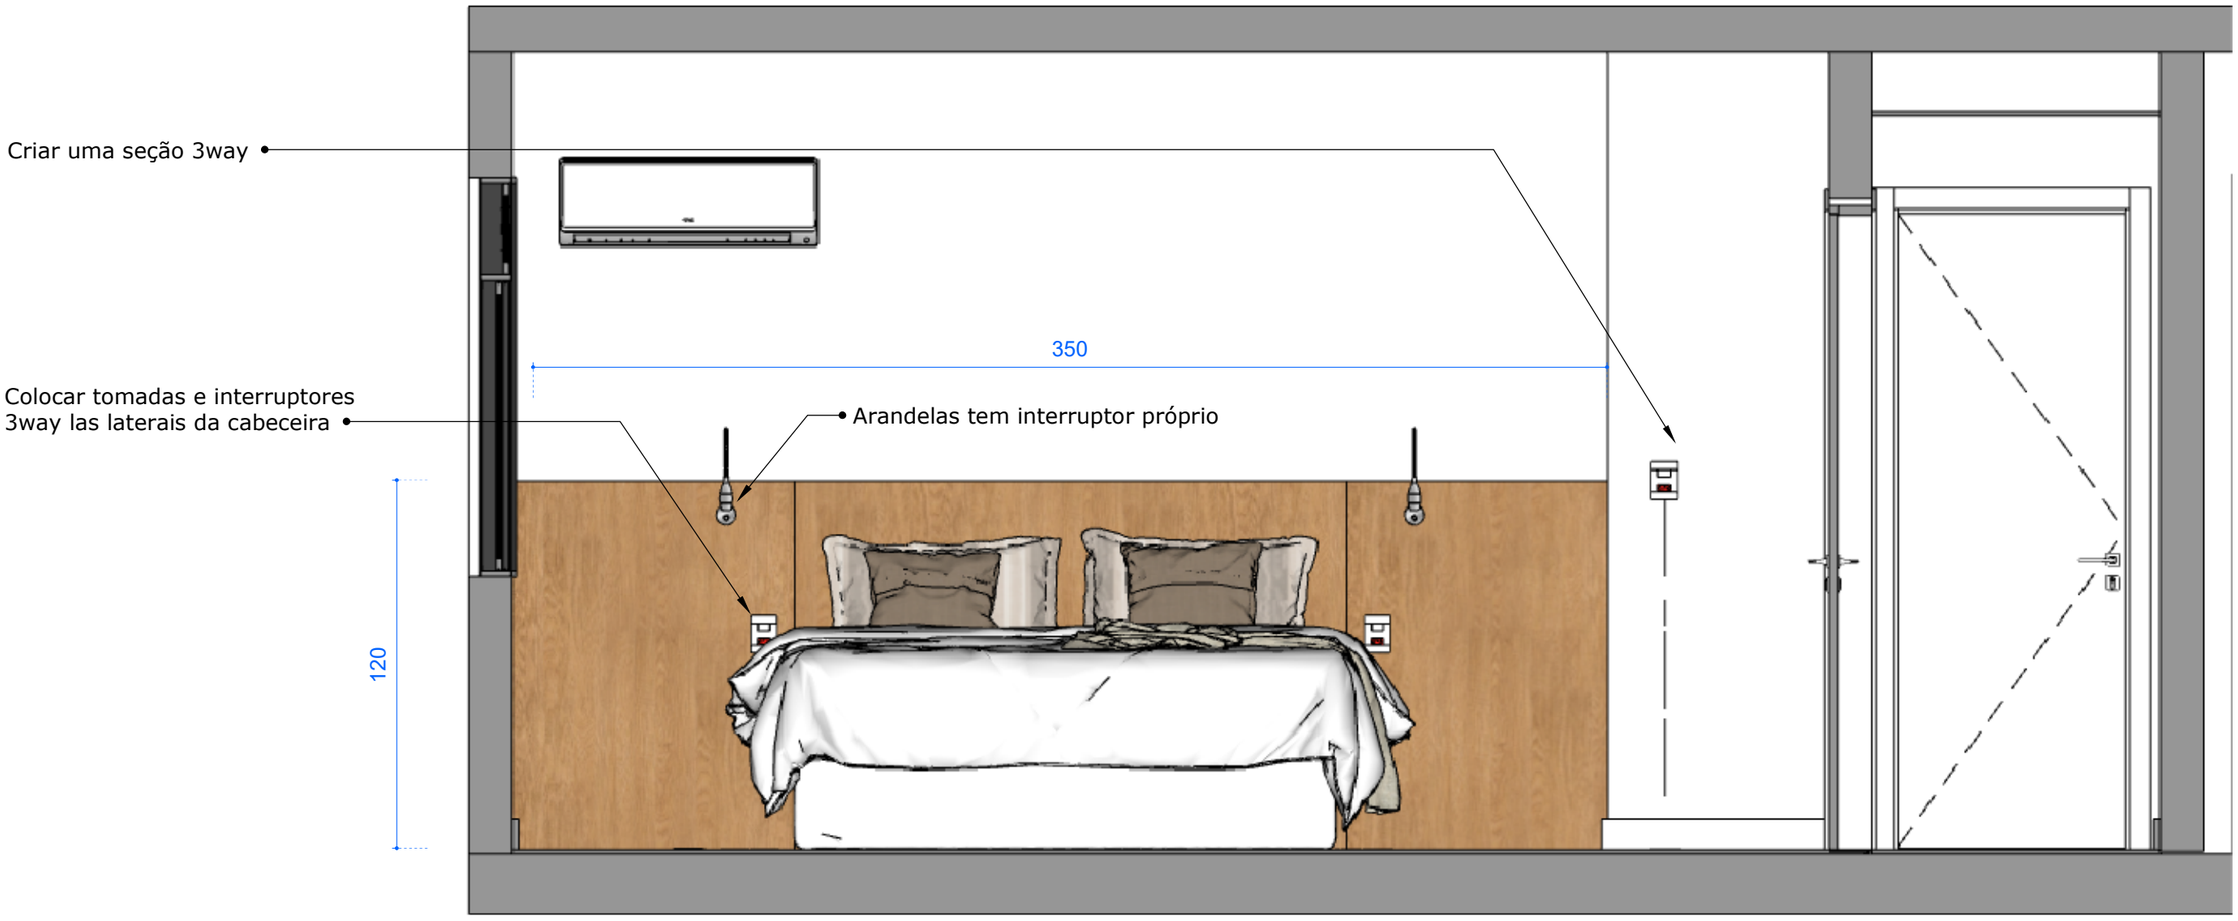

ARMÁRIO E CABECEIRA QUARTO - ELEV.

ESCALA 1:20

Projetos Residenciais
Projetos Comerciais
Projetos Interiores

ARQUITETO RESPONSÁVEL:
José Adalberto Meuren
CAU Nº 000A487848
(61)98274-3709
jmeuren@gmail.com

CONTEÚDO DA PRANCHA:
Elevação Cabeceira Quarto

ESCALA:
Indicada na Prancha

CLIENTE:
Caetana Juracy Rezende Silva
CPF: 576.328.801-78

ENDEREÇO:
SQN 403 Bl N Aptº 306
Brasília

ARQUIVO:
Marc_Caetana_SQN_403
REVISÃO Nº:
R00
DATA REVISÃO:
15-11-2025

OBSERVAÇÕES:
Consultar arquiteto em caso de dúvida e/ou alteração;
Conferir medidas no local;
Medidas em cota prevalecem sobre o desenho