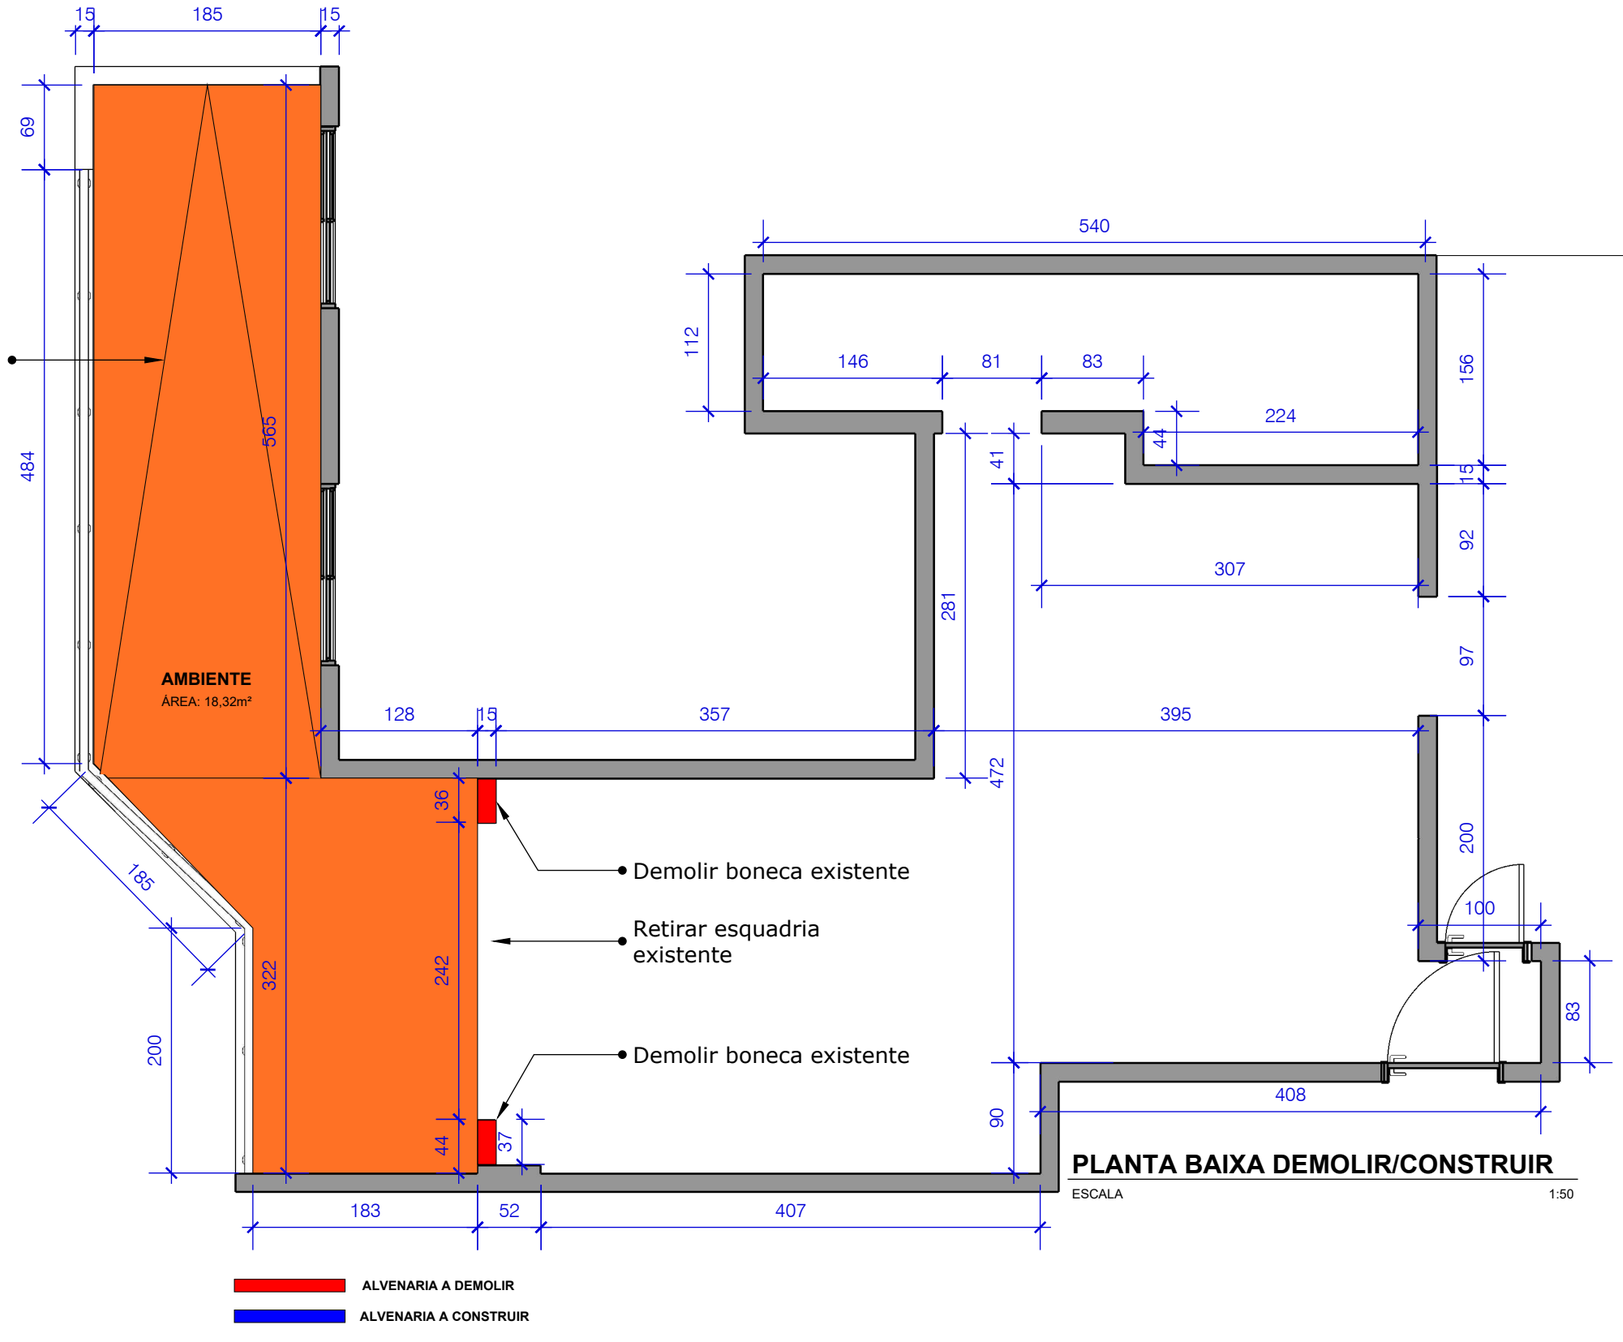



## PLANTA BAIXA DEMOLIR/CONSTRUIR

ESCALA 1:50

EMPÓRIO HASS ambientes planejados

contato@emporiohass.com.br

(61)99303-3151/98274-3709

emporiohass

# RESIDÊNCIA 314 NORTE

**CONTEÚDO**
Planta
Demolir/Construir

**TIPO**
Arquitetura de Interiores


**CLIENTE**
Débora Amarante Brancio Lopes Oliveira

**LOCALIZAÇÃO**
SQN 314 Bloco H Aptº 504
Asa Norte - DF

**ARQUIVO**
ARQ_INT_DEB_JAN2023

**AUTOR**
JMeuren - CAU Nº A487848

**REVISÃO**
01-02-2023

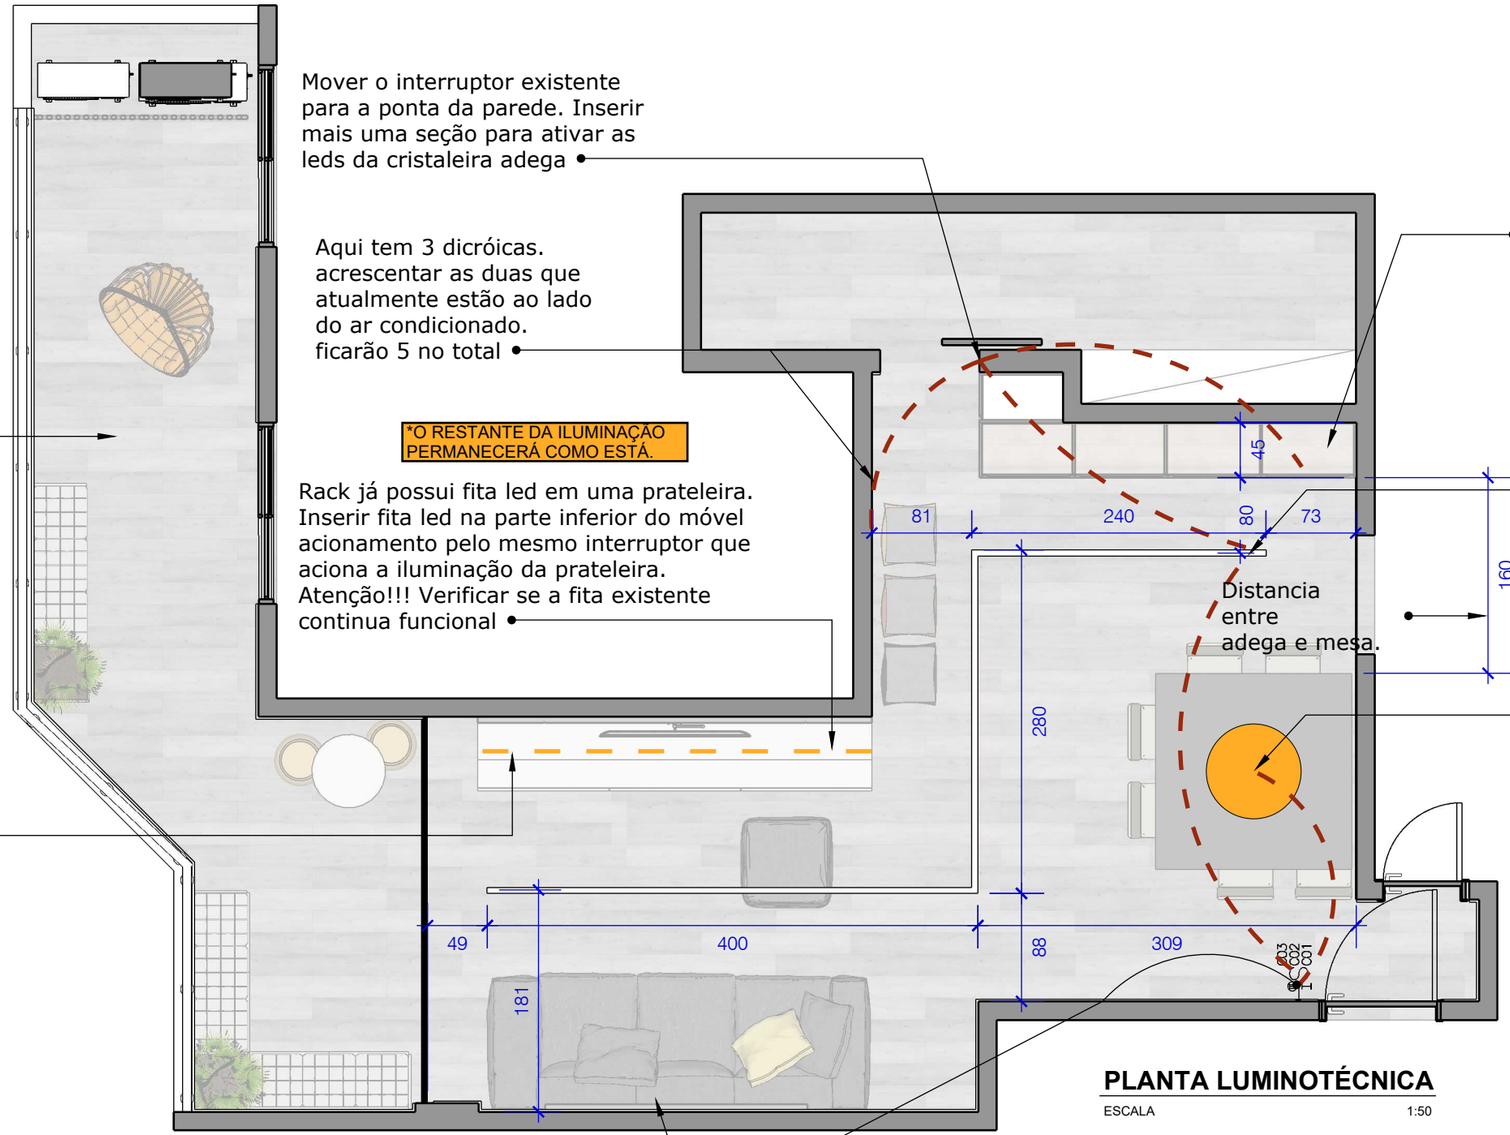


EMPÓRIO HASS ambientes planejados
contato@emporiohass.com.br
(61)99303-3151/98274-3709
emporiohass

# RESIDÊNCIA 314 NORTE

**CONTEÚDO**
Planta pontos

**TIPO**
Arquitetura de Interiores


**CLIENTE**
Débora Amarante Brancio Lopes Oliveira

**LOCALIZAÇÃO**
SQN 314 Bloco H Aptº 504
Asa Norte - DF

**ARQUIVO**
ARQ_INT_DEB_JAN2023

**AUTOR**
JMeuren - CAU Nº A487848

**REVISÃO**
01-02-2023

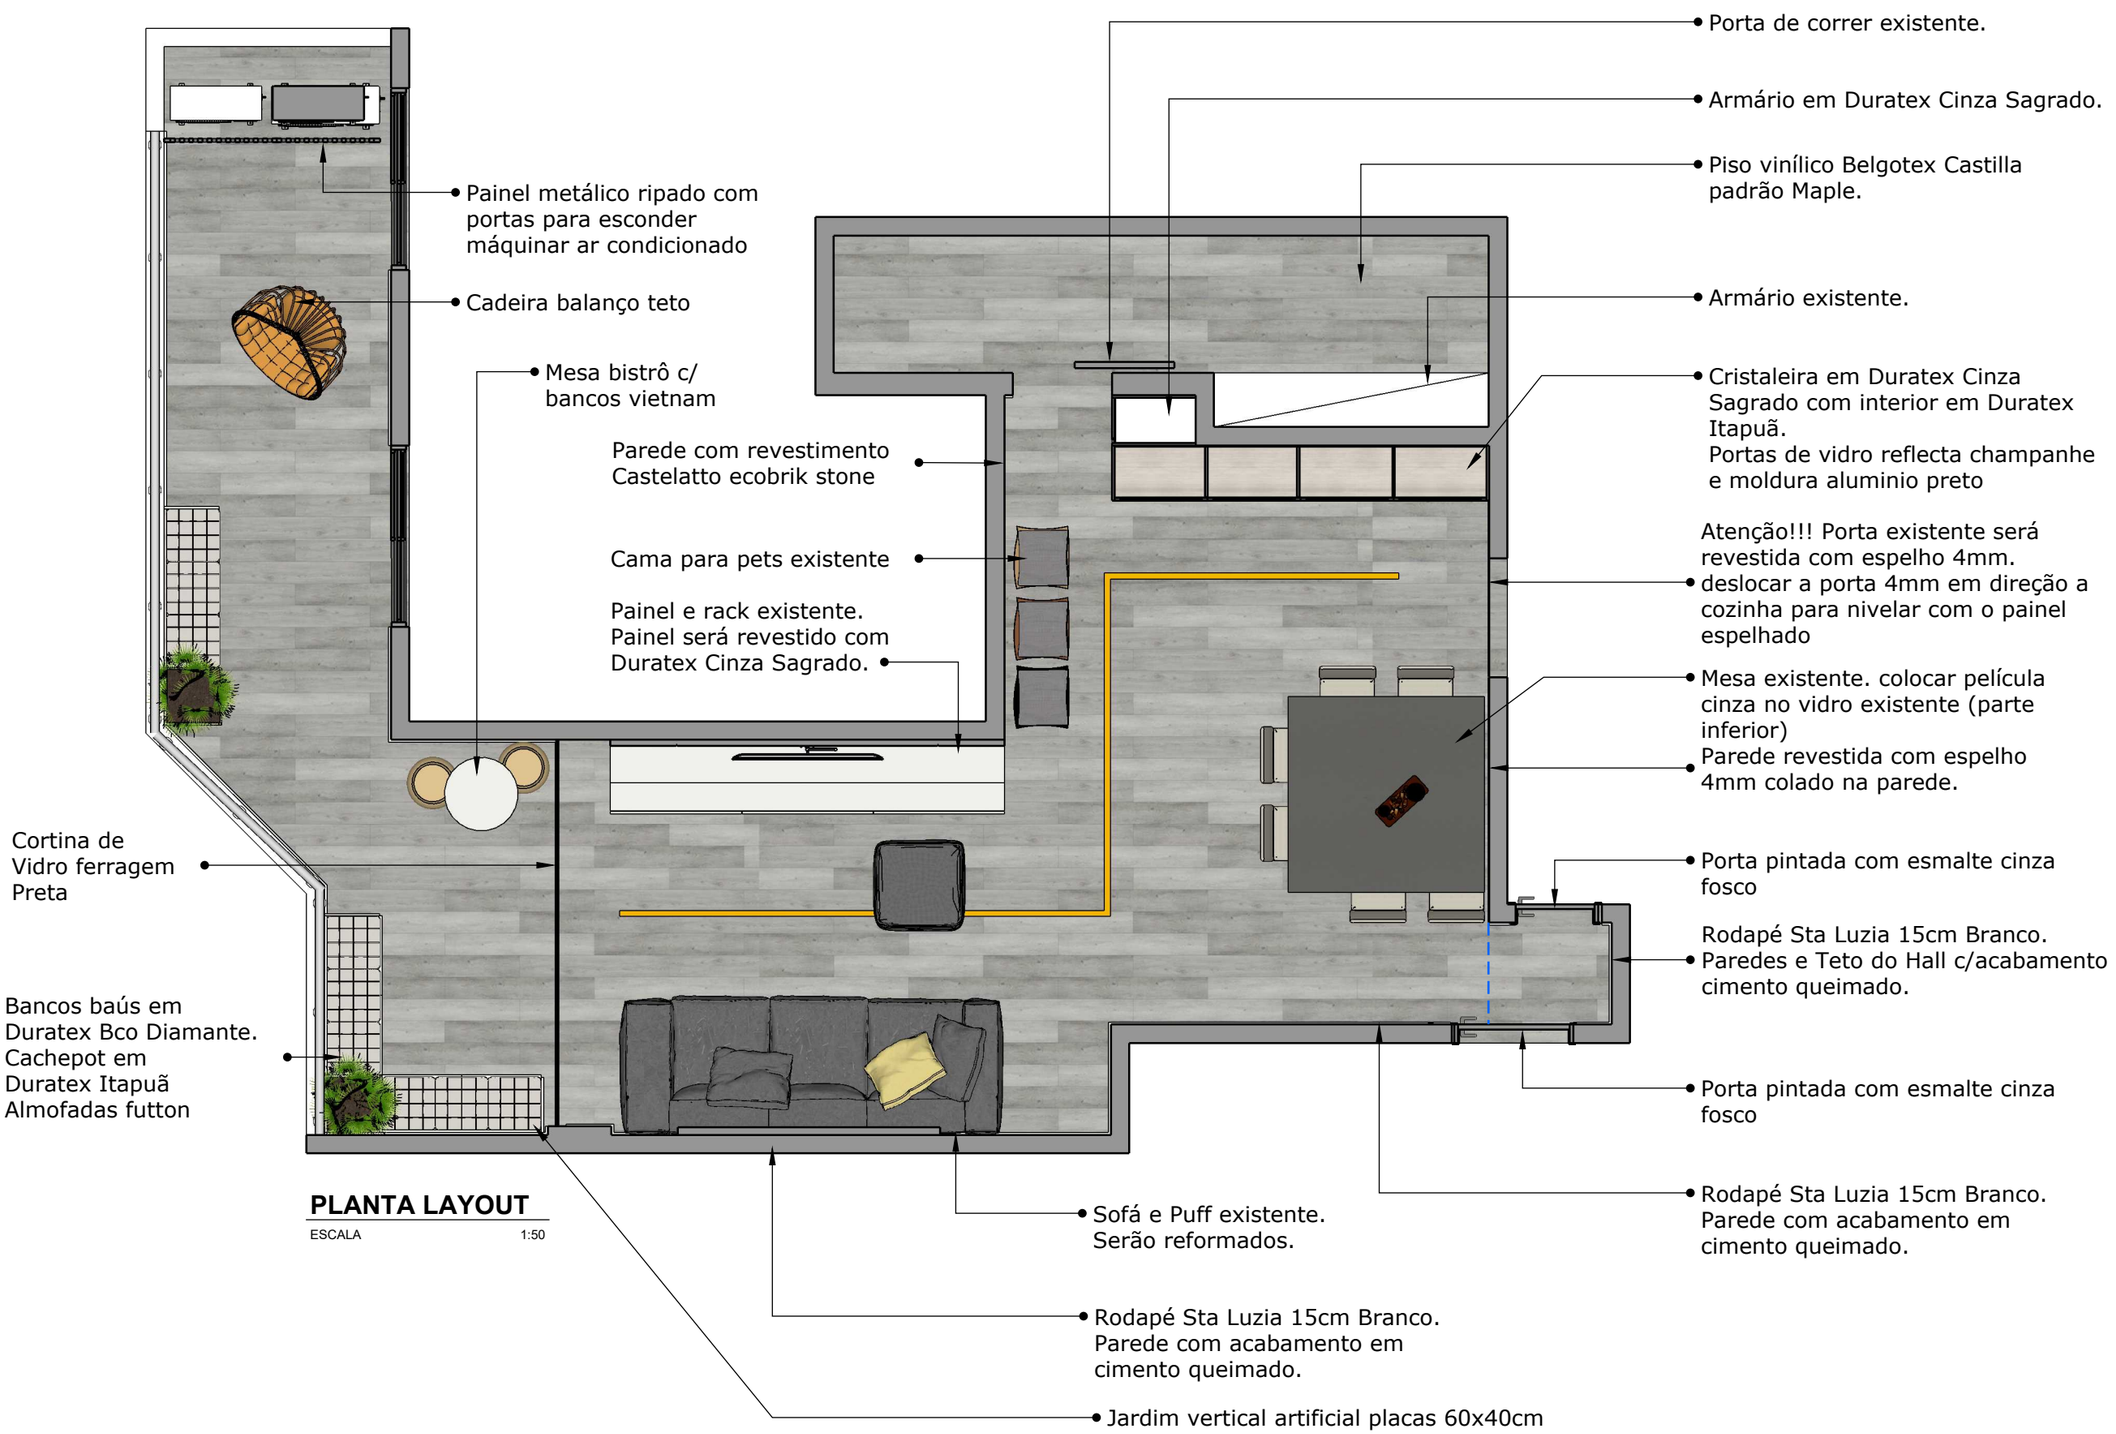


**PLANTA LAYOUT**

ESCALA 1:50

EMPÓRIO HASS ambientes planejados
contato@emporiohass.com.br
(61)99303-3151/98274-3709
emporiohass

# RESIDÊNCIA 314 NORTE

**CONTEÚDO**
Planta Layout

**TIPO**
Arquitetura de Interiores

**CLIENTE**
Débora Amarante Brancio Lopes Oliveira

**LOCALIZAÇÃO**
SQN 314 Bloco H Aptº 504
Asa Norte - DF


**ARQUIVO**
ARQ_INT_DEB_JAN2023

**AUTOR**
JMeuren - CAU Nº A487848

**REVISÃO**
01-02-2023

Porta existente será deslocada 4mm na direção da cozinha a fim de que seja colocado espelho 4mm e que a peça fique nivelada com o painel de espelhos a ser inserido

Pendente a escolher

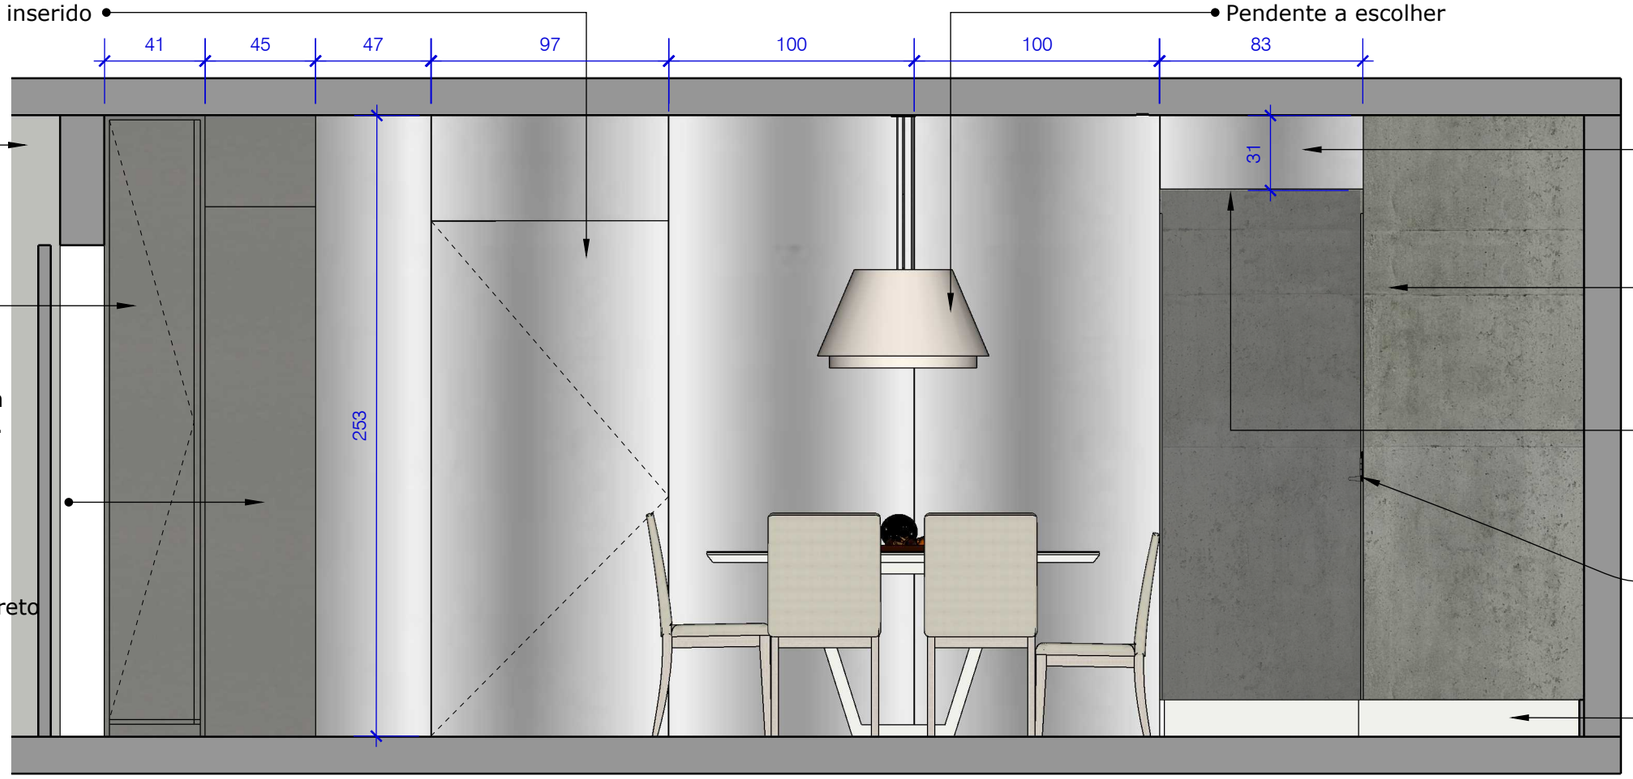


Paredes com acabamento tinta suvinil papel picado

Armário em Duratex Cinza Sagrado

Cristaleira estrutura em Duratex Cinza Sagrado. Parte interna em Duratex Itapuã. Prateleiras com iluminação Led. Portas em Vidro Reflecta Champanhe moldura em aluminio preto

Painel espelho 4mm

Parede pintura imitando cimento queimado

Teto com pintura imitando cimento queimado

Porta com pintura cinza acetinado

Rodapé Sta Luzia branco 15cm

## SALA - VISTA A

ESCALA 1:50


EMPÓRIO HASS ambientes planejados

contato@emporiohass.com.br

(61)99303-3151/98274-3709

emporiohass


# RESIDÊNCIA 314 NORTE

**CONTEÚDO**
Sala - Vista A

**TIPO**
Arquitetura de Interiores


**CLIENTE**
Débora Amarante Brancio Lopes Oliveira

**LOCALIZAÇÃO**
SQN 314 Bloco H Aptº 504
Asa Norte - DF

**ARQUIVO**
ARQ_INT_DEB_JAN2023

**AUTOR**
JMeuren - CAU Nº A487848

**REVISÃO**
01-02-2023

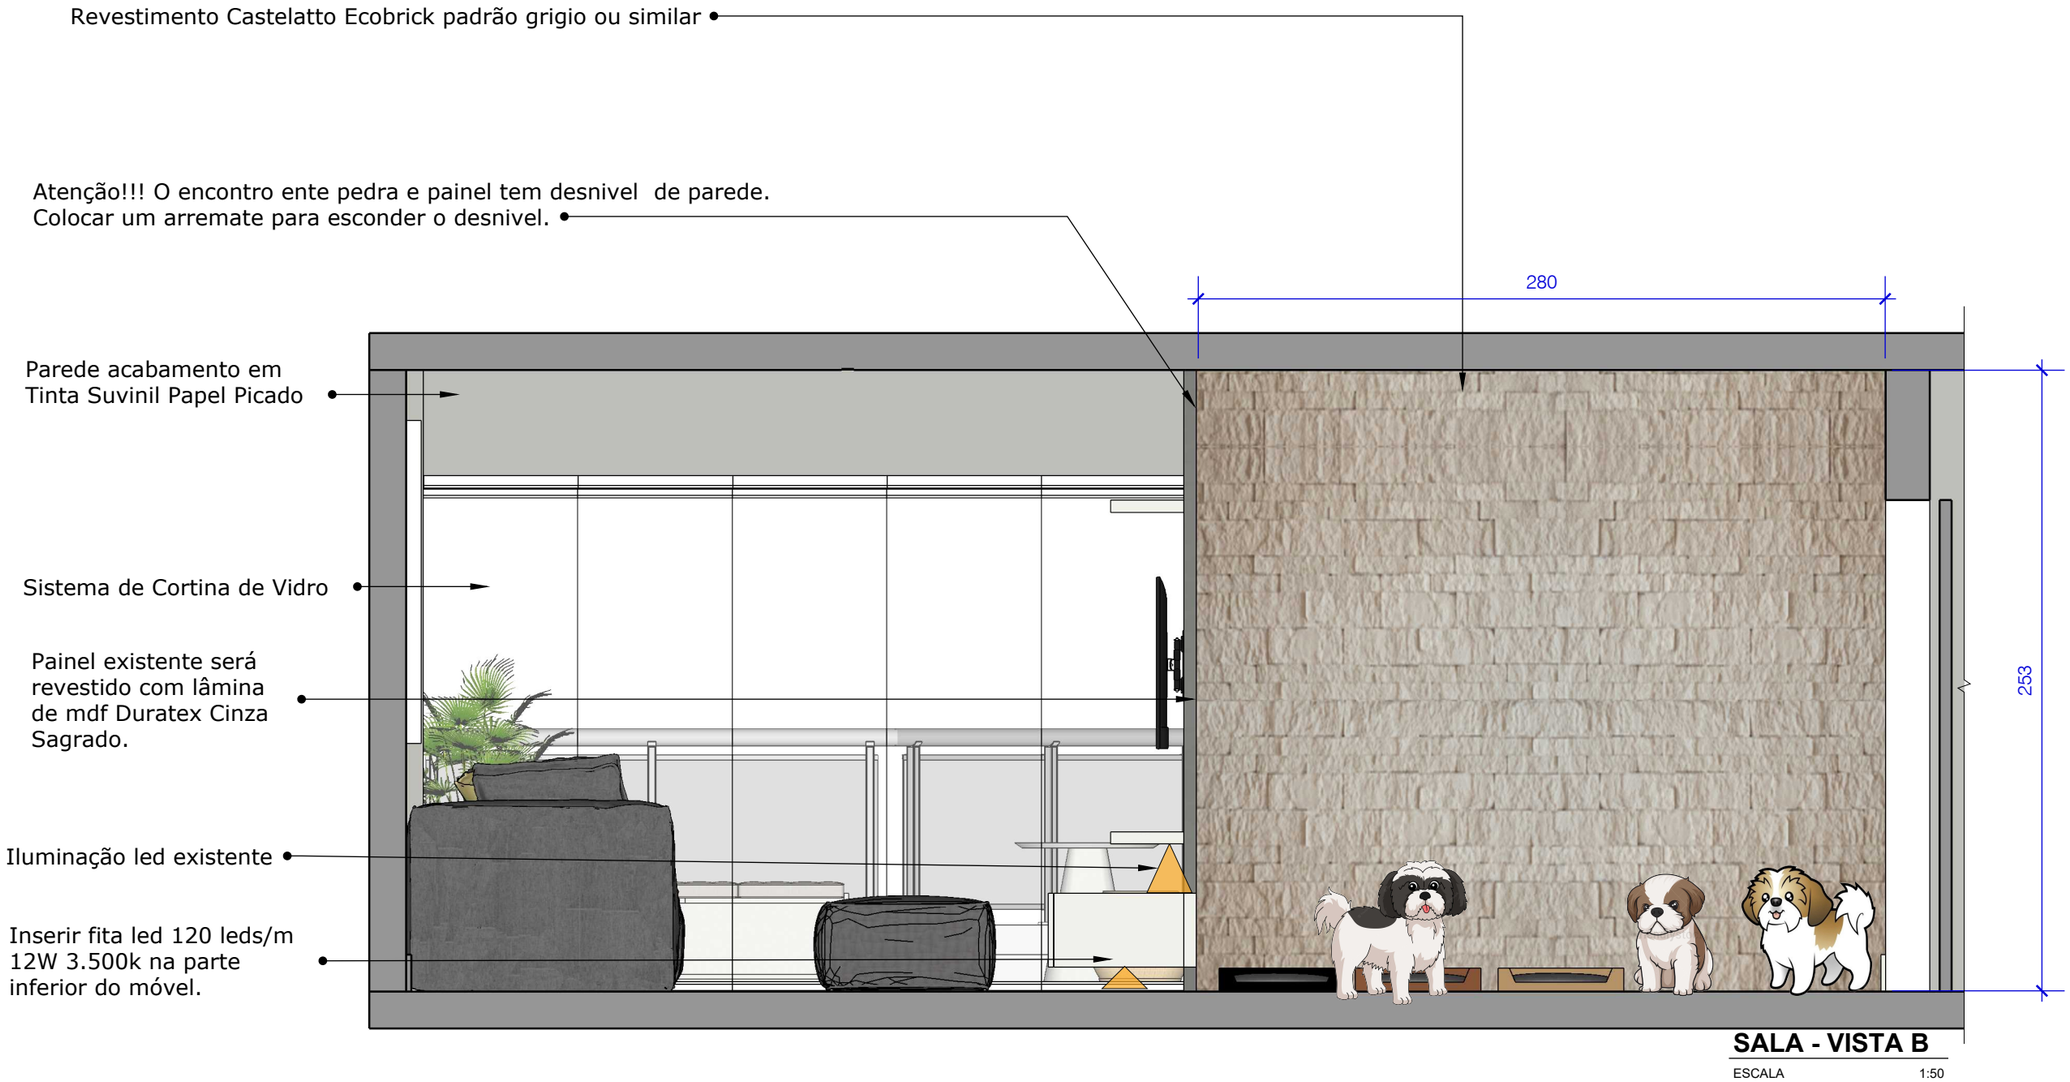


**SALA - VISTA B**

ESCALA 1:50

EMPÓRIO HASS ambientes planejados

contato@emporiohass.com.br

(61)99303-3151/98274-3709

emporiohass

# RESIDÊNCIA 314 NORTE

**CONTEÚDO**
Sala - Vista B

**TIPO**
Arquitetura de Interiores

**CLIENTE**
Débora Amarante Brancio Lopes Oliveira


**LOCALIZAÇÃO**

SQN 314 Bloco H Aptº 504
Asa Norte - DF

**ARQUIVO**
ARQ_INT_DEB_JAN2023

**AUTOR**
JMeuren - CAU Nº A487848

**REVISÃO**
01-02-2023

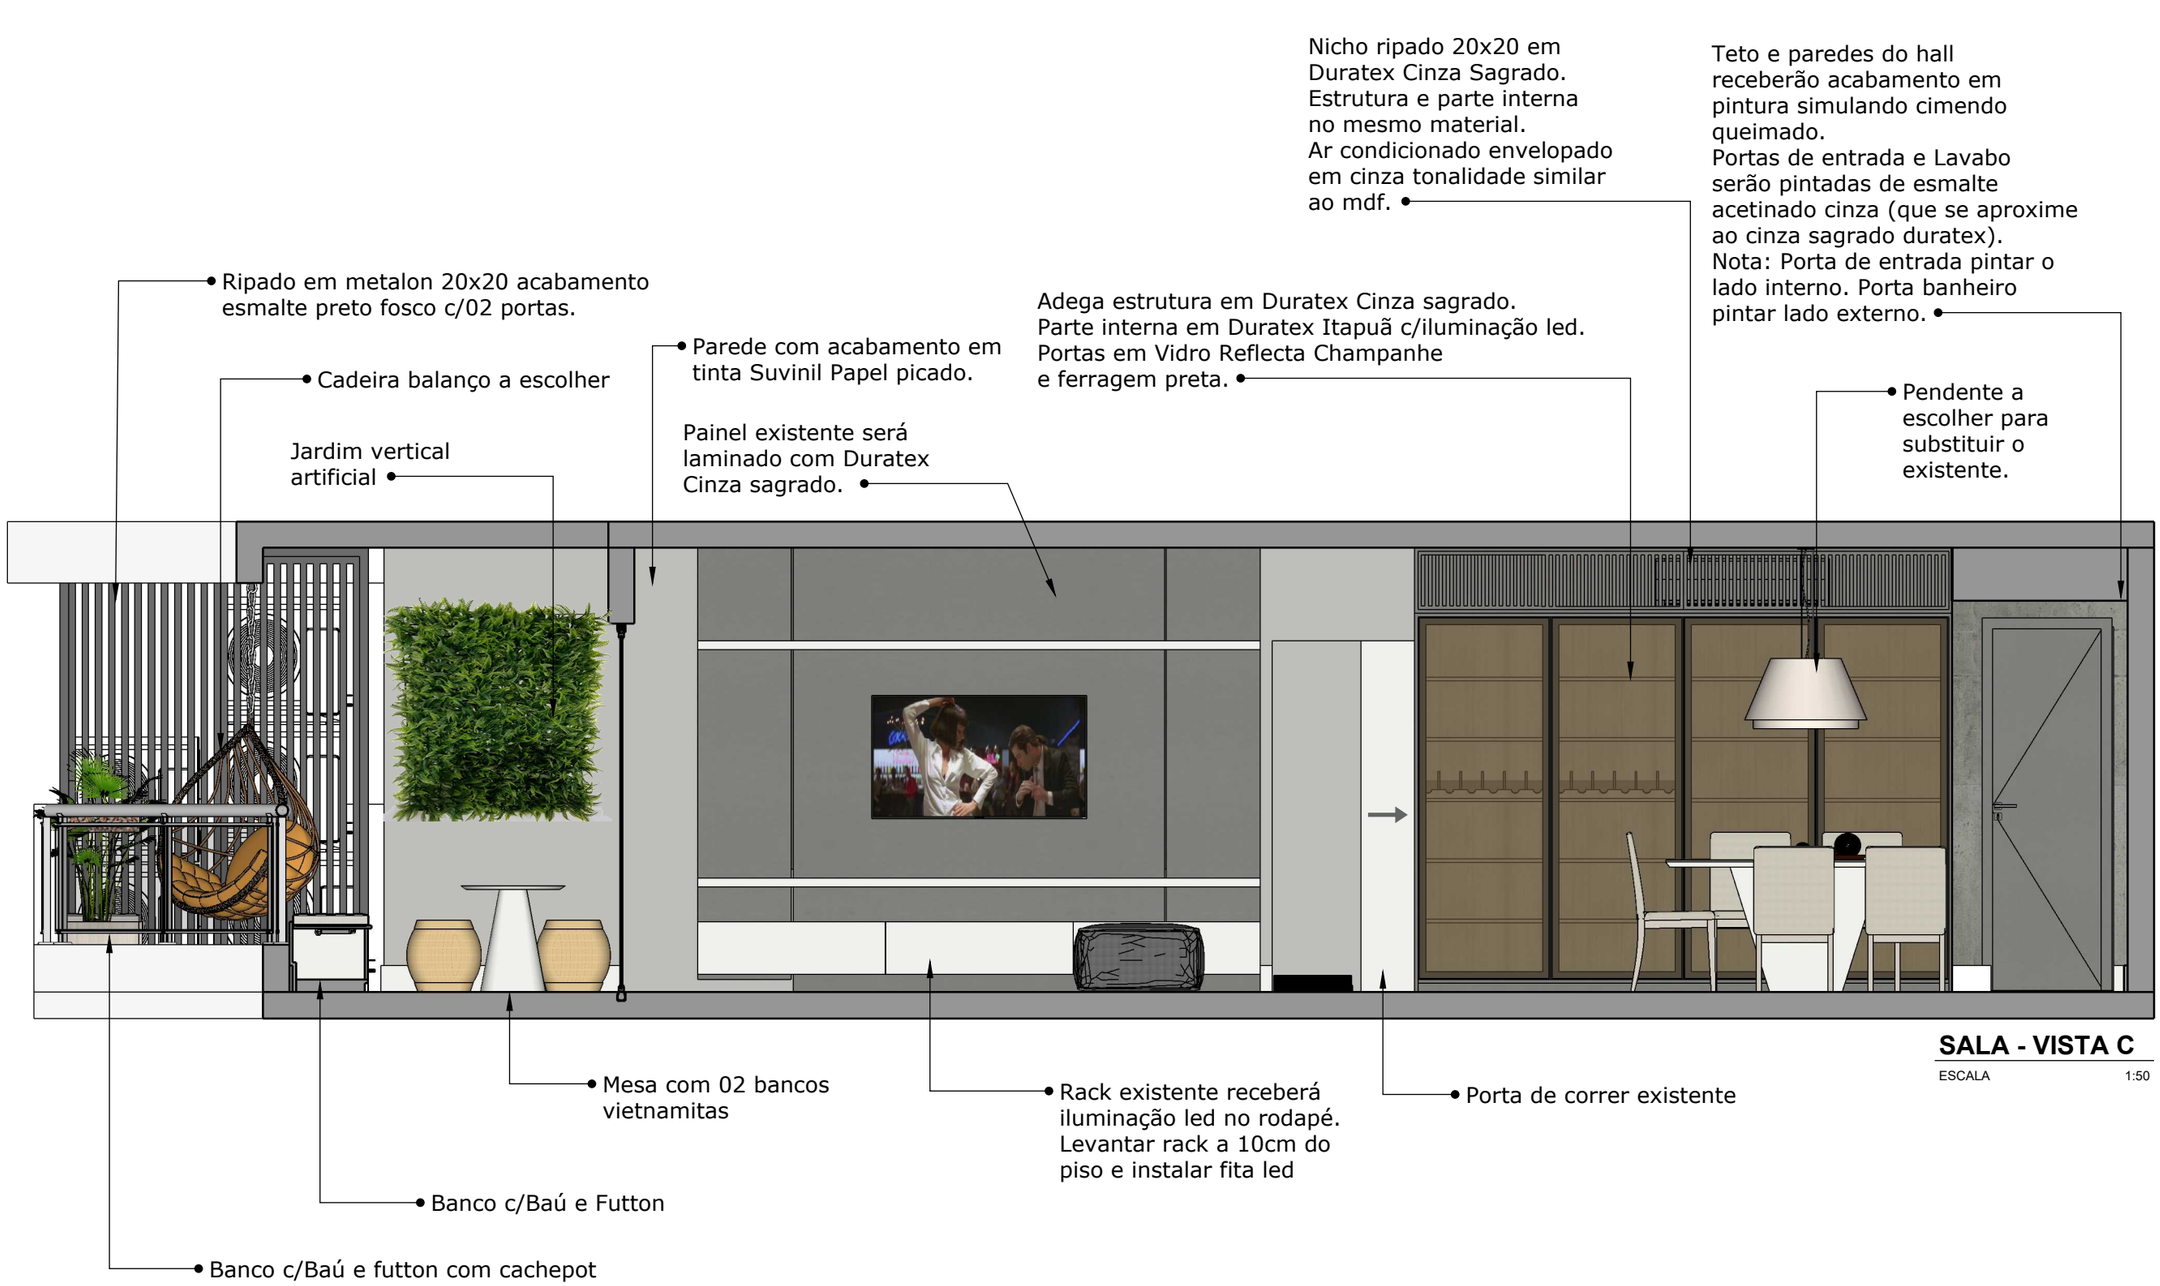


**SALA - VISTA C**

ESCALA 1:50

EMPÓRIO HASS ambientes planejados
contato@emporiohass.com.br
(61)99303-3151/98274-3709
emporiohass

# RESIDÊNCIA 314 NORTE

**CONTEÚDO**
Sala - Vista C

**TIPO**
Arquitetura de Interiores


**CLIENTE**
Débora Amarante Brancio Lopes Oliveira

**LOCALIZAÇÃO**
SQN 314 Bloco H Aptº 504
Asa Norte - DF

**ARQUIVO**
ARQ_INT_DEB_JAN2023


**AUTOR**
JMeuren - CAU Nº A487848

**REVISÃO**
01-02-2023

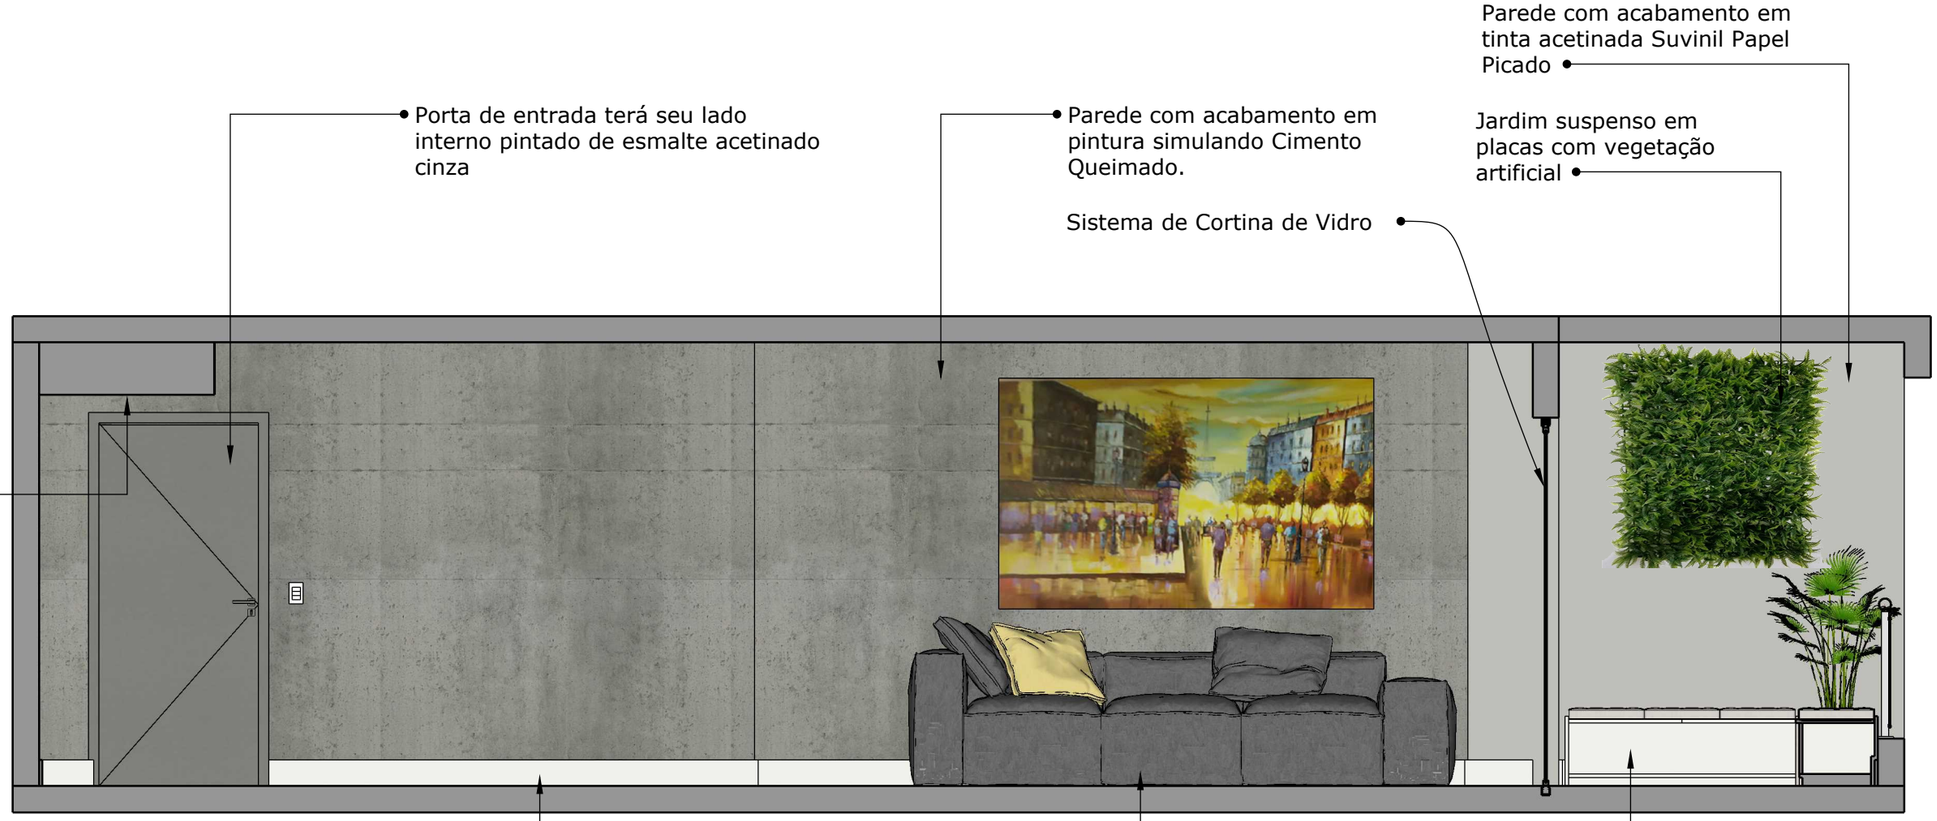


**SALA - VISTA D**

ESCALA 1:50

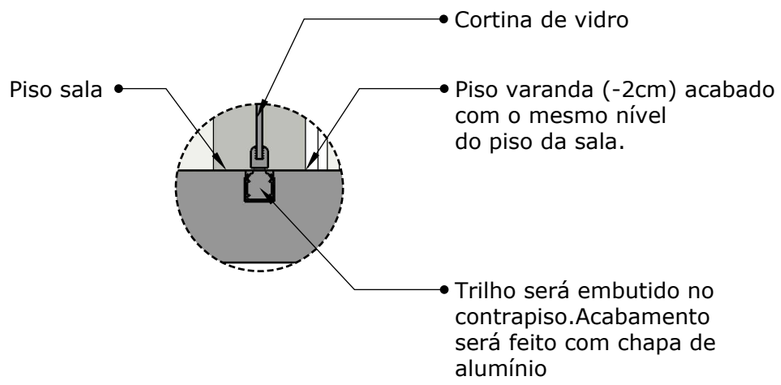


EMPÓRIO HASS ambientes planejados

contato@emporiohass.com.br
(61)99303-3151/98274-3709
emporiohass

# RESIDÊNCIA 314 NORTE

**CONTEÚDO**
Sala - Vista D

**TIPO**
Arquitetura de Interiores


**CLIENTE**
Débora Amarante Brancio Lopes Oliveira

**LOCALIZAÇÃO**
SQN 314 Bloco H Aptº 504
Asa Norte - DF

**ARQUIVO**
ARQ_INT_DEB_JAN2023


**AUTOR**
JMeuren - CAU Nº A487848


**REVISÃO**
01-02-2023

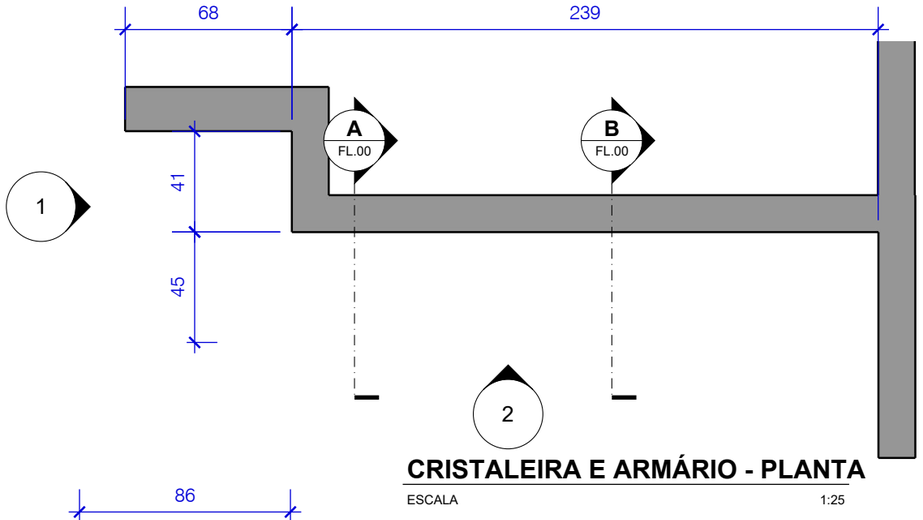


## CRISTALEIRA E ARMÁRIO - PLANTA


ESCALA 1:25

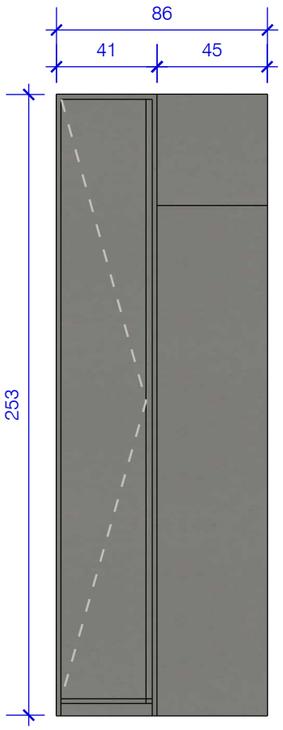

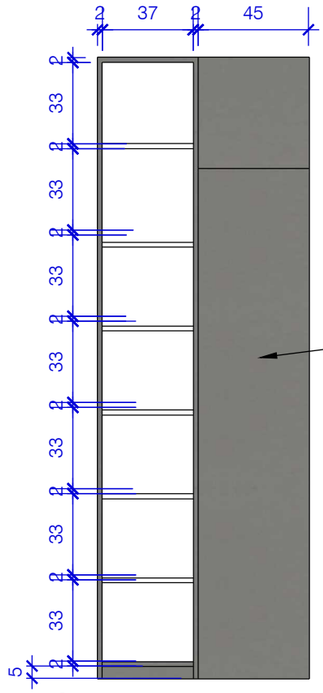

## CRISTALEIRA E ARMÁRIO - VISTA 01


ESCALA 1:25

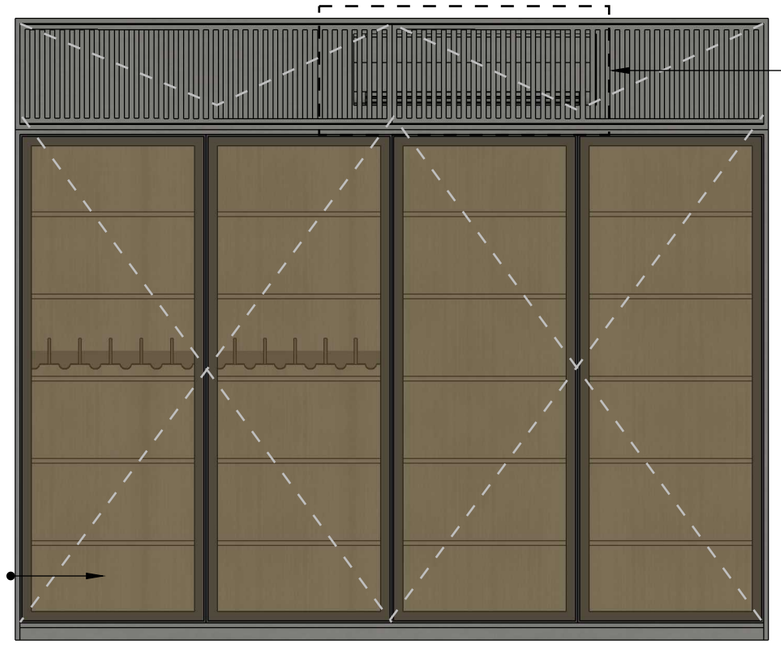


## CRISTALEIRA E ARMÁRIO - VISTA 02


ESCALA 1:25

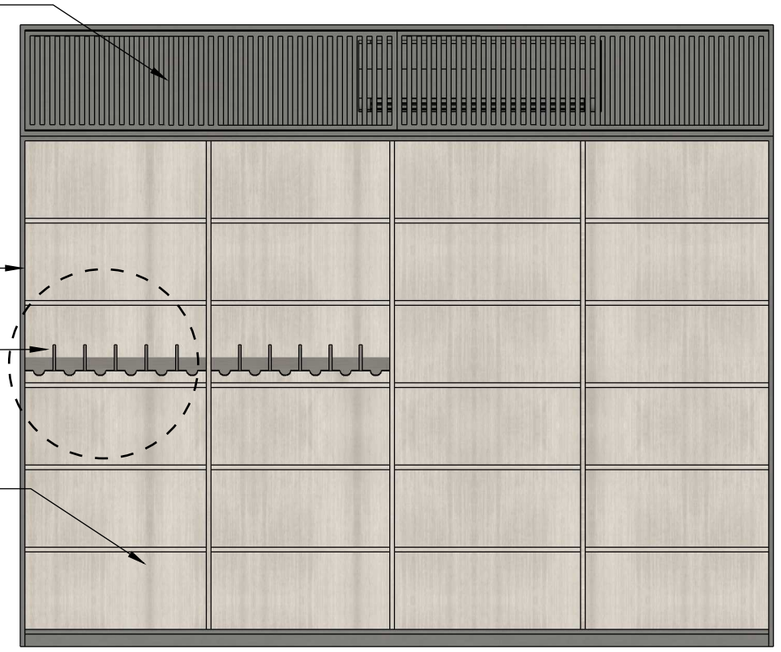

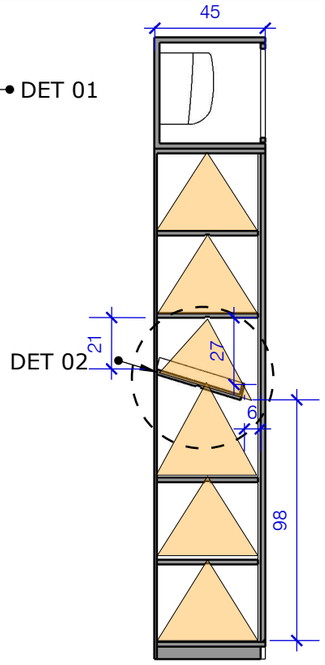

## CORTE A

ESCALA 1:25

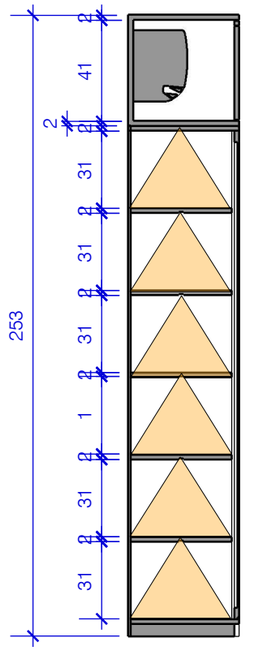



## CORTE B

ESCALA 1:25

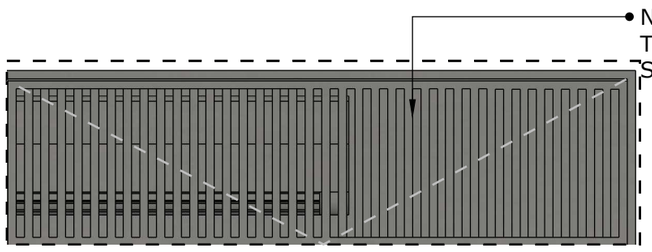



## DET 01

ESCALA 1:15

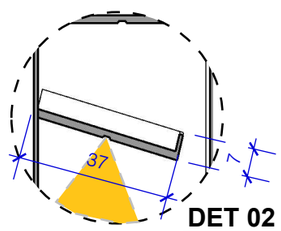


## DET 02

ESCALA 1:15

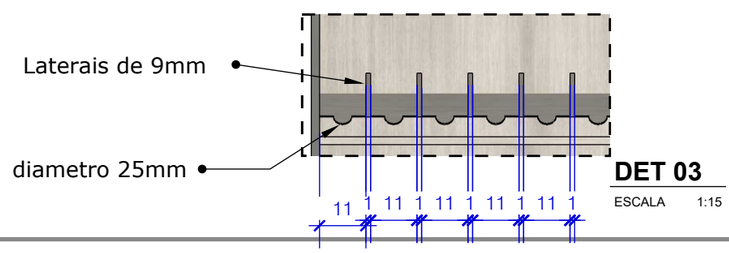


## DET 03

ESCALA 1:15

EMPÓRIO HASS ambientes planejados

contato@emporiohass.com.br
(61)99303-3151/98274-3709
emporiohass

# RESIDÊNCIA 314 NORTE

**CONTEÚDO**
Sala - Marcenaria
Adega e Armário

**TIPO**
Arquitetura de Interiores


**CLIENTE**
Débora Amarante Brancio
Lopes Oliveira

**LOCALIZAÇÃO**
SQN 314 Bloco H Aptº 504
Asa Norte - DF

**ARQUIVO**
ARQ_INT_DEB_JAN2023


**AUTOR**
JMeuren - CAU Nº A487848

**REVISÃO**
01-02-2023

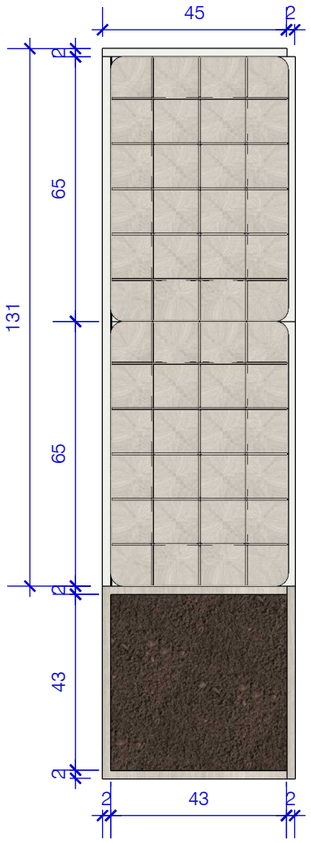



**BANCO - PLANTA**

ESCALA 1:15

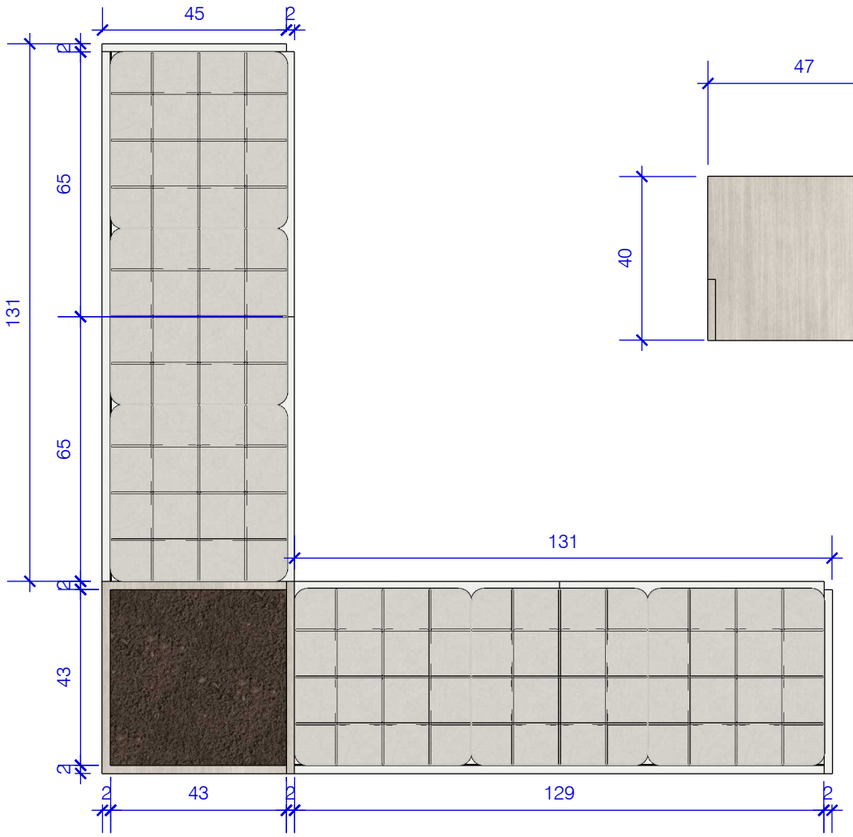



**BANCO - PLANTA**


ESCALA 1:15

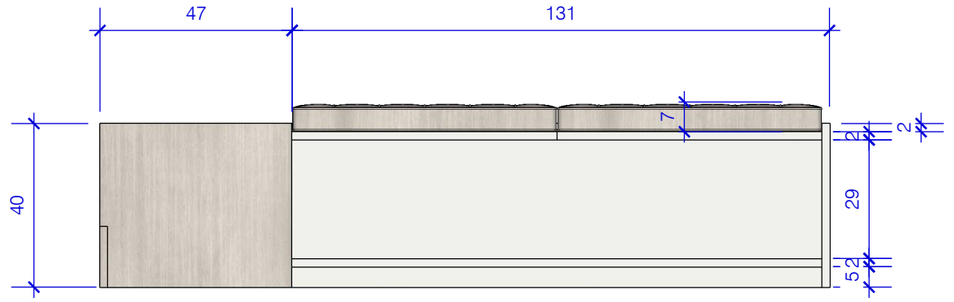


**BANCO - ELEVAÇÃO**

ESCALA 1:15

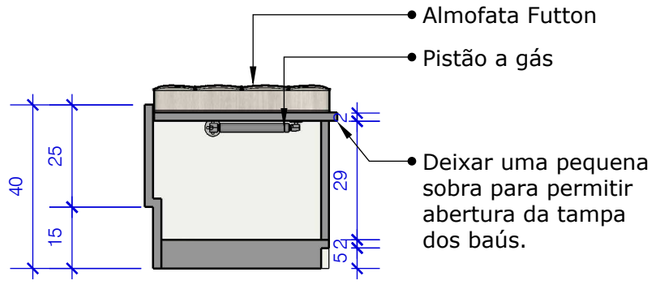

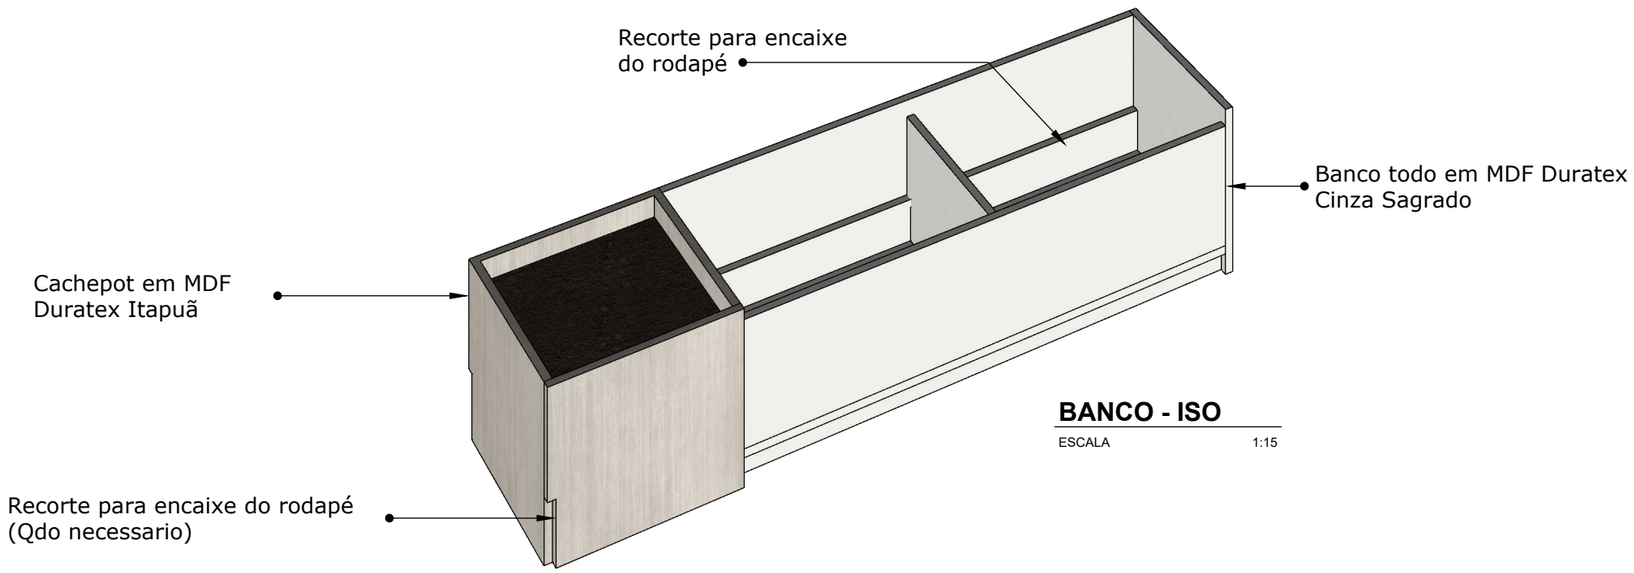
**BANCO - ISO**

ESCALA 1:15

EMPÓRIO HASS ambientes planejados

contato@emporiohass.com.br

(61)99303-3151/98274-3709

emporiohass

# RESIDÊNCIA 314 NORTE

**CONTEÚDO**
Sala - Marcenaria
Varanda

**TIPO**
Arquitetura de Interiores

**CLIENTE**
Débora Amarante Brancio Lopes Oliveira


**LOCALIZAÇÃO**

SQN 314 Bloco H Aptº 504
Asa Norte - DF

**ARQUIVO**
ARQ_INT_DEB_JAN2023

**AUTOR**
JMeuren - CAU Nº A487848

**REVISÃO**
01-02-2023

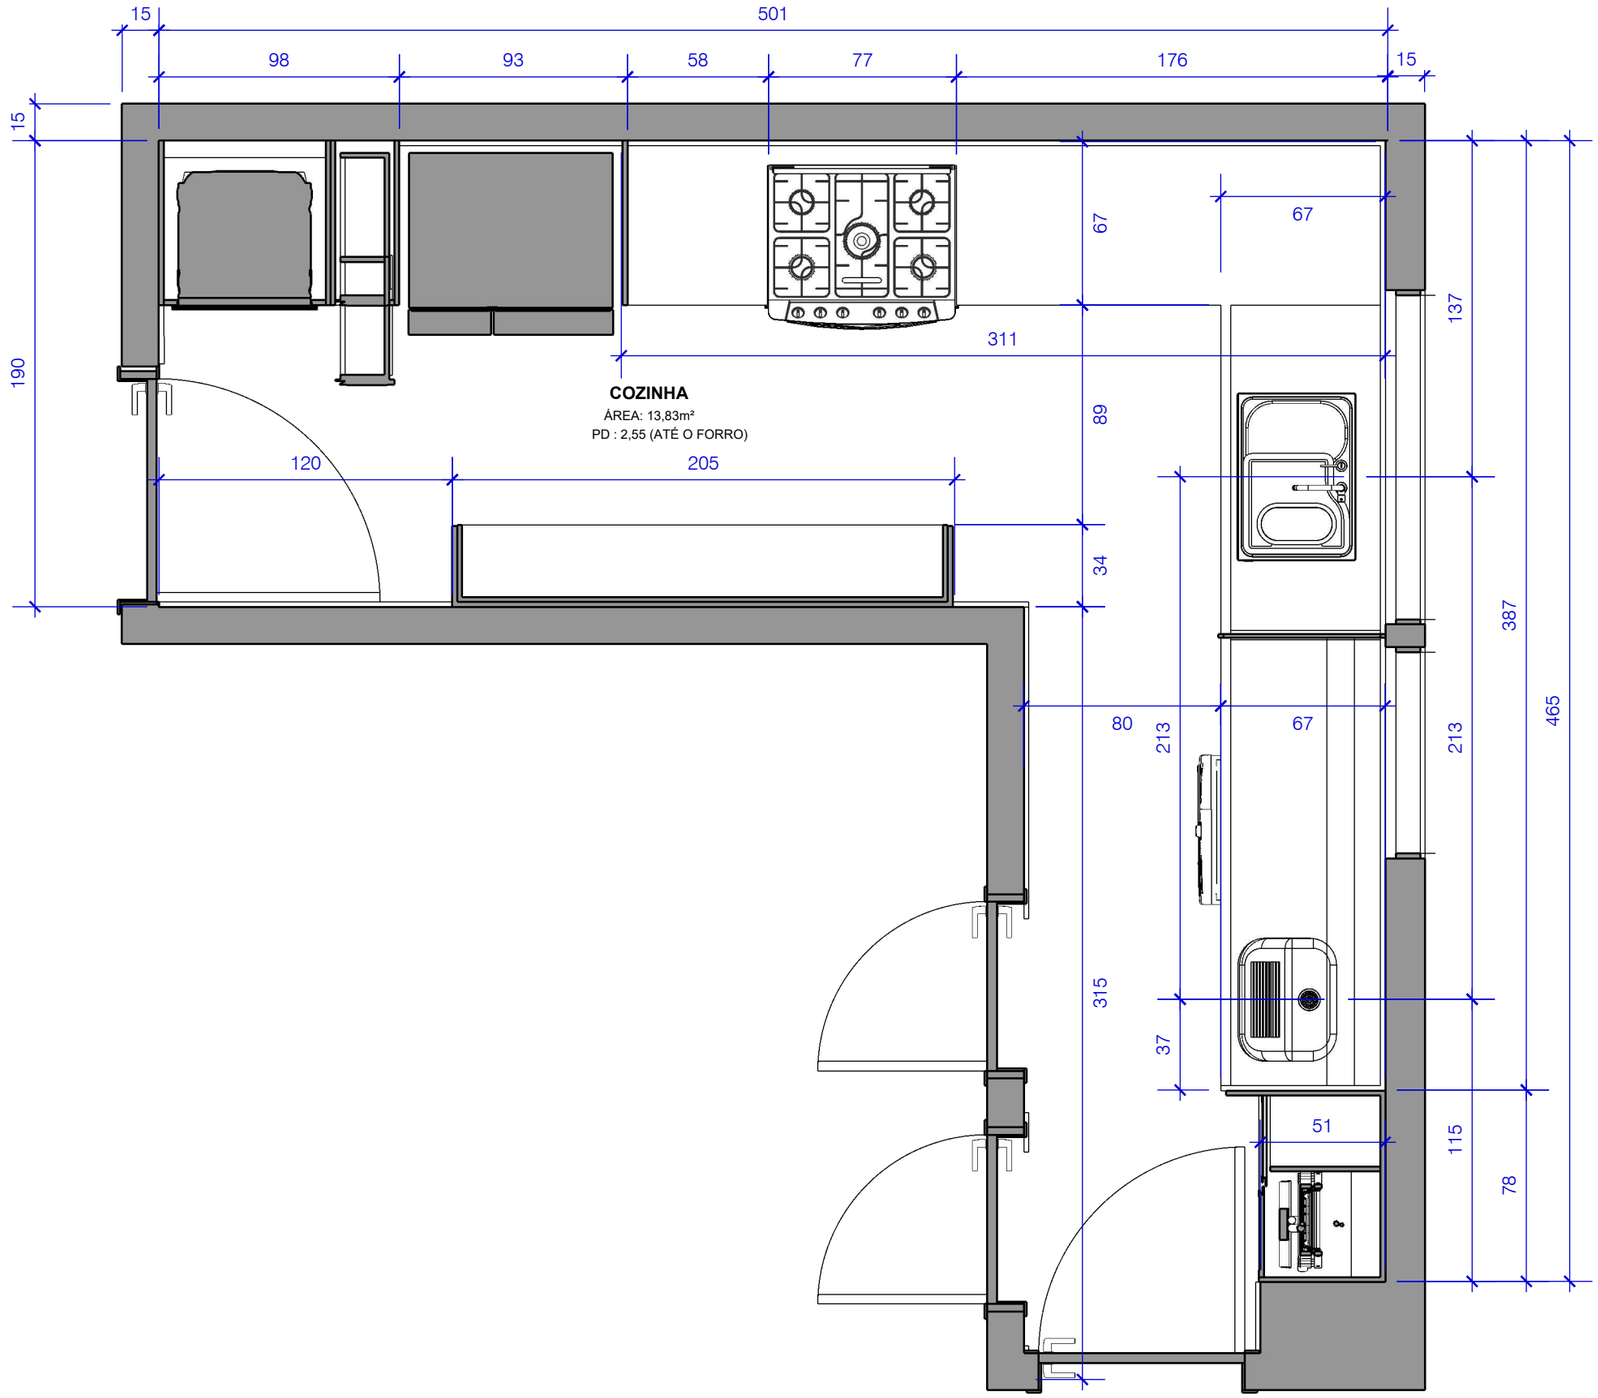


## COZINHA - PLANTA

ESCALA 1:25

EMPÓRIO HASS ambientes planejados
contato@emporiohass.com.br
(61)99303-3151/98274-3709
emporiohass

# RESIDÊNCIA 314 NORTE

**CONTEÚDO**
Cozinha - Planta Baixa

**TIPO**
Arquitetura de Interiores


**CLIENTE**
Débora Amarante Brancio Lopes Oliveira

**LOCALIZAÇÃO**
SQN 314 Bloco H Aptº 504
Asa Norte - DF

**ARQUIVO**
ARQ_INT_DEB_JAN2023

**AUTOR**
JMeuren - CAU Nº A487848

**REVISÃO**
01-02-2023

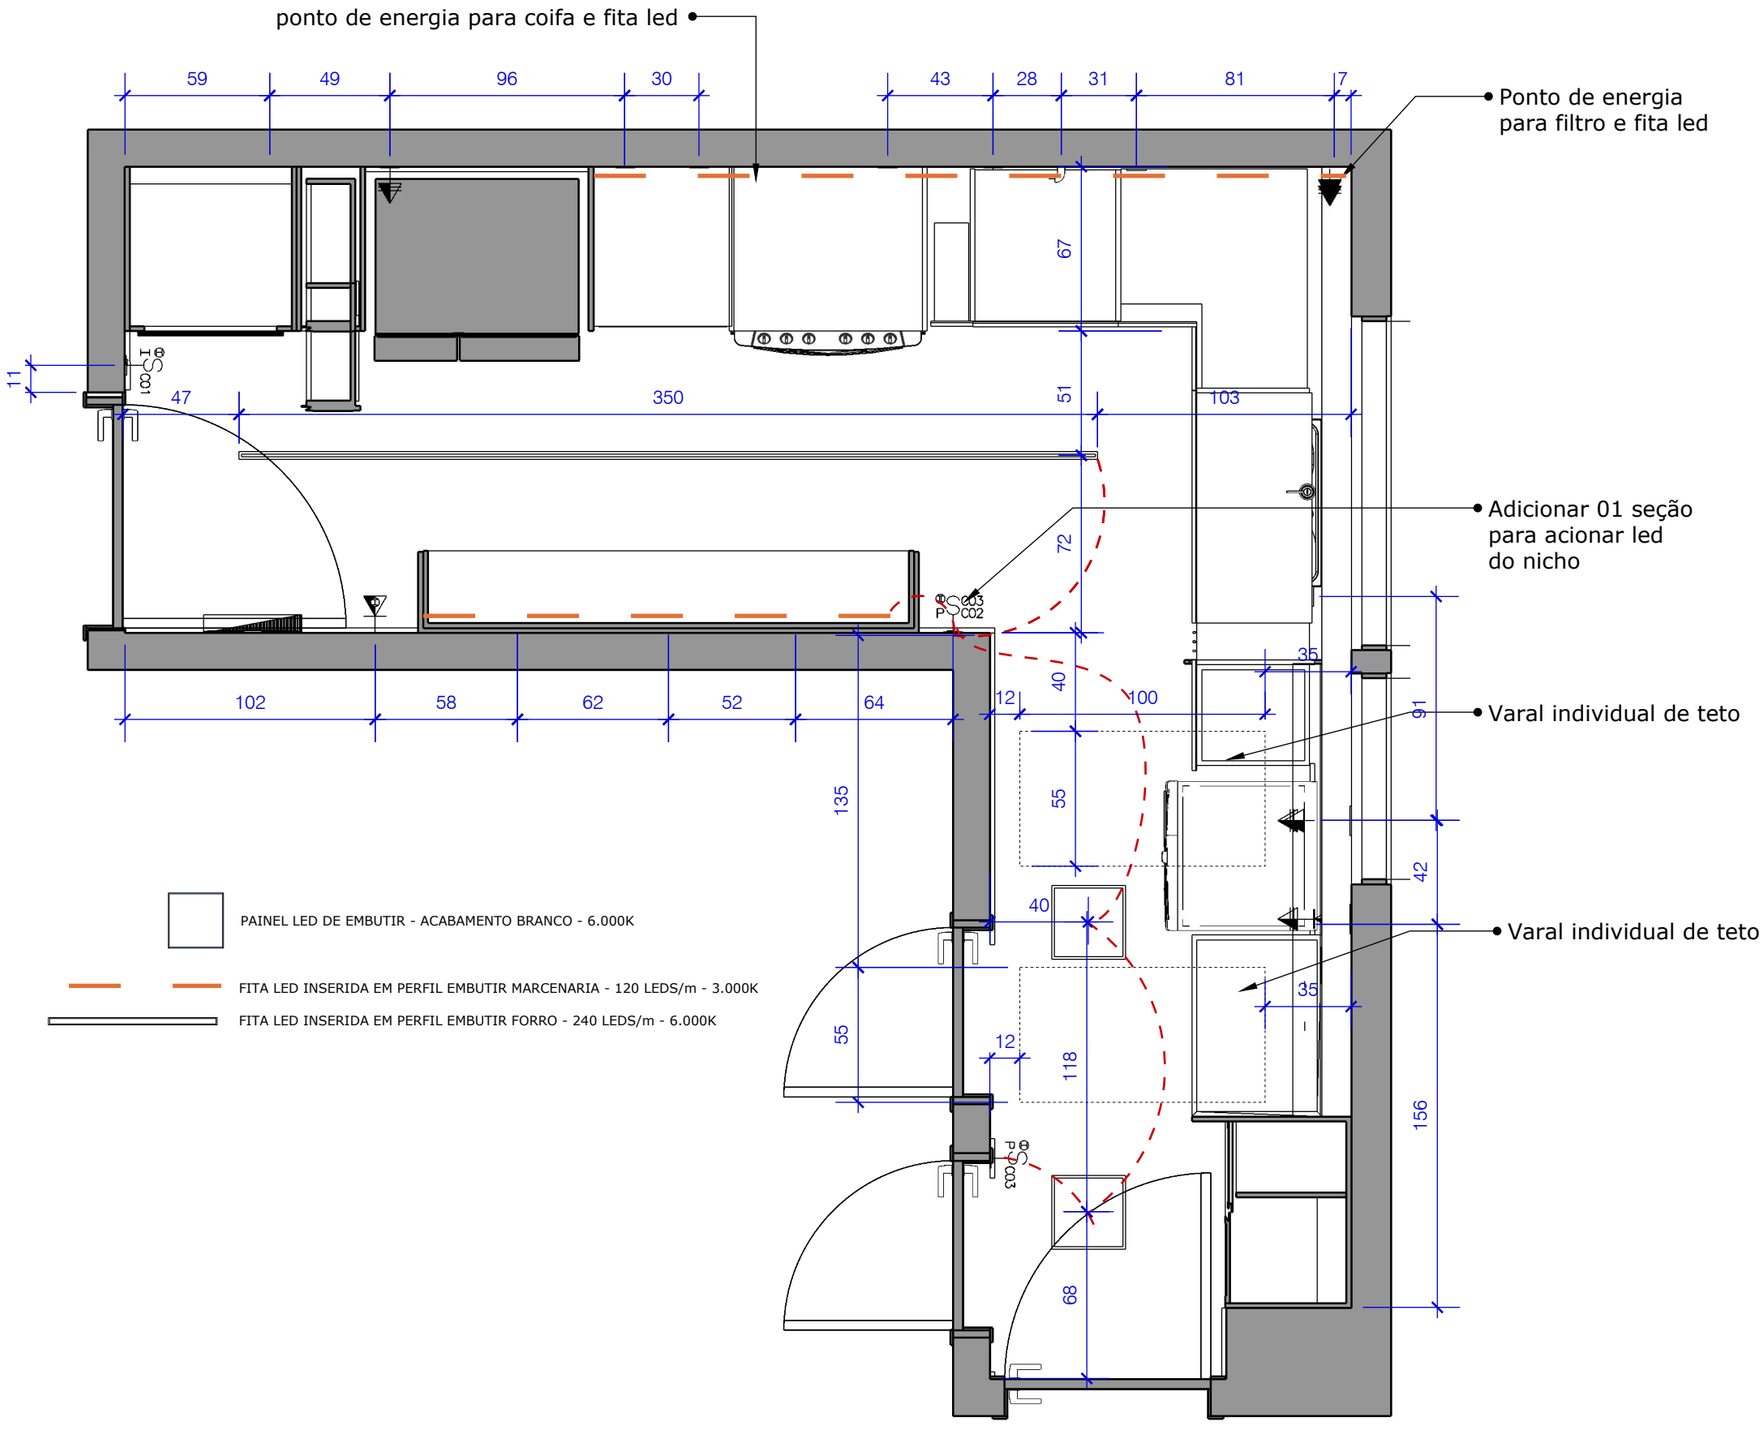


PAINEL LED DE EMBUTIR - ACABAMENTO BRANCO - 6.000K

FITA LED INSERIDA EM PERFIL EMBUTIR MARCENARIA - 120 LEDS/m - 3.000K

FITA LED INSERIDA EM PERFIL EMBUTIR FORRO - 240 LEDS/m - 6.000K

## COZINHA - LUMINOTÉCNICA

ESCALA 1:25


EMPÓRIO HASS ambientes planejados

contato@emporiohass.com.br

(61)99303-3151/98274-3709

emporiohass


# RESIDÊNCIA 314 NORTE

**CONTEÚDO**
Cozinha - Luminotécnica

**TIPO**
Arquitetura de Interiores

**CLIENTE**
Débora Amarante Brancio Lopes Oliveira


**LOCALIZAÇÃO**

SQN 314 Bloco H Aptº 504
Asa Norte - DF

**ARQUIVO**
ARQ_INT_DEB_JAN2023

**AUTOR**
JMeuren - CAU Nº A487848

**REVISÃO**
01-02-2023

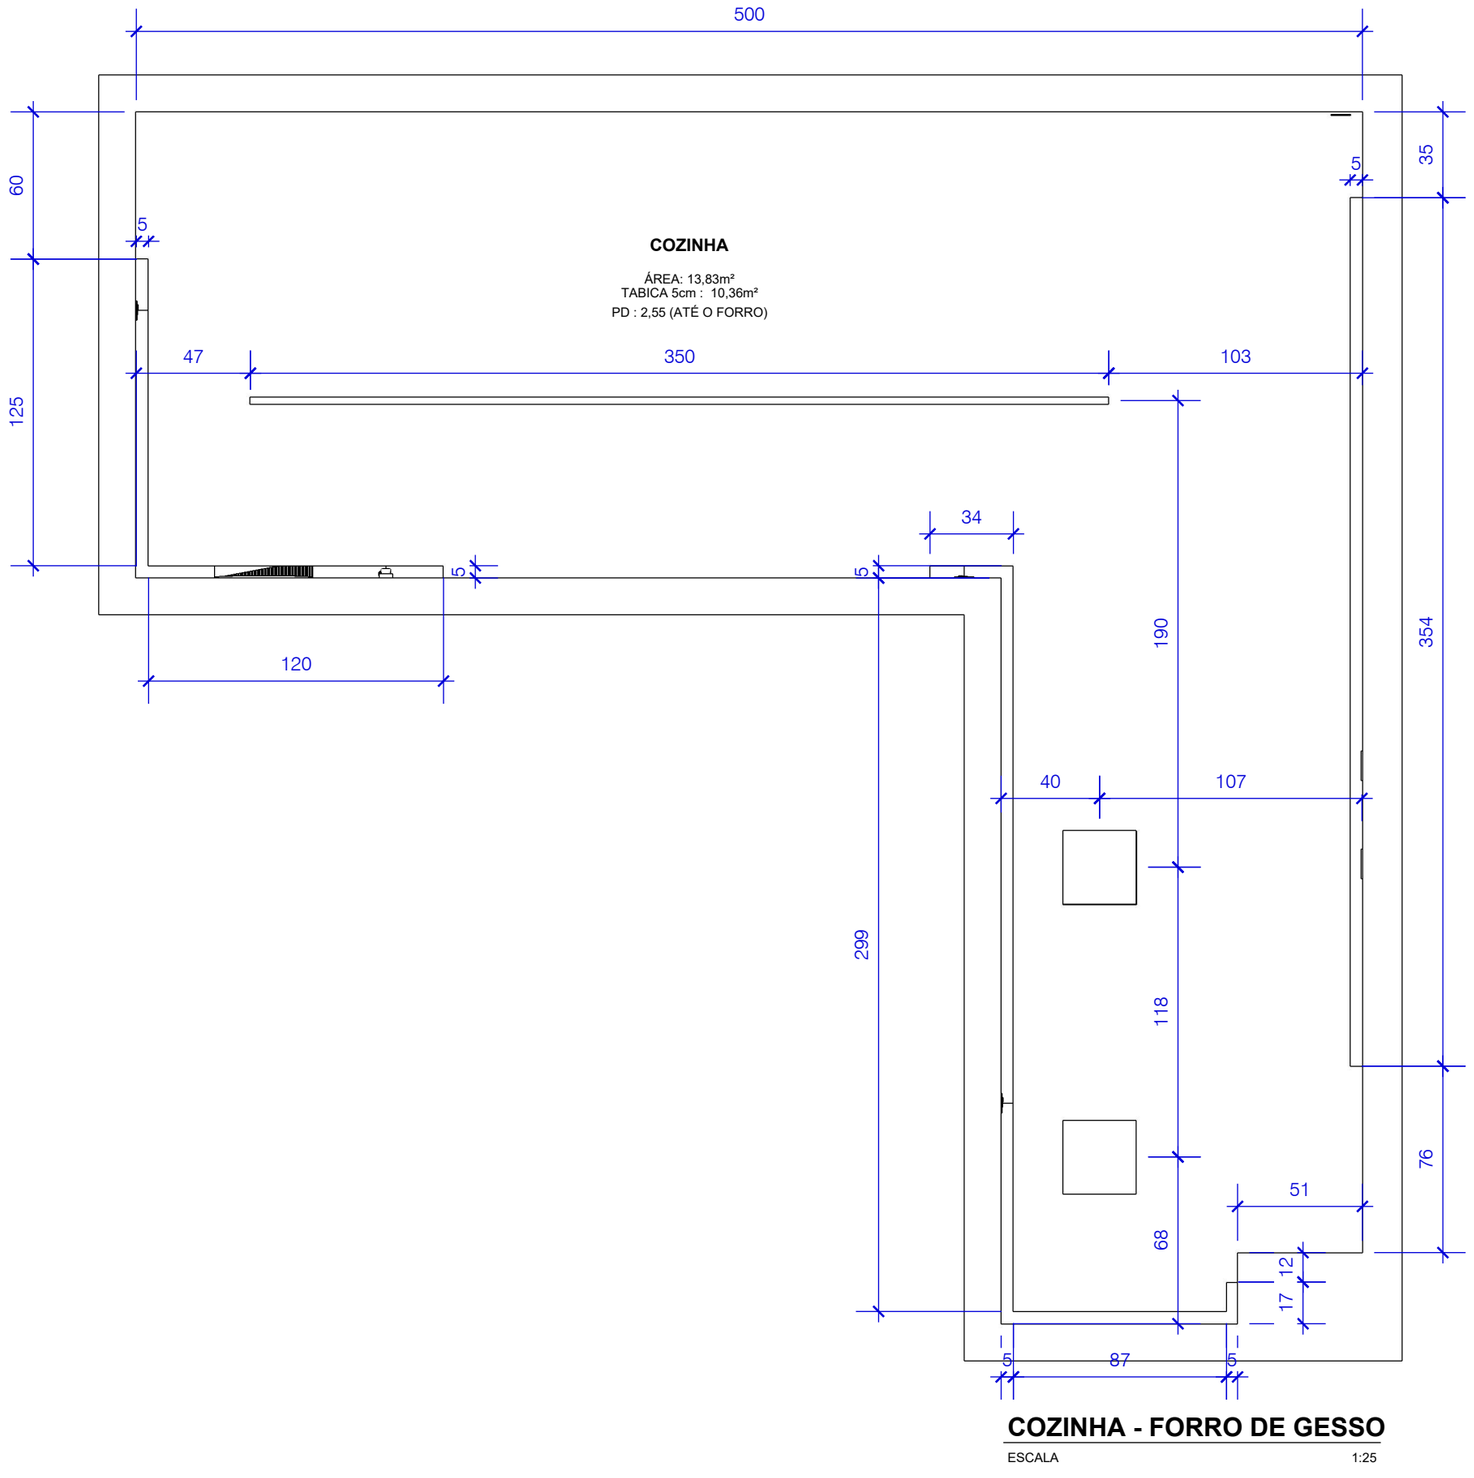


## COZINHA - FORRO DE GESSO

ESCALA 1:25

EMPÓRIO HASS ambientes planejados

contato@emporiohass.com.br
(61)99303-3151/98274-3709
emporiohass

# RESIDÊNCIA 314 NORTE

**CONTEÚDO**
Cozinha - Forro de Gesso

**TIPO**
Arquitetura de Interiores

**CLIENTE**
Débora Amarante Brancio Lopes Oliveira

**LOCALIZAÇÃO**
SQN 314 Bloco H Aptº 504
Asa Norte - DF

**ARQUIVO**
ARQ_INT_DEB_JAN2023

**AUTOR**
JMeuren - CAU Nº A487848

**REVISÃO**
01-02-2023

Geladeira Electrolux
multidoor Efficient
590 Litros

Fogão de Embutir existente


Bancad, rodabanca e
rodapé em granito preto
São Gabriel

Torre quente e despensa

Piso vinílico Belgotex
Castilla padrão Maple

Cuba Tramontina
Morgana

Armário em Duratex Cinza
Sagrado. Nicho em Duratex
Itapoã.

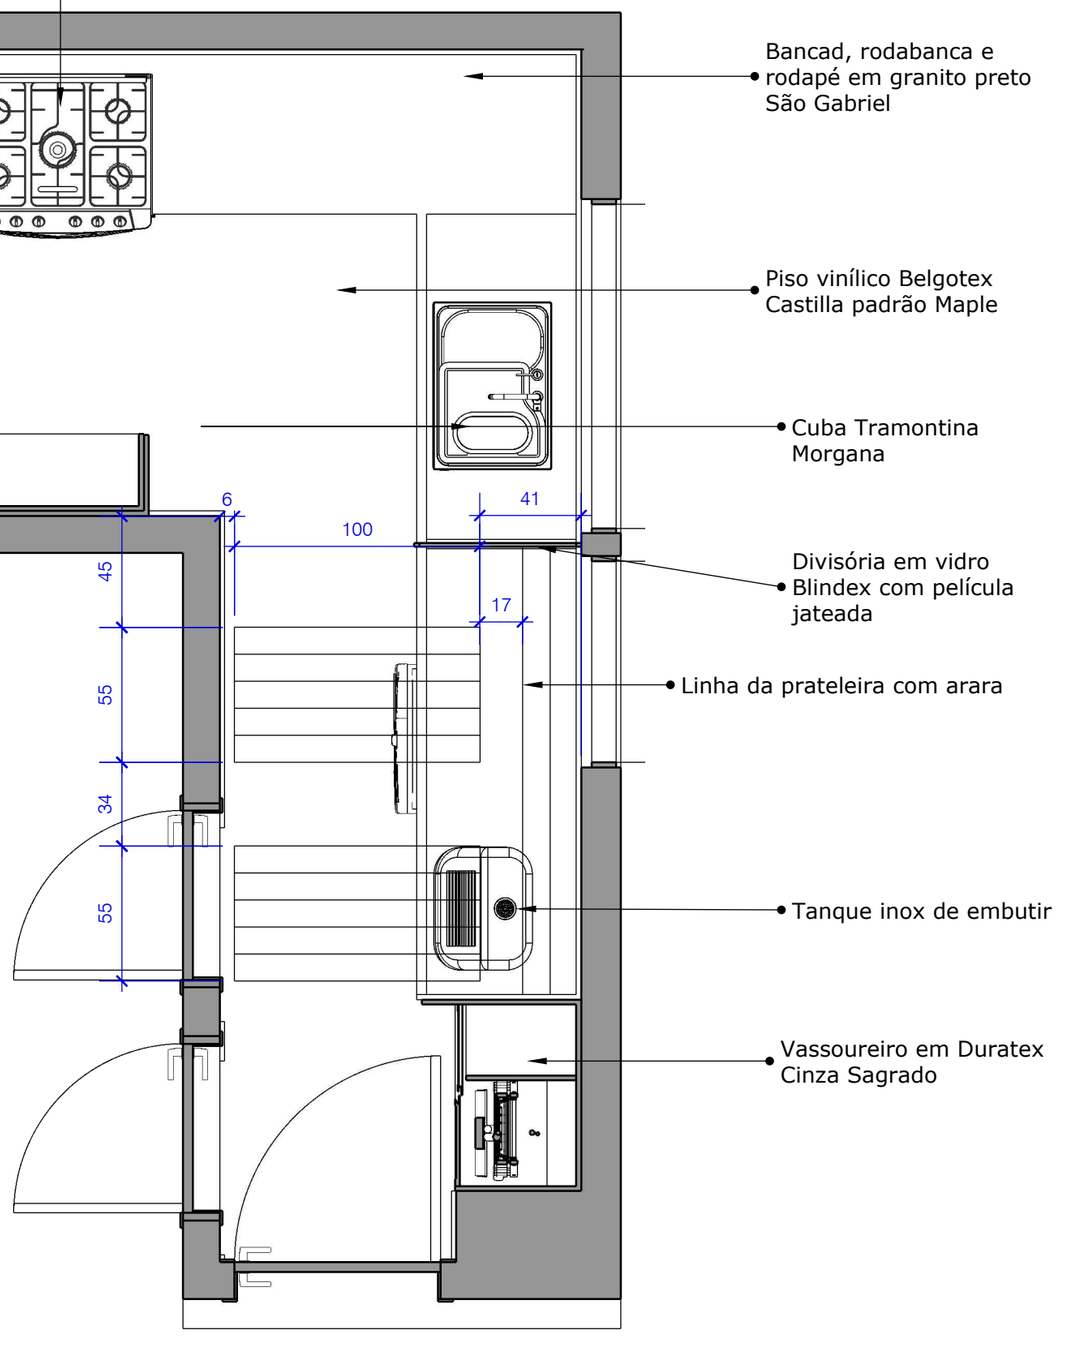


Divisória em vidro
Blindex com película
jateada

Linha da prateleira com arara

Tanque inox de embutir

Vassoureiro em Duratex
Cinza Sagrado

**COZINHA - LAYOUT**

ESCALA 1:25

EMPÓRIO HASS ambientes planejados

contato@emporiohass.com.br
(61)99303-3151/98274-3709
emporiohass

# RESIDÊNCIA 314 NORTE

**CONTEÚDO**
Cozinha - Layout

**TIPO**
Arquitetura de Interiores

**CLIENTE**
Débora Amarante Brancio
Lopes Oliveira

**LOCALIZAÇÃO**

SQN 314 Bloco H Aptº 504
Asa Norte - DF

**ARQUIVO**
ARQ_INT_DEB_JAN2023

**AUTOR**
JMeuren - CAU Nº A487848

**REVISÃO**
01-02-2023

Coifa slim retratil GE 80 cm ou
Fogatti compact new inox 75cm

Parede com revestimento eliane metro cinza 10x20. Paredes restantes receberão massa acrílica sobre revestimento existente e pintura Suvinil Papel Picado

Forro de Gesso

Armário superior em Duratex Cinza Sagrado.
Puxador sobra e fecho toque
Geladeira Electrolux Multidoor Efficient 590 L

Forno Microondas a escolher

Máscara em Duratex Itapuã

Forno Eletrico Electrolux OE8EH

Gaveteiro em Duratex Cinza Sagrado

Despensa com rodizios e corrediças (Ver Detalhe)

Rodapé em Granito Preto São Gabriel


Rodapé Sta Luzia no vão da Geladeira

Armário inferior em Duratex Cinza Sagrado. Nichos em Duratex Itapuã. Frentes com moldura e Puxador fecho unha

Fogão de embutir existente.
Nicho em Duratex Itapuã.
Gaveta na parte inferior

Vewrificar a possibilidade de se colocar uma gaveta na parte inferior do nicho, para panos,etc

Filtro soft everest existente. Embutir fiação e rabicho no armário superior. Sugestão: envelopar de cinza ou inox

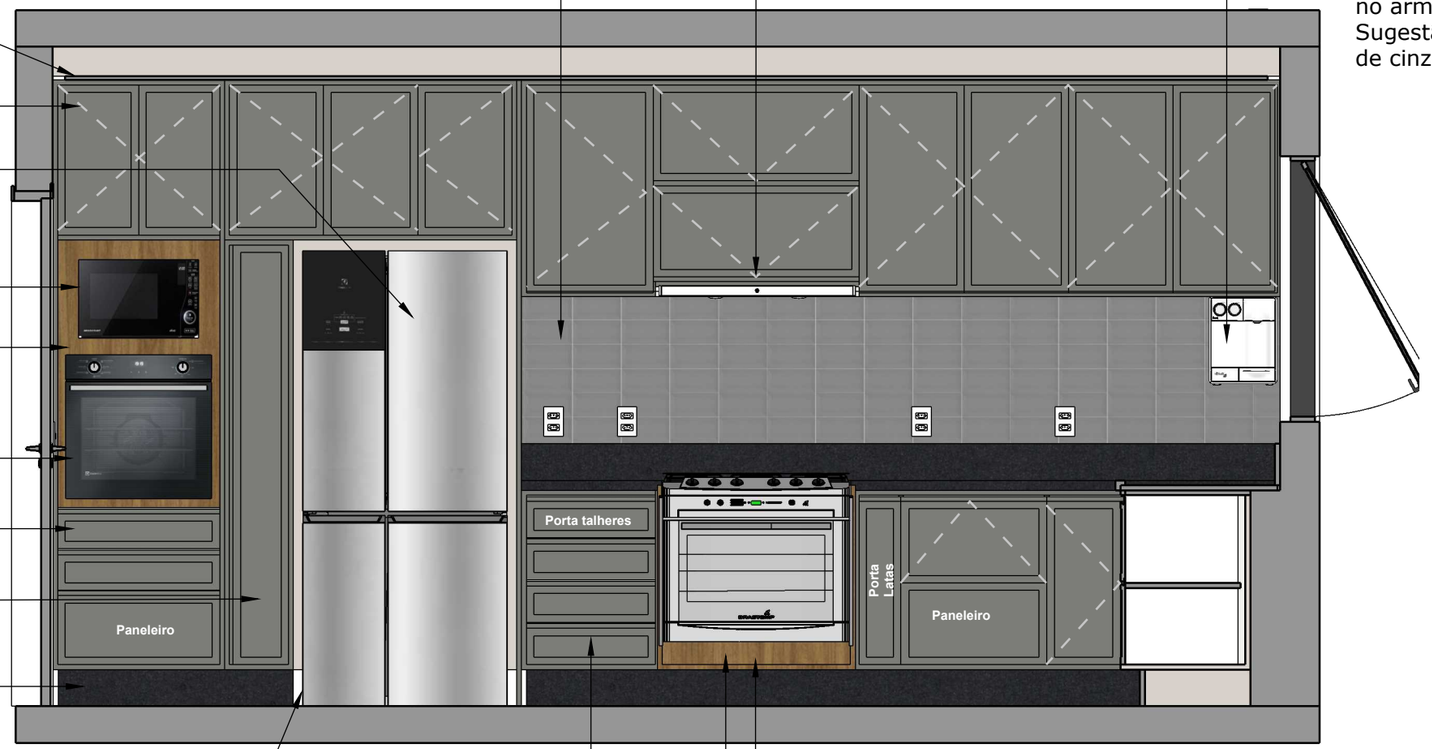


**COZINHA - VISTA A**

ESCALA 1:25

EMPÓRIO HASS ambientes planejados
contato@emporiohass.com.br
(61)99303-3151/98274-3709
emporiohass

# RESIDÊNCIA 314 NORTE

**CONTEÚDO**
Cozinha - Vista A

**TIPO**
Arquitetura de Interiores


**CLIENTE**
Débora Amarante Brancio Lopes Oliveira

**LOCALIZAÇÃO**
SQN 314 Bloco H Aptº 504
Asa Norte - DF

**ARQUIVO**
ARQ_INT_DEB_JAN2023

**AUTOR**
JMeuren - CAU Nº A487848

**REVISÃO**
01-02-2023

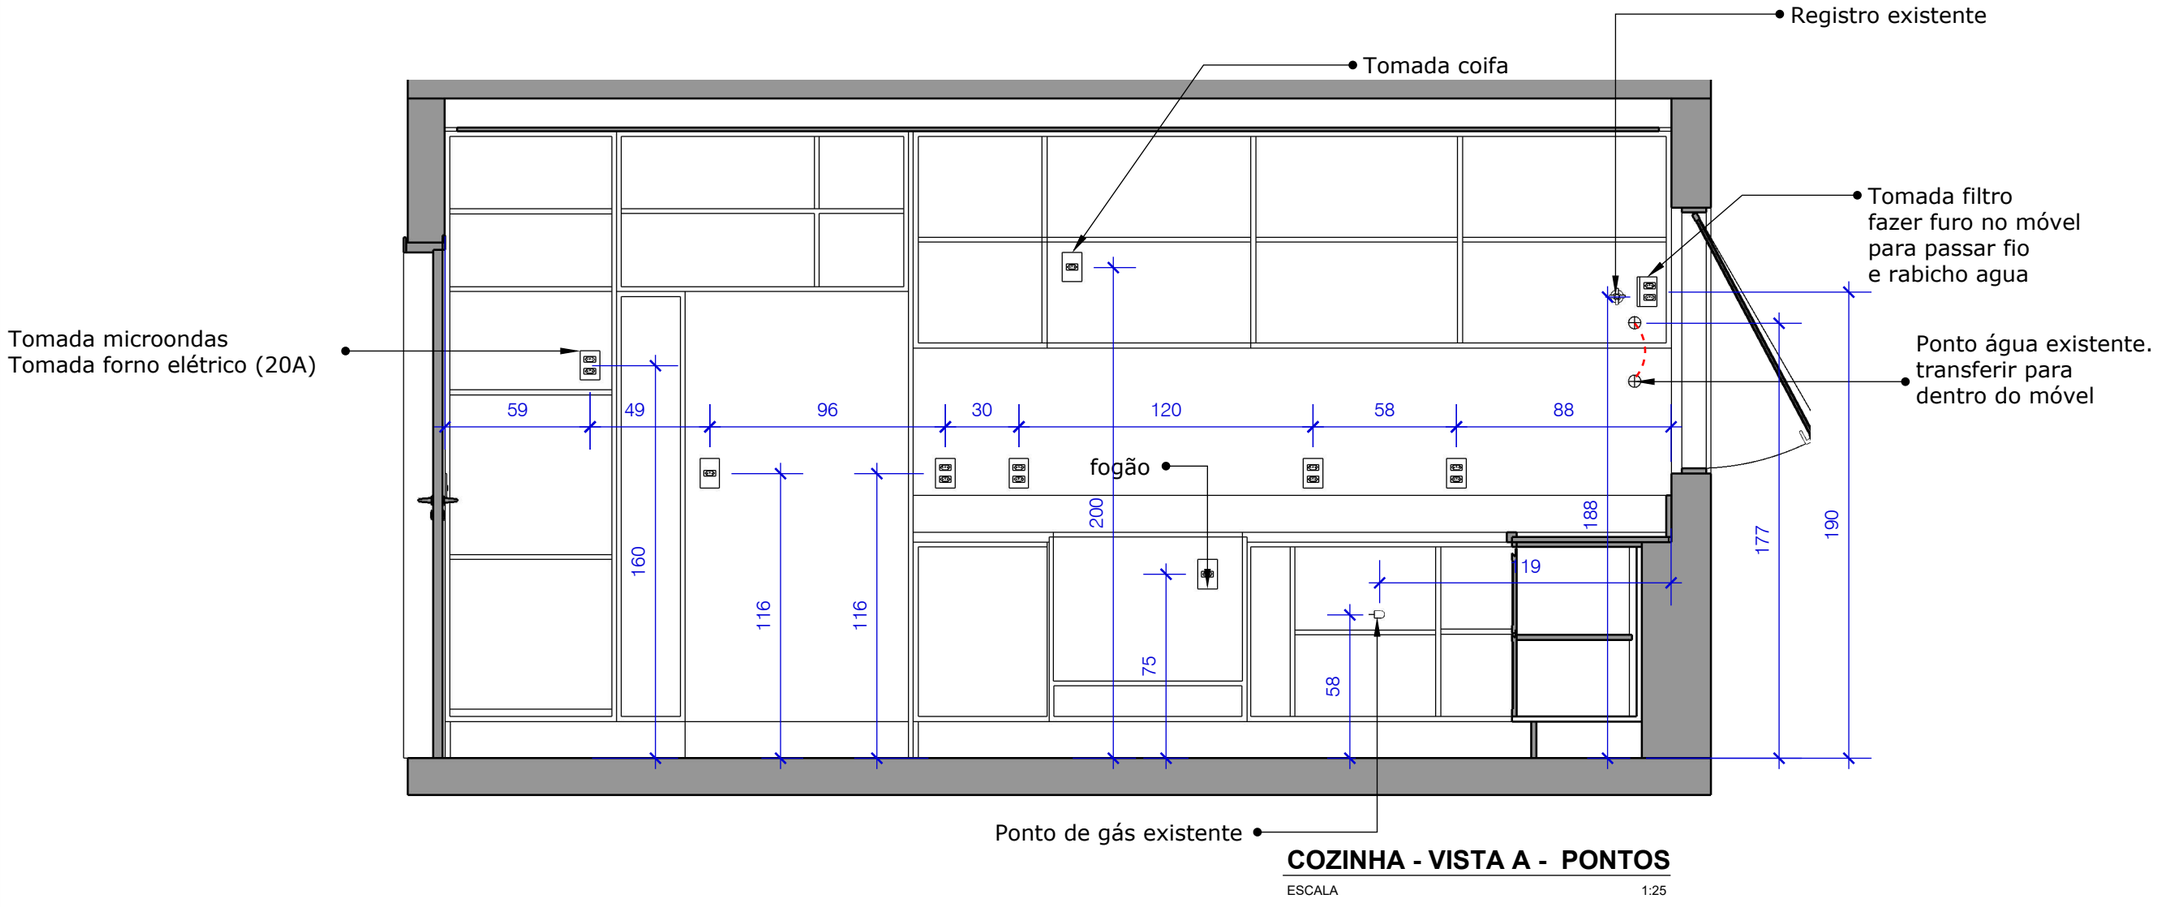


**COZINHA - VISTA A - PONTOS**

ESCALA 1:25

**OBS: -
-MARCENARIA ...VERIFICAR OS PONTOS DE GÁS , ÁGUA E ELETRICIDADE A FIM DE EVITAR RETRABALHO NOS MÓVEIS
- CONFERIR MEDIDAS NO LOCAL
- QUALQUER DÚVIDA CONFERIR COM AUTOR DO PROJETO

EMPÓRIO HASS ambientes planejados
contato@emporiohass.com.br
(61)99303-3151/98274-3709
emporiohass

# RESIDÊNCIA 314 NORTE

**CONTEÚDO**
Cozinha - Vista A - Pontos

**TIPO**
Arquitetura de Interiores


**CLIENTE**
Débora Amarante Brancio Lopes Oliveira

**LOCALIZAÇÃO**
SQN 314 Bloco H Aptº 504
Asa Norte - DF

**ARQUIVO**
ARQ_INT_DEB_JAN2023

**AUTOR**
JMeuren - CAU Nº A487848

**REVISÃO**
01-02-2023

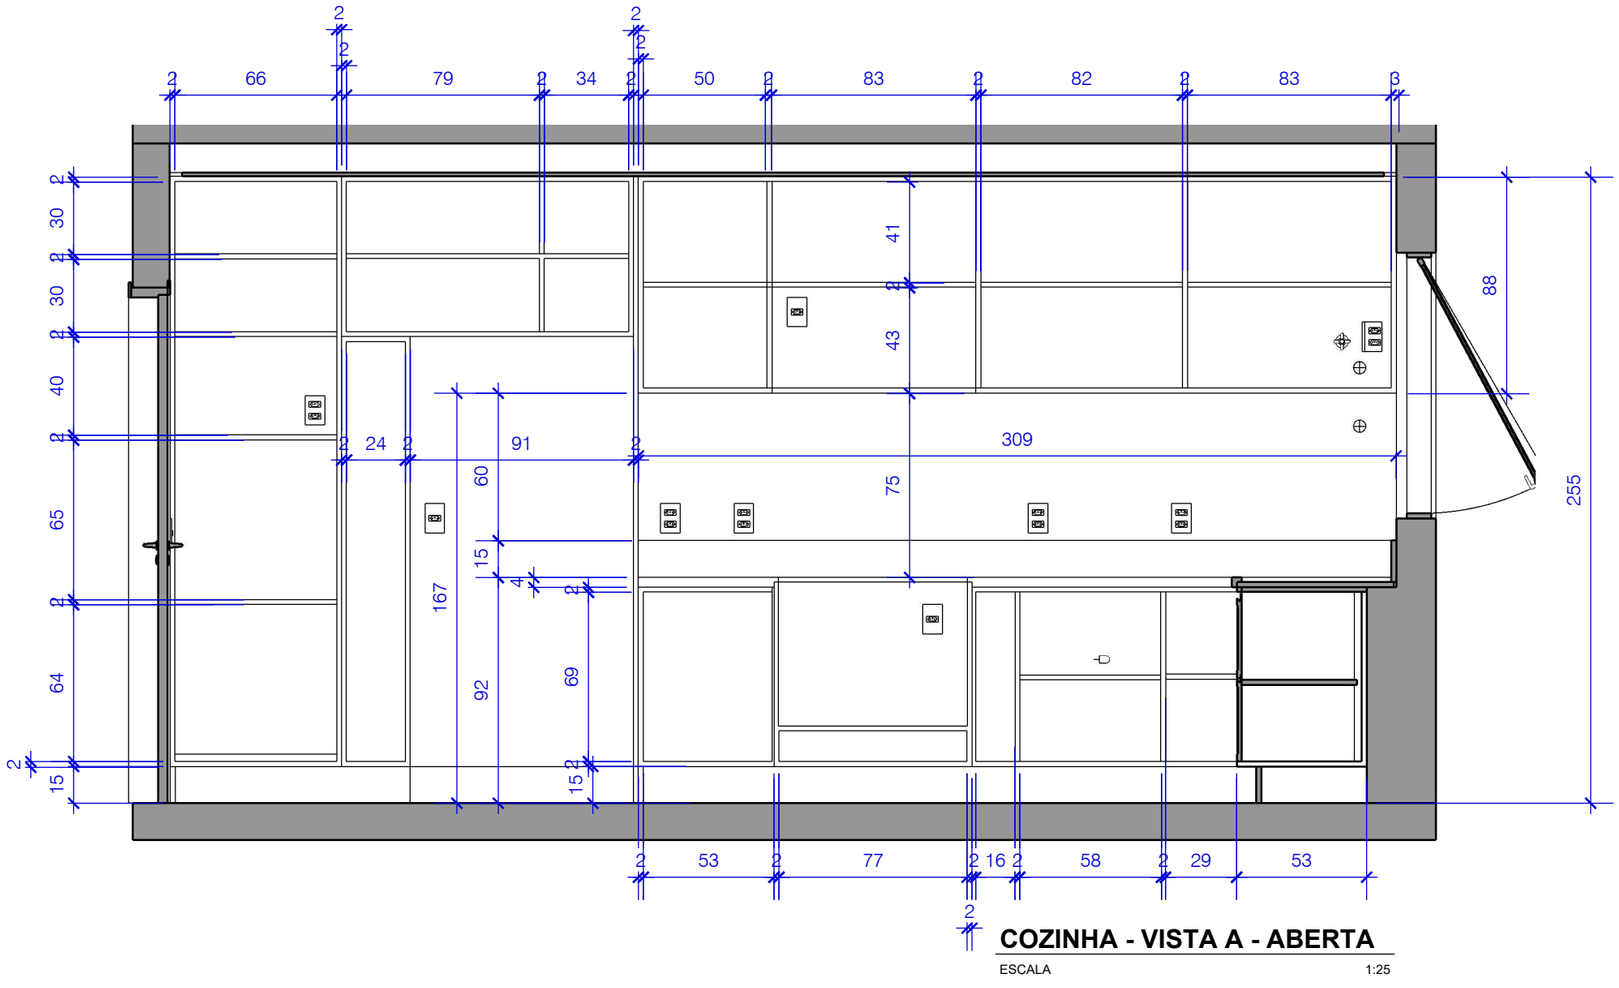


**OBS: -
-MARCENARIA ...VERIFICAR OS PONTOS DE GÁS , ÁGUA E ELETRICIDADE A FIM DE EVITAR RETRABALHO NOS MÓVEIS
- CONFERIR MEDIDAS NO LOCAL
- QUALQUER DÚVIDA CONFERIR COM AUTOR DO PROJETO

EMPÓRIO HASS ambientes planejados
contato@emporiohass.com.br
(61)99303-3151/98274-3709
emporiohass

# RESIDÊNCIA 314 NORTE

**CONTEÚDO**
Cozinha - Vista A - Aberta

**TIPO**
Arquitetura de Interiores


**CLIENTE**
Débora Amarante Brancio Lopes Oliveira

**LOCALIZAÇÃO**
SQN 314 Bloco H Aptº 504
Asa Norte - DF

**ARQUIVO**
ARQ_INT_DEB_JAN2023

**AUTOR**
JMeuren - CAU Nº A487848

**REVISÃO**
01-02-2023

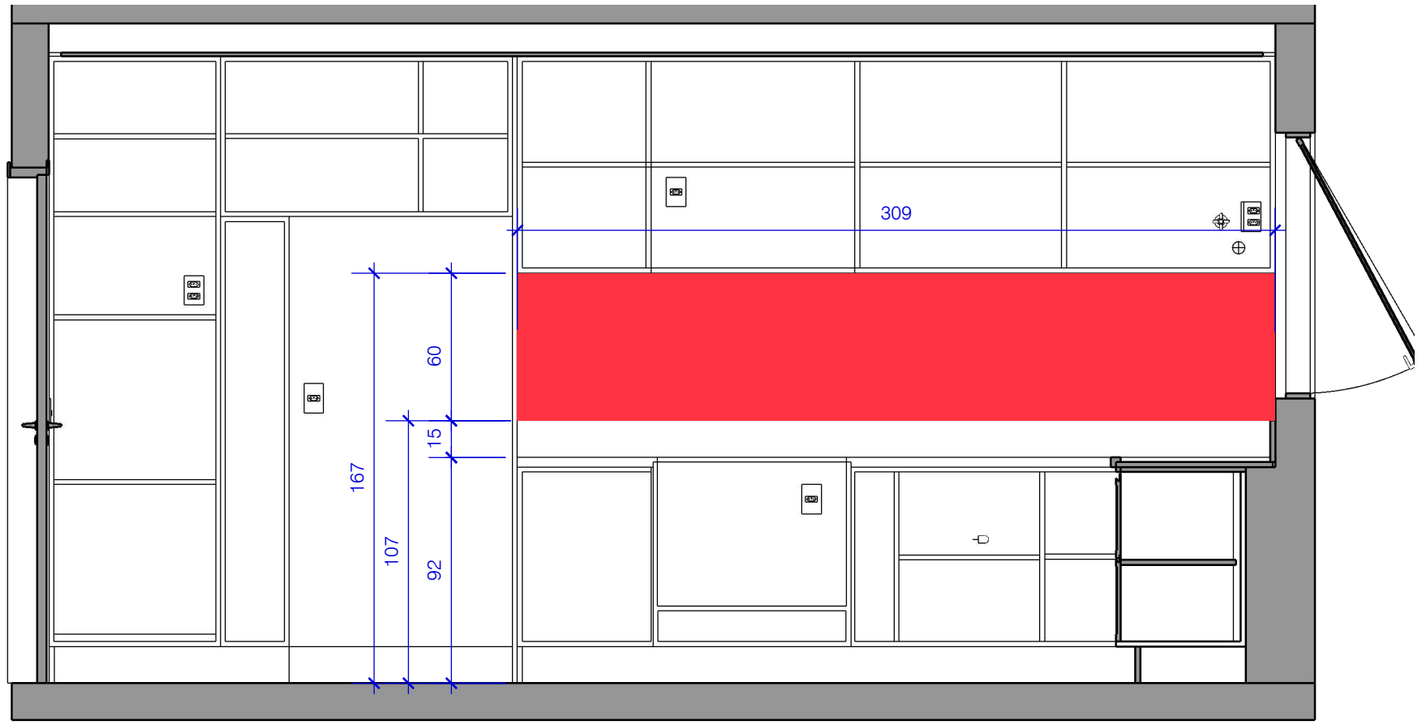


## COZINHA - VISTA A - RETIRAR AZULEJOS

ESCALA 1:25

**OBS: -
-MARCENARIA ...VERIFICAR OS PONTOS DE GÁS , ÁGUA E ELETRICIDADE A FIM DE EVITAR RETRABALHO NOS MÓVEIS
- CONFERIR MEDIDAS NO LOCAL
- QUALQUER DÚVIDA CONFERIR COM AUTOR DO PROJETO

EMPÓRIO HASS ambientes planejados
contato@emporiohass.com.br
(61)99303-3151/98274-3709
emporiohass

# RESIDÊNCIA 314 NORTE

**CONTEÚDO**
Cozinha - Vista A - Retirada de Azulejos

**TIPO**
Arquitetura de Interiores


**CLIENTE**
Débora Amarante Brancio Lopes Oliveira

**LOCALIZAÇÃO**
SQN 314 Bloco H Aptº 504
Asa Norte - DF

**ARQUIVO**
ARQ_INT_DEB_JAN2023

**AUTOR**
JMeuren - CAU Nº A487848

**REVISÃO**
01-02-2023

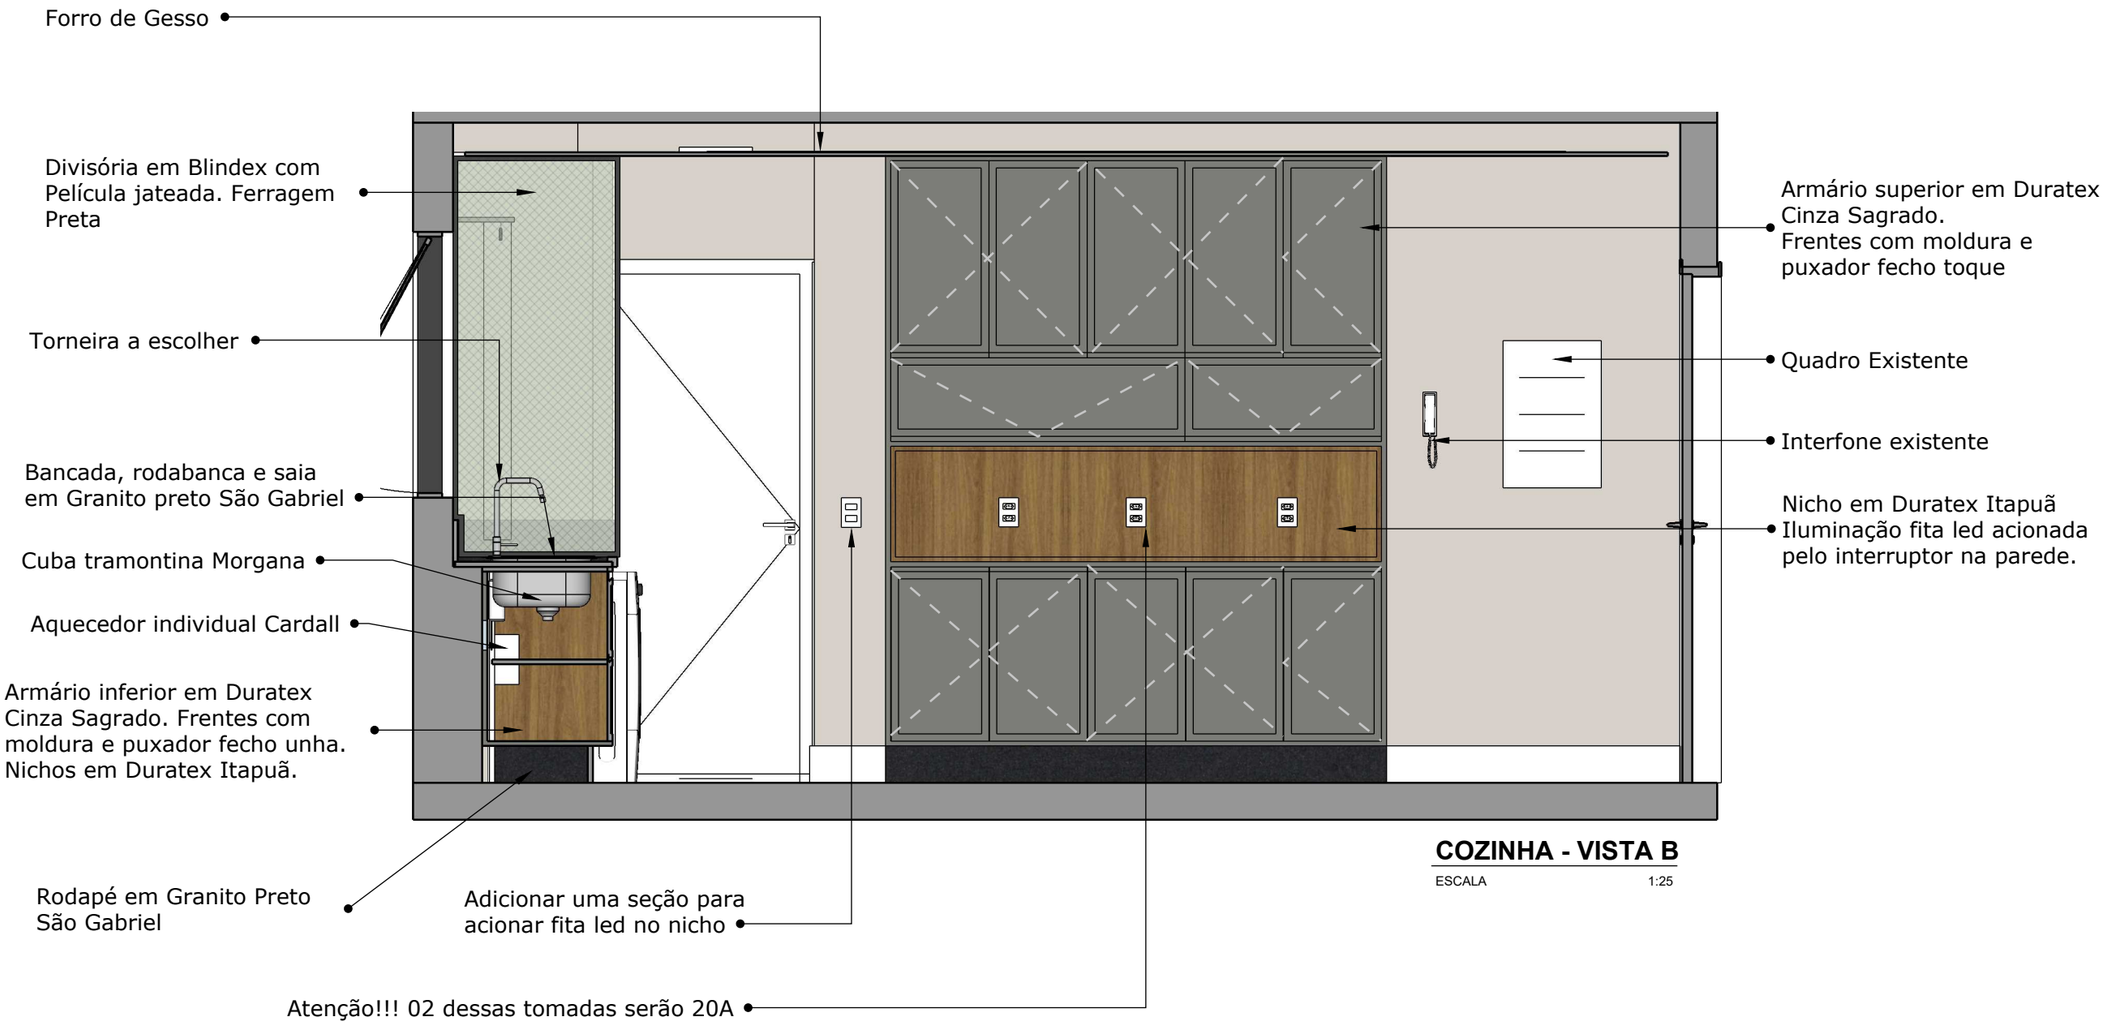


**COZINHA - VISTA B**

ESCALA 1:25

EMPÓRIO HASS ambientes planejados

contato@emporiohass.com.br

(61)99303-3151/98274-3709

emporiohass

# RESIDÊNCIA 314 NORTE

**CONTEÚDO**
Cozinha -Vista B

**TIPO**
Arquitetura de Interiores

**CLIENTE**
Débora Amarante Brancio Lopes Oliveira


**LOCALIZAÇÃO**

SQN 314 Bloco H Aptº 504
Asa Norte - DF

**ARQUIVO**
ARQ_INT_DEB_JAN2023

**AUTOR**
JMeuren - CAU Nº A487848

**REVISÃO**
01-02-2023

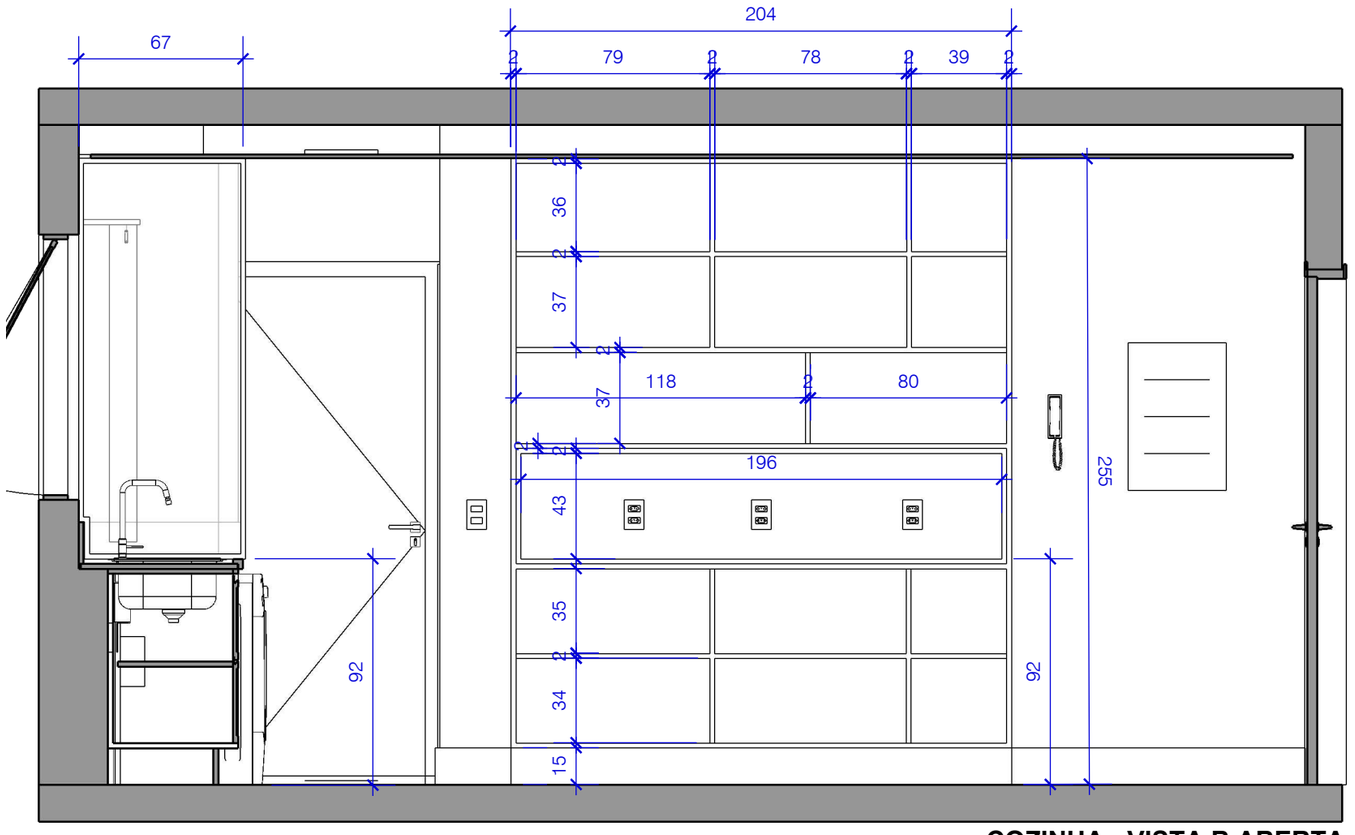


**COZINHA - VISTA B ABERTA**

ESCALA 1:25

EMPÓRIO HASS ambientes planejados

contato@emporiohass.com.br
(61)99303-3151/98274-3709
emporiohass

# RESIDÊNCIA 314 NORTE

**CONTEÚDO**
Cozinha - Vista B - Aberta

**TIPO**
Arquitetura de Interiores

**CLIENTE**
Débora Amarante Brancio Lopes Oliveira


**LOCALIZAÇÃO**

SQN 314 Bloco H Aptº 504
Asa Norte - DF

**ARQUIVO**
ARQ_INT_DEB_JAN2023

**AUTOR**
JMeuren - CAU Nº A487848

**REVISÃO**
01-02-2023

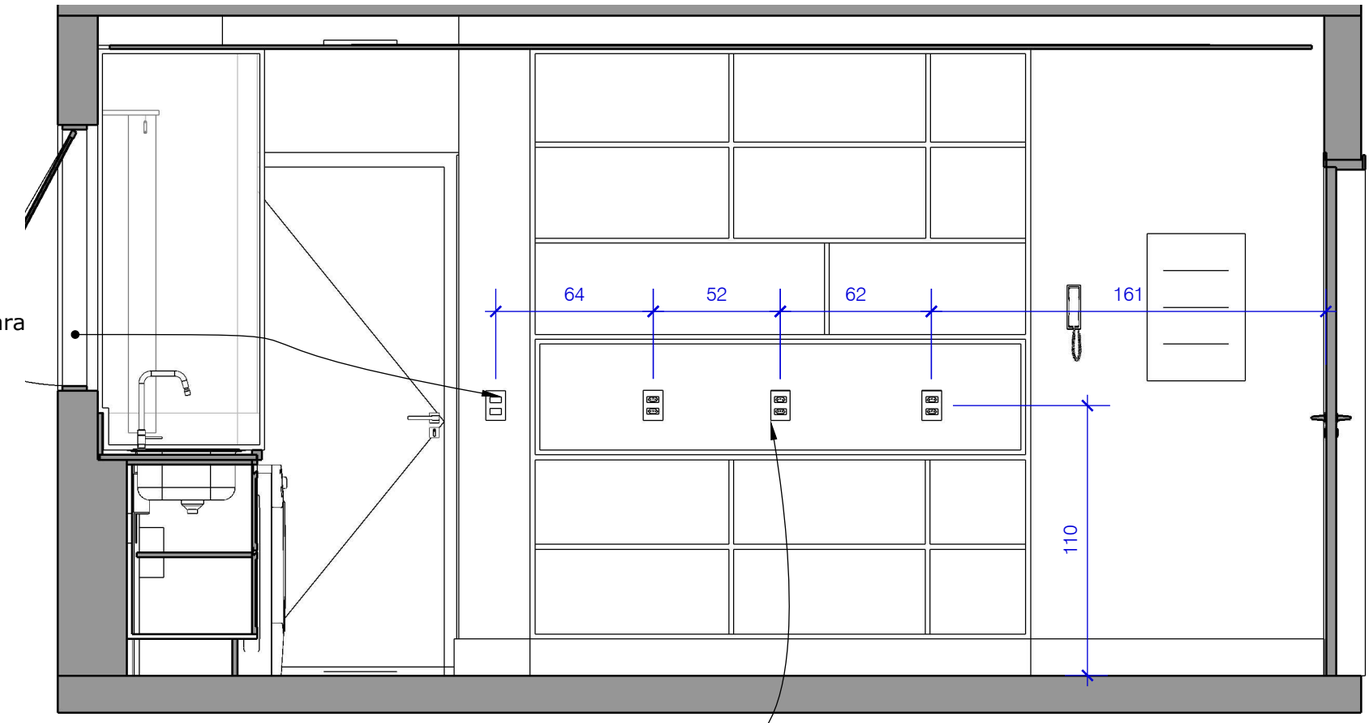


inserir + 1 seção para acionar fita led

Estas tomadas serão de 20A

**COZINHA - VISTA B - PONTOS**

ESCALA 1:25

EMPÓRIO HASS ambientes planejados

contato@emporiohass.com.br
(61)99303-3151/98274-3709
emporiohass

# RESIDÊNCIA 314 NORTE

**CONTEÚDO**
Cozinha - Vista B - Pontos

**TIPO**
Arquitetura de Interiores

**CLIENTE**
Débora Amarante Brancio Lopes Oliveira


**LOCALIZAÇÃO**

SQN 314 Bloco H Aptº 504
Asa Norte - DF

**ARQUIVO**
ARQ_INT_DEB_JAN2023

**AUTOR**
JMeuren - CAU Nº A487848

**REVISÃO**
01-02-2023

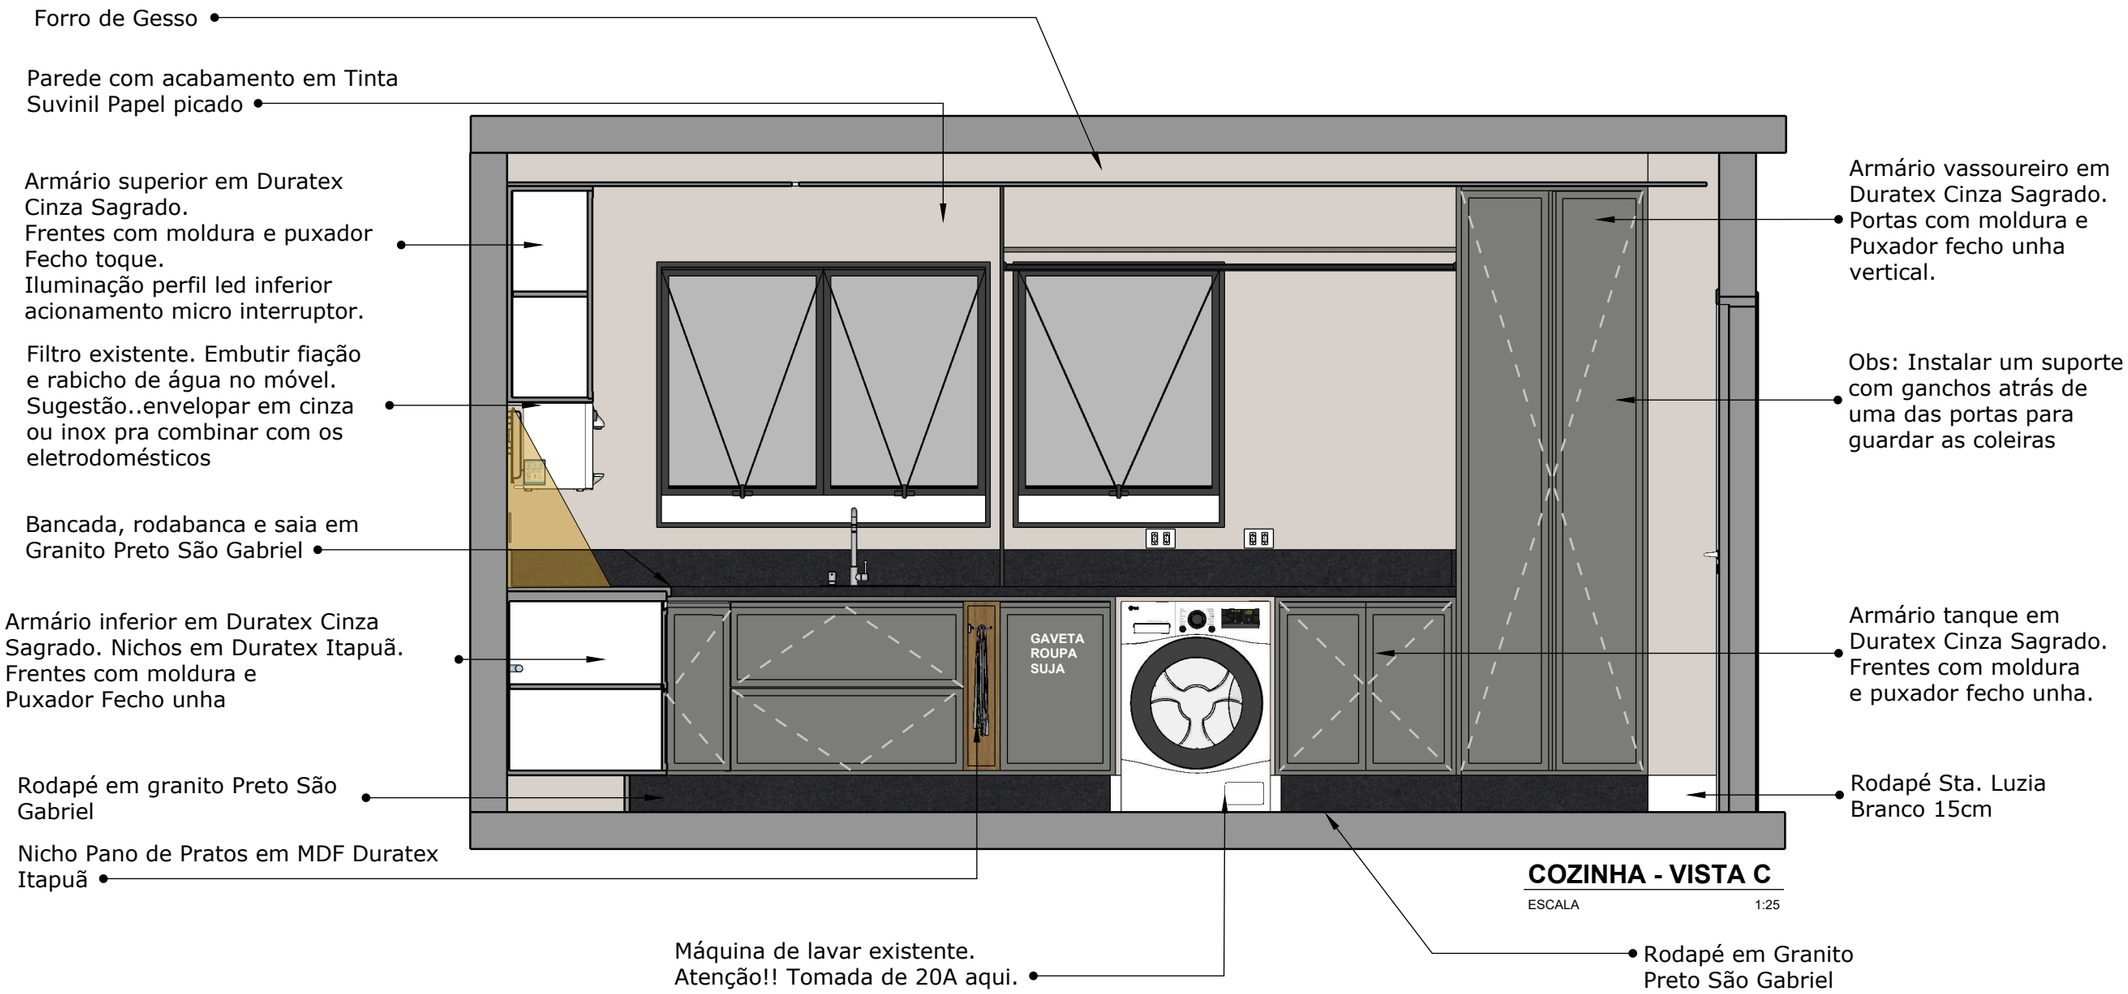


**COZINHA - VISTA C**

ESCALA 1:25

EMPÓRIO HASS ambientes planejados

contato@emporiohass.com.br

(61)99303-3151/98274-3709

emporiohass

# RESIDÊNCIA 314 NORTE

**CONTEÚDO**
Cozinha - Vista C

**TIPO**
Arquitetura de Interiores

**CLIENTE**
Débora Amarante Brancio Lopes Oliveira


**LOCALIZAÇÃO**

SQN 314 Bloco H Aptº 504
Asa Norte - DF

**ARQUIVO**
ARQ_INT_DEB_JAN2023

**AUTOR**
JMeuren - CAU Nº A487848

**REVISÃO**
01-02-2023

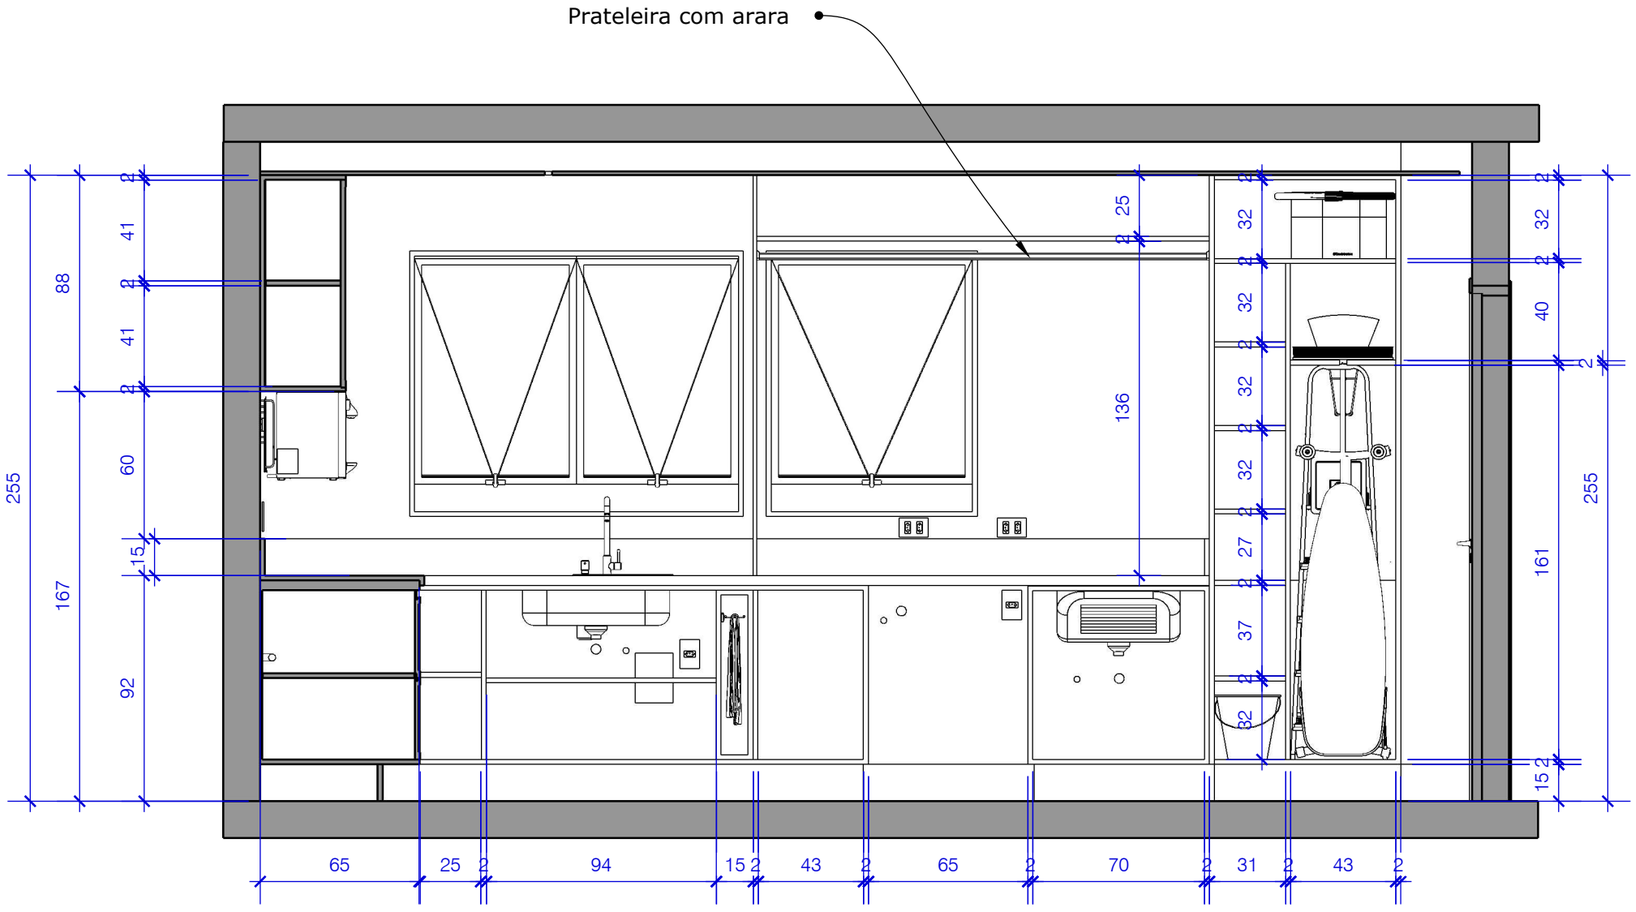


## COZINHA - VISTA C - ABERTA

ESCALA 1:25

EMPÓRIO HASS ambientes planejados

contato@emporiohass.com.br

(61)99303-3151/98274-3709

emporiohass

# RESIDÊNCIA 314 NORTE

**CONTEÚDO**
Cozinha - Vista C
Aberta

**TIPO**
Arquitetura de Interiores

**CLIENTE**
Débora Amarante Brancio
Lopes Oliveira


**LOCALIZAÇÃO**

SQN 314 Bloco H Aptº 504
Asa Norte - DF

**ARQUIVO**
ARQ_INT_DEB_JAN2023

**AUTOR**
JMeuren - CAU Nº A487848

**REVISÃO**
01-02-2023

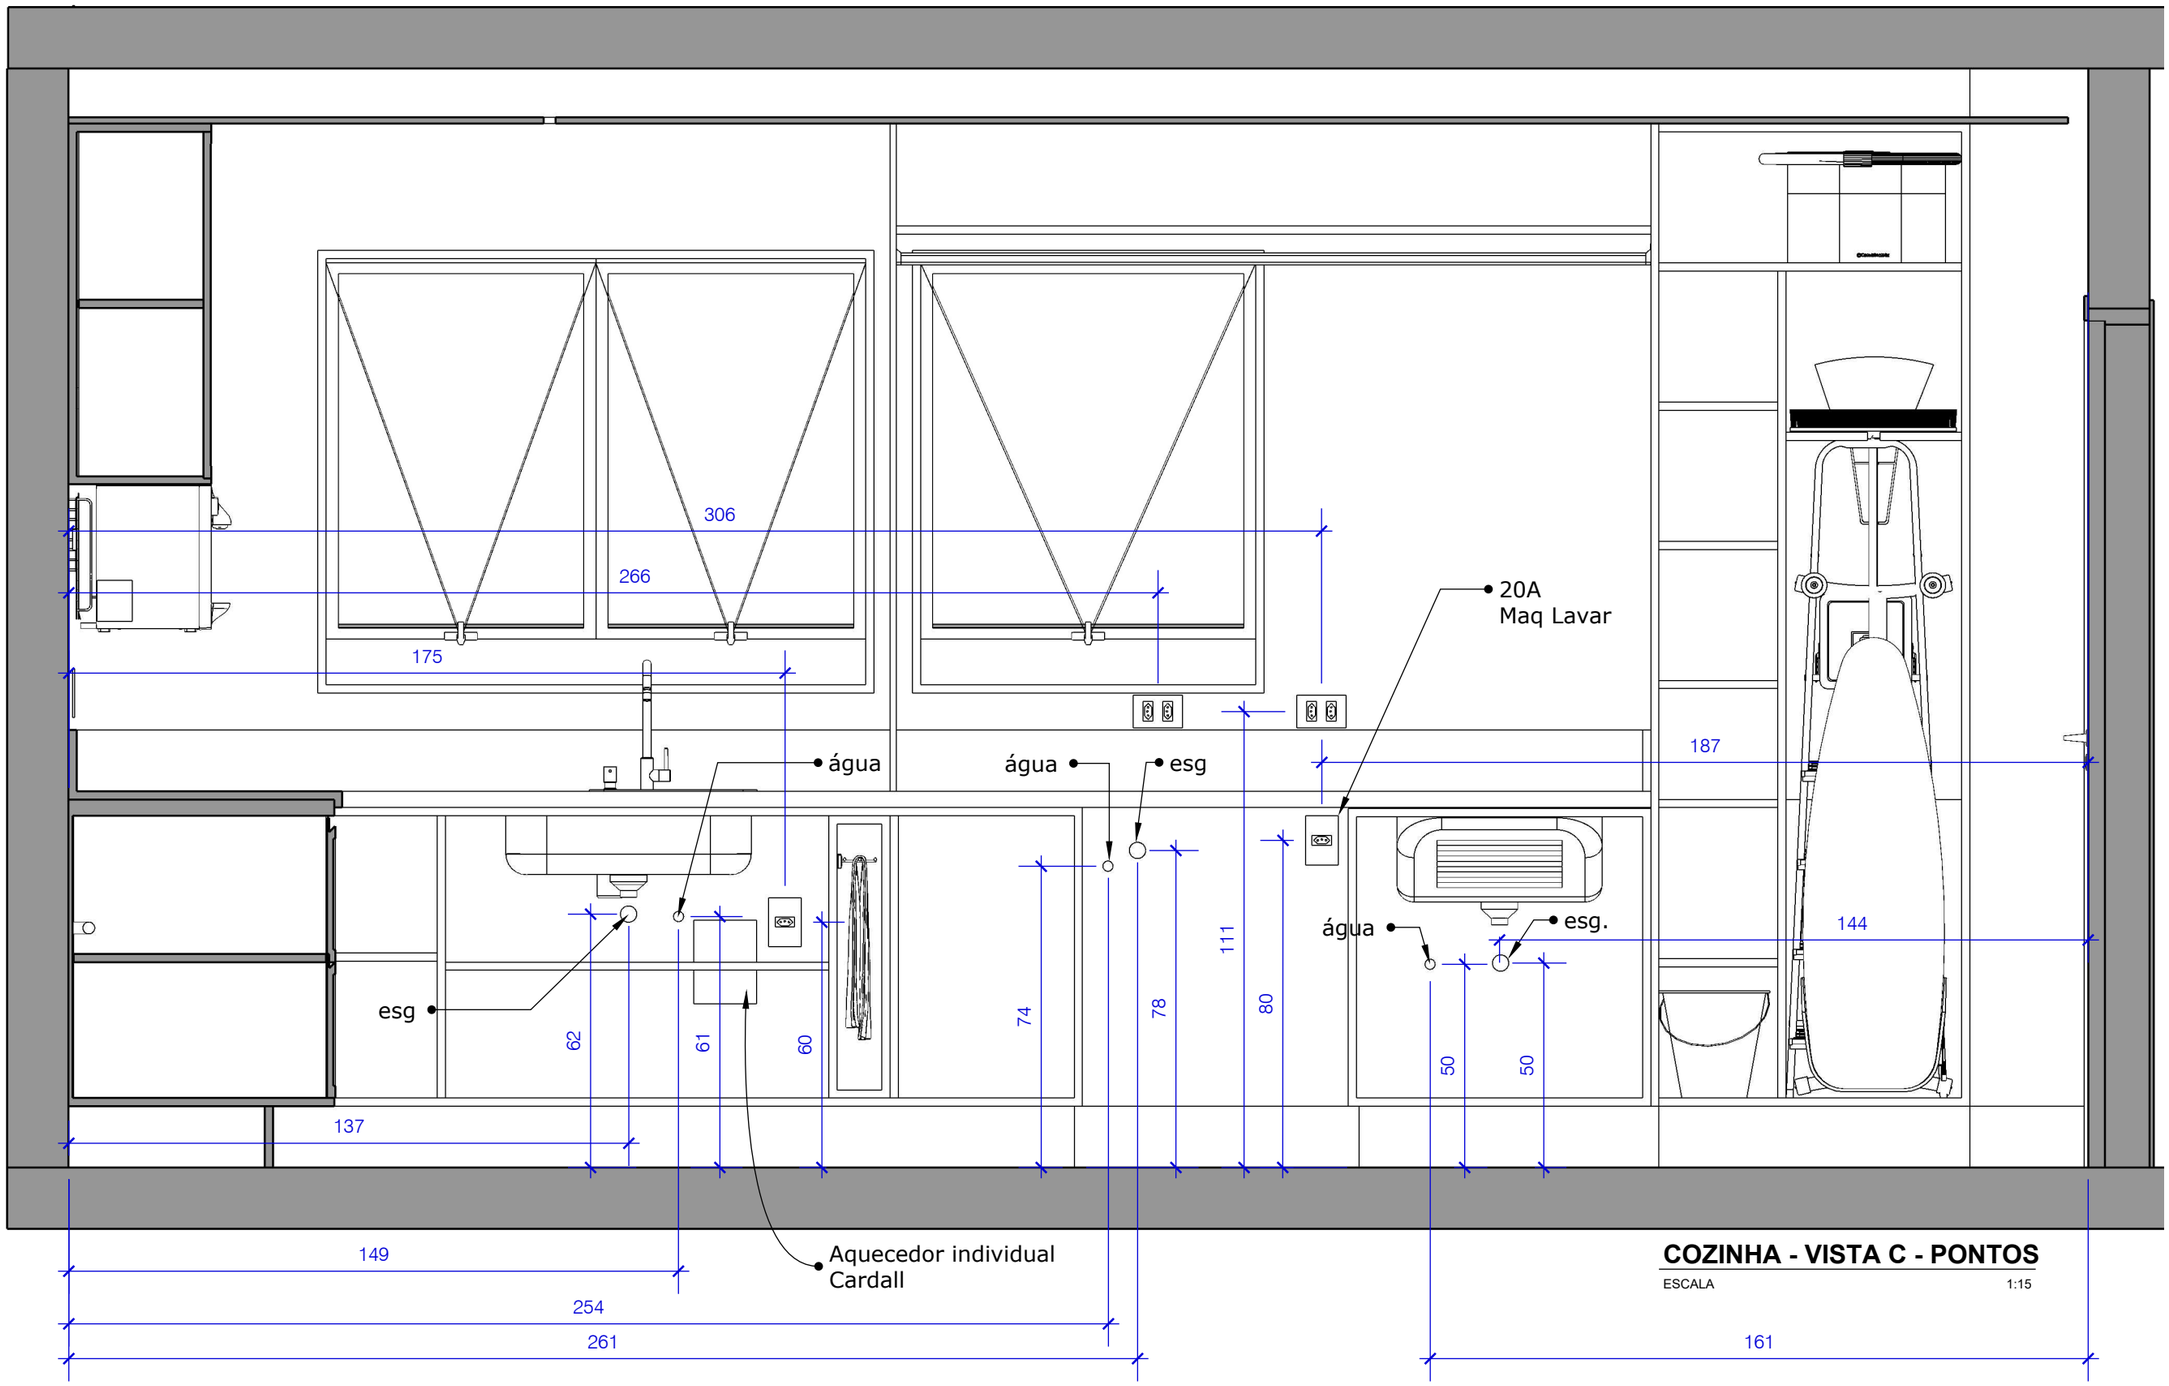


**COZINHA - VISTA C - PONTOS**

ESCALA 1:15

EMPÓRIO HASS ambientes planejados

contato@emporiohass.com.br

(61)99303-3151/98274-3709

emporiohass

# RESIDÊNCIA 314 NORTE

**CONTEÚDO**
Cozinha - Vista C
Pontos

**TIPO**
Arquitetura de Interiores

**CLIENTE**
Débora Amarante Brancio Lopes Oliveira


**LOCALIZAÇÃO**

SQN 314 Bloco H Aptº 504
Asa Norte - DF

**ARQUIVO**
ARQ_INT_DEB_JAN2023

**AUTOR**
JMeuren - CAU Nº A487848


**REVISÃO**
01-02-2023

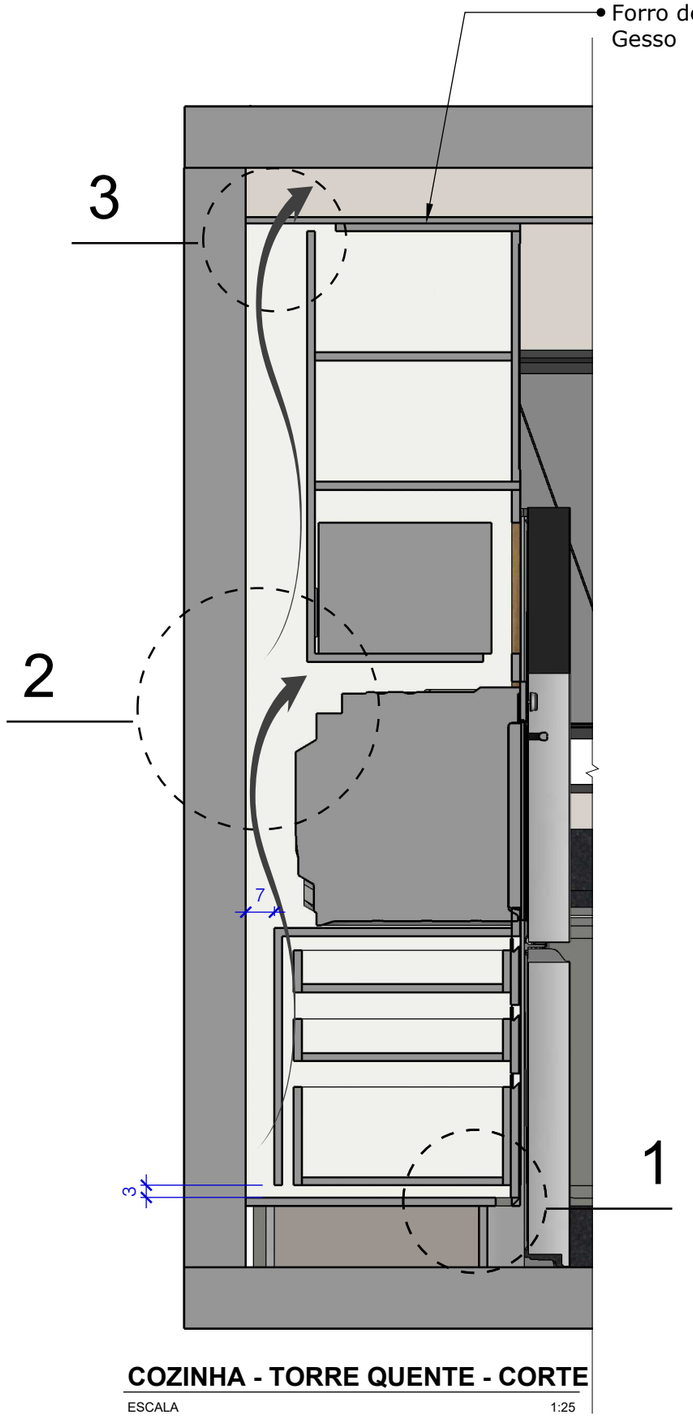


Forro de Gesso

**COZINHA - TORRE QUENTE - CORTE**

ESCALA 1:25

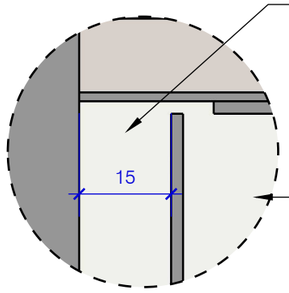



Saída de ar Quente

Armário acima microondas

**DETALHE 03**

ESCALA 1:10

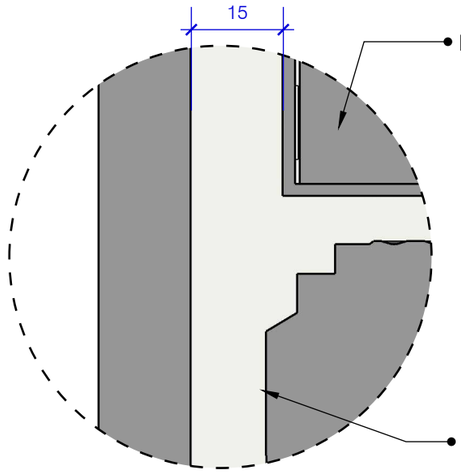



Microondas

Forno elétrico

**DETALHE 02**

ESCALA 1:10

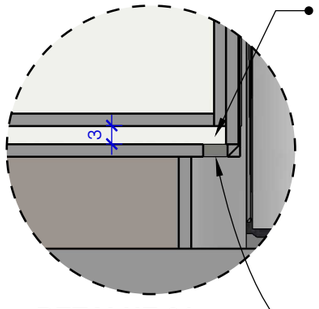



Ar corre por baixo do gaveteiro

Entrada de ar frio

**DETALHE 01**


ESCALA 1:10

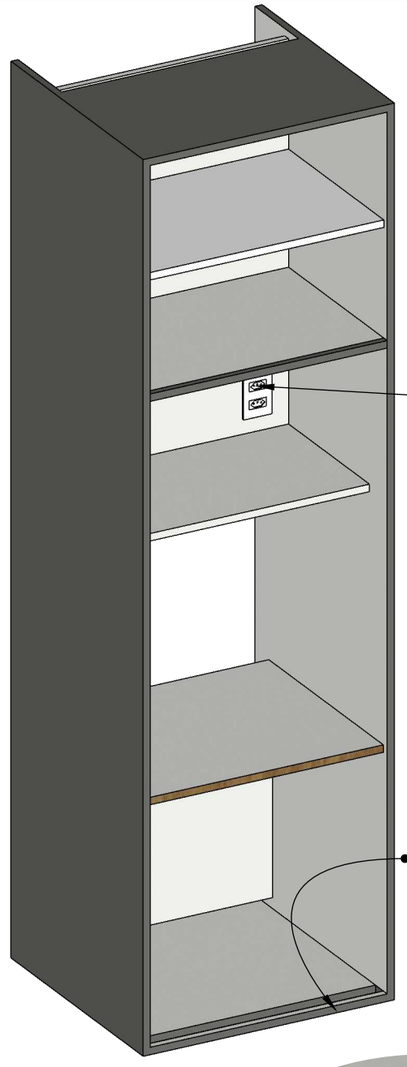

Tomadas na região do microondas, longe do calor do forno

recorte para entrada de ar

Rasgo de 66x4cm para entrada de ar frio

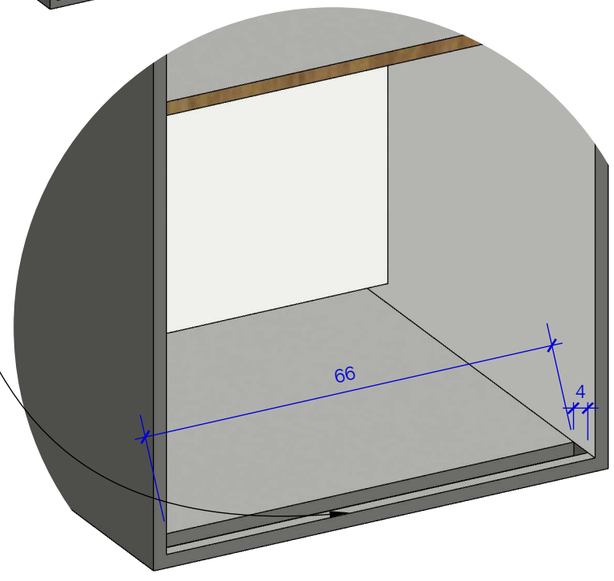


EMPÓRIO HASS ambientes planejados

contato@emporiohass.com.br
(61)99303-3151/98274-3709
emporiohass

# RESIDÊNCIA 314 NORTE

**CONTEÚDO**
Cozinha - Cortes e Isos

**TIPO**
Arquitetura de Interiores


**CLIENTE**
Débora Amarante Brancio Lopes Oliveira

**LOCALIZAÇÃO**
SQN 314 Bloco H Aptº 504
Asa Norte - DF

**ARQUIVO**
ARQ_INT_DEB_JAN2023


**AUTOR**
JMeuren - CAU Nº A487848

**REVISÃO**
01-02-2023

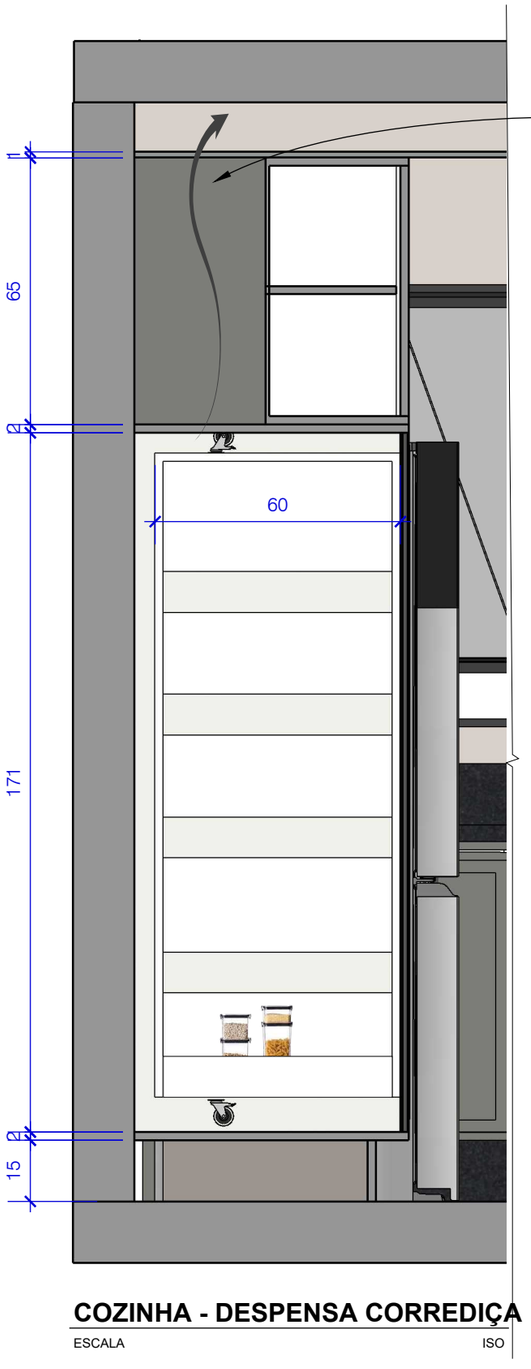


**COZINHA - DESPENSA CORREDIÇA**

ESCALA ISO

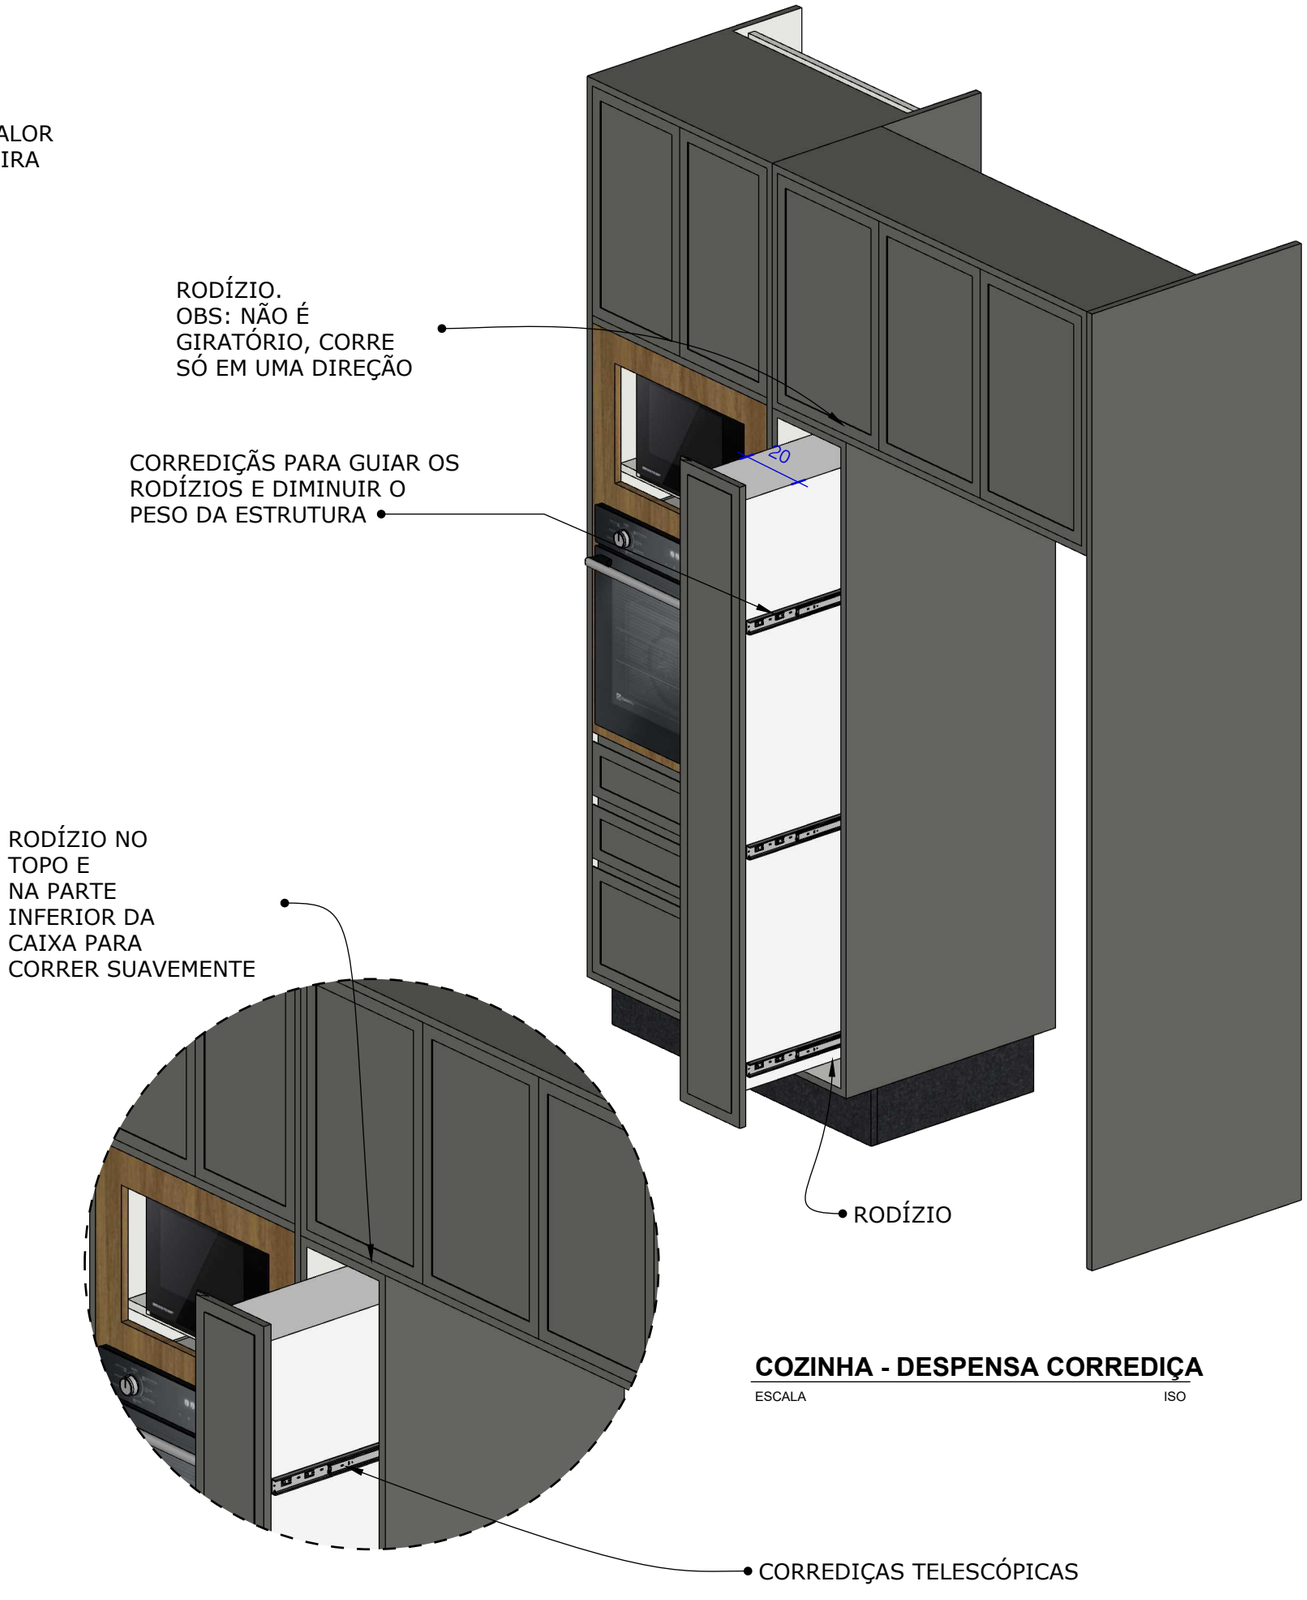


**COZINHA - DESPENSA CORREDIÇA**

ESCALA ISO

EMPÓRIO HASS ambientes planejados

contato@emporiohass.com.br

(61)99303-3151/98274-3709

emporiohass

# RESIDÊNCIA 314 NORTE

**CONTEÚDO**
Cozinha - Despensa - iso

**TIPO**
Arquitetura de Interiores

**CLIENTE**
Débora Amarante Brancio Lopes Oliveira


**LOCALIZAÇÃO**

SQN 314 Bloco H Aptº 504
Asa Norte - DF

**ARQUIVO**
ARQ_INT_DEB_JAN2023

**AUTOR**
JMeuren - CAU Nº A487848

**REVISÃO**
01-02-2023

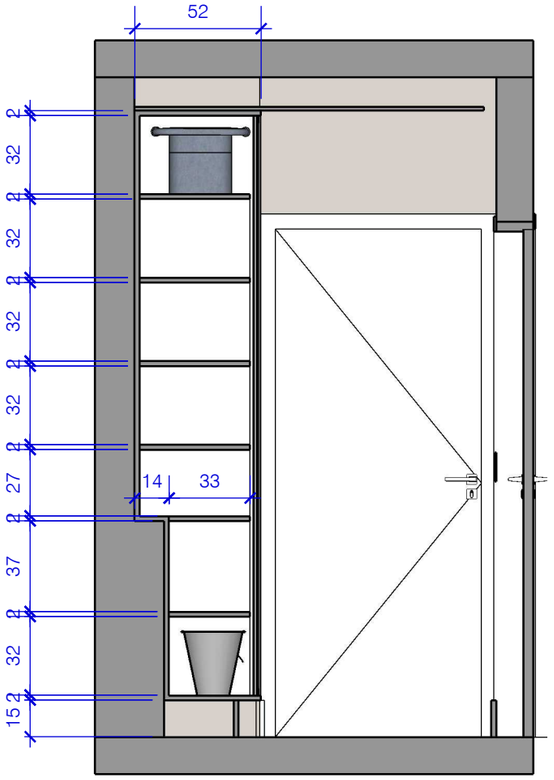



**COZINHA - CORTE VASSOUREIRO**

ESCALA 1:25

Essa lateral é mais longa para nivelar com a profundidade da bancada



OBS: Colocar atrás de uma das portas esse suporte para que se pendure as coleiras

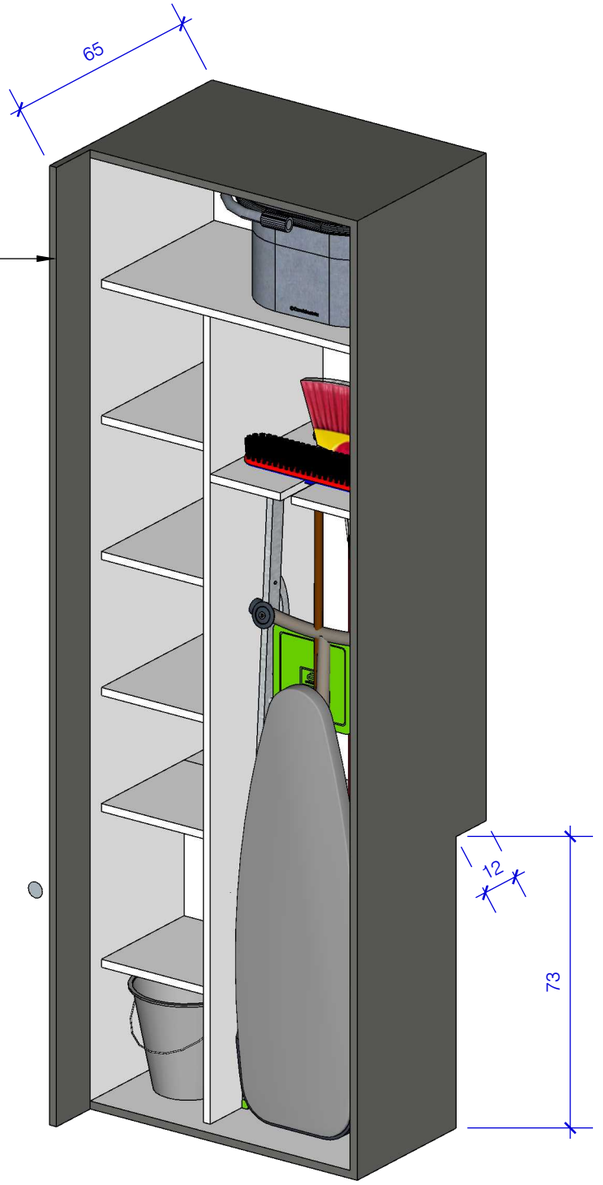


**COZINHA - VASSOUREIRO**

ESCALA ISO

EMPÓRIO HASS ambientes planejados

contato@emporiohass.com.br

(61)99303-3151/98274-3709

emporiohass

# RESIDÊNCIA 314 NORTE

**CONTEÚDO**
Área - Vassoureiro

**TIPO**
Arquitetura de Interiores

**CLIENTE**
Débora Amarante Brancio Lopes Oliveira


**LOCALIZAÇÃO**

SQN 314 Bloco H Aptº 504
Asa Norte - DF

**ARQUIVO**
ARQ_INT_DEB_JAN2023

**AUTOR**
JMeuren - CAU Nº A487848

**REVISÃO**
01-02-2023

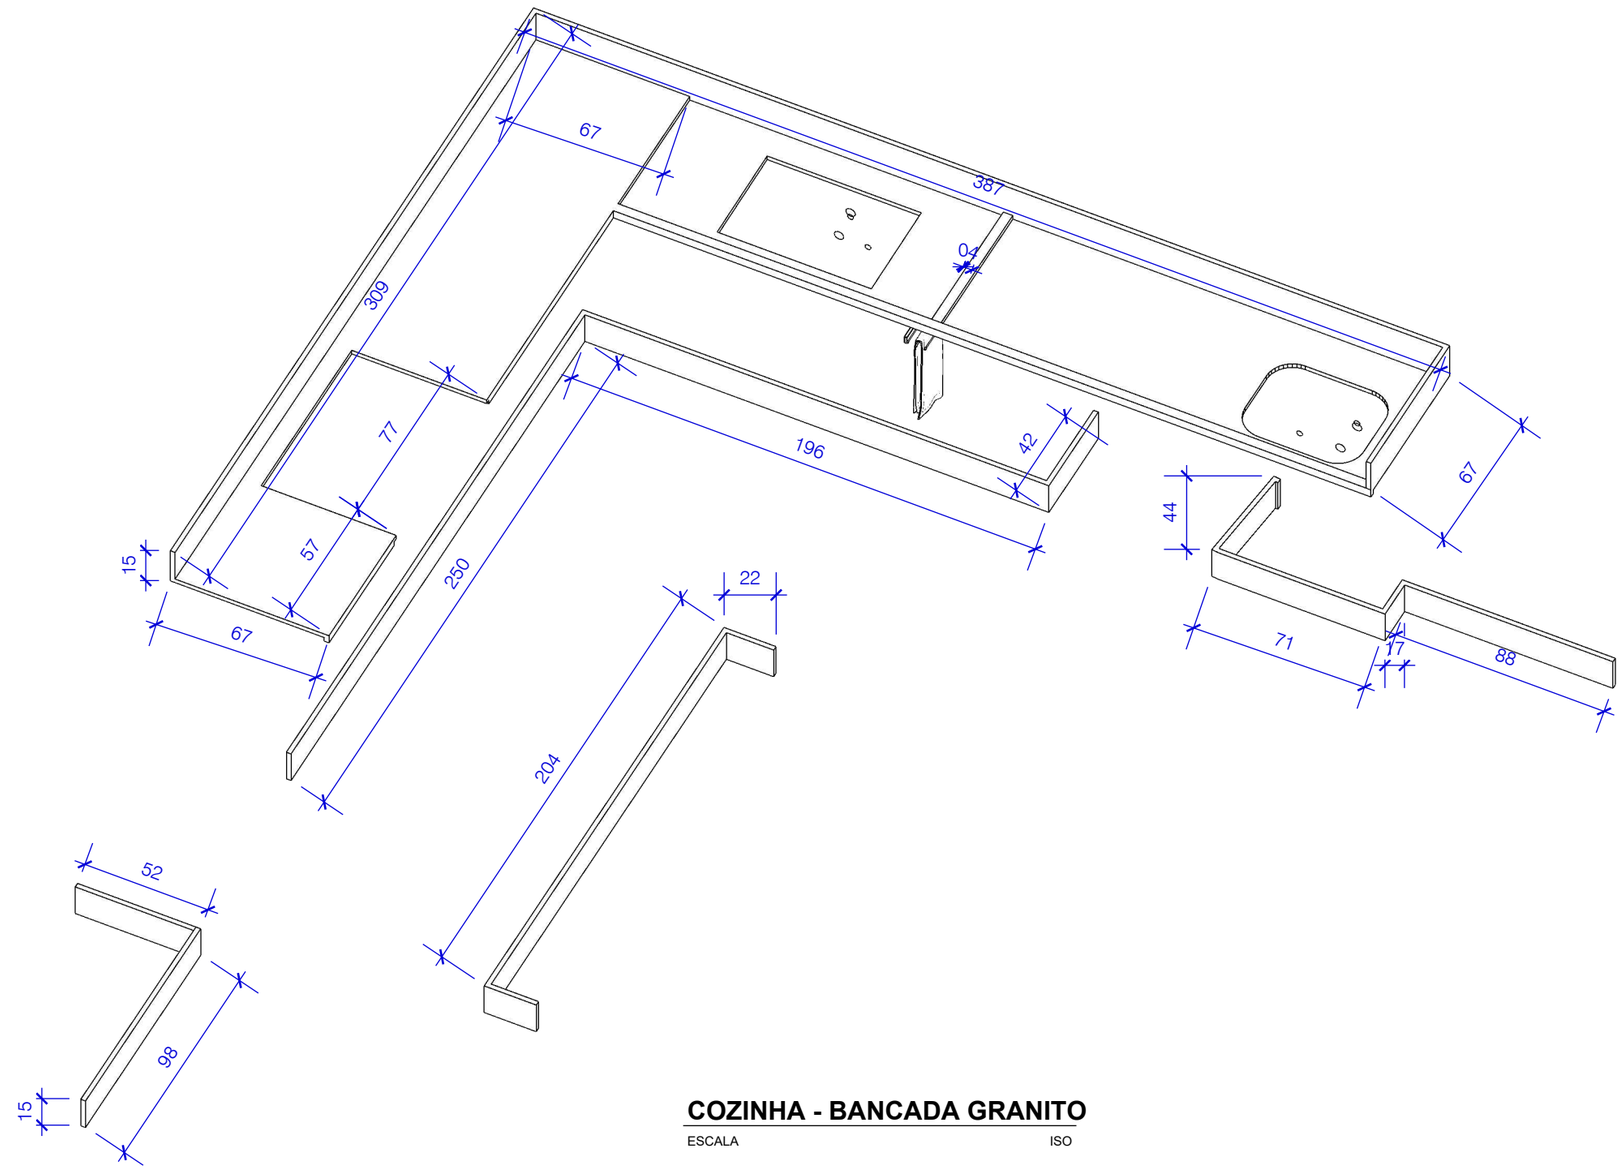


**COZINHA - BANCADA GRANITO**

ESCALA ISO

EMPÓRIO HASS ambientes planejados

contato@emporiohass.com.br
(61)99303-3151/98274-3709
emporiohass

# RESIDÊNCIA 314 NORTE

**CONTEÚDO**
Bancada Granito

**TIPO**
Arquitetura de Interiores

**CLIENTE**
Débora Amarante Brancio Lopes Oliveira

**LOCALIZAÇÃO**

SQN 314 Bloco H Aptº 504
Asa Norte - DF

**ARQUIVO**
ARQ_INT_DEB_JAN2023

**AUTOR**
JMeuren - CAU Nº A487848

**REVISÃO**
01-02-2023



EMPÓRIO HASS ambientes planejados

contato@emporiohass.com.br

(61)99303-3151/98274-3709

emporiohass

# RESIDÊNCIA 314 NORTE

**CONTEÚDO**
Perspectiva

**TIPO**
Arquitetura de Interiores

**CLIENTE**
Débora Amarante Brancio Lopes Oliveira

**LOCALIZAÇÃO**

SQN 314 Bloco H Aptº 504
Asa Norte - DF

**ARQUIVO**
ARQ_INT_DEB_JAN2023

**AUTOR**
JMeuren - CAU Nº A487848

**REVISÃO**
01-02-2023



EMPÓRIO HASS ambientes planejados
contato@emporiohass.com.br
(61)99303-3151/98274-3709
emporiohass

# RESIDÊNCIA 314 NORTE

**CONTEÚDO**
Perspectiva

**TIPO**
Arquitetura de Interiores

**CLIENTE**
Débora Amarante Brancio Lopes Oliveira

**LOCALIZAÇÃO**

SQN 314 Bloco H Aptº 504
Asa Norte - DF

**ARQUIVO**
ARQ_INT_DEB_JAN2023

**AUTOR**
JMeuren - CAU Nº A487848

**REVISÃO**
01-02-2023



EMPÓRIO HASS ambientes planejados

contato@emporiohass.com.br
(61)99303-3151/98274-3709
emporiohass

# RESIDÊNCIA 314 NORTE

**CONTEÚDO**
Perspectiva

**TIPO**
Arquitetura de Interiores

**CLIENTE**
Débora Amarante Brancio Lopes Oliveira

**LOCALIZAÇÃO**

SQN 314 Bloco H Aptº 504
Asa Norte - DF

**ARQUIVO**
ARQ_INT_DEB_JAN2023

**AUTOR**
JMeuren - CAU Nº A487848

**REVISÃO**
01-02-2023



EMPÓRIO HASS ambientes planejados

contato@emporiohass.com.br

(61)99303-3151/98274-3709

emporiohass

# RESIDÊNCIA 314 NORTE

**CONTEÚDO**
Perspectiva

**TIPO**
Arquitetura de Interiores

**CLIENTE**
Débora Amarante Brancio Lopes Oliveira

**LOCALIZAÇÃO**

SQN 314 Bloco H Aptº 504
Asa Norte - DF

**ARQUIVO**
ARQ_INT_DEB_JAN2023

**AUTOR**
JMeuren - CAU Nº A487848

**REVISÃO**
01-02-2023



EMPÓRIO HASS ambientes planejados

contato@emporiohass.com.br
(61)99303-3151/98274-3709
emporiohass

# RESIDÊNCIA 314 NORTE

**CONTEÚDO**
Persectiva

**TIPO**
Arquitetura de Interiores

**CLIENTE**
Débora Amarante Brancio Lopes Oliveira

**LOCALIZAÇÃO**

SQN 314 Bloco H Aptº 504
Asa Norte - DF

**ARQUIVO**
ARQ_INT_DEB_JAN2023

**AUTOR**
JMeuren - CAU Nº A487848

**REVISÃO**
01-02-2023